A2	Tarique Hasan & Associates Ltd.	BOREHOLE NO: 03	Easting: 222837.47	Northing: 2525070.24
		LOCATION : Barisal Airport, Barisal.		
PROJECT : Consultant Services for Development of Saidpur, Barisal and Osmani International Airport Projects (Design Phase)		DEPTH OF BORING : 15.0m		R. L. : 1.552m
CLIENT : Civil Aviation Authority of Bangladesh.		DATE OF BORING : 30-09-2018		B. W. T : 1.6m below from E. G. L.

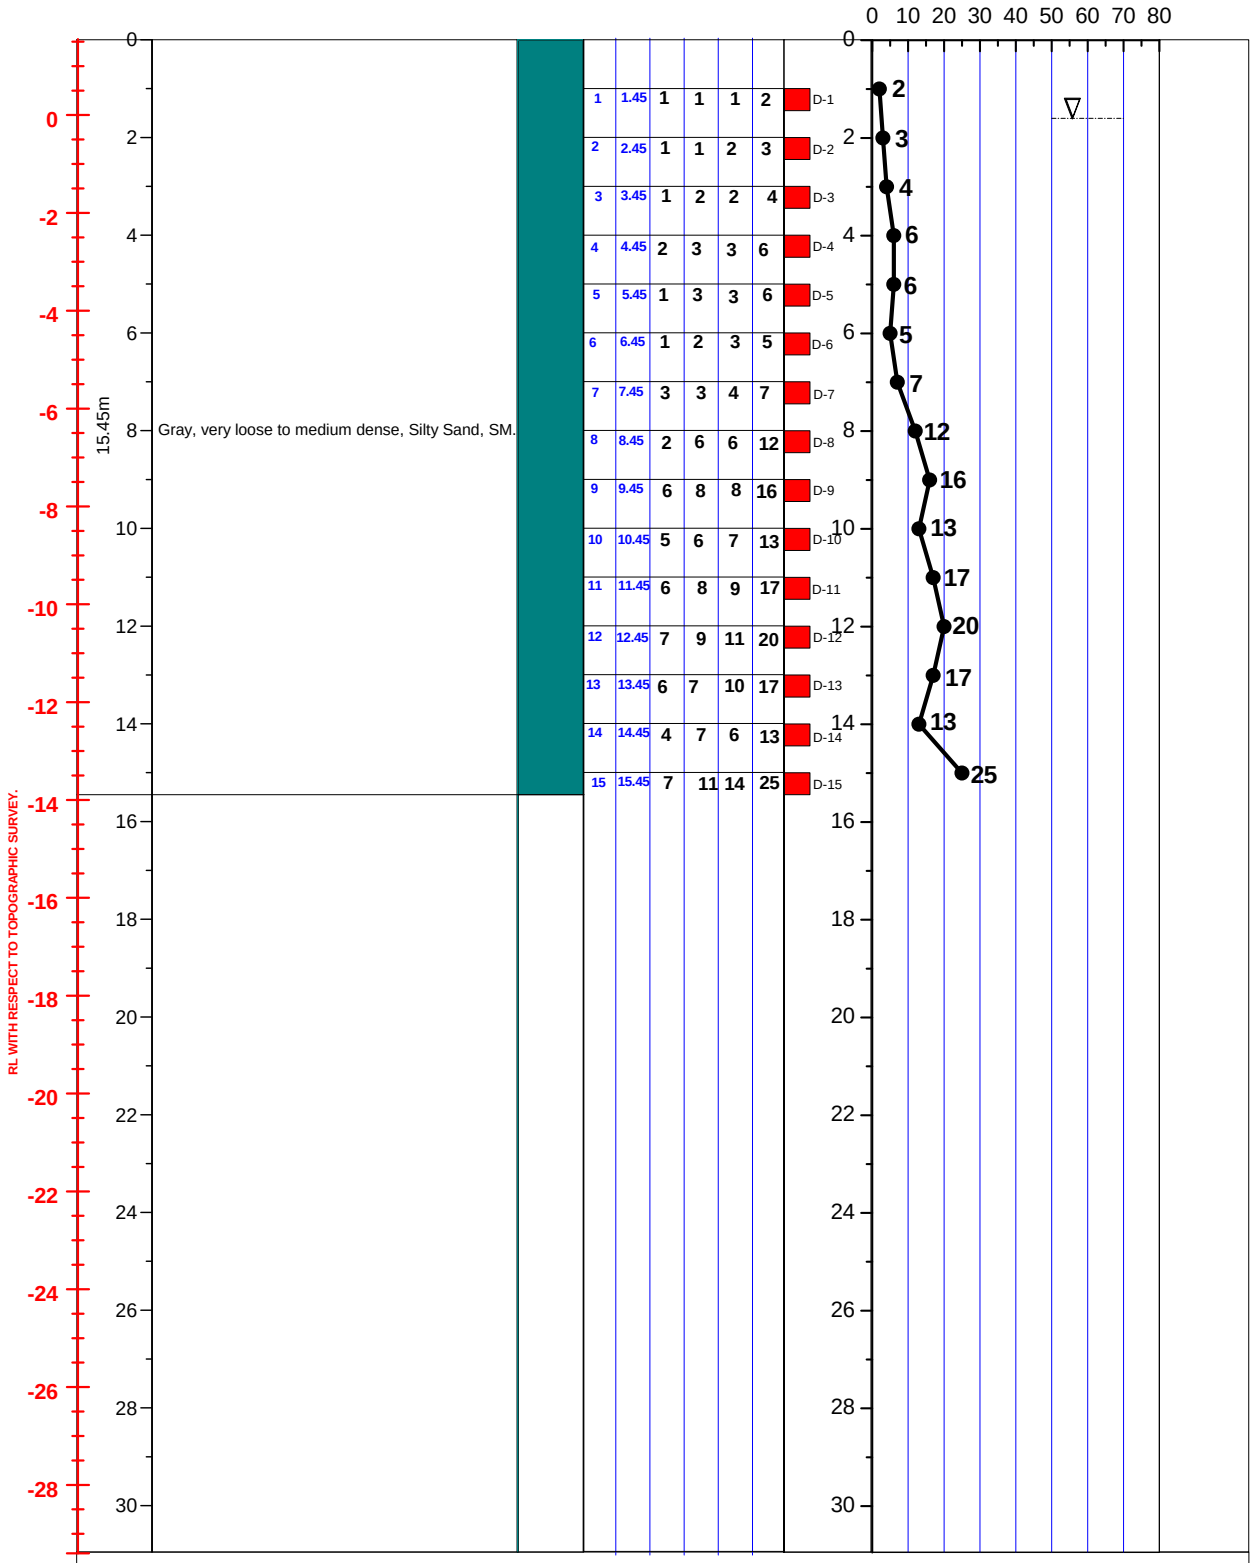

	FROM (m)	TO (m)	N1=150 (mm)	N2=300 (mm)	N3=450 (mm)	N=N2+N3	DISTURBED SAMPLE	SPT VALUES (BLOWS / 300mm)
1	1.45		1	1	1	2	D-1	2
2	2.45		1	1	2	3	D-2	3
3	3.45		1	2	2	4	D-3	4
4	4.45		2	3	3	6	D-4	6
5	5.45		1	3	3	6	D-5	6
6	6.45		1	2	3	5	D-6	5
7	7.45		3	3	4	7	D-7	7
8	8.45		2	6	6	12	D-8	12
9	9.45		6	8	8	16	D-9	16
10	10.45		5	6	7	13	D-10	13
11	11.45		6	8	9	17	D-11	17
12	12.45		7	9	11	20	D-12	20
13	13.45		6	7	10	17	D-13	17
14	14.45		4	7	6	13	D-14	13
15	15.45		7	11	14	25	D-15	25

LEGEND FOR BOREHOLE AND GRAIN SIZE DISTRIBUTION (BASED ON 'ASTM CLASSIFICATION D-2487')

PLASTIC CLAY | SILT | PEAT/HIGHLY ORGANIC SOIL | UNDISTURBED SAMPLE

MICACEOUS FINE SAND/SILT | SAND | SHALE | DISTURBED SAMPLE

N- BLOWS DELIVERED PER FOOT BY A 140 LB HAMMER FALLING 30 INCHES

MAX^m PENETRATION= 50 BLOWS. AFTER 50 BLOWS PENETRATION DEPTH WERE MEASURED