A2	PROSOIL	BOREHOLE NO: BH-1	
		LOCATION : Chainage 22+147 to 22+184m at Feni-Porshuram-Bilonia Road.	
PROJECT : Proposed Porshuram Bridge at Gap No 23/1.		DEPTH OF BORING : 30.0m	Chainage: 22+191 R. L. : 9.4
CLIENT : Road Division, Feni.		DATE OF BORING : 15-11-2012.	G. W. T : 7.32m below from E.G.L.

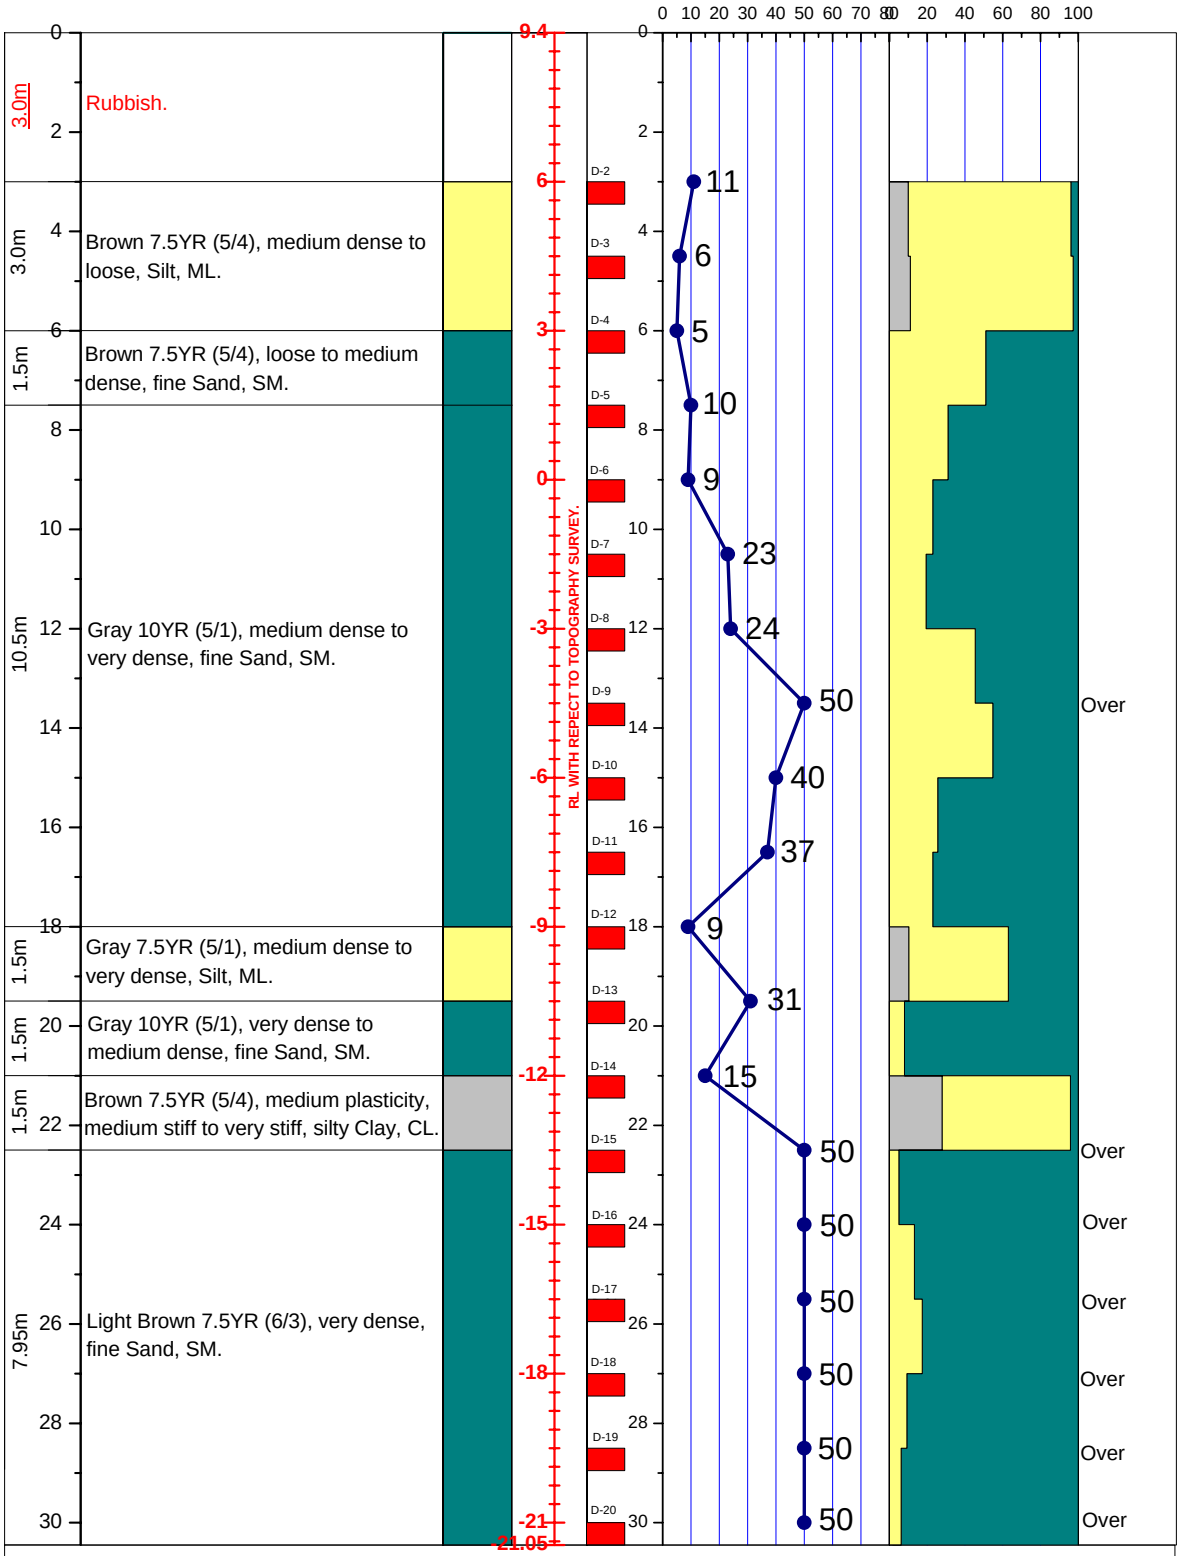

LEGEND FOR BORELOG AND GRAIN SIZE DISTRIBUTION (BASED ON 'ASTM CLASSIFICATION D-2487')

PLASTIC CLAY	SILT	PEAT/HIGHLY ORGANIC SOIL	UNDISTURBED SAMPLE
MICACEOUS FINE SAND/SILT	SAND	SHALE	DISTURBED SAMPLE

N- BLOWS DELIVERED PER FOOT BY A 140 LB HAMMER FALLING 30 INCHES

MAX^m PENETRATION= 50 BLOWS. AFTER 50 BLOWS PENETRATION DEPTH WERE MEASURED