A2	PROSOIL	BOREHOLE NO: BH-1	
		LOCATION: Vill-Baliapur, P. O: Pirojpur, P. S: Meherpur, Dist-Meherpur.	
PROJECT : Telecommunication Tower.		DEPTH OF BORING: 15.0m	R. L.: 0.49m below from Road Level.
CLIENT : Grameenphone Ltd.		DATE OF BORING: 22-02-2015.	B. W. T : 6.10m below from E. G. L.

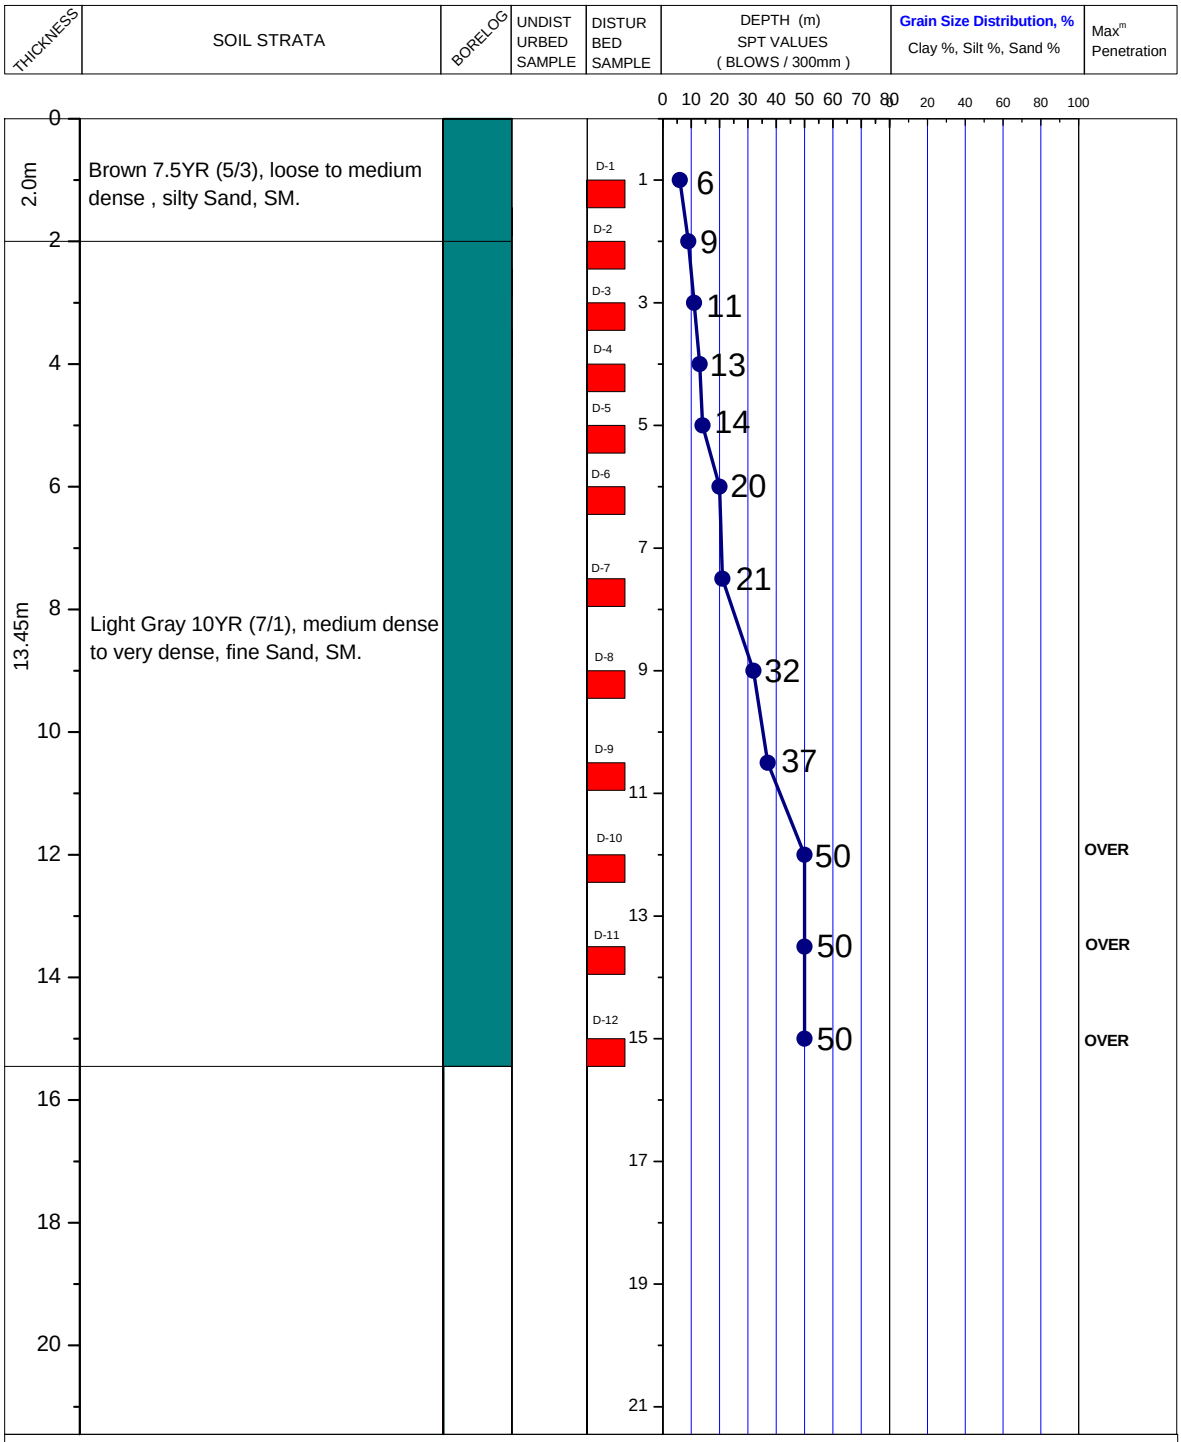

LEGEND FOR BORELOG AND GRAIN SIZE DISTRIBUTION (BASED ON 'ASTM CLASSIFICATION D-2487')

PLASTIC CLAY	SHALE	SILT	SAND
PEAT/HIGHLY ORGANIC SOIL	MICACEOUS FINE SAND/SILT	UNDISTURBED SAMPLE	DISTURBED SAMPLE

N- BLOWS DELIVERED PER FOOT BY A 140 LB HAMMER FALLING 30 INCHES

MAX^{m} PENETRATION= 50 BLOWS

AFTER 50 BLOWS PENETRATION DEPTH WERE MEASURED