A2 PROSOIL	BOREHOLE NO: BH-1	
	LOCATION : Chainage 1+192km Of Kushtia Town By-Pass Road, Kushtia.	
PROJECT : Proposed Kushtia Bridge No 02.	DEPTH OF BORING : 33.0m	Chainage: 1+192 R. L. : 2.9
CLIENT : Road Division, Kushtia.	DATE OF BORING: 24-05-2010.	G. W. T : 1.0m below from E.G.L.

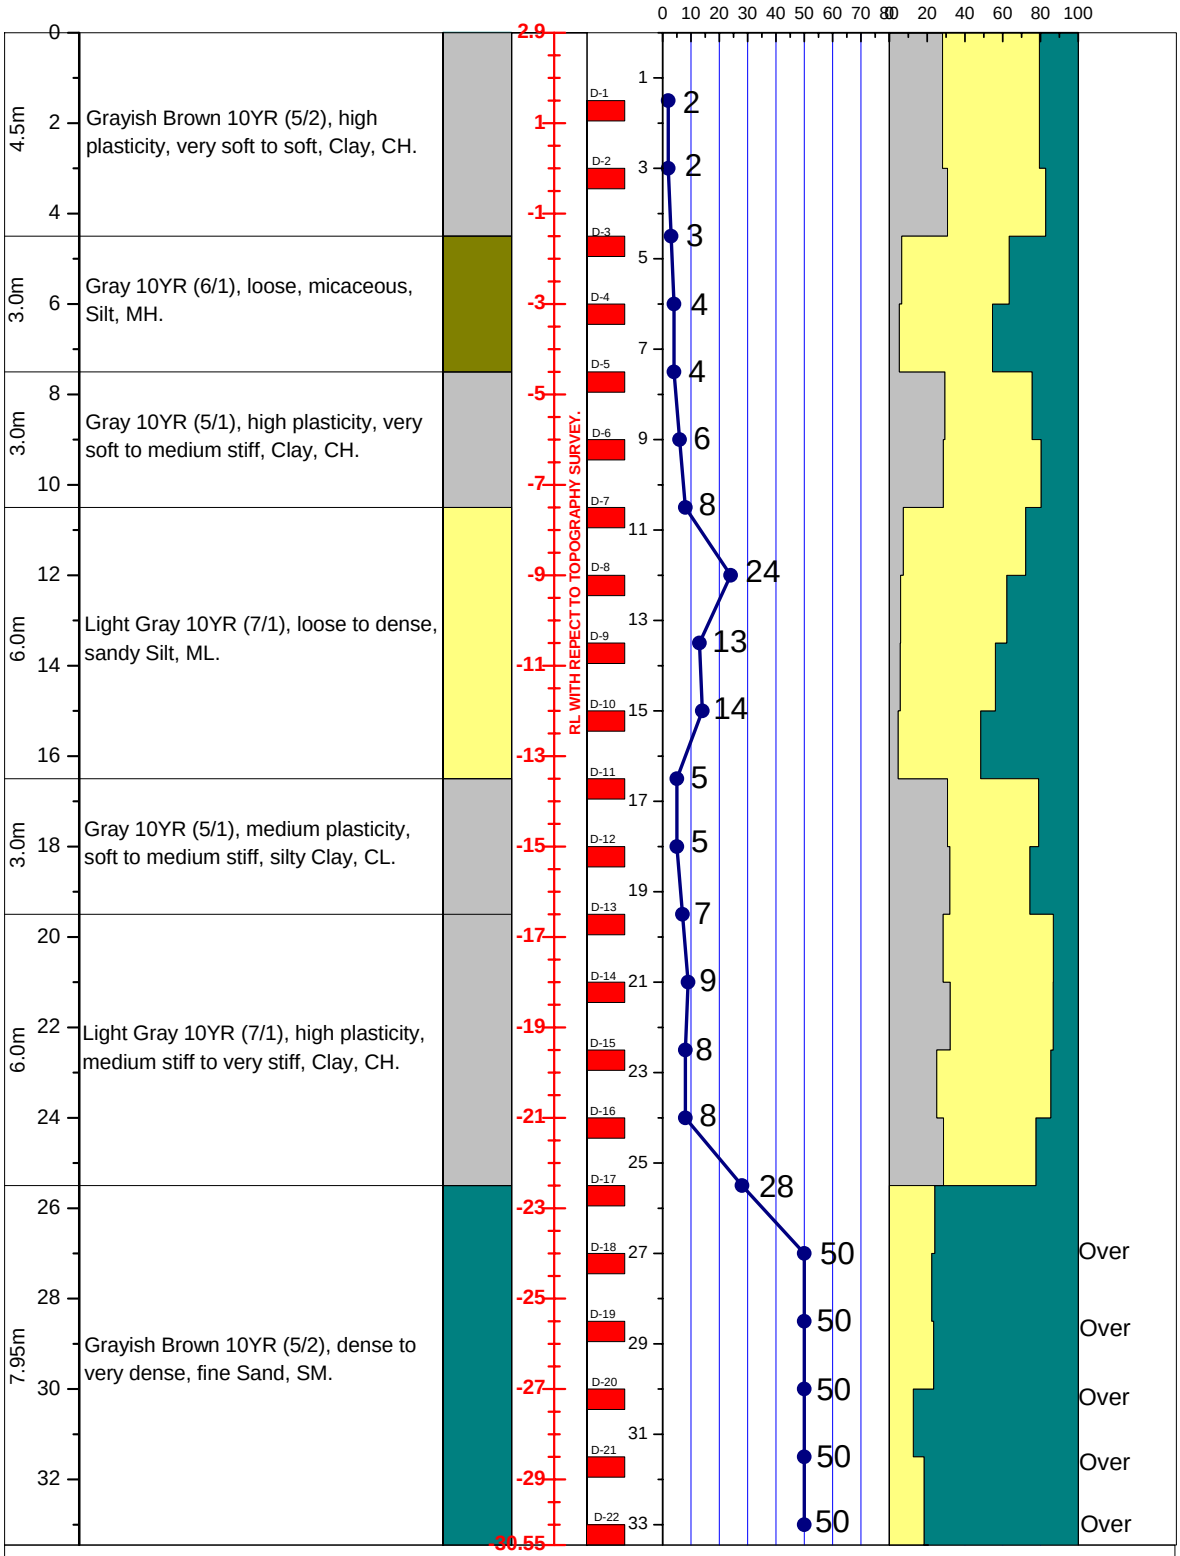

LEGEND FOR BORELOG AND GRAIN SIZE DISTRIBUTION (BASED ON 'ASTM CLASSIFICATION D-2487')

PLASTIC CLAY	SILT	PEAT/HIGHLY ORGANIC SOIL	UNDISTURBED SAMPLE
MICACEOUS FINE SAND/SILT	SAND	SHALE	DISTURBED SAMPLE

N- BLOWS DELIVERED PER FOOT BY A 140 LB HAMMER FALLING 30 INCHES

MAX^{m} PENETRATION= 50 BLOWS. AFTER 50 BLOWS PENETRATION DEPTH WERE MEASURED