A2	PROSOIL	BOREHOLE NO: BH-1	
		LOCATION: Komolapur, Sharatnagar, Kotowali, Comilla, 1 No. Kalir Bazar.	
PROJECT : Telecommunication Tower.		DEPTH OF BORING: 21.0m	R. L.: 0.40m below from Road Level.
CLIENT : Grameenphone Ltd.		DATE OF BORING: 13-04-2012.	G. W. T : 0.12m above from E. G. L .

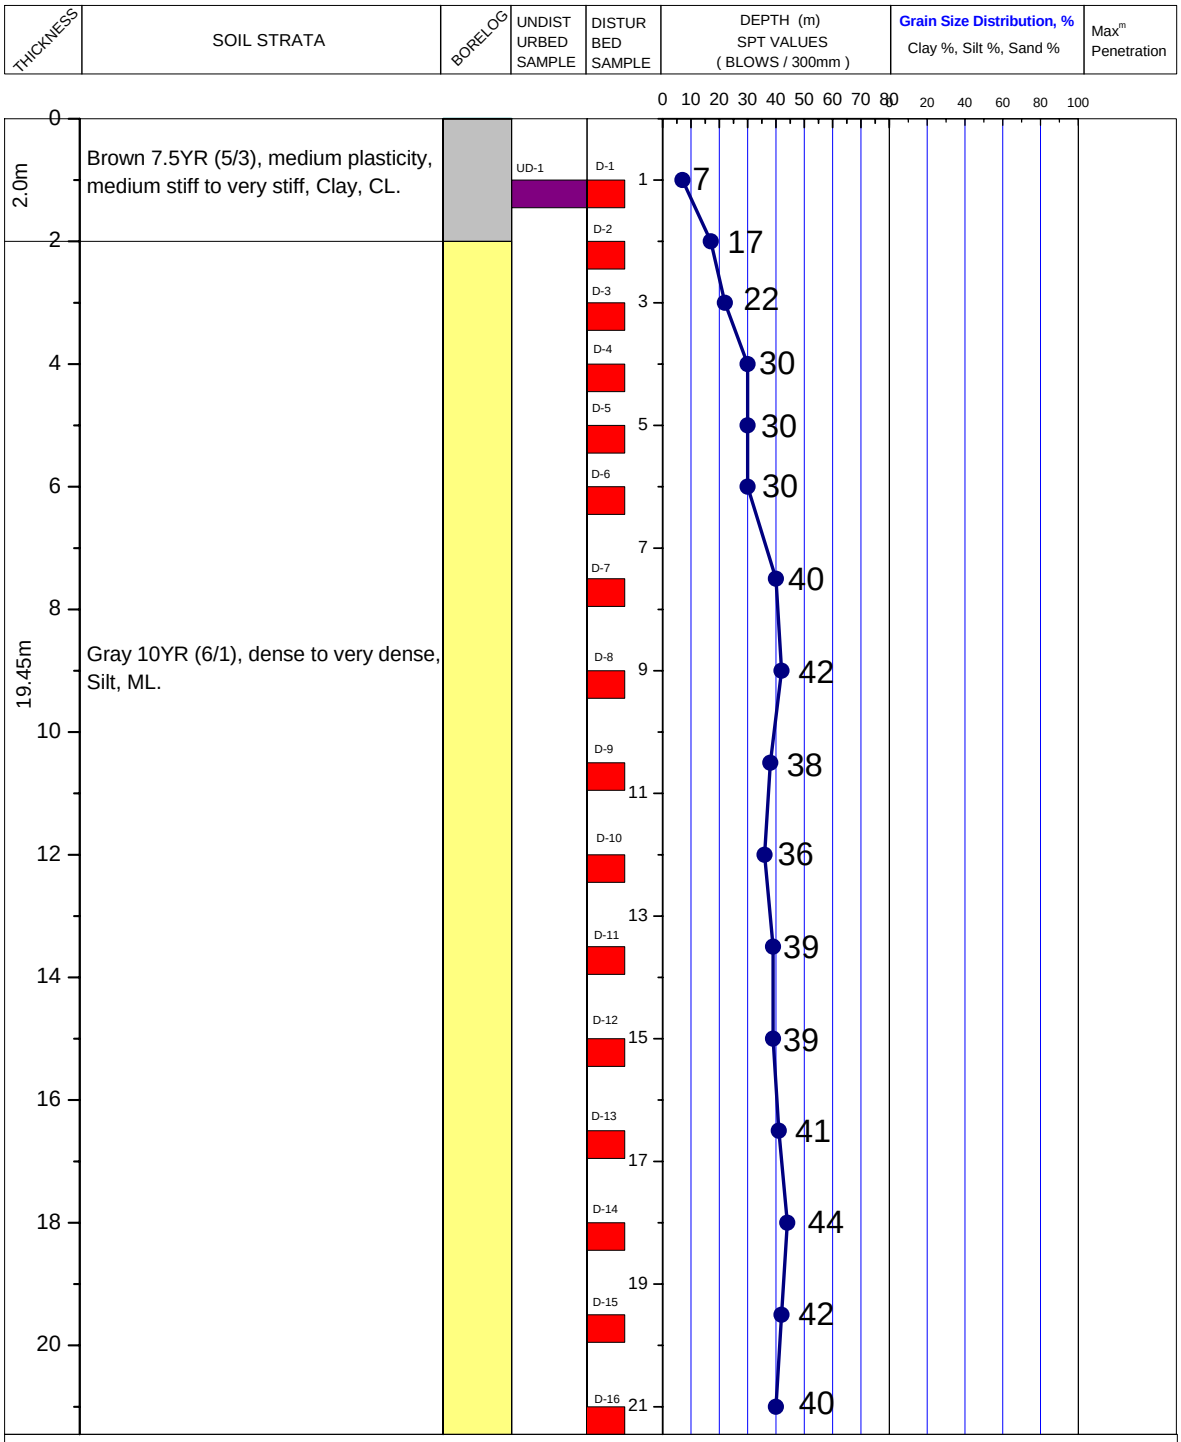

LEGEND FOR BORELOG AND GRAIN SIZE DISTRIBUTION (BASED ON 'ASTM CLASSIFICATION D-2487')

PLASTIC CLAY | SHALE | SILT | SAND

PEAT/HIGHLY ORGANIC SOIL | MICACEOUS FINE SAND/SILT | UNDISTURBED SAMPLE | DISTURBED SAMPLE

N- BLOWS DELIVERED PER FOOT BY A 140 LB HAMMER FALLING 30 INCHES

MAX^{m} PENETRATION= 50 BLOWS

AFTER 50 BLOWS PENETRATION DEPTH WERE MEASURED