| A2 PROSOIL | BOREHOLE NO: BH-1 | |
|---|---|---|
| | LOCATION : Additmari, Lalmonirhat. | |
| PROJECT : Telecommunication Tower. | DEPTH OF BORING : 21.0m | R. L.: 1.21m below from Road Level. |
| CLIENT : Sheba Telecom (PVT.) Ltd. | DATE OF BORING : 10-08-2007. | G. W. T : 2.13m below from E. G. L. |

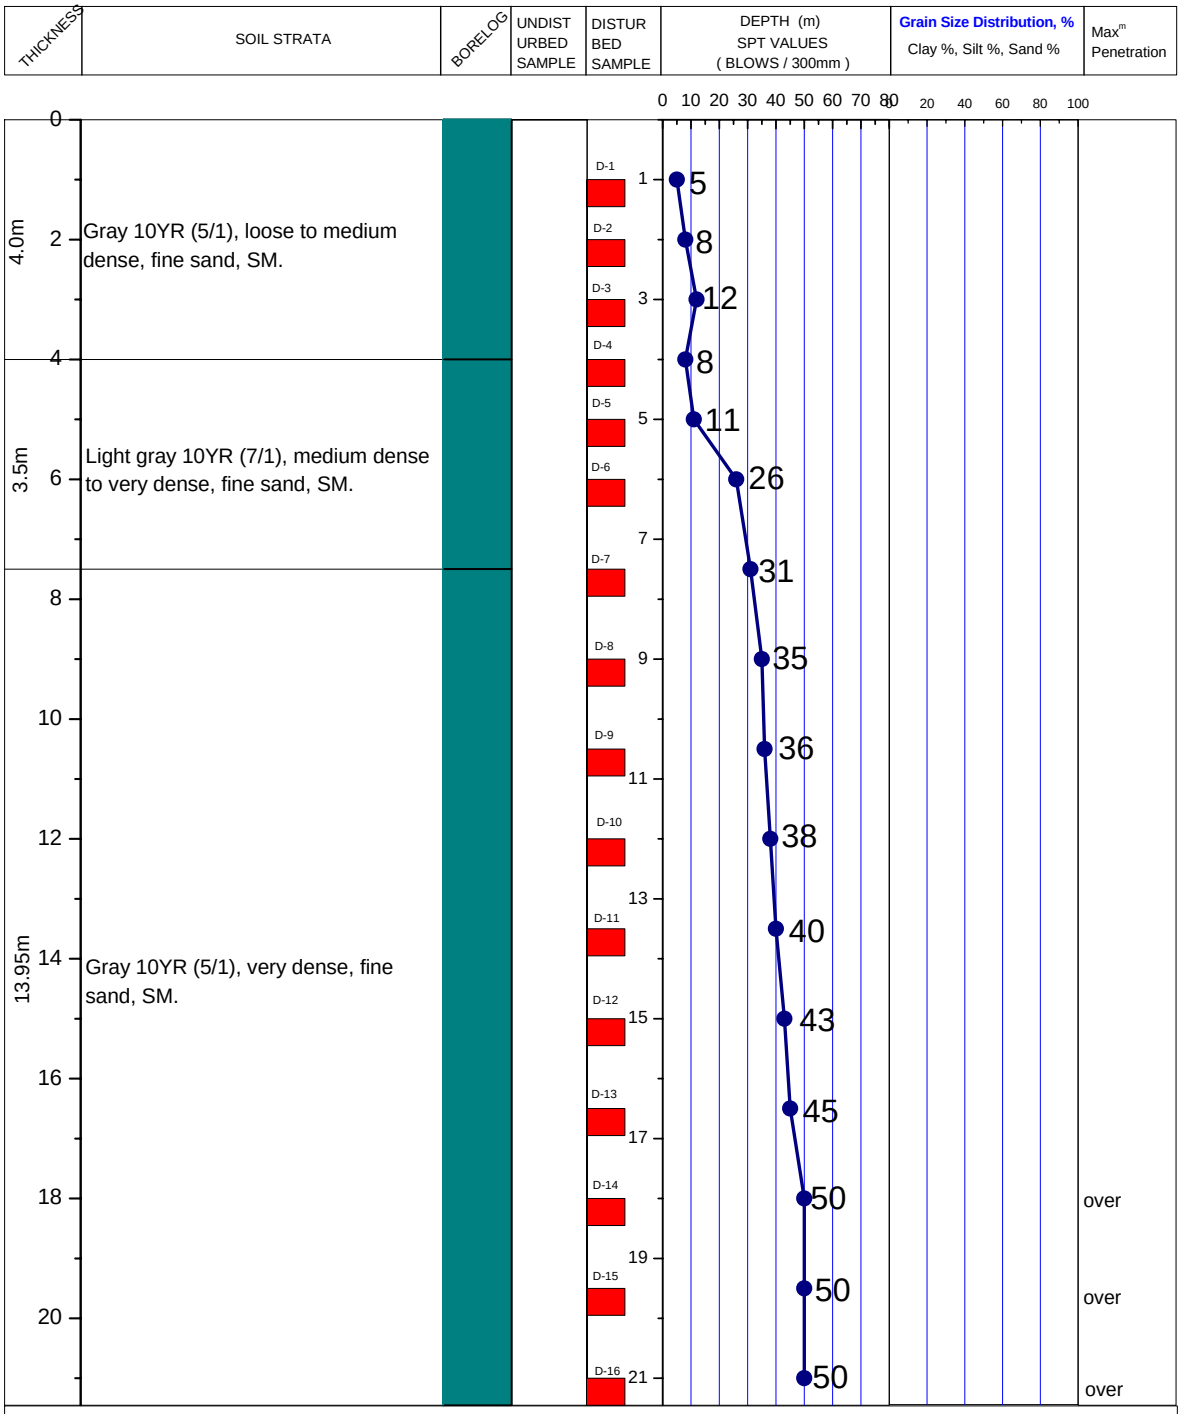


LEGEND FOR BORELOG AND GRAIN SIZE DISTRIBUTION

PLASTIC SILTY CLAY

LOW PLASTIC CLAYEY SILT

NON PLASTIC SILT

SAND

ORGANIC

UNDISTURBED SAMPLE

DISTURBED SAMPLE

SHALE

N- BLOWS DELIVERED PER FOOT BY A 140 LB HAMMER FALLING 30 INCHES

MAX$^{m}$ PENETRATION= 50 BLOWS

AFTER 50 BLOWS PENETRATION DEPTH WERE MEASURED