A2	PROSOIL	BOREHOLE NO: BH-1 (A1)	
		LOCATION : 21st km. of Narail-Kalia Road over Nobaganga River.	
PROJECT : 565.0m (42.68mx13) Long P.C. Girder Bridge.		DEPTH OF BORING : 42.0m	Chainage: 21+996 R. L. : 2.96
CLIENT : Road Division, Narail.		DATE OF BORING : 26-09-2013.	G. W. T : 1.25m below from E.G.L.

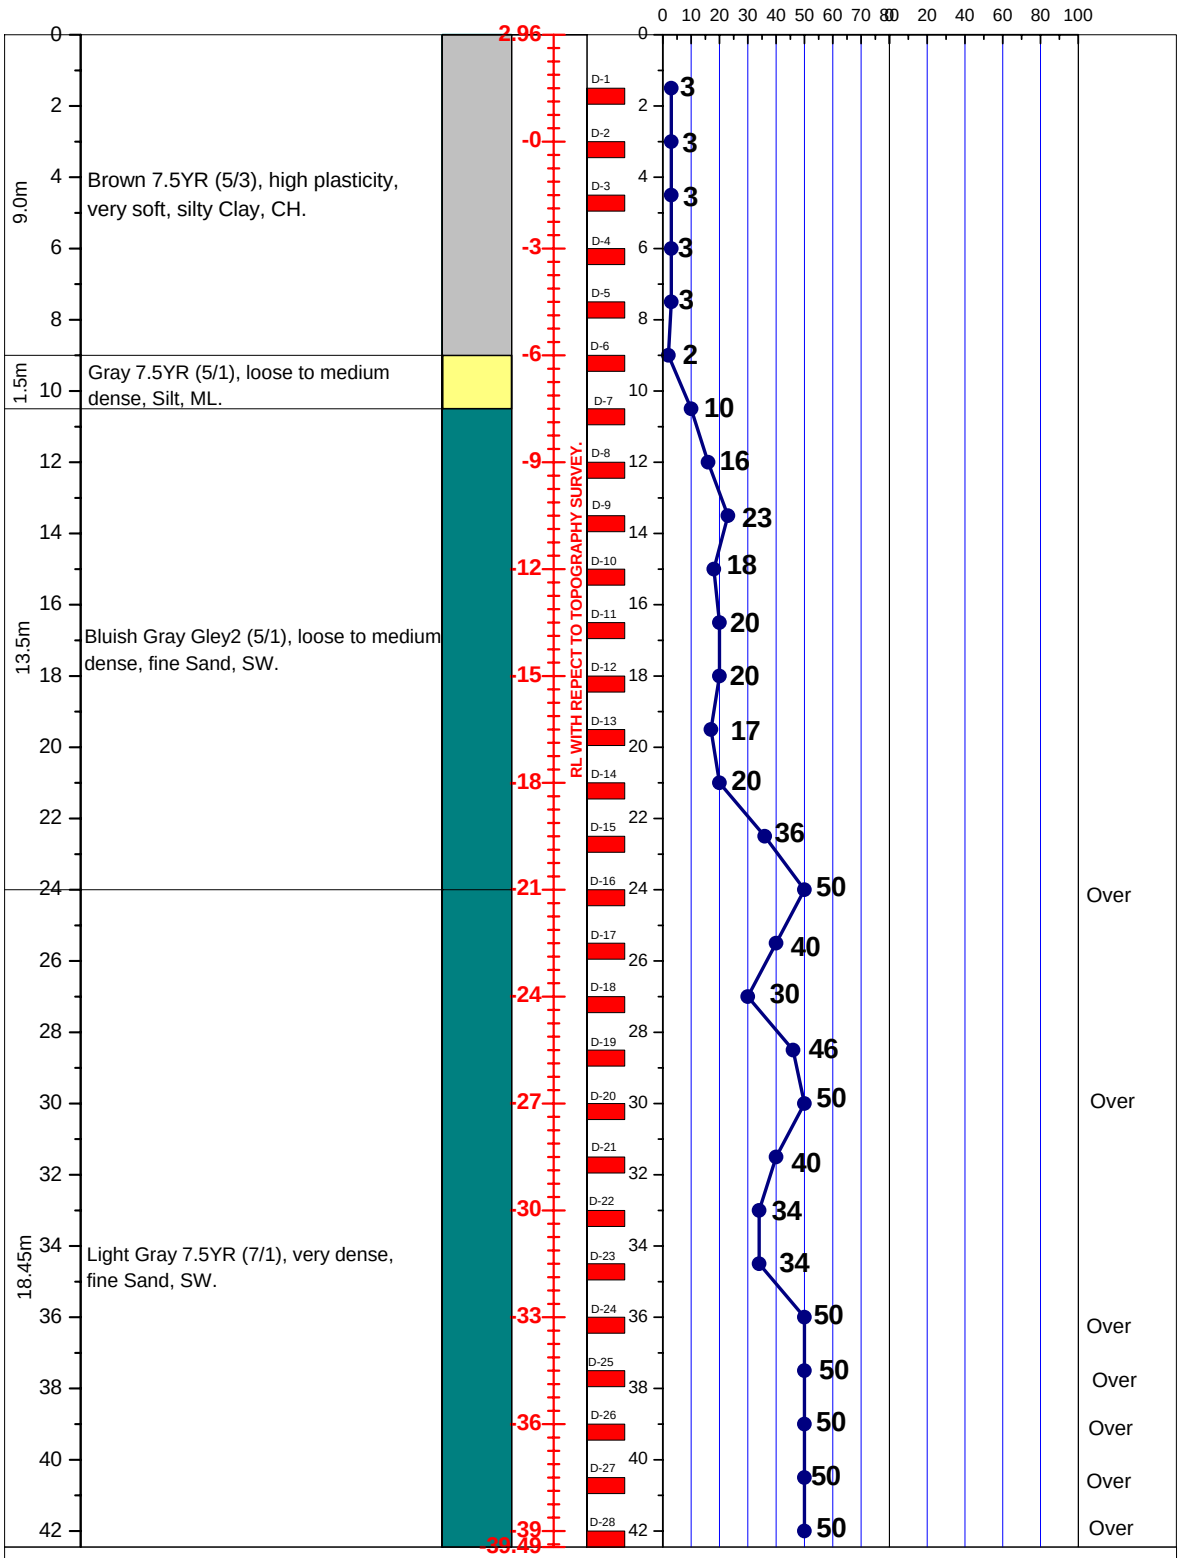

LEGEND FOR BORELOG AND GRAIN SIZE DISTRIBUTION (BASED ON 'ASTM CLASSIFICATION D-2487')

PLASTIC CLAY	SILT	PEAT/HIGHLY ORGANIC SOIL	UNDISTURBED SAMPLE
MICACEOUS FINE SAND/SILT	SAND	SHALE	DISTURBED SAMPLE

N- BLOWS DELIVERED PER FOOT BY A 140 LB HAMMER FALLING 30 INCHES

MAX^m PENETRATION= 50 BLOWS. AFTER 50 BLOWS PENETRATION DEPTH WERE MEASURED