A2	PROSOIL	BOREHOLE NO: BH-1	
		LOCATION : Langalbondh-Kaikertek-Nobigonj Road (1st k.m. Ch. 00+780).	
PROJECT : Proposed Bridge.		DEPTH OF BORING : 51.0m	Chainage: 00+777 R. L. : 5.69
CLIENT : Road Division, Narayangonj.		DATE OF BORING : 23-06-2013.	G. W. T : 6.10m below from E.G.L.

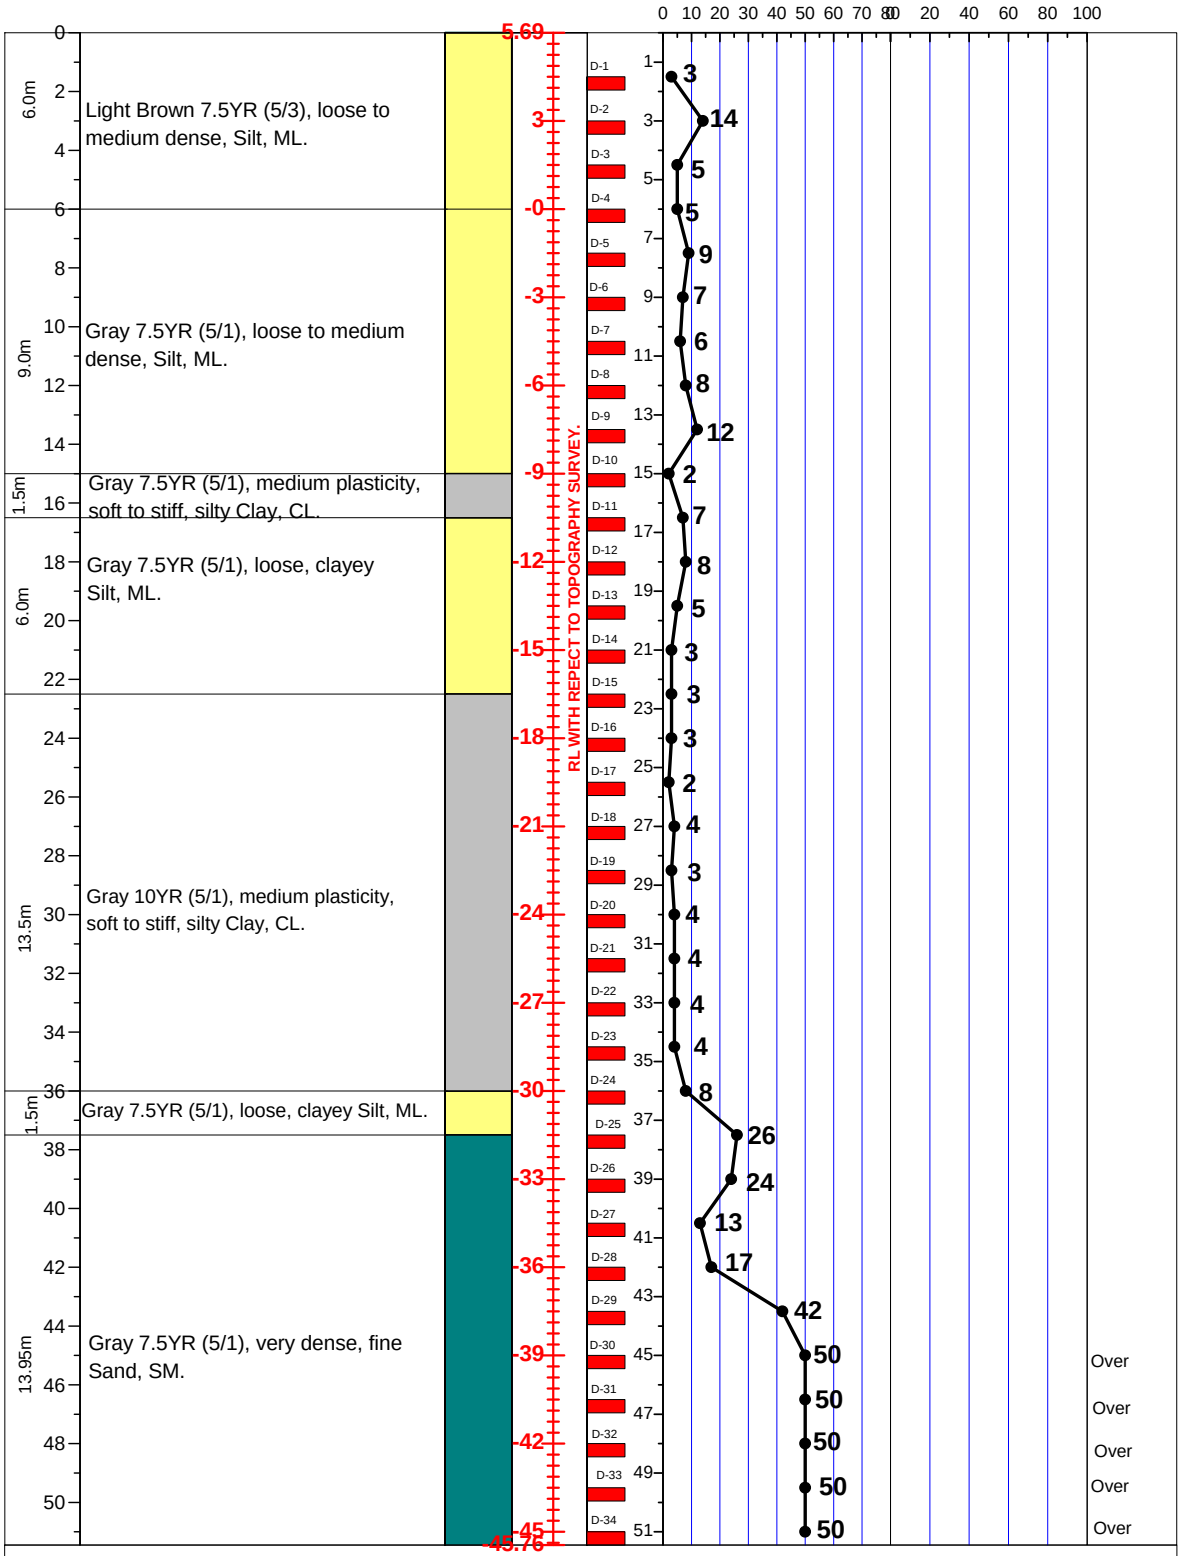

LEGEND FOR BOREHOLE AND GRAIN SIZE DISTRIBUTION (BASED ON 'ASTM CLASSIFICATION D-2487')

PLASTIC CLAY	SILT	PEAT/HIGHLY ORGANIC SOIL	UNDISTURBED SAMPLE
MICACEOUS FINE SAND/SILT	SAND	SHALE	DISTURBED SAMPLE

N- BLOWS DELIVERED PER FOOT BY A 140 LB HAMMER FALLING 30 INCHES

MAX^m PENETRATION= 50 BLOWS. AFTER 50 BLOWS PENETRATION DEPTH WERE MEASURED