A2	PROSOIL	BOREHOLE NO: BH-1	
		LOCATION : Khulsi Bazar, Chapai Nawabgonj.	
PROJECT : Telecommunication Tower.		DEPTH OF BORING : 21.0m	R. L.: 0.51m below from Road Level.
CLIENT : AXIATA (Bangladesh) Ltd.		DATE OF BORING : 11-03-2010.	G. W. T : 1.21m below from E. G. L.

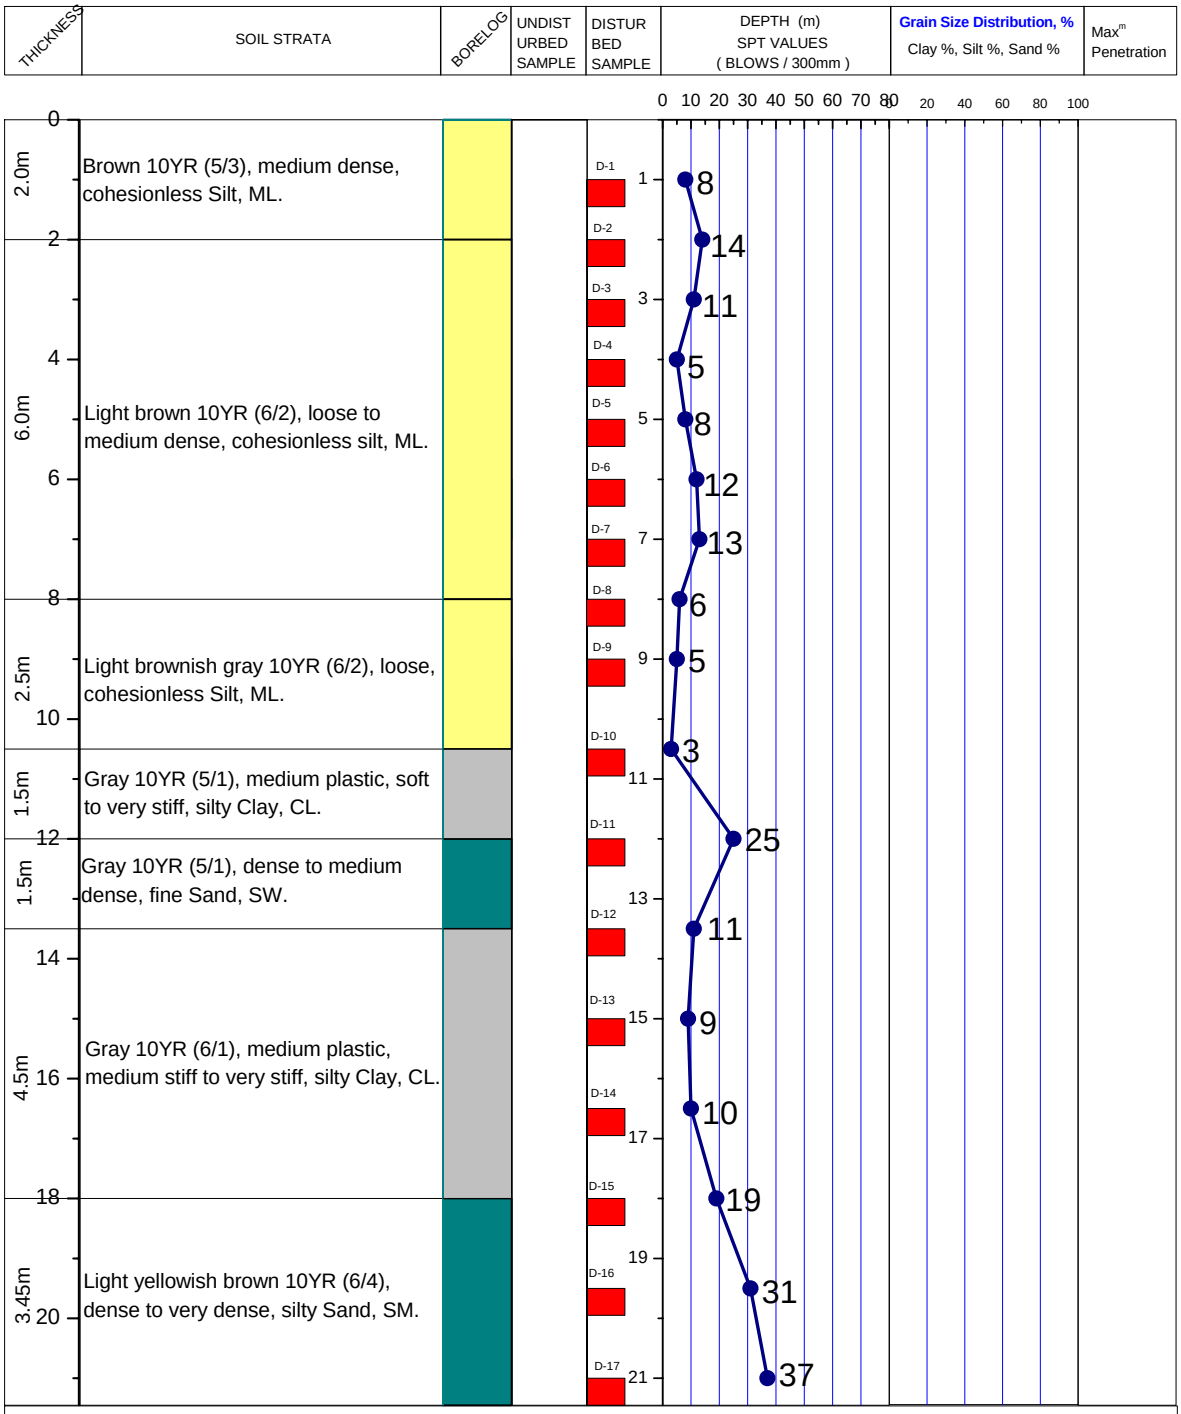

LEGEND FOR BORELOG AND GRAIN SIZE DISTRIBUTION (BASED ON 'ASTM CLASSIFICATION D-2487')

PLASTIC CLAY | MICACEOUS FINE SAND/SILT | SILT | SAND

PEAT/HIGHLY ORGANIC SOIL | UNDISTURBED SAMPLE | DISTURBED SAMPLE | SHALE

N- BLOWS DELIVERED PER FOOT BY A 140 LB HAMMER FALLING 30 INCHES

MAX^{m} PENETRATION= 50 BLOWS

AFTER 50 BLOWS PENETRATION DEPTH WERE MEASURED