
A2	PROSOIL	BOREHOLE NO: BH-1	
		LOCATION : Chandra, Ramu, Cox's Bazar.	
PROJECT : Telecommunication Tower.		DEPTH OF BORING : 51.0m	R. L.: 1.37m below from Road Level.
CLIENT : AXIATA (Bangladesh) Ltd.		DATE OF BORING : 12-05-2010.	G. W. T : 1.37m below from E. G. L.

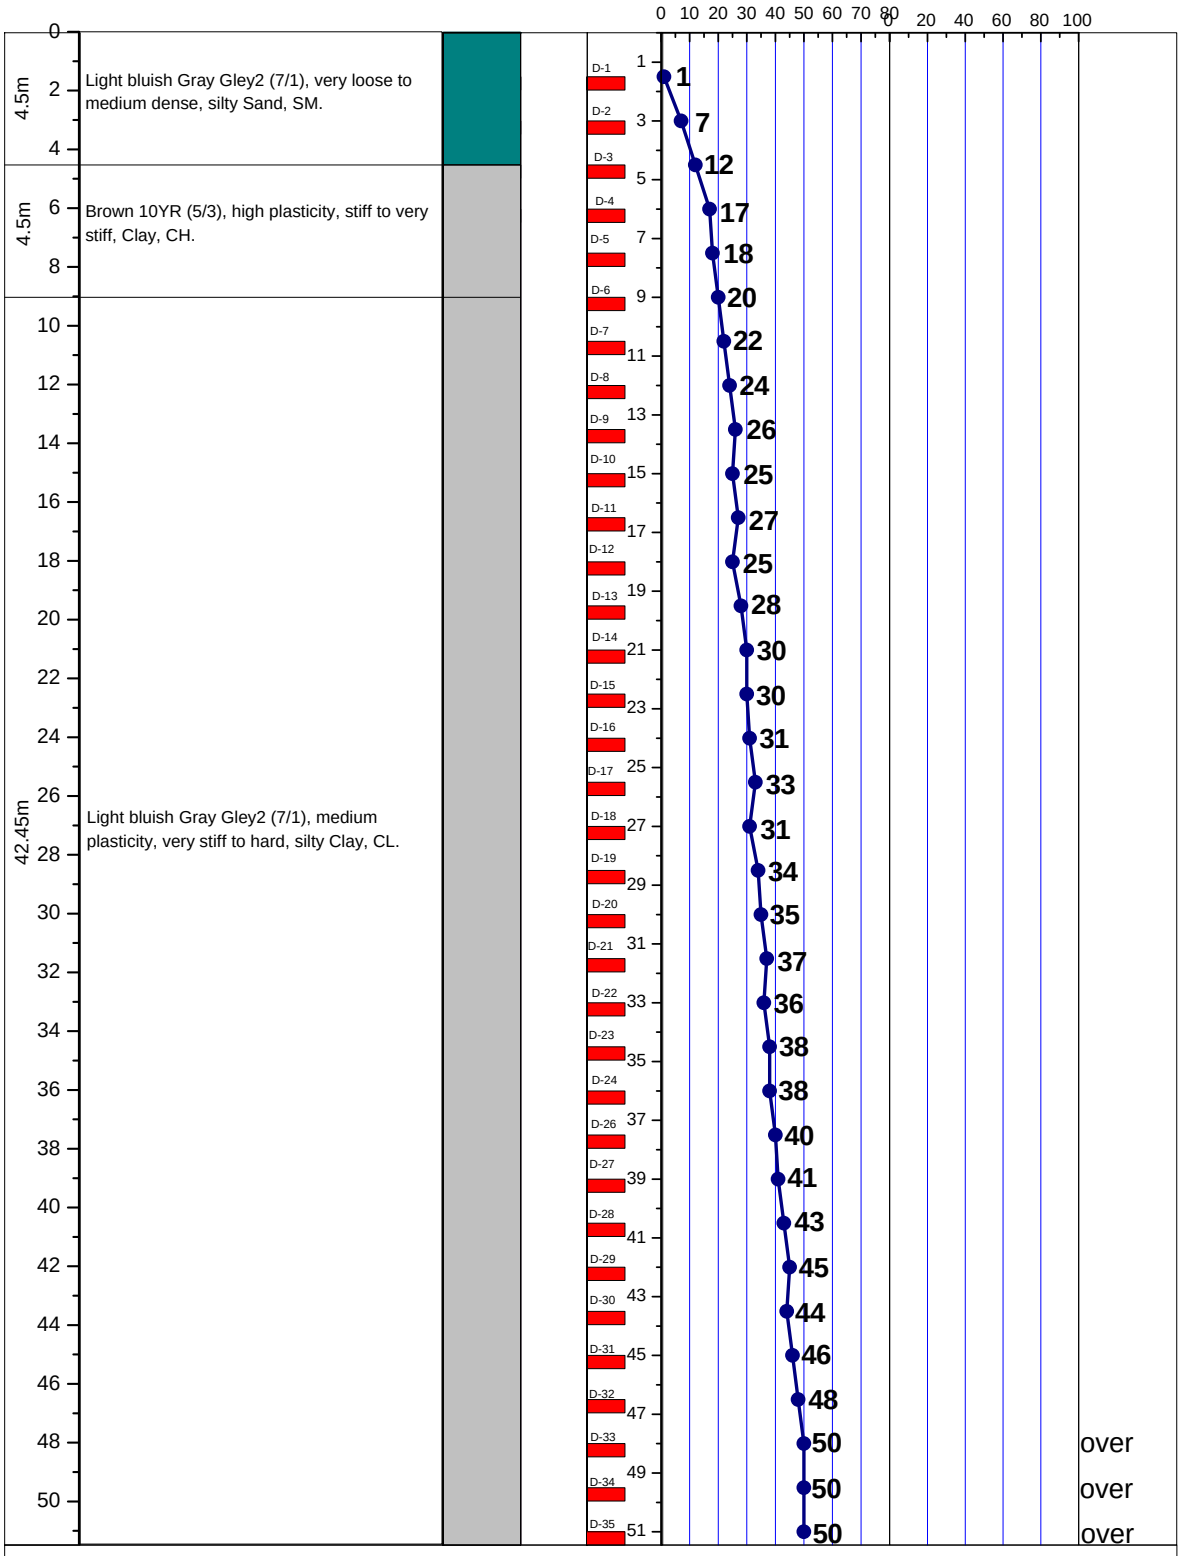


LEGEND FOR BORELOG AND GRAIN SIZE DISTRIBUTION (BASED ON 'ASTM CLASSIFICATION D-2487')

PLASTIC CLAY	SILT	PEAT/HIGHLY ORGANIC SOIL	UNDISTURBED SAMPLE
MICACEOUS FINE SAND/SILT	SAND	SHALE	DISTURBED SAMPLE

N- BLOWS DELIVERED PER FOOT BY A 140 LB HAMMER FALLING 30 INCHES

MAX^{m} PENETRATION= 50 BLOWS. AFTER 50 BLOWS PENETRATION DEPTH WERE MEASURED

A2 PROSOIL	BOREHOLE NO: BH-1	
	LOCATION : Naptardia, Pekua, cox's Bazar.	
PROJECT : Telecommunication Tower.	DEPTH OF BORING : 51.0m	R. L.: 0.30m below from Road Level.
CLIENT :Grameenphone Ltd.	DATE OF BORING : 22-08-2007.	G. W. T : 0.15m above from E. G. L. (Rain Water.)

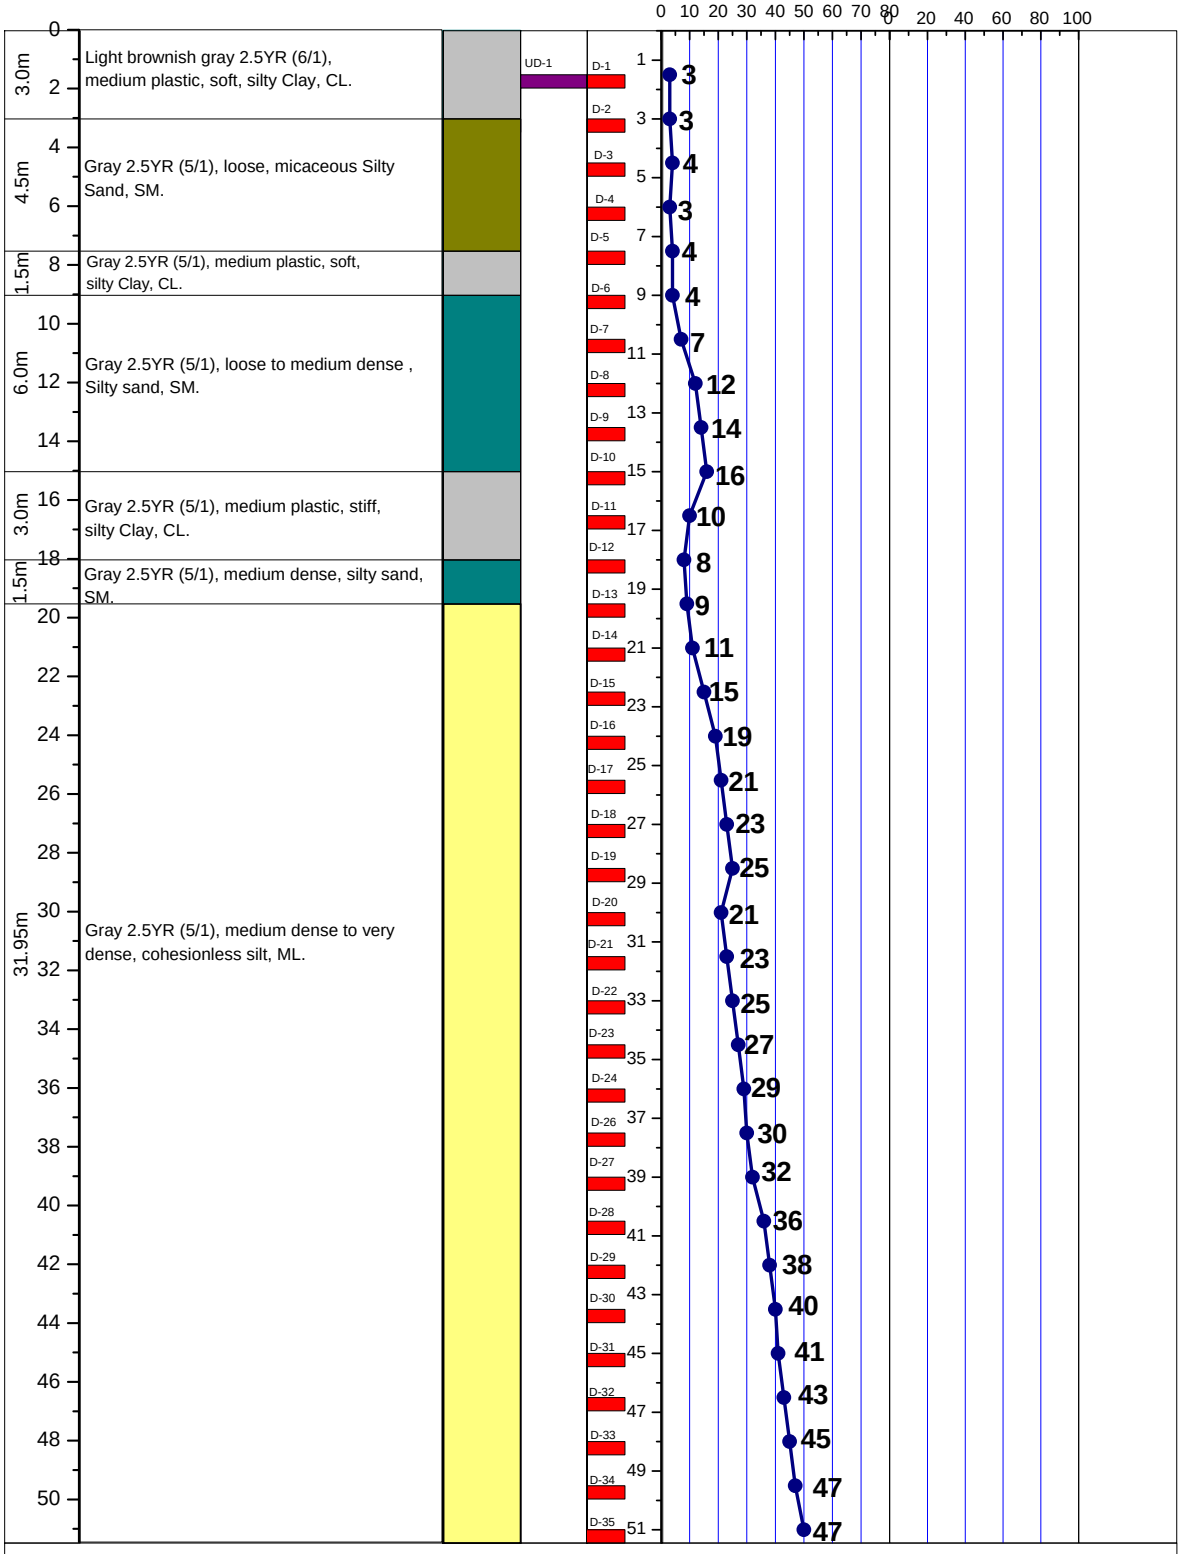

LEGEND FOR BORELOG AND GRAIN SIZE DISTRIBUTION (BASED ON 'ASTM CLASSIFICATION D-2487')

PLASTIC CLAY	SILT	PEAT/HIGHLY ORGANIC SOIL	UNDISTURBED SAMPLE
MICACEOUS FINE SAND/SILT	SAND	SHALE	DISTURBED SAMPLE

N- BLOWS DELIVERED PER FOOT BY A 140 LB HAMMER FALLING 30 INCHES

MAX^{m} PENETRATION= 50 BLOWS. AFTER 50 BLOWS PENETRATION DEPTH WERE MEASURED

A2	PROSOIL	BOREHOLE NO: BH-1	
		LOCATION :Janarguna, Cox's Bazar Sadar, Cox's Bazar.	
PROJECT : Telecommunication Tower.		DEPTH OF BORING : 51.0m	R. L.: 0.91m below from Road Level.
CLIENT :Grameenphone Ltd.		DATE OF BORING : 08-05-2009.	G. W. T : 0.76m below from E. G. L.

THICKNESS	SOIL STRATA	BORELOG	DISTURBED SAMPLE	DEPTH (m) SPT VALUES (BLOWS / 300mm)	Grain Size Distribution, % Clay %, Silt %, Sand %	Max^{m} Penetration
3.0m	Very pale brown 10YR (7/3), medium plastic, very soft, silty Clay, CL.		UD-1, UD-2, D-1, D-2	1, 1		
1.5m	Gray 10YR (6/1), medium plastic, very soft, silty Clay, CL.		D-3	6		
1.5m	Gray 10YR (6/1), loose, Silty sand, SM.		D-4, D-5	3, 1		
1.5m	Gray 10YR (6/1), medium plastic, soft, silty Clay, CL.		D-6	11		
1.5m	Gray 10YR (6/1), very loose, silty Sand, SM.		D-7, D-8	4, 5		
3.0m	Gray 10YR (6/1), medium plastic, soft to stiff, silty Clay, CL.		D-9, D-10	7, 11		
1.5m	Gray 10YR (6/1), loose, silty Sand, SM.		D-11	10		
1.5m	Gray 10YR (6/1), medium dense, cohesionless silt, ML.		D-12, D-13	11, 11		
1.5m	Gray 10YR (6/1), medium dense, silty Sand, SM.		D-14	12		
4.5m	Gray 10YR (6/1), medium dense, cohesionless silt, ML.		D-15, D-16	9, 13		
30.45m	Gray 10YR (6/1), medium dense to very dense, Silty sand, SM.		D-17, D-18, D-19, D-20, D-21, D-22, D-23, D-24, D-26, D-27, D-28, D-29, D-30, D-31, D-32, D-33, D-34, D-35	15, 17, 19, 21, 23, 25, 27, 29, 33, 31, 35, 37, 39, 38, 41, 43, 45, 48		


LEGEND FOR BORELOG AND GRAIN SIZE DISTRIBUTION (BASED ON 'ASTM CLASSIFICATION D-2487')

PLASTIC CLAY	SILT	PEAT/HIGHLY ORGANIC SOIL	UNDISTURBED SAMPLE
MICACEOUS FINE SAND/SILT	SAND	SHALE	DISTURBED SAMPLE

N- BLOWS DELIVERED PER FOOT BY A 140 LB HAMMER FALLING 30 INCHES

MAX^{m} PENETRATION= 50 BLOWS. AFTER 50 BLOWS PENETRATION DEPTH WERE MEASURED

A2 PROSOIL	BOREHOLE NO: BH-1	
	LOCATION : Dadimora, Ranginkhali, Teknaf, Cox's Bazar.	
PROJECT : Telecommunication Tower.	DEPTH OF BORING : 51.0m	R. L.: 0.61m below from Road Level.
CLIENT : AXIATA (Bangladesh) Ltd.	DATE OF BORING : 29-05-2010.	G. W. T : 1.52m below from E. G. L.

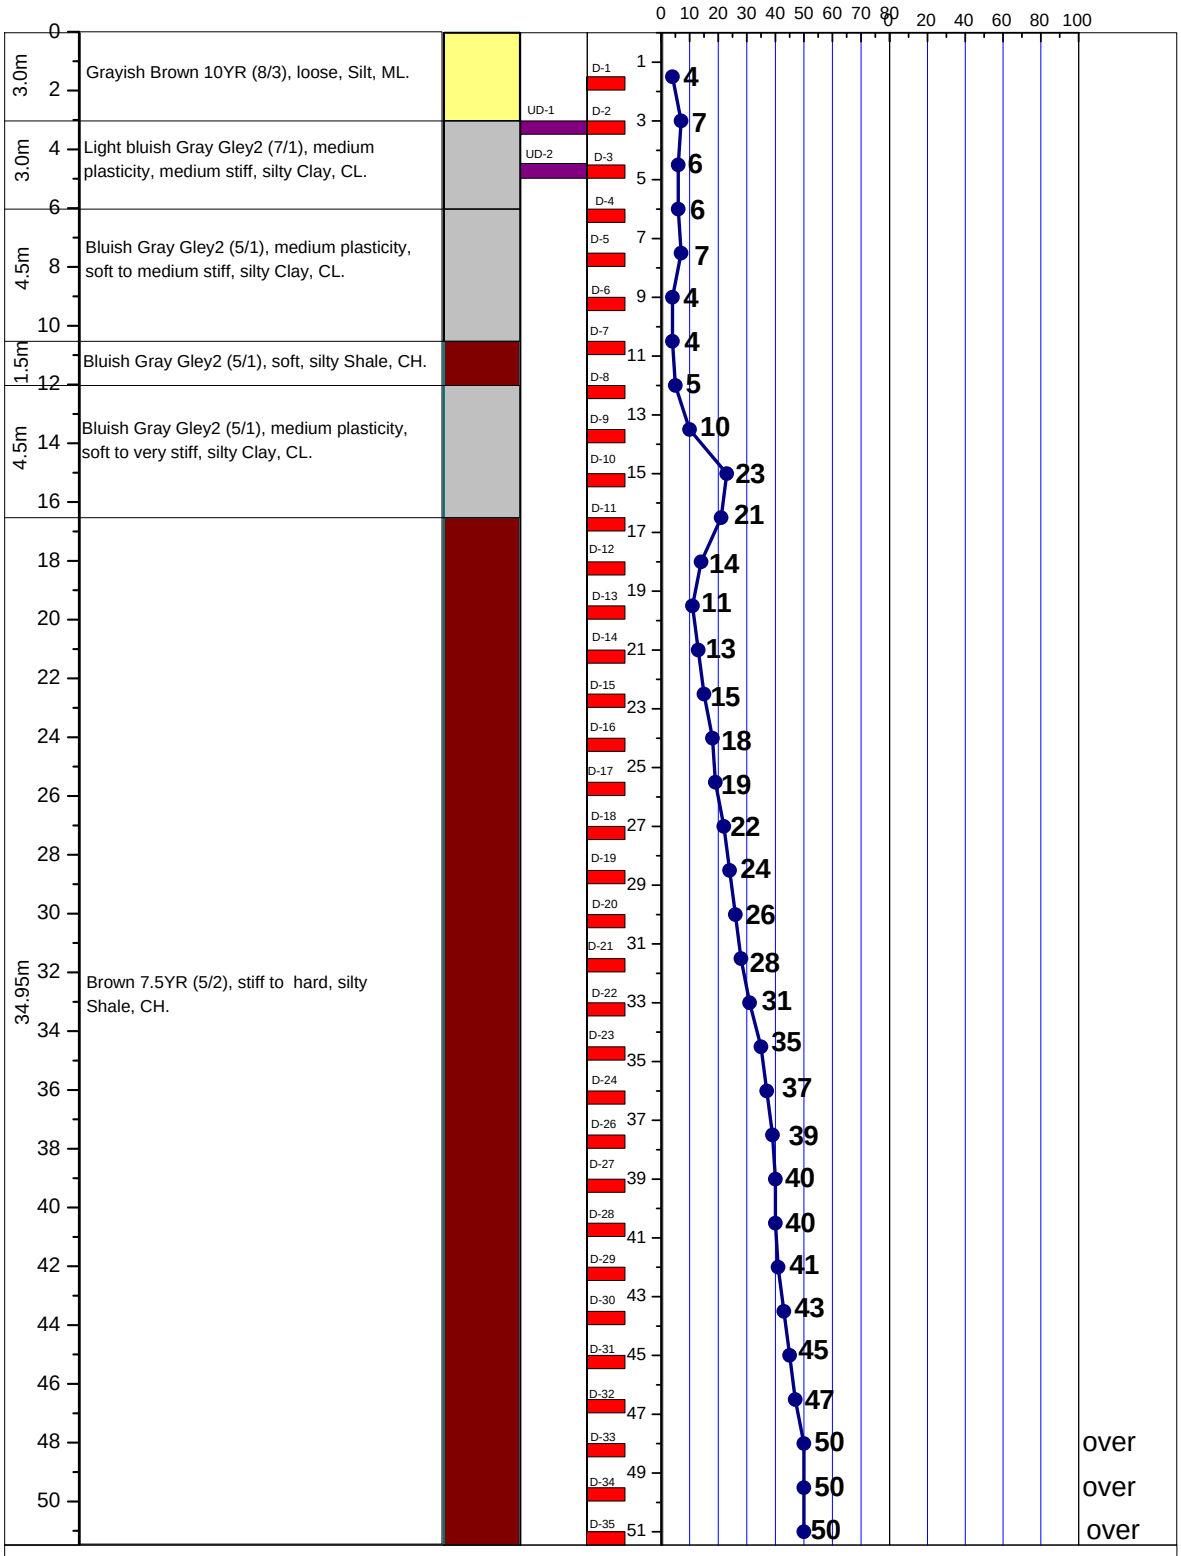


LEGEND FOR BORELOG AND GRAIN SIZE DISTRIBUTION (BASED ON 'ASTM CLASSIFICATION D-2487')

PLASTIC CLAY	SILT	PEAT/HIGHLY ORGANIC SOIL	UNDISTURBED SAMPLE
MICACEOUS FINE SAND/SILT	SAND	SHALE	DISTURBED SAMPLE

N- BLOWS DELIVERED PER FOOT BY A 140 LB HAMMER FALLING 30 INCHES

MAX^{m} PENETRATION= 50 BLOWS. AFTER 50 BLOWS PENETRATION DEPTH WERE MEASURED

A2	PROSOIL	BOREHOLE NO: BH-1	
		LOCATION :Doriardighi, Ramu, Cox's Bazar.	
PROJECT : Telecommunication Tower.		DEPTH OF BORING : 51.0m	R. L.: 1.22m below from Road Level.
CLIENT :AXIATA (Bangladesh) Ltd.		DATE OF BORING : 23-04-2010.	G. W. T : 3.66m below from E. G. L.

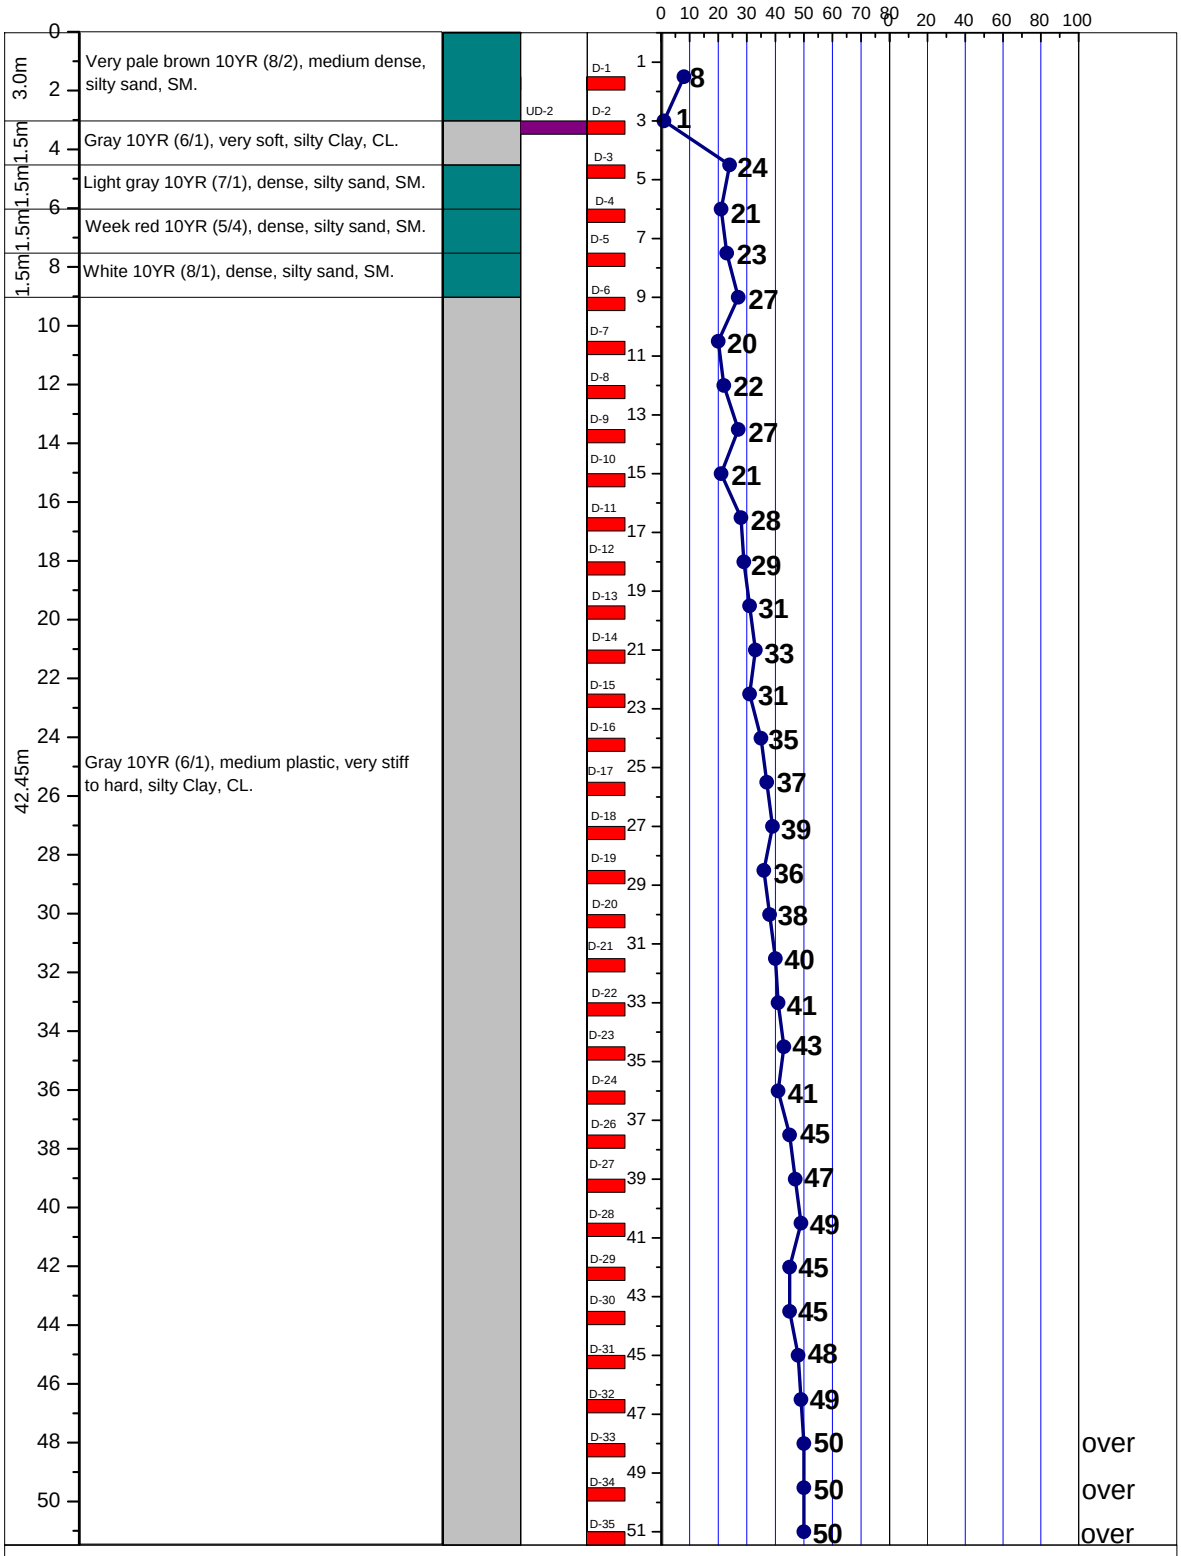


LEGEND FOR BORELOG AND GRAIN SIZE DISTRIBUTION (BASED ON 'ASTM CLASSIFICATION D-2487')

PLASTIC CLAY	SILT	PEAT/HIGHLY ORGANIC SOIL	UNDISTURBED SAMPLE
MICACEOUS FINE SAND/SILT	SAND	SHALE	DISTURBED SAMPLE

N- BLOWS DELIVERED PER FOOT BY A 140 LB HAMMER FALLING 30 INCHES

MAX^{m} PENETRATION= 50 BLOWS. AFTER 50 BLOWS PENETRATION DEPTH WERE MEASURED

A2 PROSOIL	BOREHOLE NO: BH-1	
	LOCATION :Golia Palong, Ramu, Cox's Bazar.	
PROJECT : Telecommunication Tower.	DEPTH OF BORING : 51.0m	R. L.: 1.52m below from Road Level.
CLIENT :AXIATA (Bangladesh) Ltd.	DATE OF BORING : 20-04-2010.	G. W. T : 3.96m below from E. G. L.

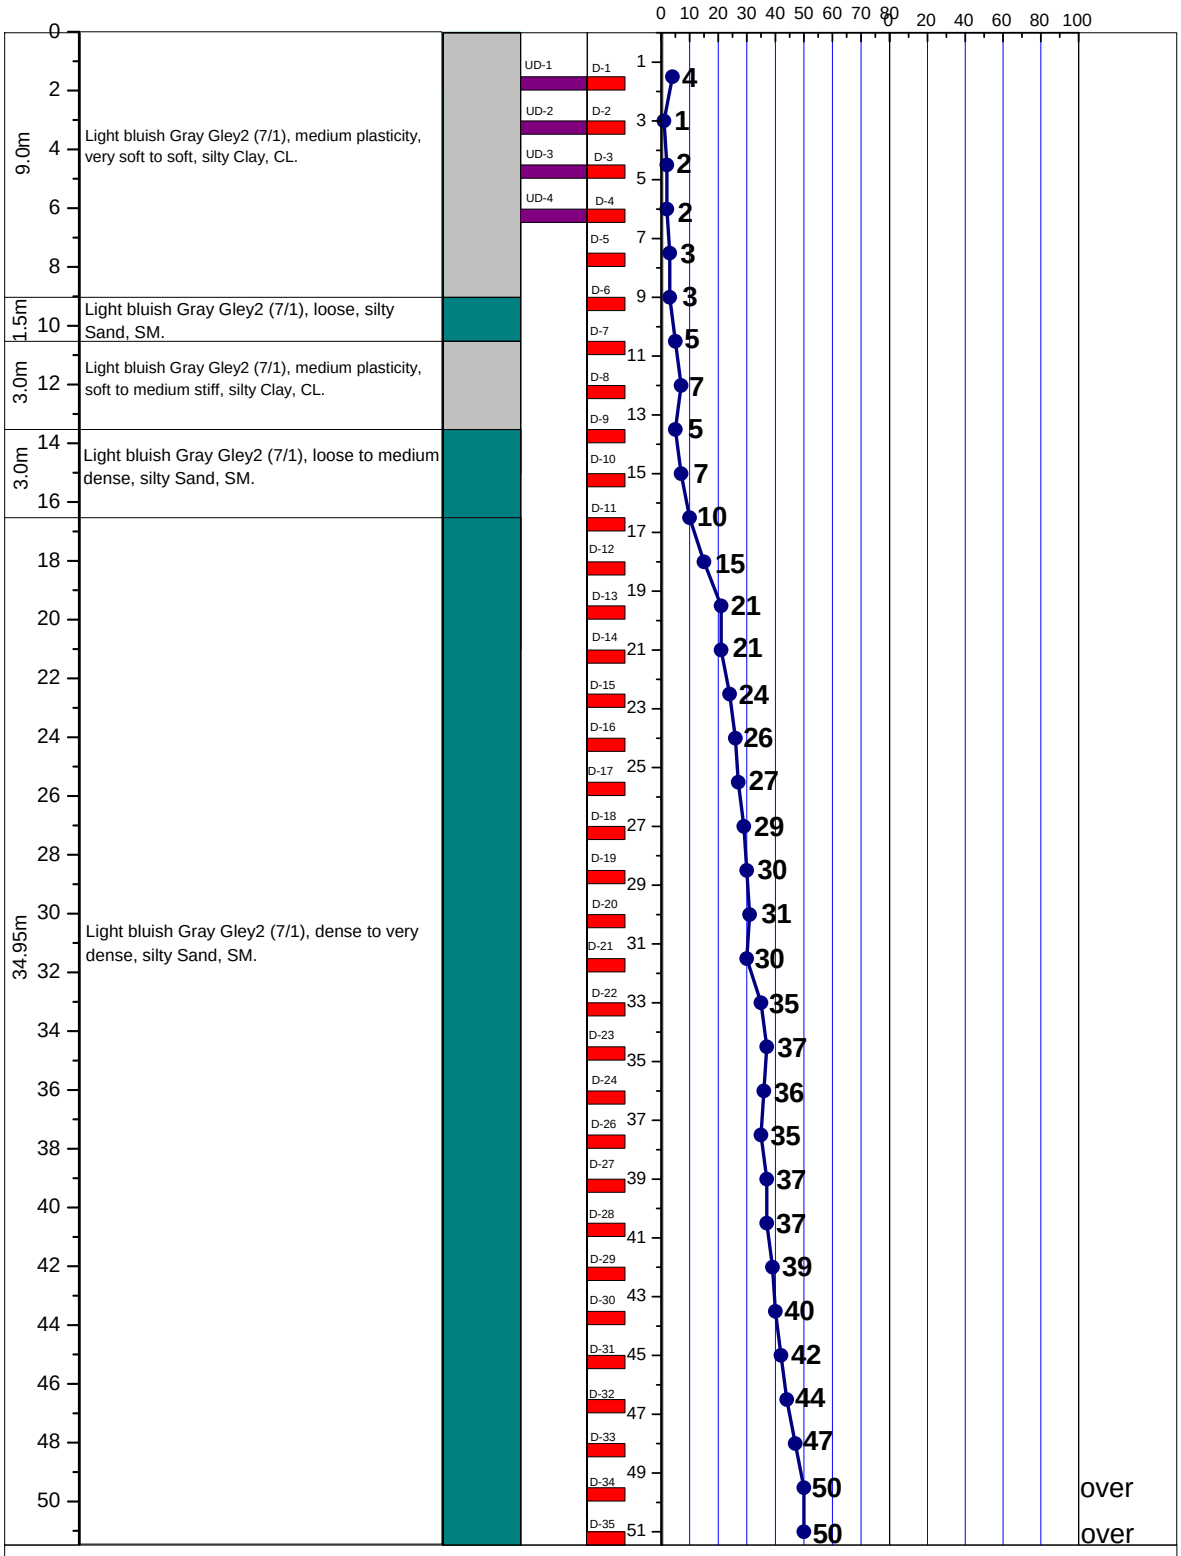


LEGEND FOR BORELOG AND GRAIN SIZE DISTRIBUTION (BASED ON 'ASTM CLASSIFICATION D-2487')

PLASTIC CLAY	SILT	PEAT/HIGHLY ORGANIC SOIL	UNDISTURBED SAMPLE
MICACEOUS FINE SAND/SILT	SAND	SHALE	DISTURBED SAMPLE

N- BLOWS DELIVERED PER FOOT BY A 140 LB HAMMER FALLING 30 INCHES

MAX^{m} PENETRATION= 50 BLOWS. AFTER 50 BLOWS PENETRATION DEPTH WERE MEASURED

A2	PROSOIL	BOREHOLE NO: BH-1	
		LOCATION :Sonadia, Gotibazar, Moheskhali, Cox's Bazar.	
PROJECT : Telecommunication Tower.		DEPTH OF BORING : 51.0m	R. L.: 0.46m above from Road Level.
CLIENT :AXIATA (Bangladesh) Ltd.		DATE OF BORING : 27-05-2010.	G. W. T : 1.52m below from E. G. L.

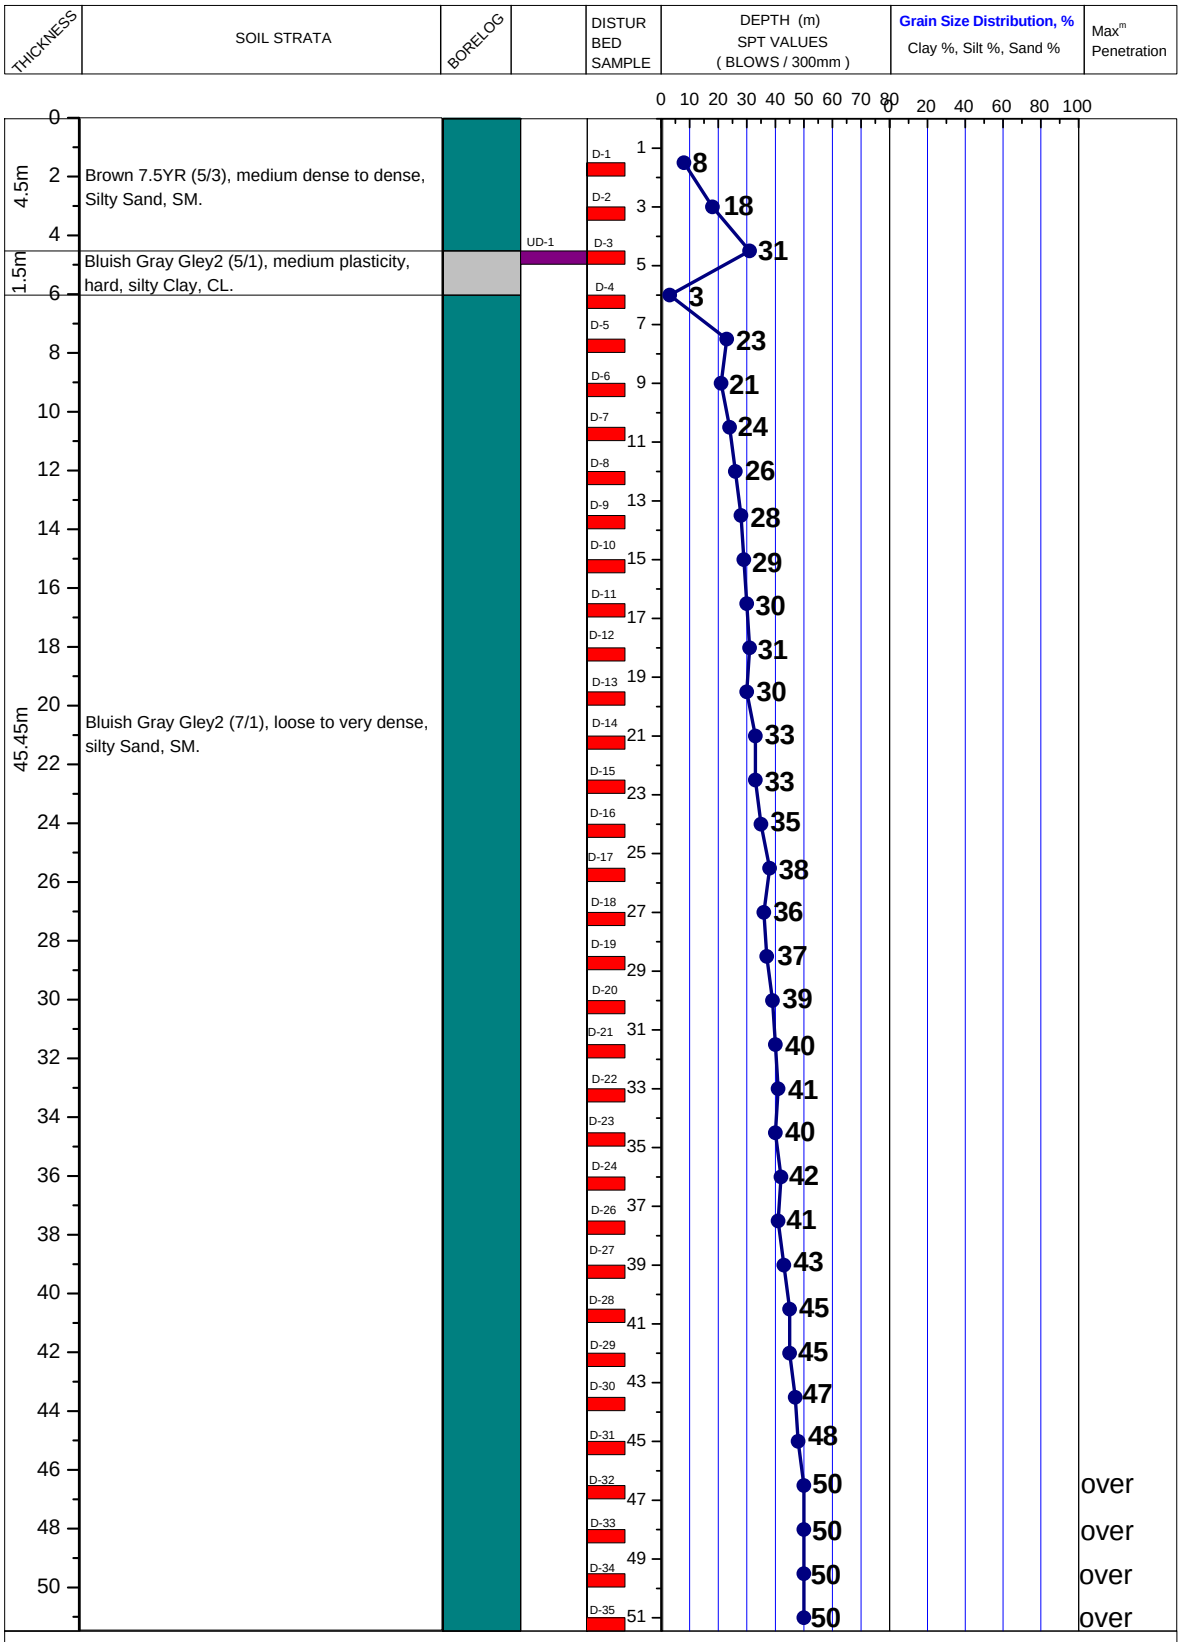

LEGEND FOR BORELOG AND GRAIN SIZE DISTRIBUTION (BASED ON 'ASTM CLASSIFICATION D-2487')

PLASTIC CLAY	SILT	PEAT/HIGHLY ORGANIC SOIL	UNDISTURBED SAMPLE
MICACEOUS FINE SAND/SILT	SAND	SHALE	DISTURBED SAMPLE

N- BLOWS DELIVERED PER FOOT BY A 140 LB HAMMER FALLING 30 INCHES

MAX^{m} PENETRATION= 50 BLOWS. AFTER 50 BLOWS PENETRATION DEPTH WERE MEASURED

A2 PROSOIL	BOREHOLE NO: BH-1	
	LOCATION :Kona Khali, Banglabazar, Chokoria.	
PROJECT : Telecommunication Tower.	DEPTH OF BORING : 51.0m	R. L.: On Road Level.
CLIENT :AXIATA (Bangladesh) Ltd.	DATE OF BORING : 23-04-2010.	G. W. T : 0.76m below from E. G. L.

THICKNESS	SOIL STRATA	BORELOG	DISTURBED SAMPLE	DEPTH (m) SPT VALUES (BLOWS / 300mm)	Grain Size Distribution, % Clay %, Silt %, Sand %	Max^{m} Penetration
4.5m	Very pale Brown 10YR (7/3), medium plasticity, very soft, silty Clay, CL.		UD-1, UD-2, D-1 to D-5	1, 1, 1, 3, 4		
3.0m	Light bluish Gray Gley2 (7/1), very loose to loose, Silt, ML.		D-6 to D-9	7, 15, 18, 16		
7.5m	Light bluish Gray Gley2 (7/1), loose to dense, silty Sand, SM.		D-10 to D-14	20, 18, 14, 14, 4		
3.0m	Light bluish Gray Gley2 (7/1), medium plasticity, very stiff, silty Clay, CL.		D-15 to D-19	14, 19, 21, 20, 24		
33.45m	Light bluish Gray Gley2 (7/1), loose to very dense, silty Sand, SM.		D-20 to D-35	27, 26, 28, 28, 30, 31, 35, 34, 36, 37, 39, 40, 43, 45, 48		


LEGEND FOR BORELOG AND GRAIN SIZE DISTRIBUTION (BASED ON 'ASTM CLASSIFICATION D-2487')

PLASTIC CLAY	SILT	PEAT/HIGHLY ORGANIC SOIL	UNDISTURBED SAMPLE
MICACEOUS FINE SAND/SILT	SAND	SHALE	DISTURBED SAMPLE

N- BLOWS DELIVERED PER FOOT BY A 140 LB HAMMER FALLING 30 INCHES

MAX^{m} PENETRATION= 50 BLOWS. AFTER 50 BLOWS PENETRATION DEPTH WERE MEASURED

A2 PROSOIL	BOREHOLE NO: BH-1	
	LOCATION : Kutubjoom, Bottali, Moheshkhali, Cox's Bazar.	
PROJECT : Telecommunication Tower.	DEPTH OF BORING : 51.0m	R. L.: 0.60m above from Road Level.
CLIENT : AXIATA (Bangladesh) Ltd.	DATE OF BORING : 12-10-2009.	G. W. T : 2.10m below from E. G. L.

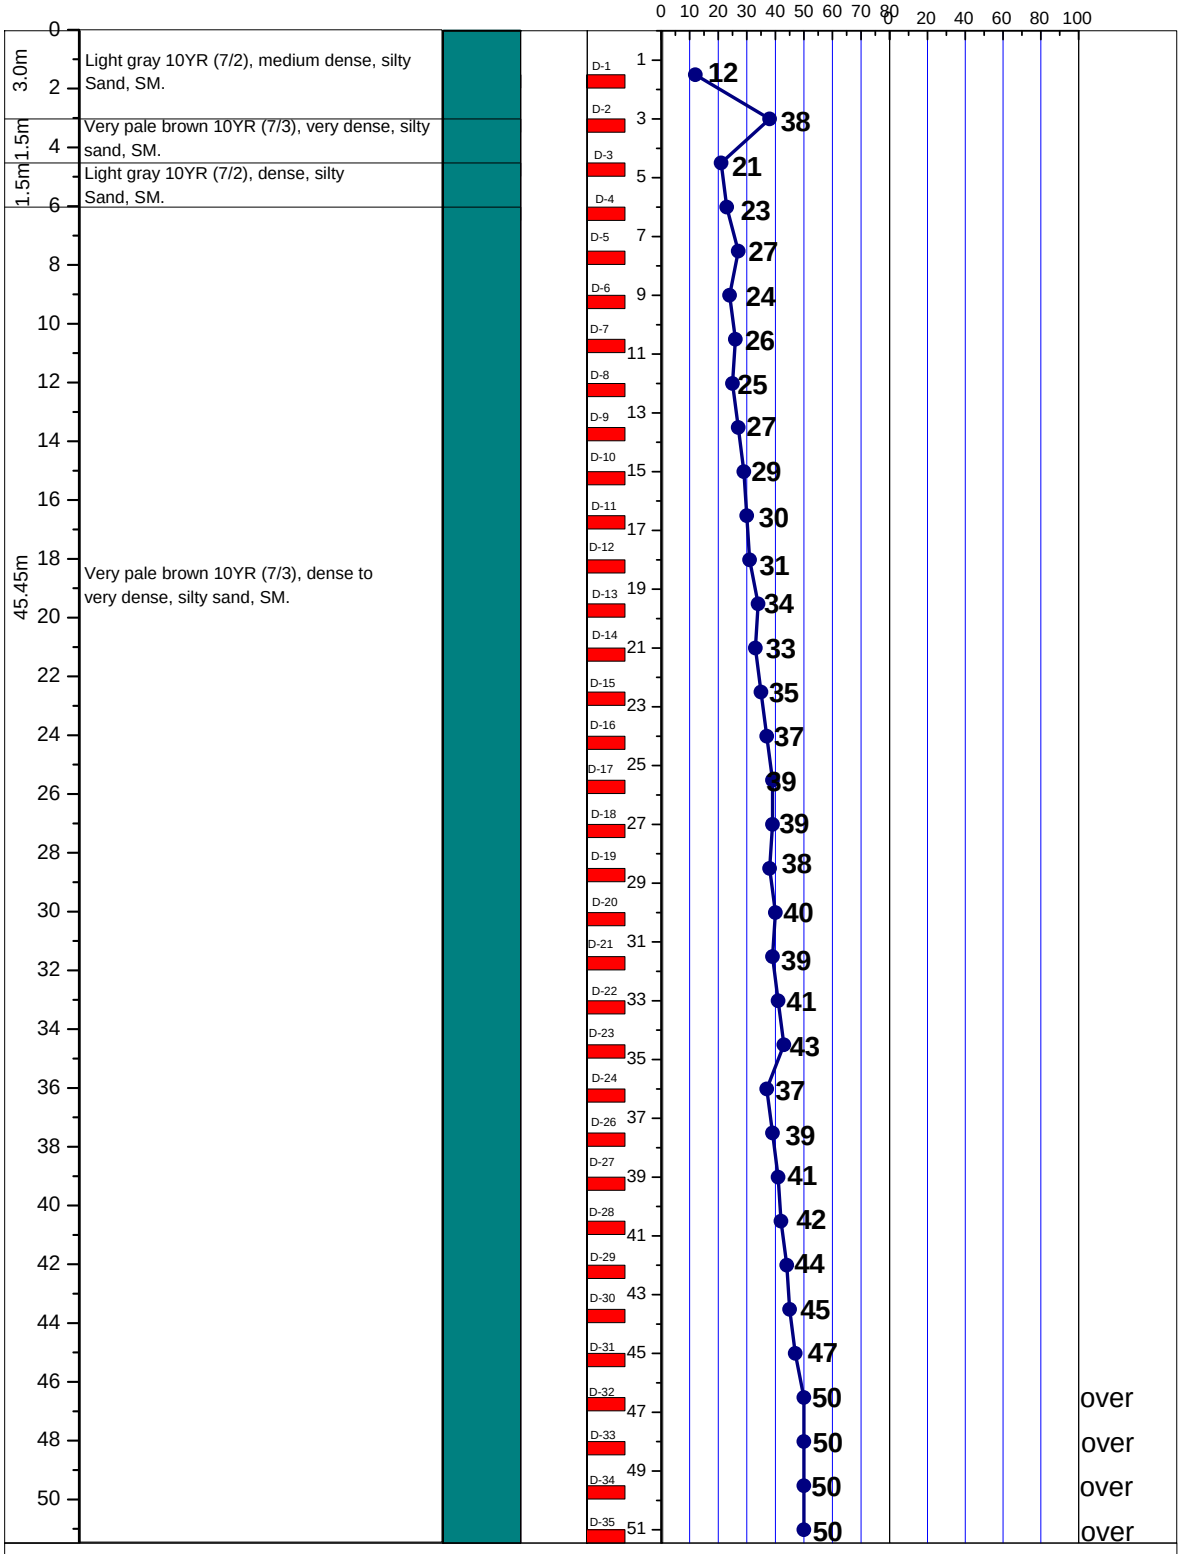


LEGEND FOR BORELOG AND GRAIN SIZE DISTRIBUTION (BASED ON 'ASTM CLASSIFICATION D-2487')

PLASTIC CLAY	SILT	PEAT/HIGHLY ORGANIC SOIL	UNDISTURBED SAMPLE
MICACEOUS FINE SAND/SILT	SAND	SHALE	DISTURBED SAMPLE

N- BLOWS DELIVERED PER FOOT BY A 140 LB HAMMER FALLING 30 INCHES

MAX^{m} PENETRATION= 50 BLOWS. AFTER 50 BLOWS PENETRATION DEPTH WERE MEASURED

A2 PROSOIL	BOREHOLE NO: BH-1	
	LOCATION : Manikpur, Chokoria, Cox's Bazar.	
PROJECT : Telecommunication Tower.	DEPTH OF BORING : 51.0m	R. L.: 0.30m below from Road Level.
CLIENT : AXIATA (Bangladesh) Ltd.	DATE OF BORING : 14-09-2009.	G. W. T : 0.45m below from E. G. L.

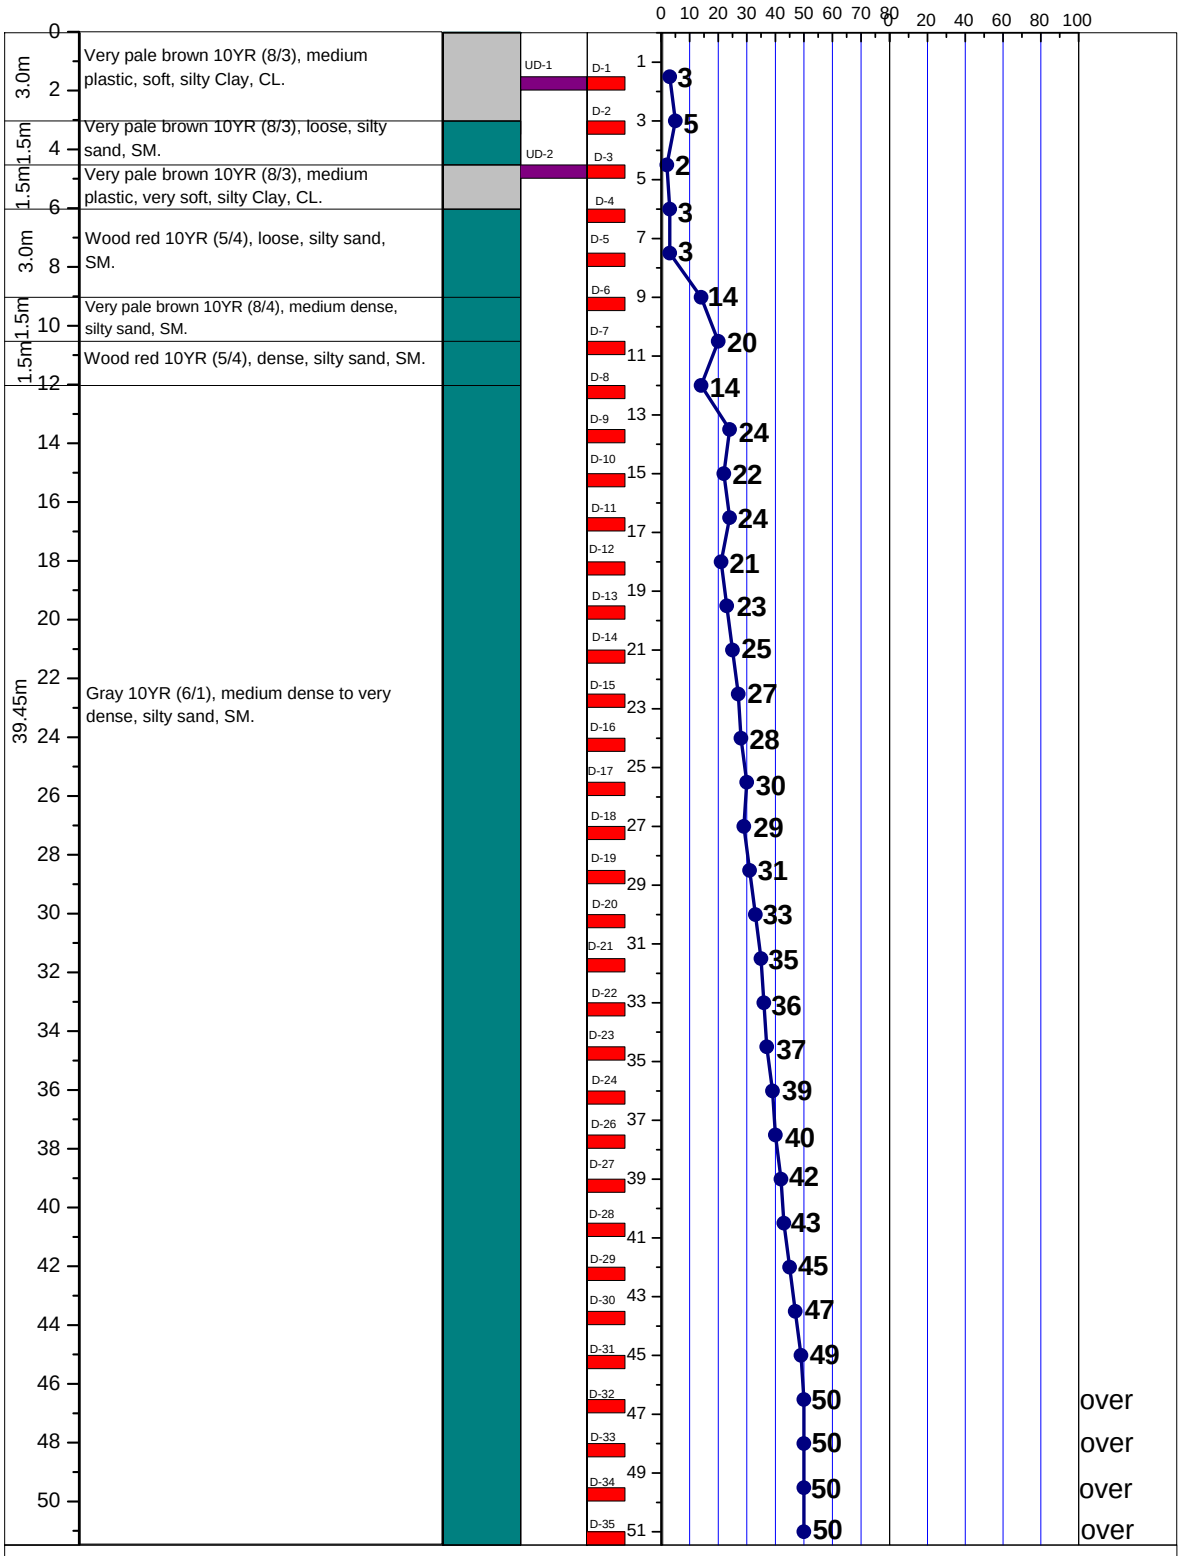


LEGEND FOR BORELOG AND GRAIN SIZE DISTRIBUTION (BASED ON 'ASTM CLASSIFICATION D-2487')

PLASTIC CLAY	SILT	PEAT/HIGHLY ORGANIC SOIL	UNDISTURBED SAMPLE
MICACEOUS FINE SAND/SILT	SAND	SHALE	DISTURBED SAMPLE

N- BLOWS DELIVERED PER FOOT BY A 140 LB HAMMER FALLING 30 INCHES

MAX^{m} PENETRATION= 50 BLOWS. AFTER 50 BLOWS PENETRATION DEPTH WERE MEASURED

A2	PROSOIL	BOREHOLE NO: BH-1	
		LOCATION : North Shilkhali, Teknaf, Cox's Bazar.	
PROJECT : Telecommunication Tower.		DEPTH OF BORING : 51.0m	R. L.: 0.61m below from Road Level.
CLIENT : AXIATA (Bangladesh) Ltd.		DATE OF BORING : 11-05-2010.	G. W. T : 2.13m below from E. G. L.

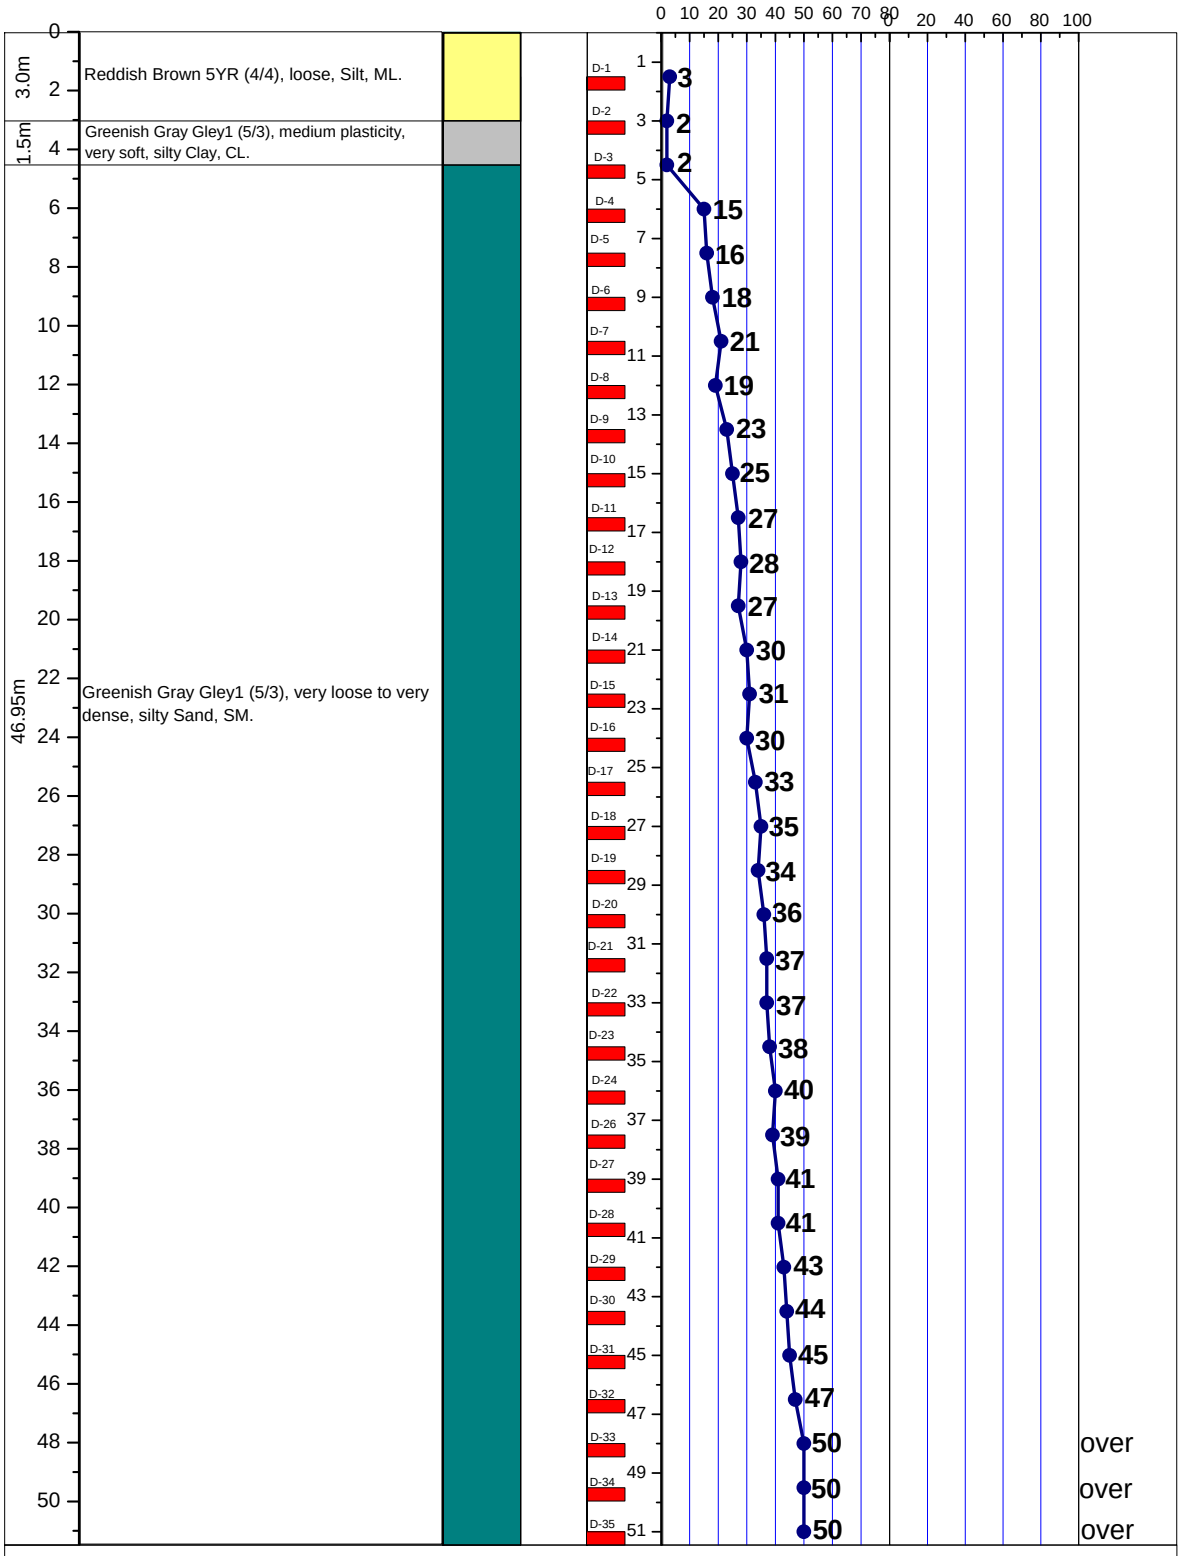


LEGEND FOR BORELOG AND GRAIN SIZE DISTRIBUTION (BASED ON 'ASTM CLASSIFICATION D-2487')

PLASTIC CLAY	SILT	PEAT/HIGHLY ORGANIC SOIL	UNDISTURBED SAMPLE
MICACEOUS FINE SAND/SILT	SAND	SHALE	DISTURBED SAMPLE

N- BLOWS DELIVERED PER FOOT BY A 140 LB HAMMER FALLING 30 INCHES

MAX^{m} PENETRATION= 50 BLOWS. AFTER 50 BLOWS PENETRATION DEPTH WERE MEASURED

A2 PROSOIL	BOREHOLE NO: BH-1	
	LOCATION : Ratna Palong, Ukhia, Cox's Bazar.	
PROJECT : Telecommunication Tower.	DEPTH OF BORING : 51.0m	R. L.: 1.21m below from Road Level.
CLIENT : AXIATA (Bangladesh) Ltd.	DATE OF BORING : 05-10-2009.	G. W. T : 0.07m below from E. G. L.

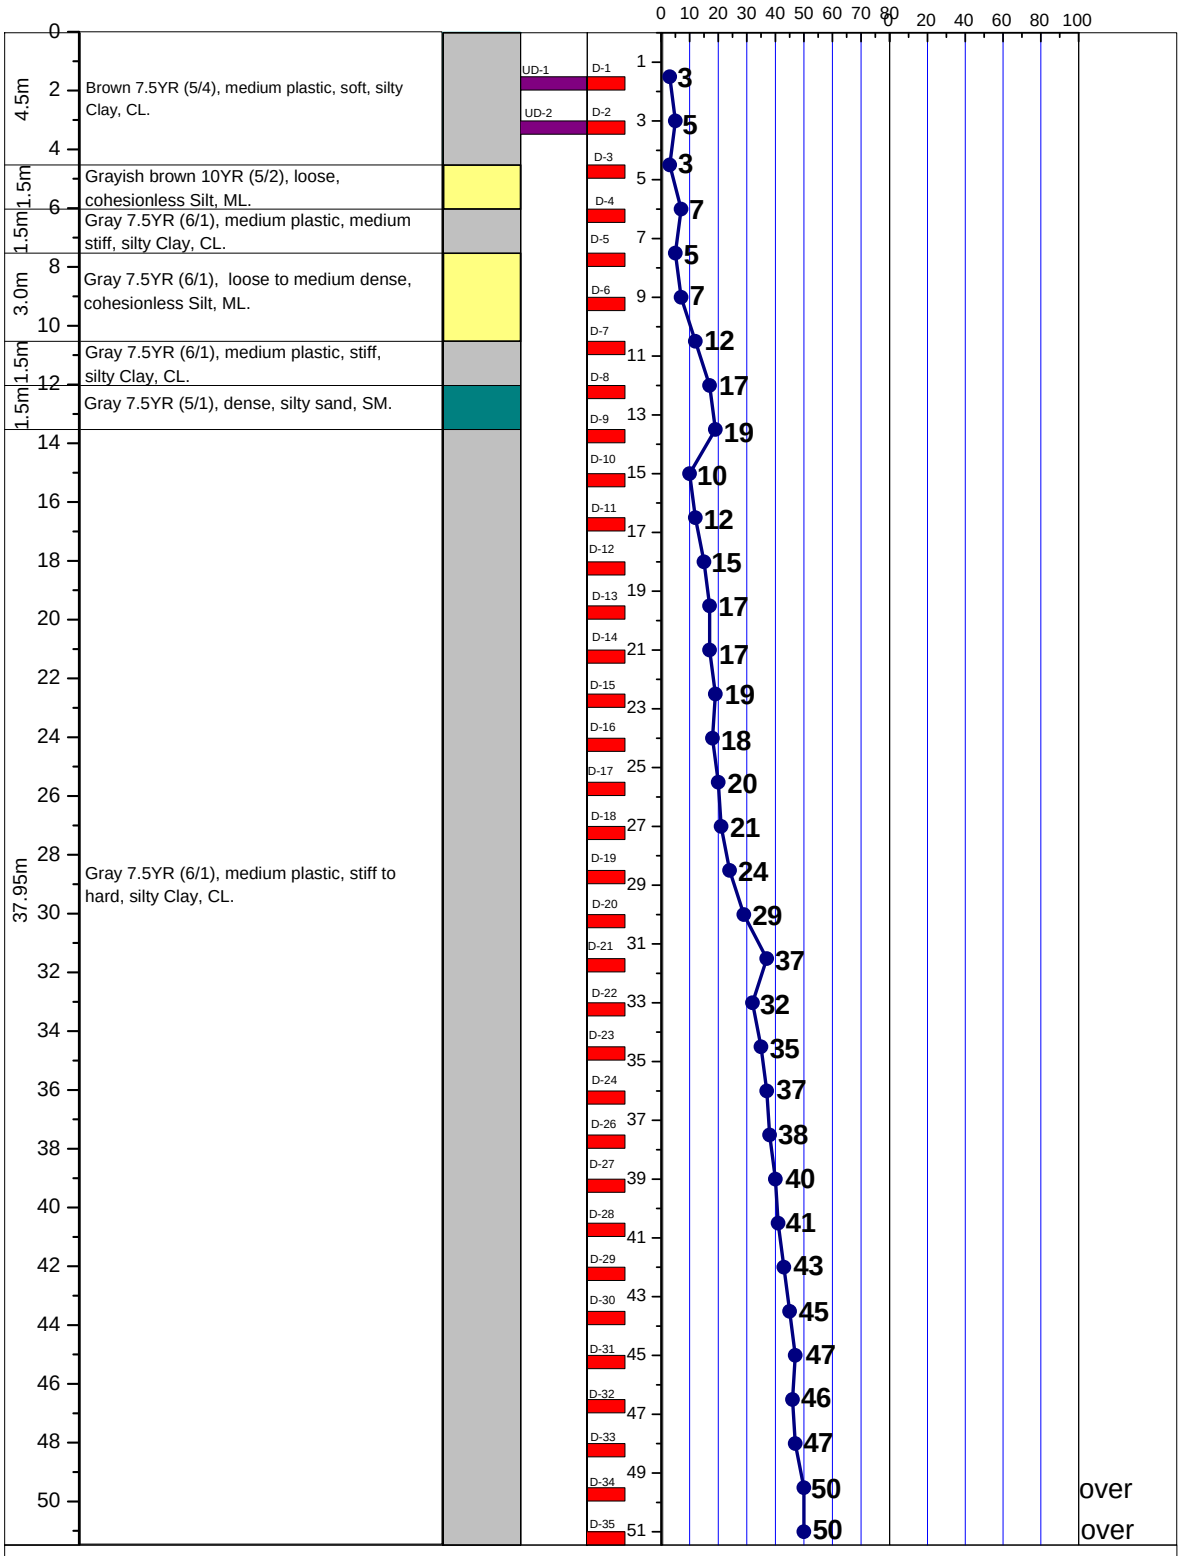


LEGEND FOR BORELOG AND GRAIN SIZE DISTRIBUTION (BASED ON 'ASTM CLASSIFICATION D-2487')

PLASTIC CLAY	SILT	PEAT/HIGHLY ORGANIC SOIL	UNDISTURBED SAMPLE
MICACEOUS FINE SAND/SILT	SAND	SHALE	DISTURBED SAMPLE

N- BLOWS DELIVERED PER FOOT BY A 140 LB HAMMER FALLING 30 INCHES

MAX^{m} PENETRATION= 50 BLOWS. AFTER 50 BLOWS PENETRATION DEPTH WERE MEASURED

A2	PROSOIL	BOREHOLE NO: BH-1	
		LOCATION : Sattar Hat, Mazighona, Chokoria, Cox's Bazar.	
PROJECT : Telecommunication Tower.		DEPTH OF BORING : 51.0m	R. L.: 0.61m below from Road Level.
CLIENT : AXIATA (Bangladesh) Ltd.		DATE OF BORING : 04-07-2010.	G. W. T : 1.52m below from E. G. L.

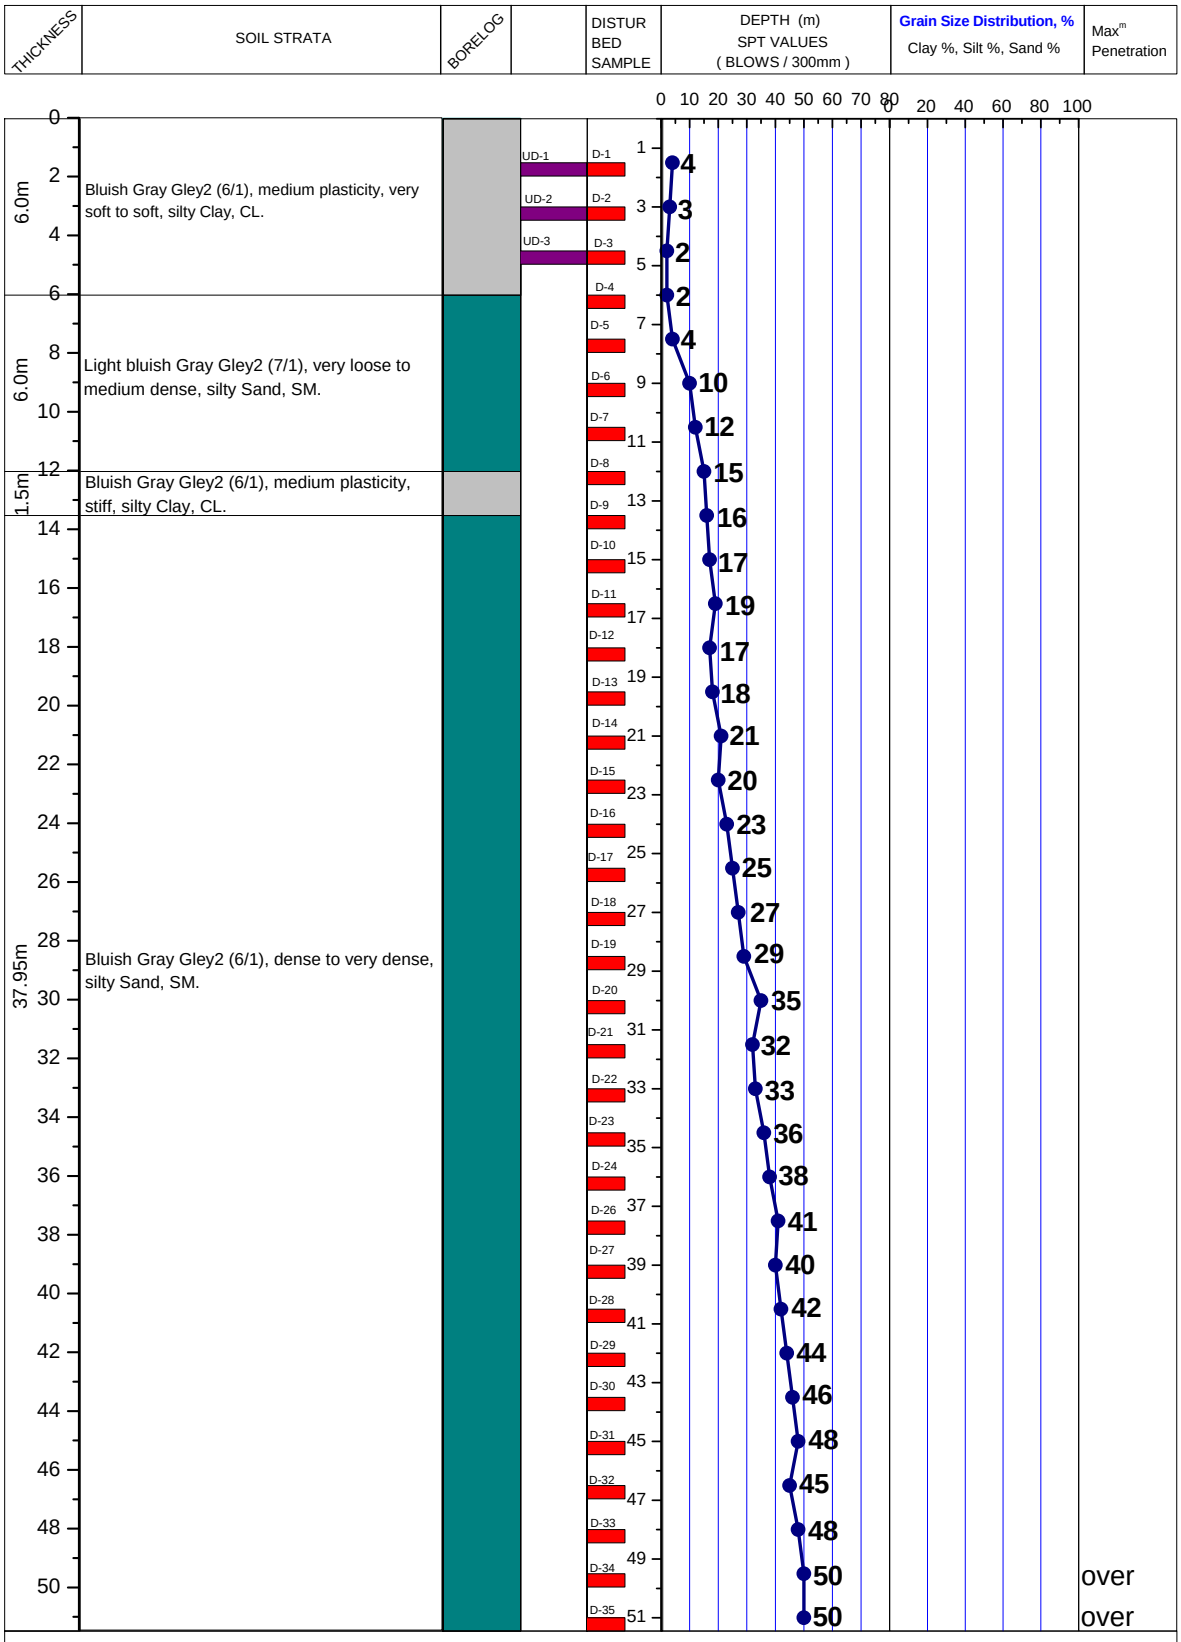


LEGEND FOR BORELOG AND GRAIN SIZE DISTRIBUTION (BASED ON 'ASTM CLASSIFICATION D-2487')

PLASTIC CLAY	SILT	PEAT/HIGHLY ORGANIC SOIL	UNDISTURBED SAMPLE
MICACEOUS FINE SAND/SILT	SAND	SHALE	DISTURBED SAMPLE

N- BLOWS DELIVERED PER FOOT BY A 140 LB HAMMER FALLING 30 INCHES

MAX^{m} PENETRATION= 50 BLOWS. AFTER 50 BLOWS PENETRATION DEPTH WERE MEASURED

A2	PROSOIL	BOREHOLE NO: BH-1	
		LOCATION : Sattar Paishad, Chokoria, Cox's Bazar.	
PROJECT : Telecommunication Tower.		DEPTH OF BORING : 51.0m	R. L.: 0.76m below from Road Level.
CLIENT : AXIATA (Bangladesh) Ltd.		DATE OF BORING : 24-04-2010.	G. W. T : 3.05m below from E. G. L.

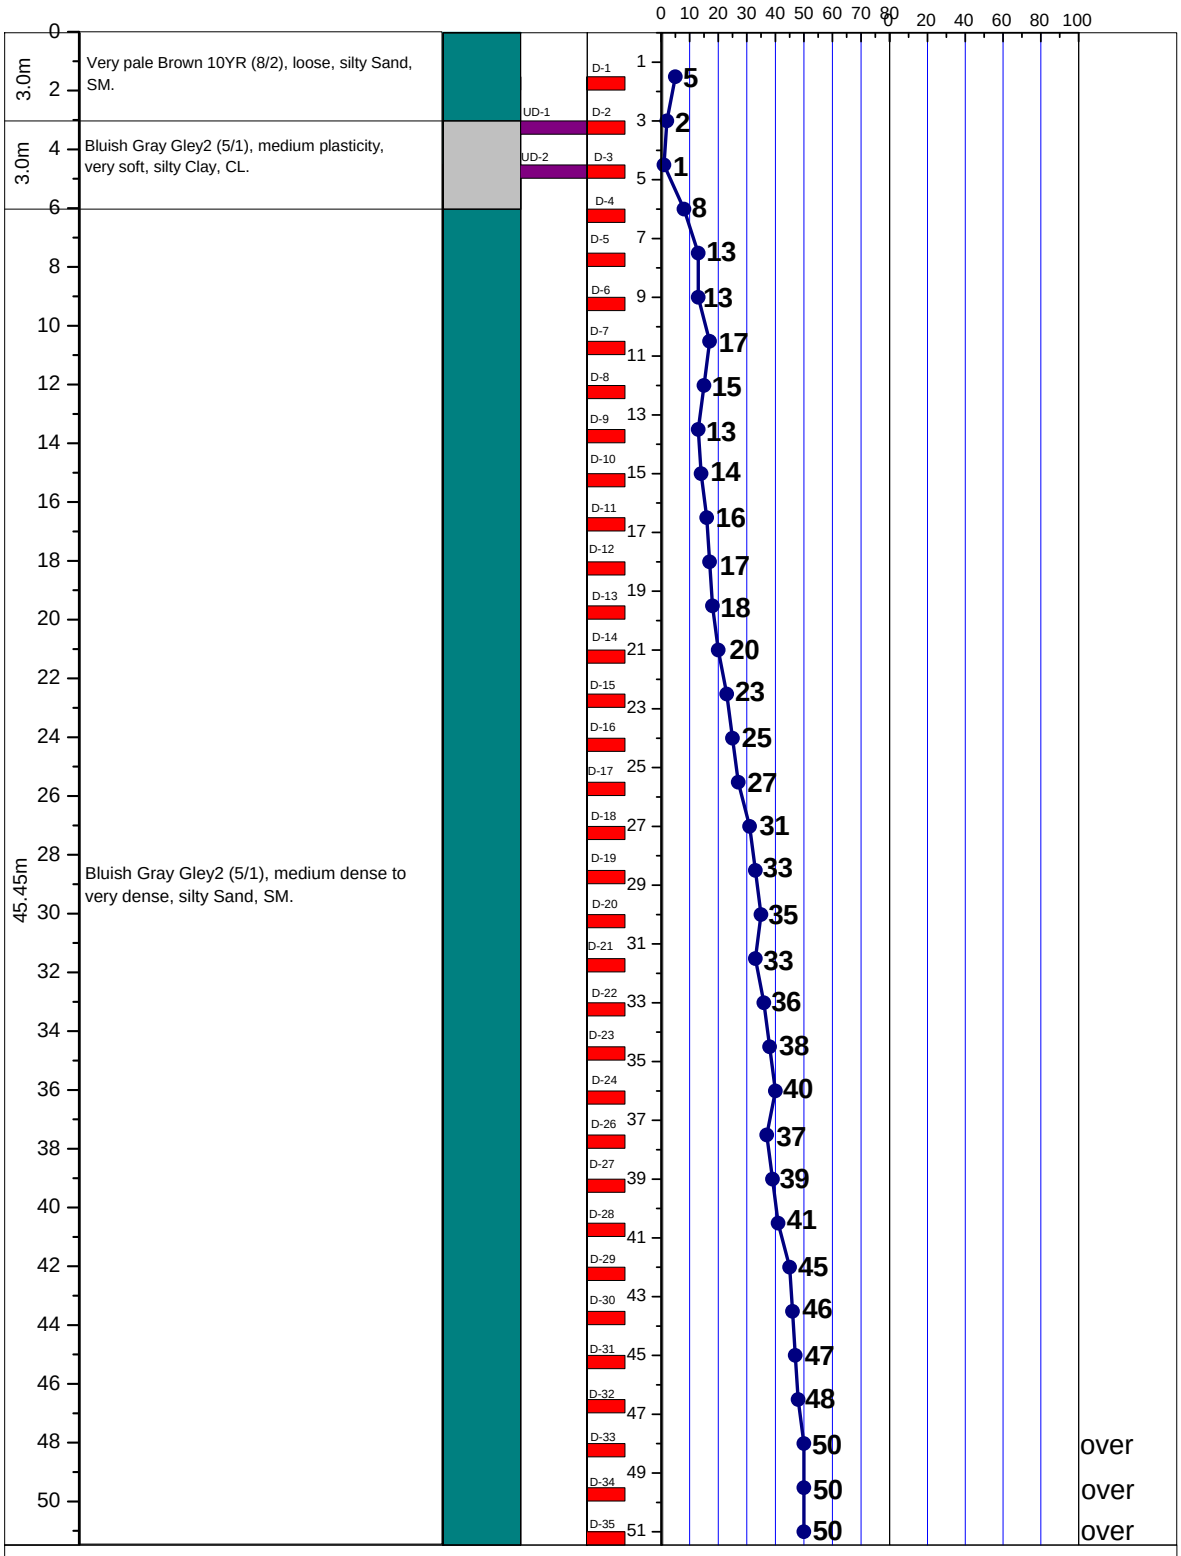


LEGEND FOR BORELOG AND GRAIN SIZE DISTRIBUTION (BASED ON 'ASTM CLASSIFICATION D-2487')

PLASTIC CLAY	SILT	PEAT/HIGHLY ORGANIC SOIL	UNDISTURBED SAMPLE
MICACEOUS FINE SAND/SILT	SAND	SHALE	DISTURBED SAMPLE

N- BLOWS DELIVERED PER FOOT BY A 140 LB HAMMER FALLING 30 INCHES

MAX^{m} PENETRATION= 50 BLOWS. AFTER 50 BLOWS PENETRATION DEPTH WERE MEASURED

A2	PROSOIL	BOREHOLE NO: BH-1	
		LOCATION : Sha Porir Deep, Teknaf, Cox's Bazar.	
PROJECT : Telecommunication Tower.		DEPTH OF BORING : 51.0m	R. L.: 0.61m below from Road Level.
CLIENT : AXIATA (Bangladesh) Ltd.		DATE OF BORING : 11-05-2010.	G. W. T : 2.13m below from E. G. L.

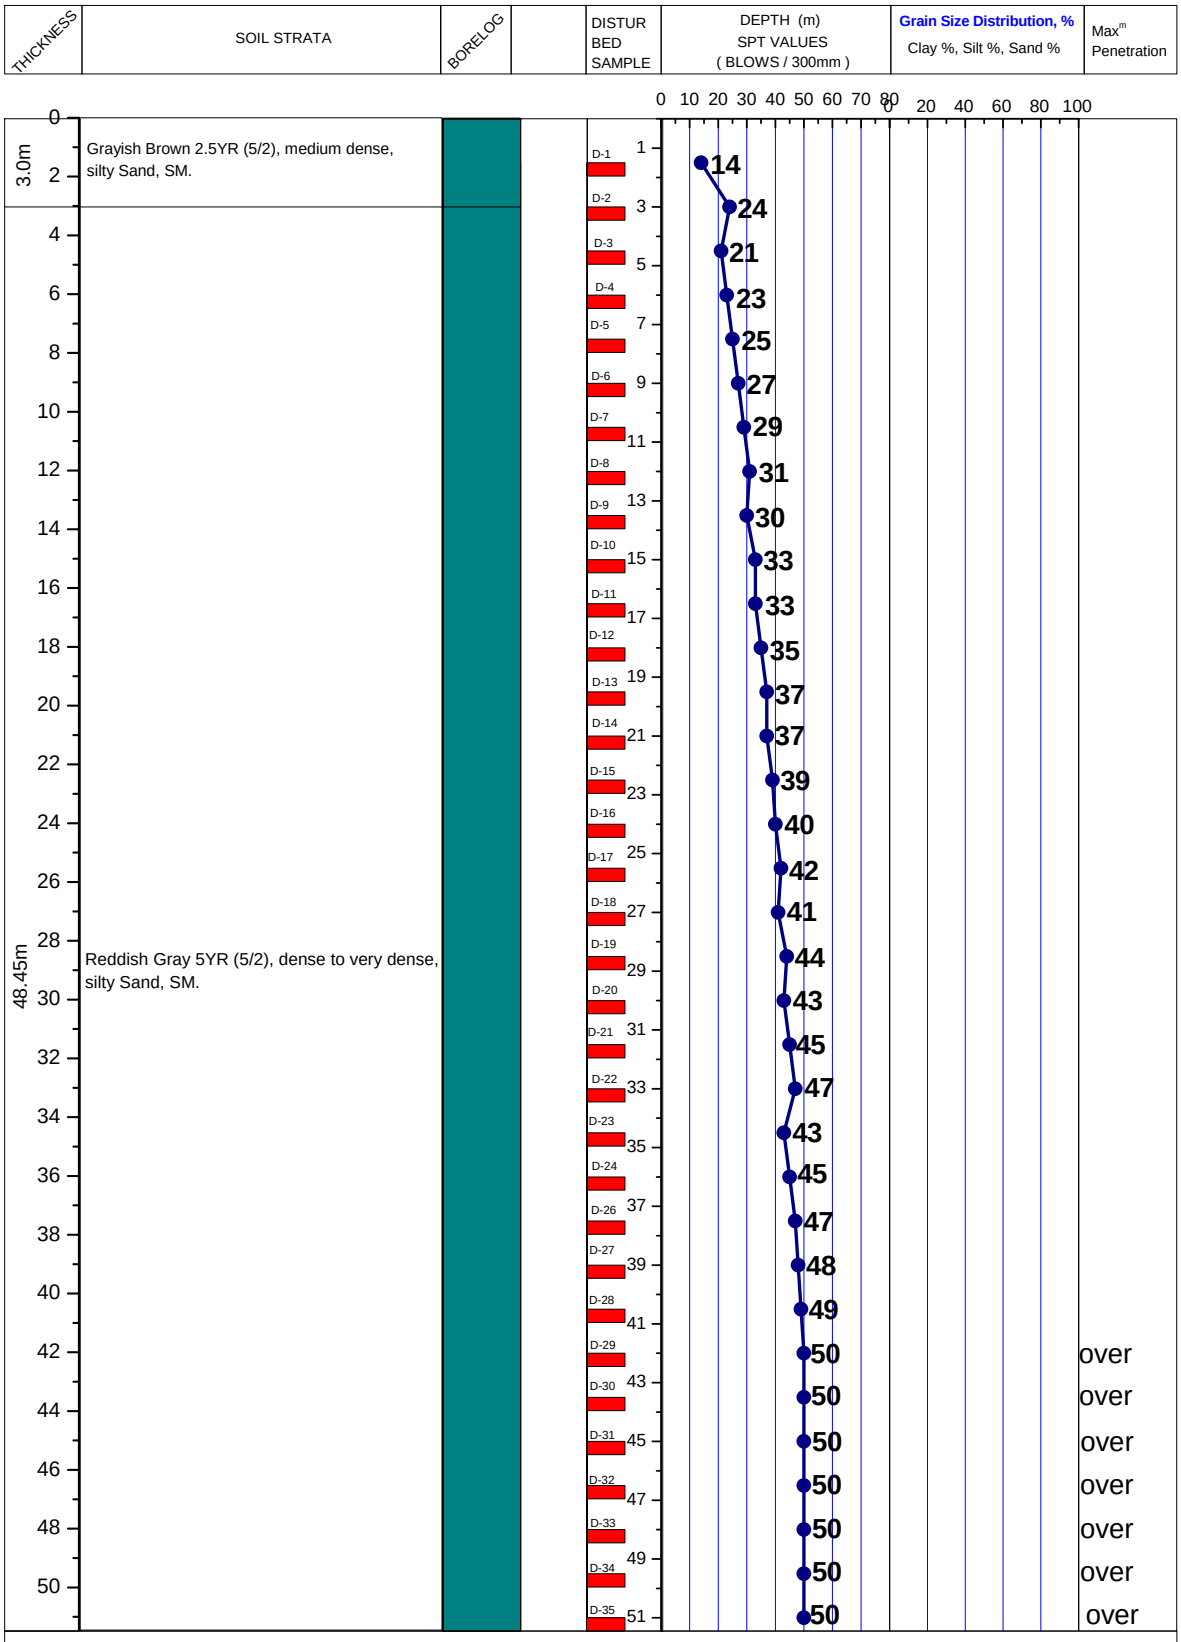


LEGEND FOR BORELOG AND GRAIN SIZE DISTRIBUTION (BASED ON 'ASTM CLASSIFICATION D-2487')

PLASTIC CLAY	SILT	PEAT/HIGHLY ORGANIC SOIL	UNDISTURBED SAMPLE
MICACEOUS FINE SAND/SILT	SAND	SHALE	DISTURBED SAMPLE

N- BLOWS DELIVERED PER FOOT BY A 140 LB HAMMER FALLING 30 INCHES

MAX^{m} PENETRATION= 50 BLOWS. AFTER 50 BLOWS PENETRATION DEPTH WERE MEASURED

A2 PROSOIL	BOREHOLE NO: BH-1	
	LOCATION : Shilkhali Station, Pecua, Cox's Bazar.	
PROJECT : Telecommunication Tower.	DEPTH OF BORING : 51.0m	R. L.: 1.52m below from Road Level.
CLIENT : AXIATA (Bangladesh) Ltd.	DATE OF BORING : 22-04-2010.	G. W. T : 0.61m below from E. G. L.

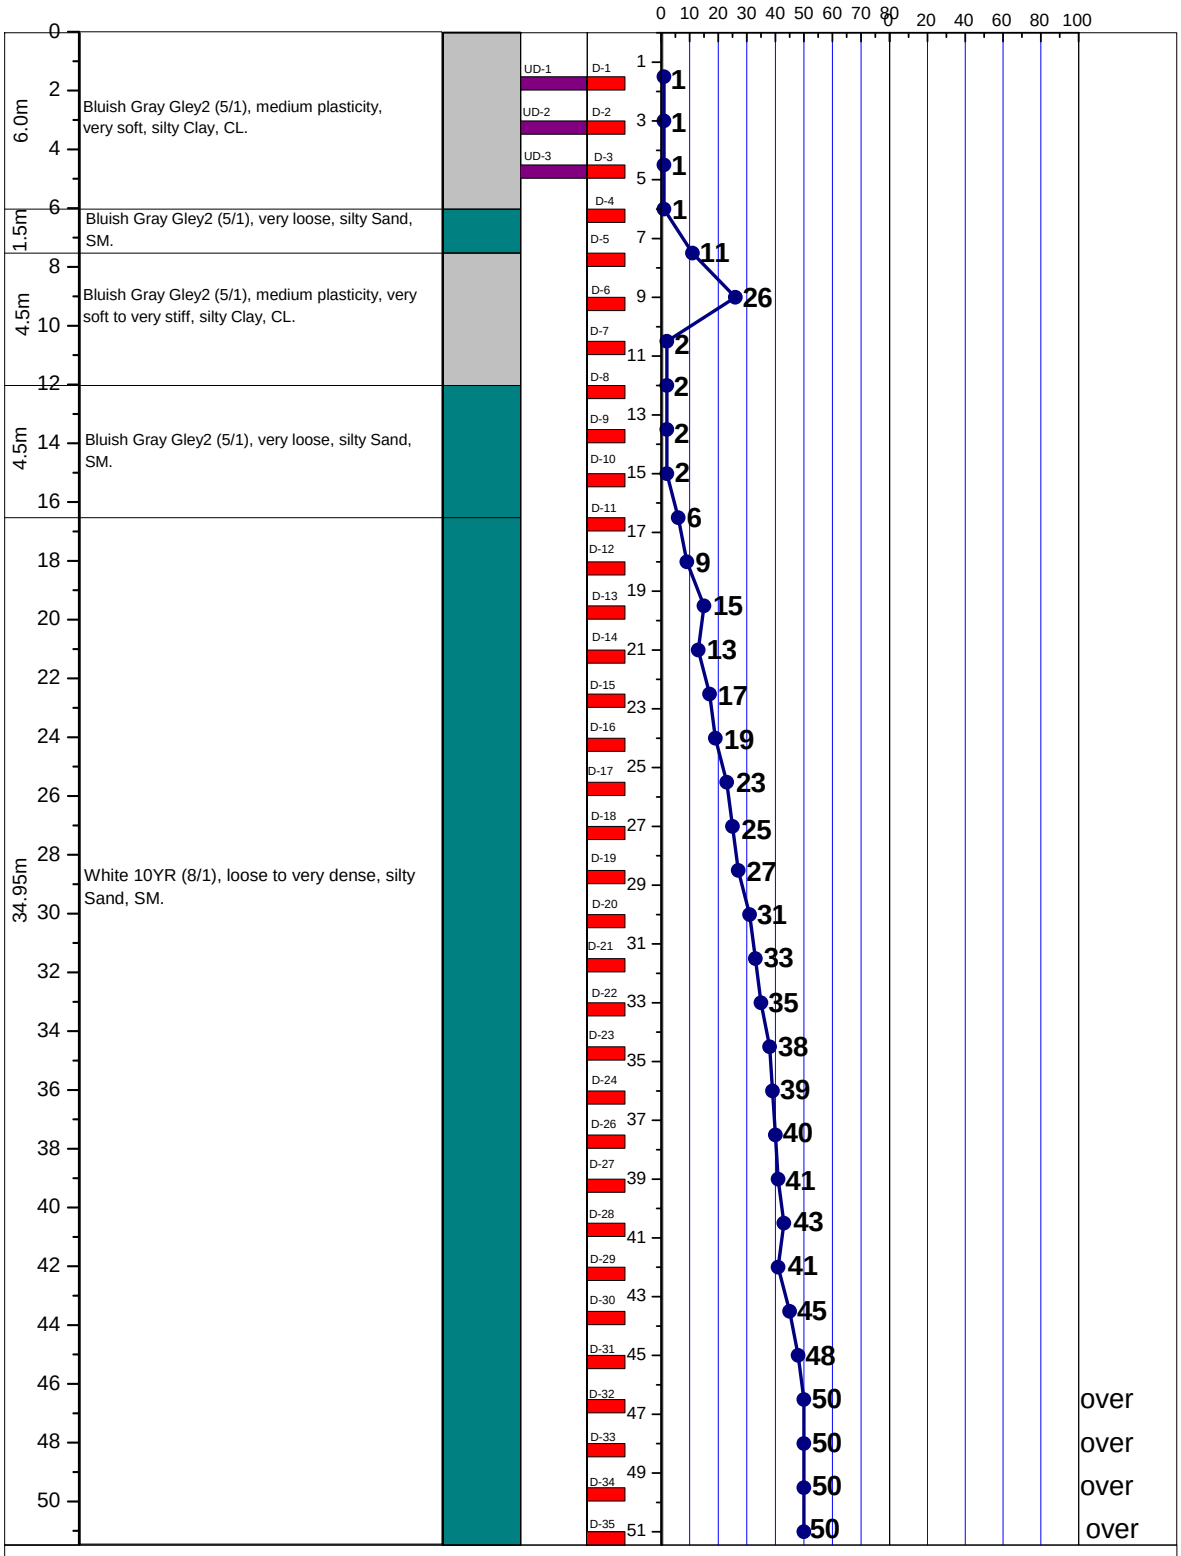


LEGEND FOR BORELOG AND GRAIN SIZE DISTRIBUTION (BASED ON 'ASTM CLASSIFICATION D-2487')

PLASTIC CLAY	SILT	PEAT/HIGHLY ORGANIC SOIL	UNDISTURBED SAMPLE
MICACEOUS FINE SAND/SILT	SAND	SHALE	DISTURBED SAMPLE

N- BLOWS DELIVERED PER FOOT BY A 140 LB HAMMER FALLING 30 INCHES

MAX^{m} PENETRATION= 50 BLOWS. AFTER 50 BLOWS PENETRATION DEPTH WERE MEASURED

A2 PROSOIL	BOREHOLE NO: BH-1	
	LOCATION : Ali Akbar Dail Bazar, Kutubdia, Cox's Bazar.	
PROJECT : Telecommunication Tower.	DEPTH OF BORING : 51.0m	R. L.: 1.52m below from Road Level.
CLIENT : AXIATA (Bangladesh) Ltd.	DATE OF BORING : 23-10-2010.	G. W. T : On E. G. L.

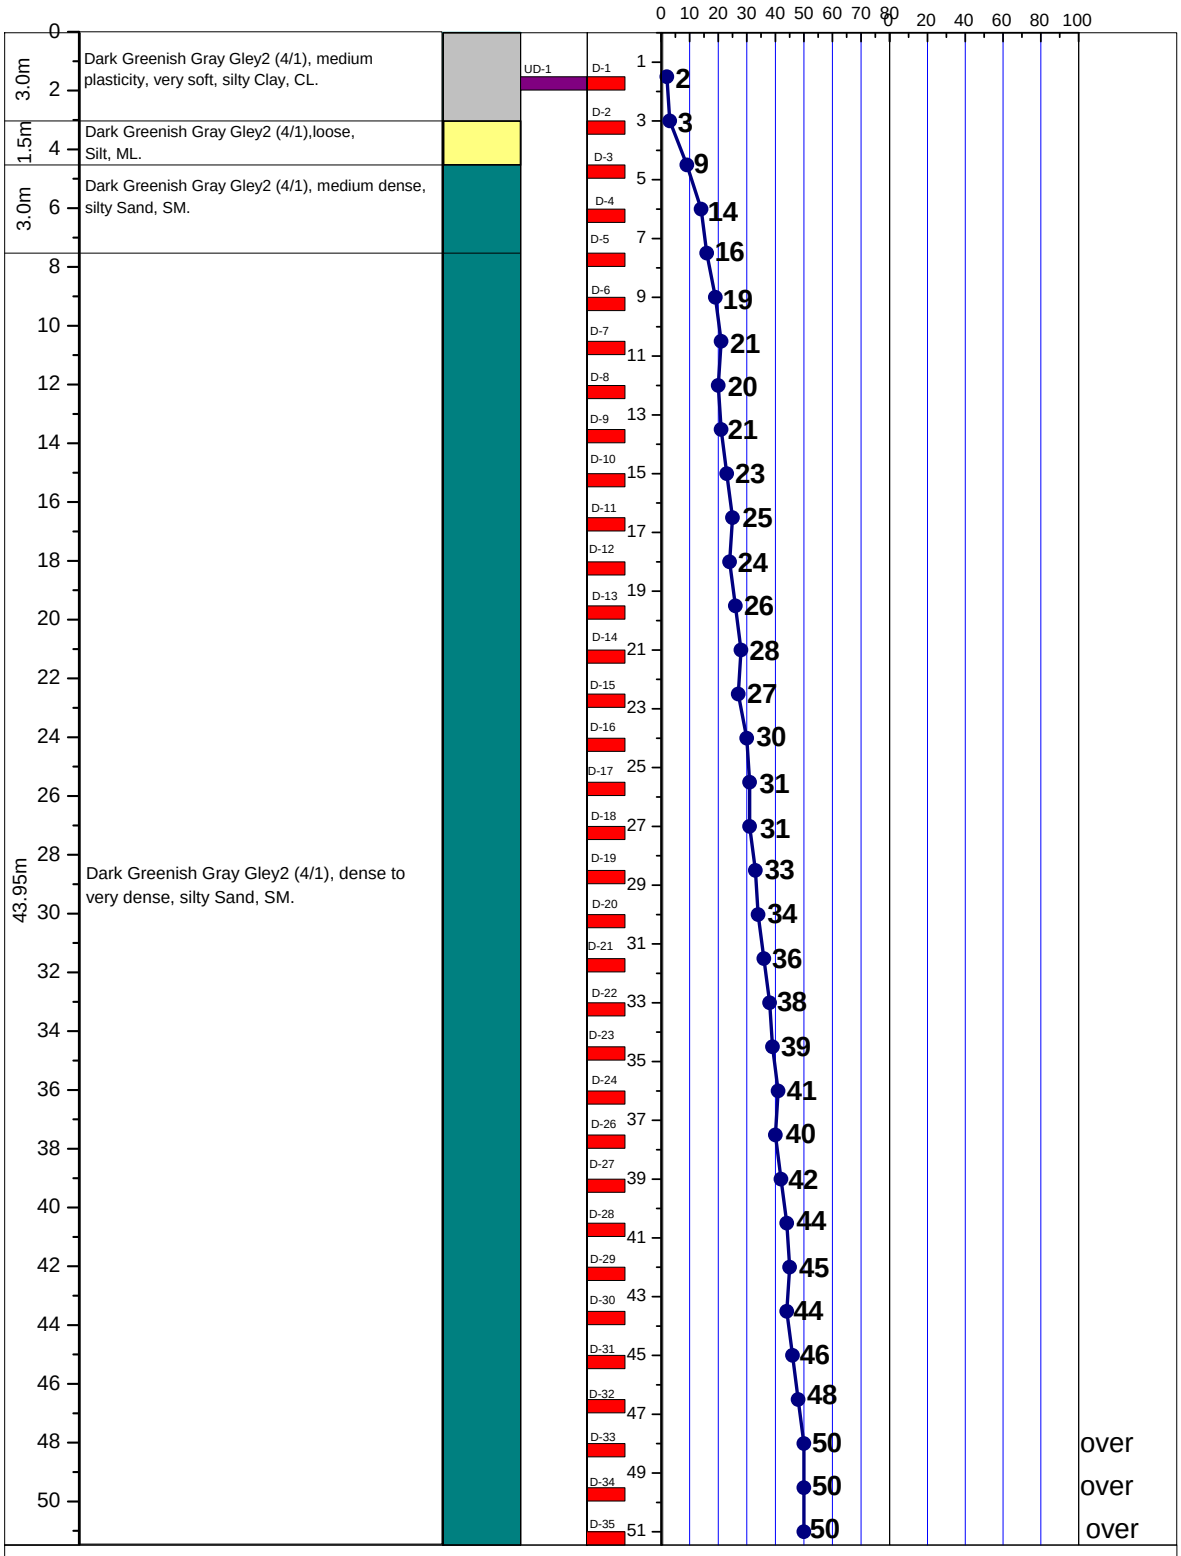


LEGEND FOR BORELOG AND GRAIN SIZE DISTRIBUTION (BASED ON 'ASTM CLASSIFICATION D-2487')

PLASTIC CLAY	SILT	PEAT/HIGHLY ORGANIC SOIL	UNDISTURBED SAMPLE
MICACEOUS FINE SAND/SILT	SAND	SHALE	DISTURBED SAMPLE

N- BLOWS DELIVERED PER FOOT BY A 140 LB HAMMER FALLING 30 INCHES

MAX^{m} PENETRATION= 50 BLOWS. AFTER 50 BLOWS PENETRATION DEPTH WERE MEASURED

A2 PROSOIL	BOREHOLE NO: BH-1	
	LOCATION : Balukkali Pan Bazar, Cox's Bazar.	
PROJECT : Telecommunication Tower.	DEPTH OF BORING : 51.0m	R. L.: 0.30m below from Road Level.
CLIENT : AXIATA (Bangladesh) Ltd.	DATE OF BORING : 20-10-2010.	G. W. T : 0.30m below from E. G. L.

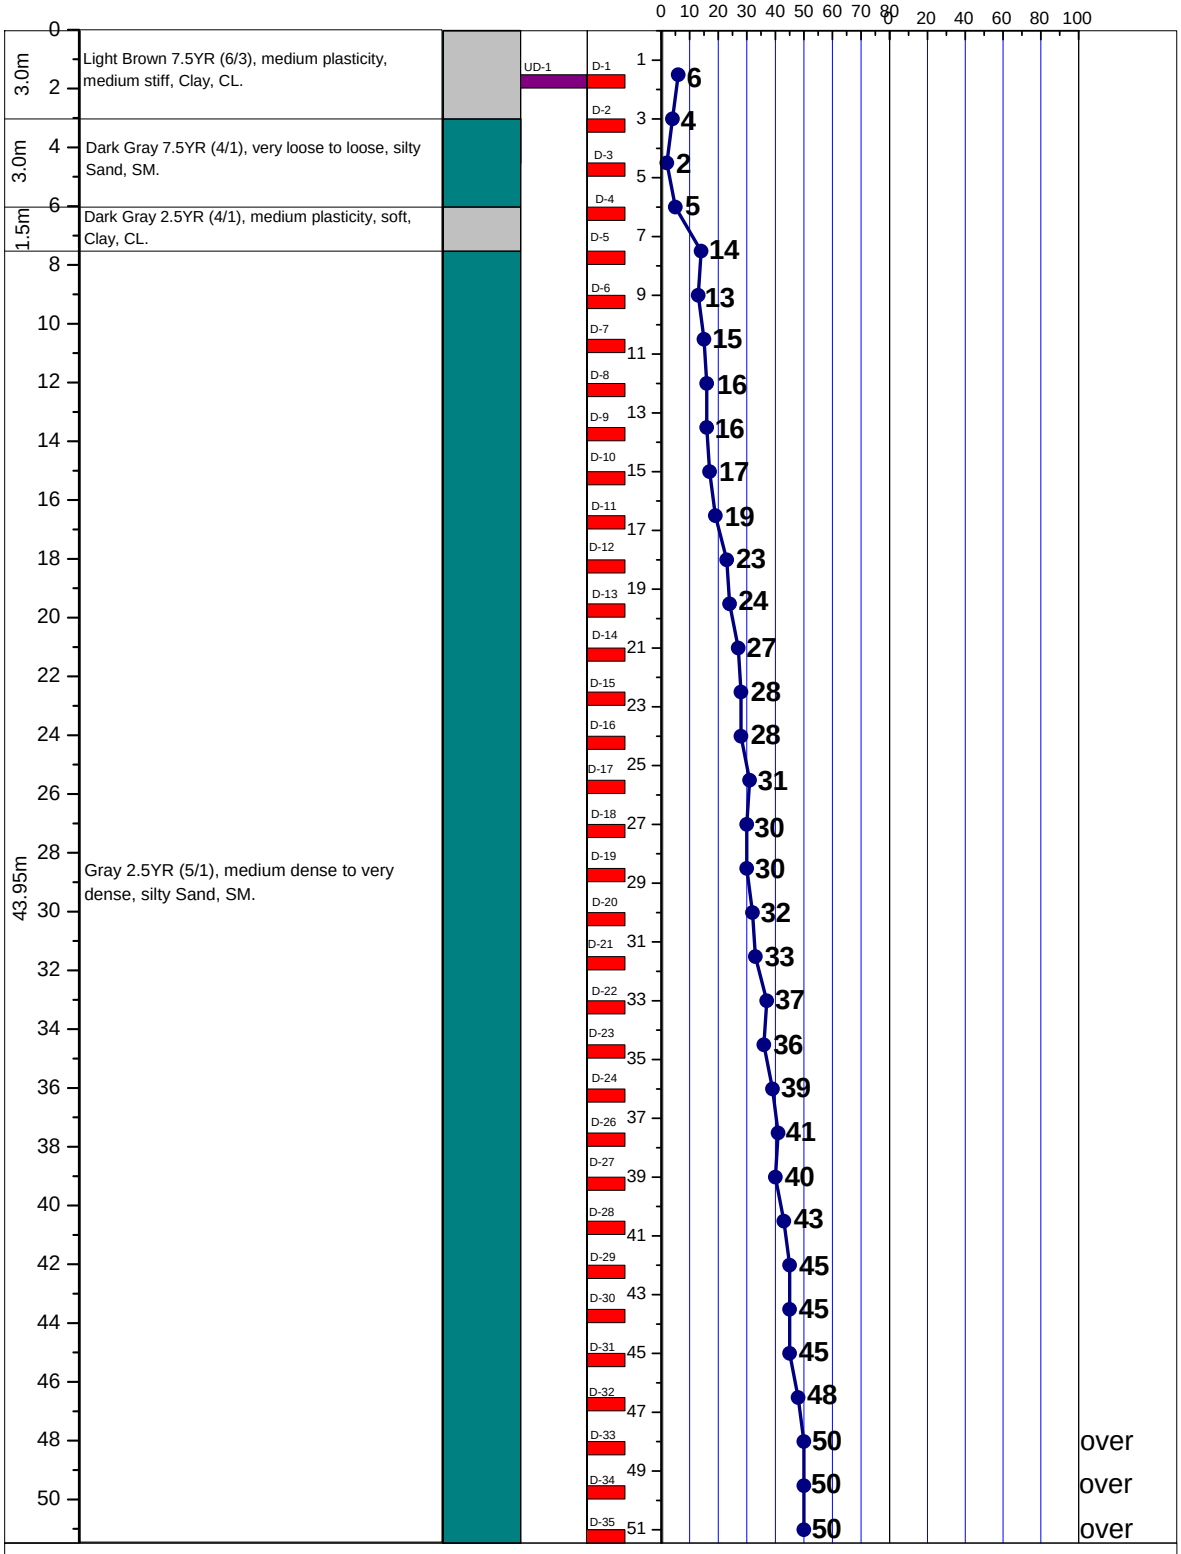


LEGEND FOR BORELOG AND GRAIN SIZE DISTRIBUTION (BASED ON 'ASTM CLASSIFICATION D-2487')

PLASTIC CLAY	SILT	PEAT/HIGHLY ORGANIC SOIL	UNDISTURBED SAMPLE
MICACEOUS FINE SAND/SILT	SAND	SHALE	DISTURBED SAMPLE

N- BLOWS DELIVERED PER FOOT BY A 140 LB HAMMER FALLING 30 INCHES

MAX^{m} PENETRATION= 50 BLOWS. AFTER 50 BLOWS PENETRATION DEPTH WERE MEASURED

A2	PROSOIL	BOREHOLE NO: BH-1	
		LOCATION : Chowfaldondi Ghat, Eidgah, Cox's Bazar.	
PROJECT : Telecommunication Tower.		DEPTH OF BORING : 51.0m	R. L.: 3.05m below from Road Level.
CLIENT : AXIATA (Bangladesh) Ltd.		DATE OF BORING : 28-06-2010.	G. W. T : 0.30m above from E. G. L.(Rain Water)

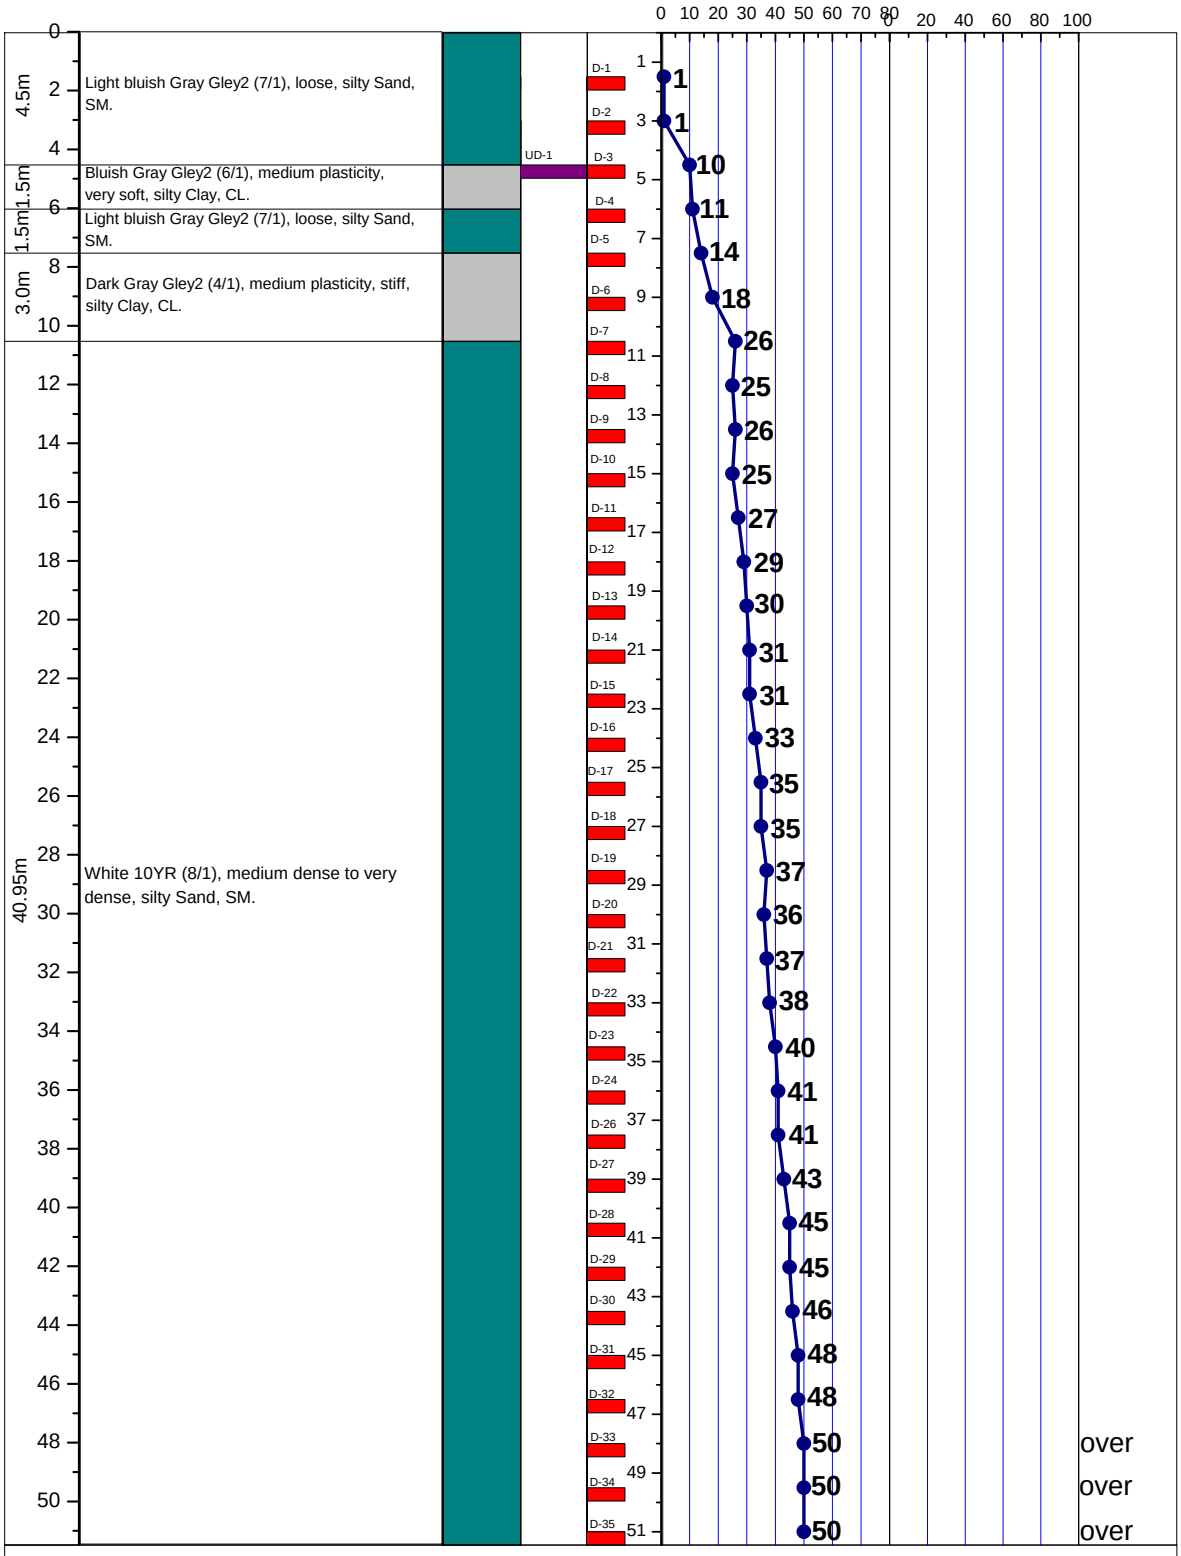


LEGEND FOR BORELOG AND GRAIN SIZE DISTRIBUTION (BASED ON 'ASTM CLASSIFICATION D-2487')

PLASTIC CLAY	SILT	PEAT/HIGHLY ORGANIC SOIL	UNDISTURBED SAMPLE
MICACEOUS FINE SAND/SILT	SAND	SHALE	DISTURBED SAMPLE

N- BLOWS DELIVERED PER FOOT BY A 140 LB HAMMER FALLING 30 INCHES

MAX^{m} PENETRATION= 50 BLOWS. AFTER 50 BLOWS PENETRATION DEPTH WERE MEASURED

A2 PROSOIL	BOREHOLE NO: BH-1	
	LOCATION : Dailyaghona (Osmanpur 2), Cox's Bazar.	
PROJECT : Telecommunication Tower.	DEPTH OF BORING : 51.0m	R. L.: Road Level
CLIENT : AXIATA (Bangladesh) Ltd.	DATE OF BORING : 31-08-2010.	G. W. T : 0.76m below from E. G. L.

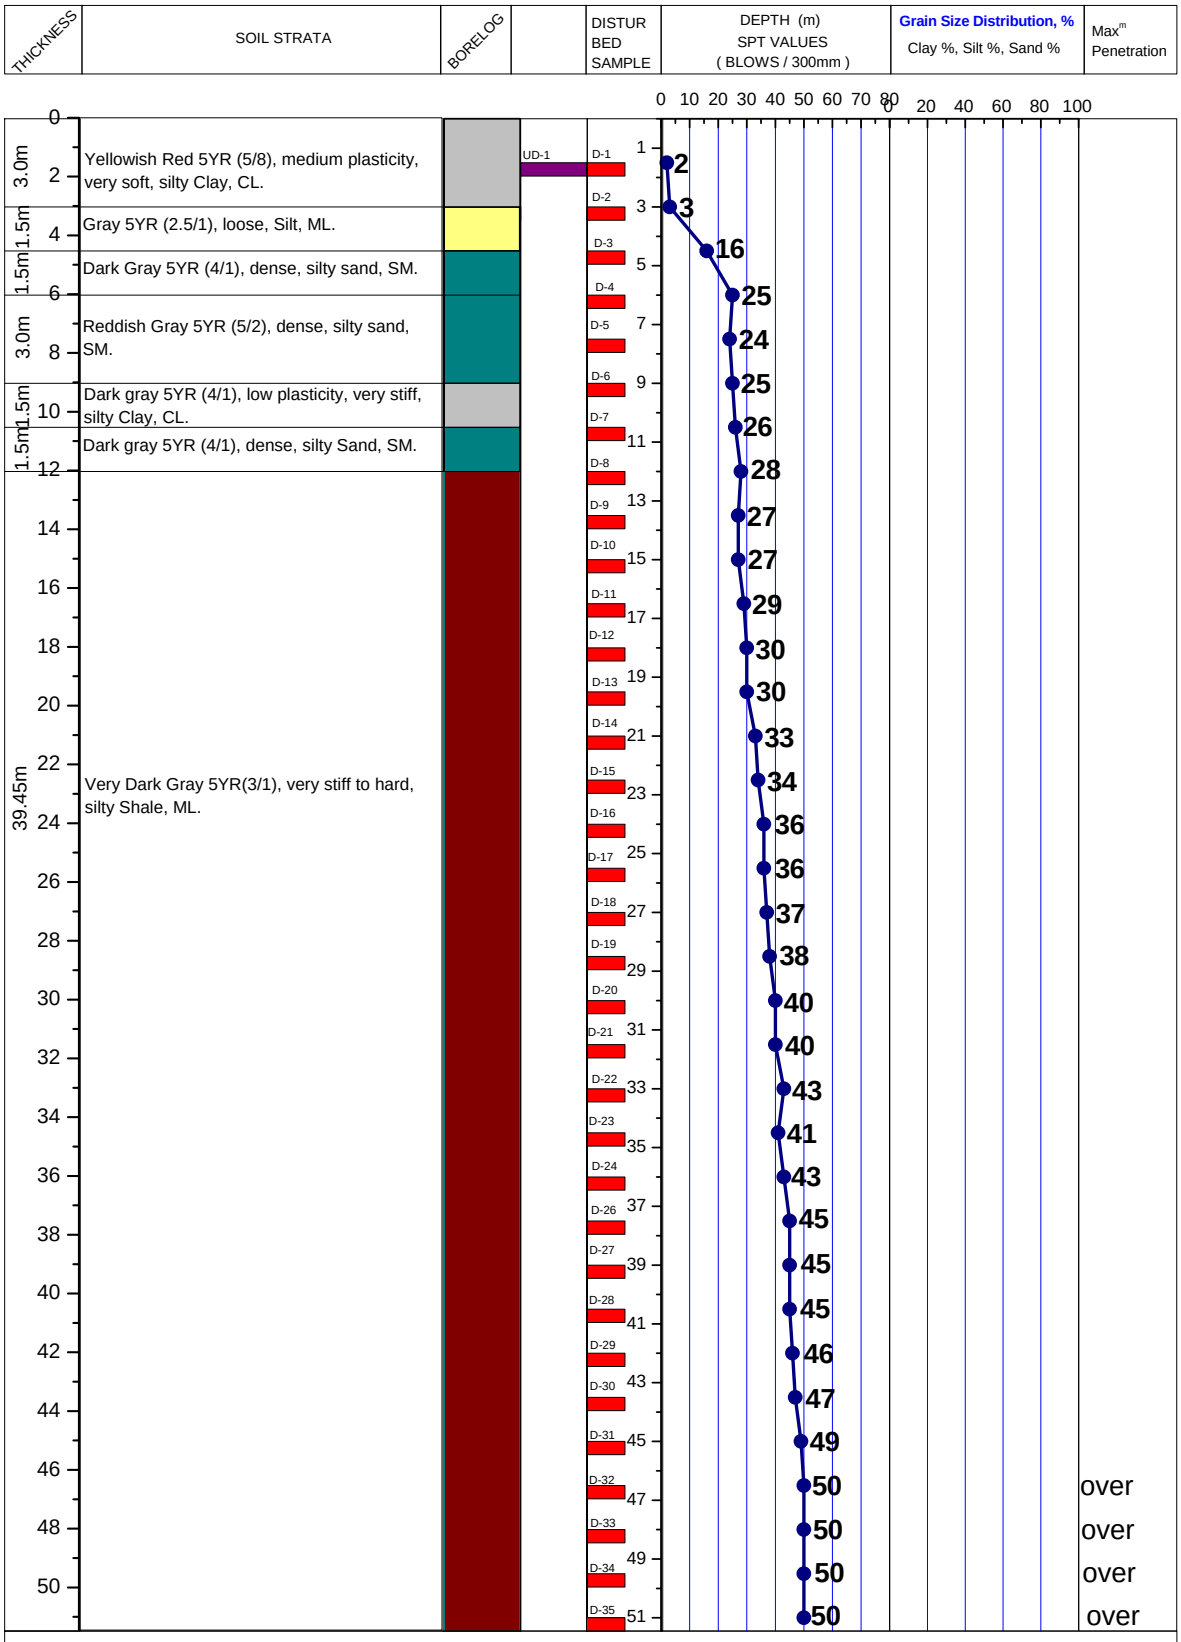


LEGEND FOR BORELOG AND GRAIN SIZE DISTRIBUTION (BASED ON 'ASTM CLASSIFICATION D-2487')

PLASTIC CLAY	SILT	PEAT/HIGHLY ORGANIC SOIL	UNDISTURBED SAMPLE
MICACEOUS FINE SAND/SILT	SAND	SHALE	DISTURBED SAMPLE

N- BLOWS DELIVERED PER FOOT BY A 140 LB HAMMER FALLING 30 INCHES

MAX^{m} PENETRATION= 50 BLOWS. AFTER 50 BLOWS PENETRATION DEPTH WERE MEASURED

A2 PROSOIL	BOREHOLE NO: BH-1	
	LOCATION : Faithong, Faithong Headman para, Boroitoli, Lama.	
PROJECT : Telecommunication Tower.	DEPTH OF BORING : 51.0m	R. L.: 0.91m below from Road Level.
CLIENT : AXIATA (Bangladesh) Ltd.	DATE OF BORING : 02-04-2011.	G. W. T : 1.83m below from E. G. L.

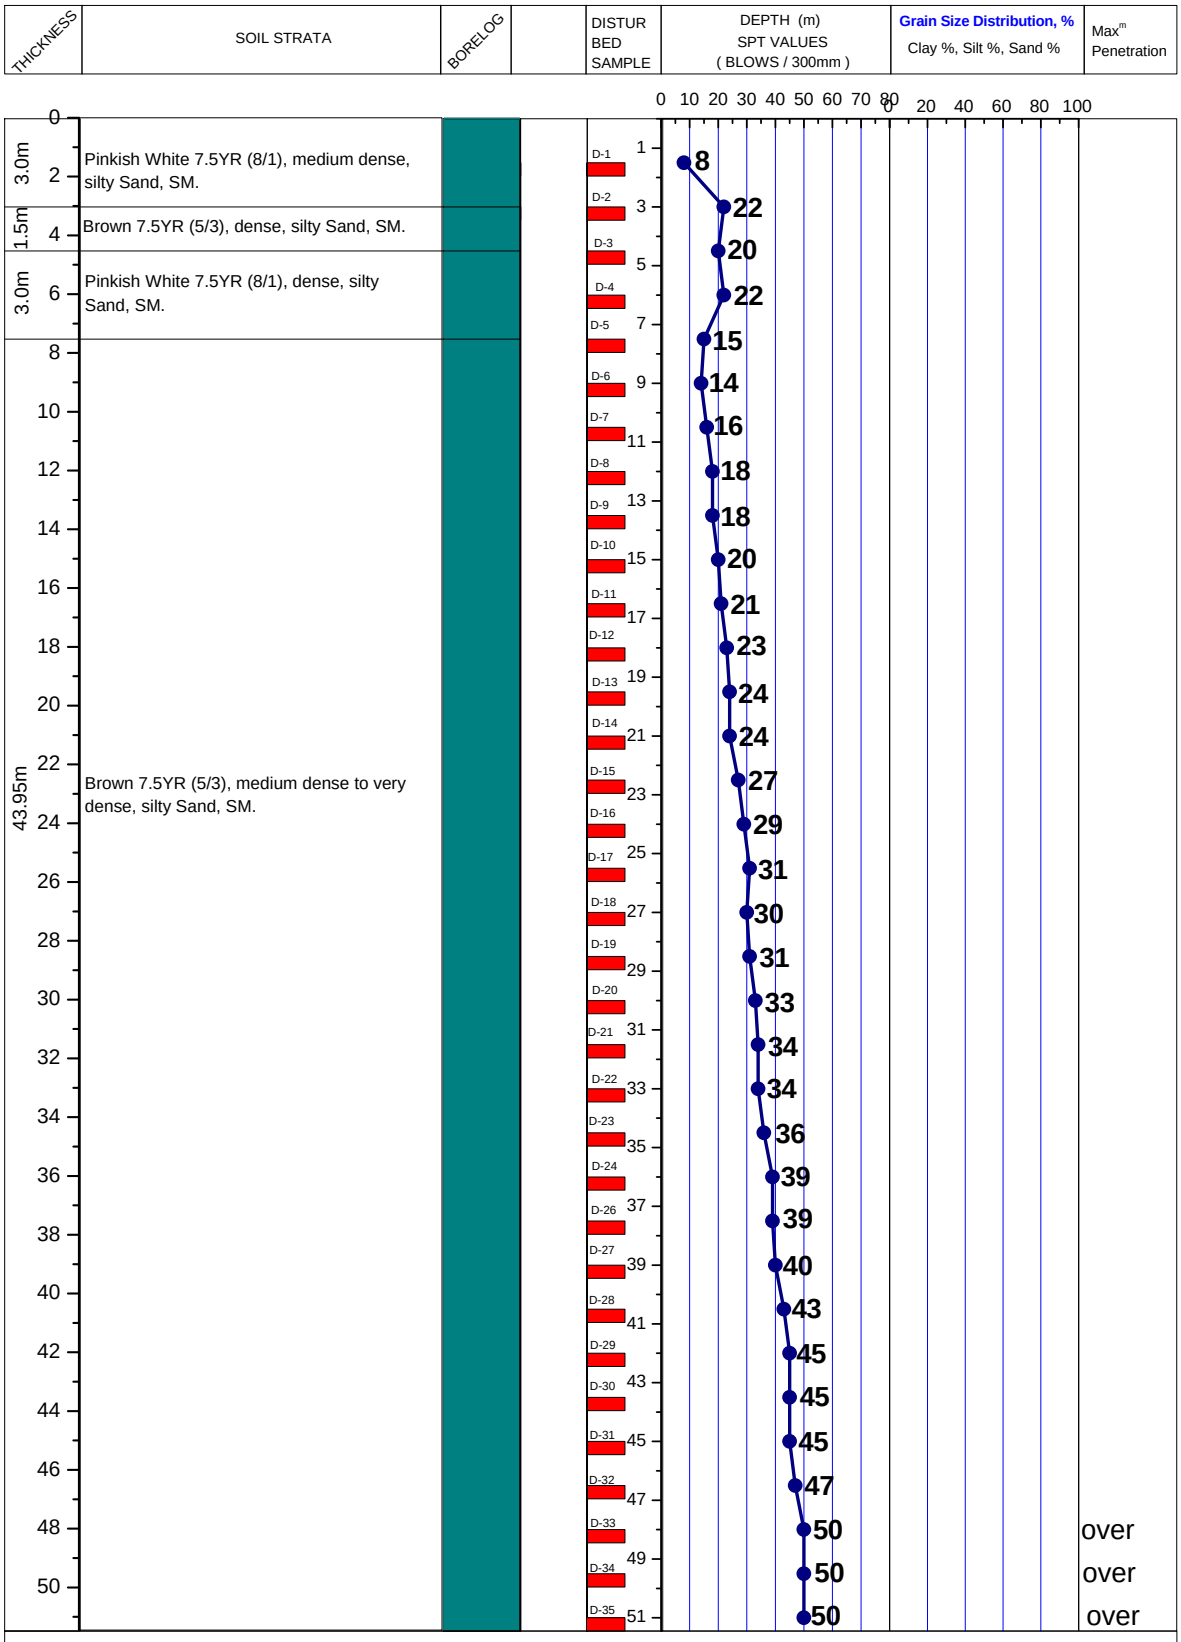


LEGEND FOR BORELOG AND GRAIN SIZE DISTRIBUTION (BASED ON 'ASTM CLASSIFICATION D-2487')

PLASTIC CLAY	SILT	PEAT/HIGHLY ORGANIC SOIL	UNDISTURBED SAMPLE
MICACEOUS FINE SAND/SILT	SAND	SHALE	DISTURBED SAMPLE

N- BLOWS DELIVERED PER FOOT BY A 140 LB HAMMER FALLING 30 INCHES

MAX^{m} PENETRATION= 50 BLOWS. AFTER 50 BLOWS PENETRATION DEPTH WERE MEASURED

A2	PROSOIL	BOREHOLE NO: BH-1	
		LOCATION : Innani Beach, Cox's Bazar.	
PROJECT : Telecommunication Tower.		DEPTH OF BORING : 51.0m	R. L.:On Road Level
CLIENT : AXIATA (Bangladesh) Ltd.		DATE OF BORING : 30-07-2010.	G. W. T : 0.07m below from E. G. L.

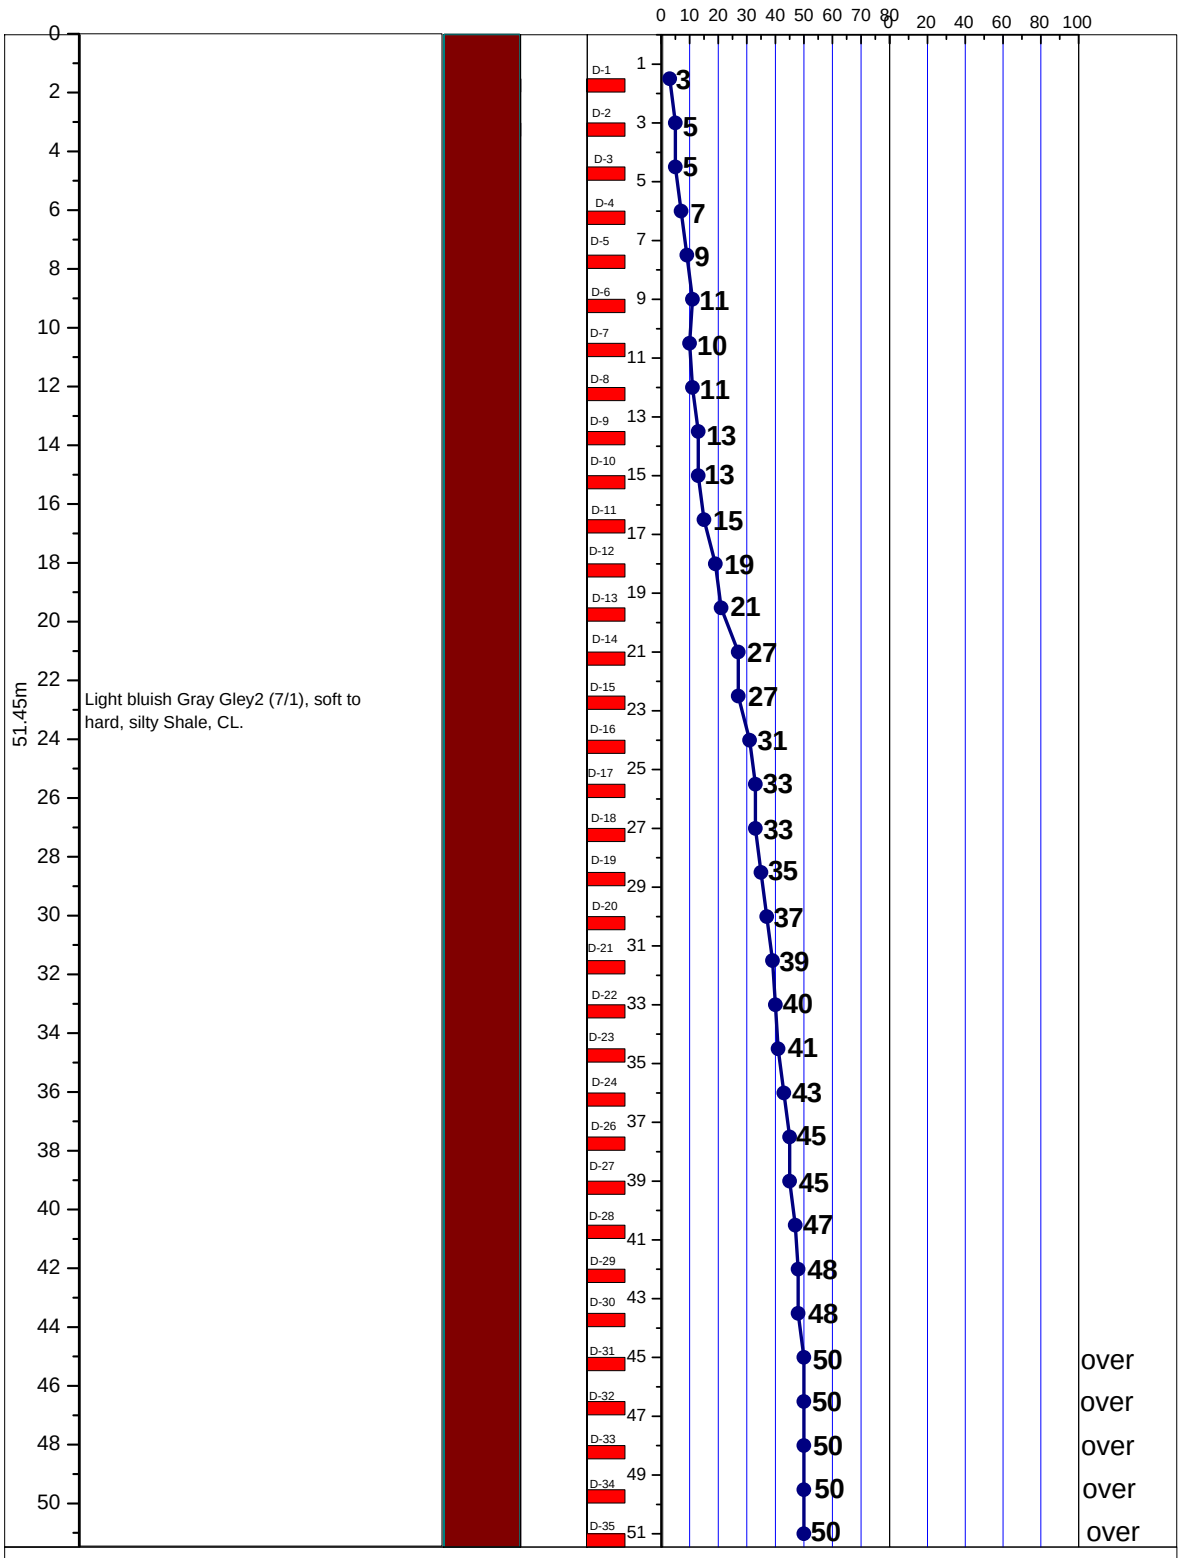


LEGEND FOR BORELOG AND GRAIN SIZE DISTRIBUTION (BASED ON 'ASTM CLASSIFICATION D-2487')

PLASTIC CLAY	SILT	PEAT/HIGHLY ORGANIC SOIL	UNDISTURBED SAMPLE
MICACEOUS FINE SAND/SILT	SAND	SHALE	DISTURBED SAMPLE

N- BLOWS DELIVERED PER FOOT BY A 140 LB HAMMER FALLING 30 INCHES

MAX^{m} PENETRATION= 50 BLOWS. AFTER 50 BLOWS PENETRATION DEPTH WERE MEASURED

A2	PROSOIL	BOREHOLE NO: BH-1	
		LOCATION : Katakali Madrasa, Whykong2, Cox's Bazar.	
PROJECT : Telecommunication Tower.		DEPTH OF BORING : 51.0m	R. L.: 0.51m below from Road Level.
CLIENT : AXIATA (Bangladesh) Ltd.		DATE OF BORING : 28-11-2010.	G. W. T : 0.60m below from E. G. L.

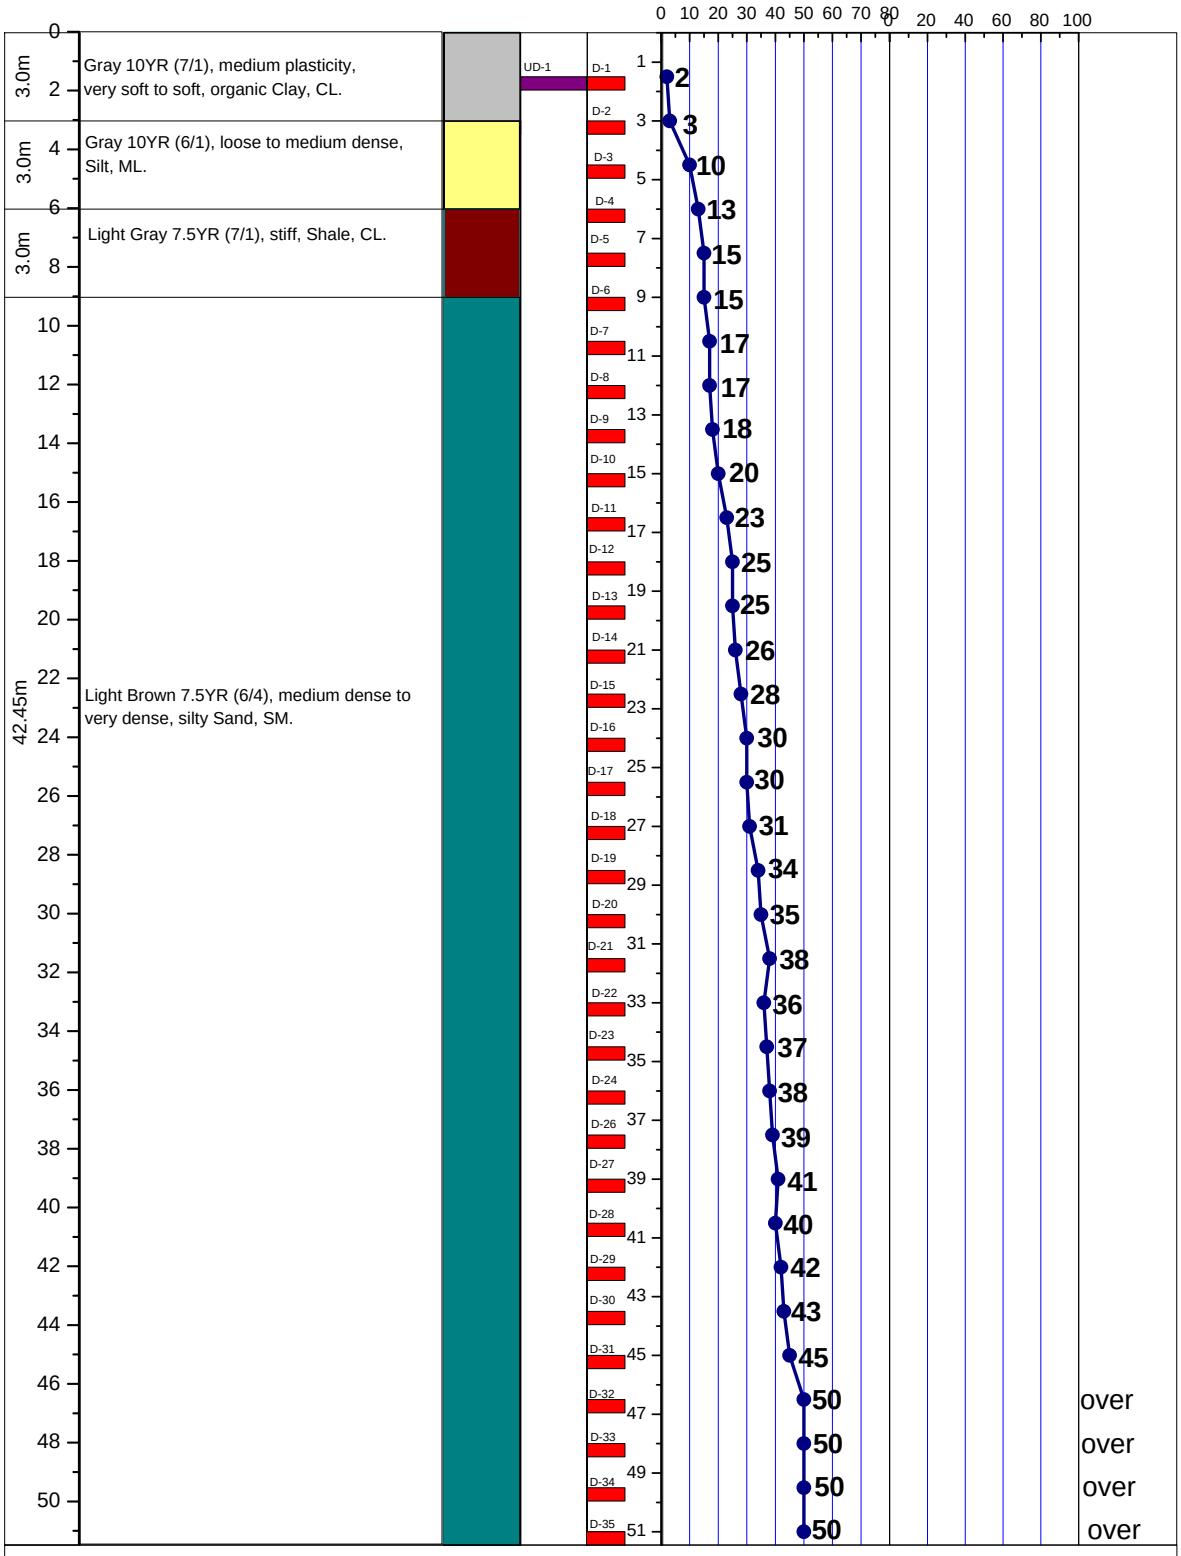


LEGEND FOR BORELOG AND GRAIN SIZE DISTRIBUTION (BASED ON 'ASTM CLASSIFICATION D-2487')

PLASTIC CLAY	SILT	PEAT/HIGHLY ORGANIC SOIL	UNDISTURBED SAMPLE
MICACEOUS FINE SAND/SILT	SAND	SHALE	DISTURBED SAMPLE

N- BLOWS DELIVERED PER FOOT BY A 140 LB HAMMER FALLING 30 INCHES

MAX^{m} PENETRATION= 50 BLOWS. AFTER 50 BLOWS PENETRATION DEPTH WERE MEASURED

A2 PROSOIL	BOREHOLE NO: BH-1	
	LOCATION : Keyedabad Bazar, Keyedabad, Shaplapur, Moheshkhali.	
PROJECT : Telecommunication Tower.	DEPTH OF BORING : 51.0m	R. L.: 0.61m below from Road Level.
CLIENT : AXIATA (Bangladesh) Ltd.	DATE OF BORING : 01-04-2011.	G. W. T : 3.66m below from E. G. L.

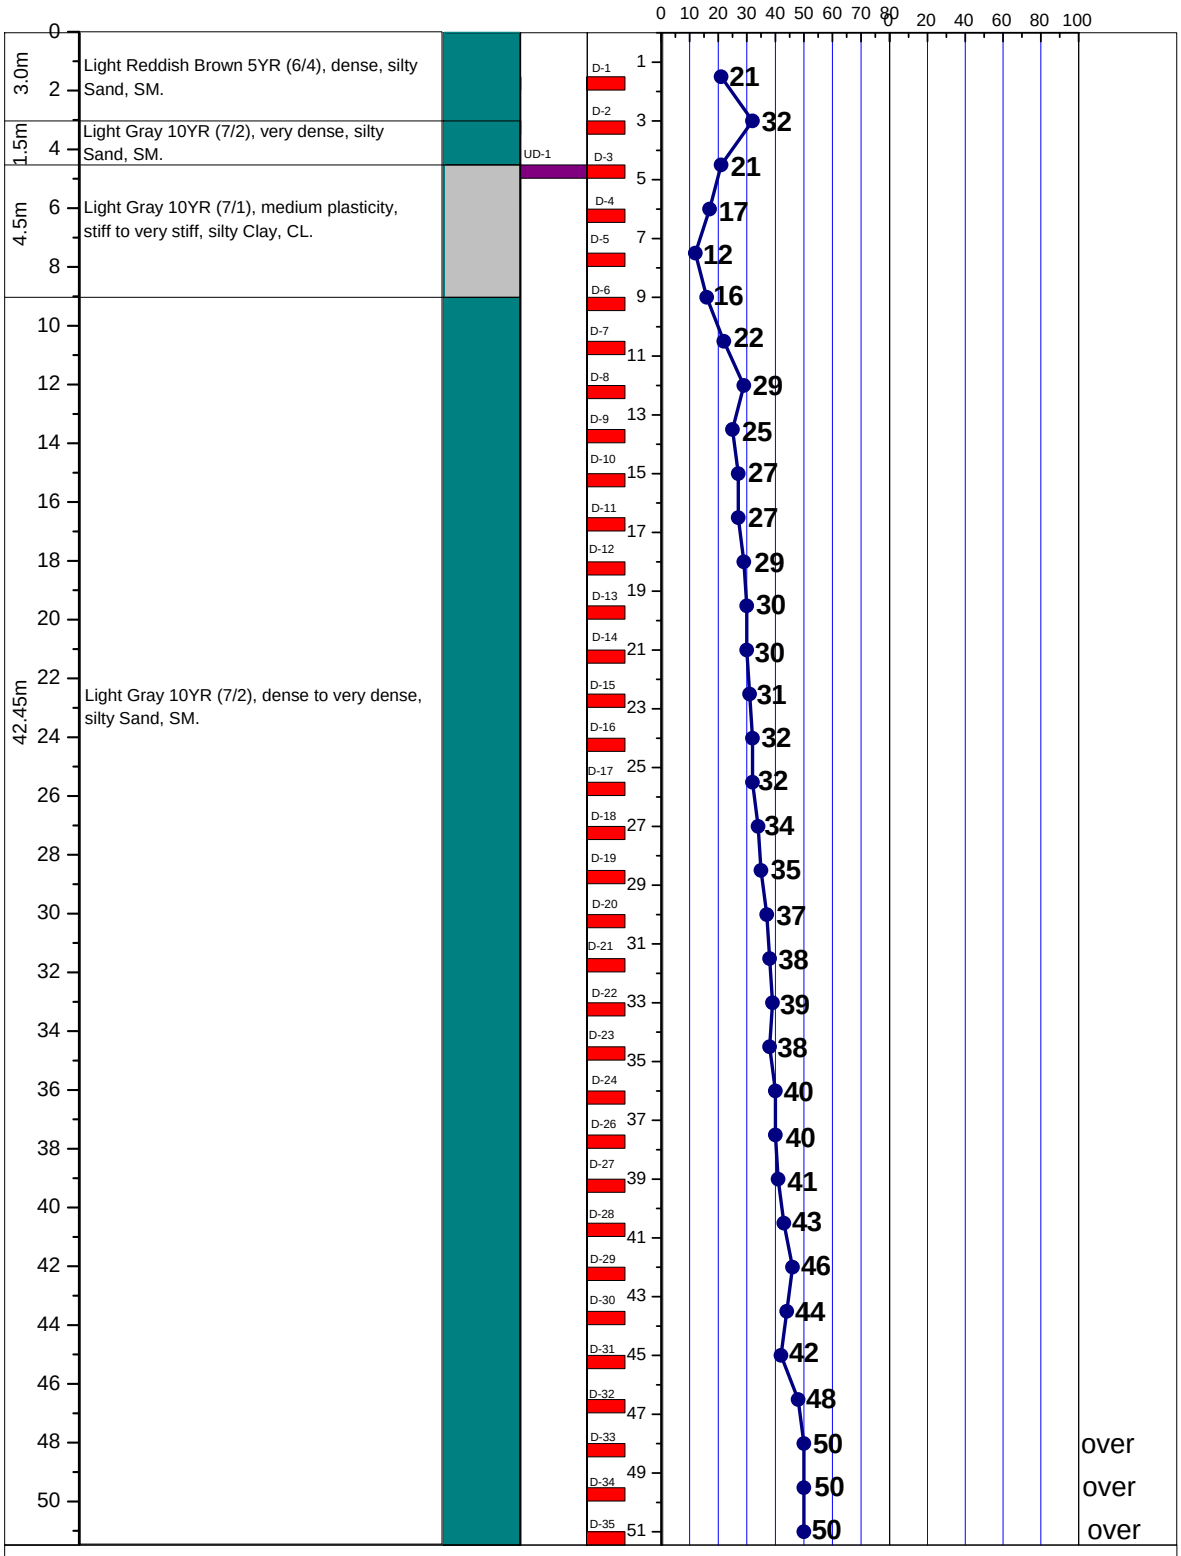


LEGEND FOR BORELOG AND GRAIN SIZE DISTRIBUTION (BASED ON 'ASTM CLASSIFICATION D-2487')

PLASTIC CLAY	SILT	PEAT/HIGHLY ORGANIC SOIL	UNDISTURBED SAMPLE
MICACEOUS FINE SAND/SILT	SAND	SHALE	DISTURBED SAMPLE

N- BLOWS DELIVERED PER FOOT BY A 140 LB HAMMER FALLING 30 INCHES

MAX^{m} PENETRATION= 50 BLOWS. AFTER 50 BLOWS PENETRATION DEPTH WERE MEASURED

A2 PROSOIL	BOREHOLE NO: BH-1	
	LOCATION : Kutubdia Model High School, Kutubdia, Cox's Bazar.	
PROJECT : Telecommunication Tower.	DEPTH OF BORING : 51.0m	R. L.: On Road Level.
CLIENT : AXIATA (Bangladesh) Ltd.	DATE OF BORING : 03-04-2011.	G. W. T : 0.61m below from E. G. L.

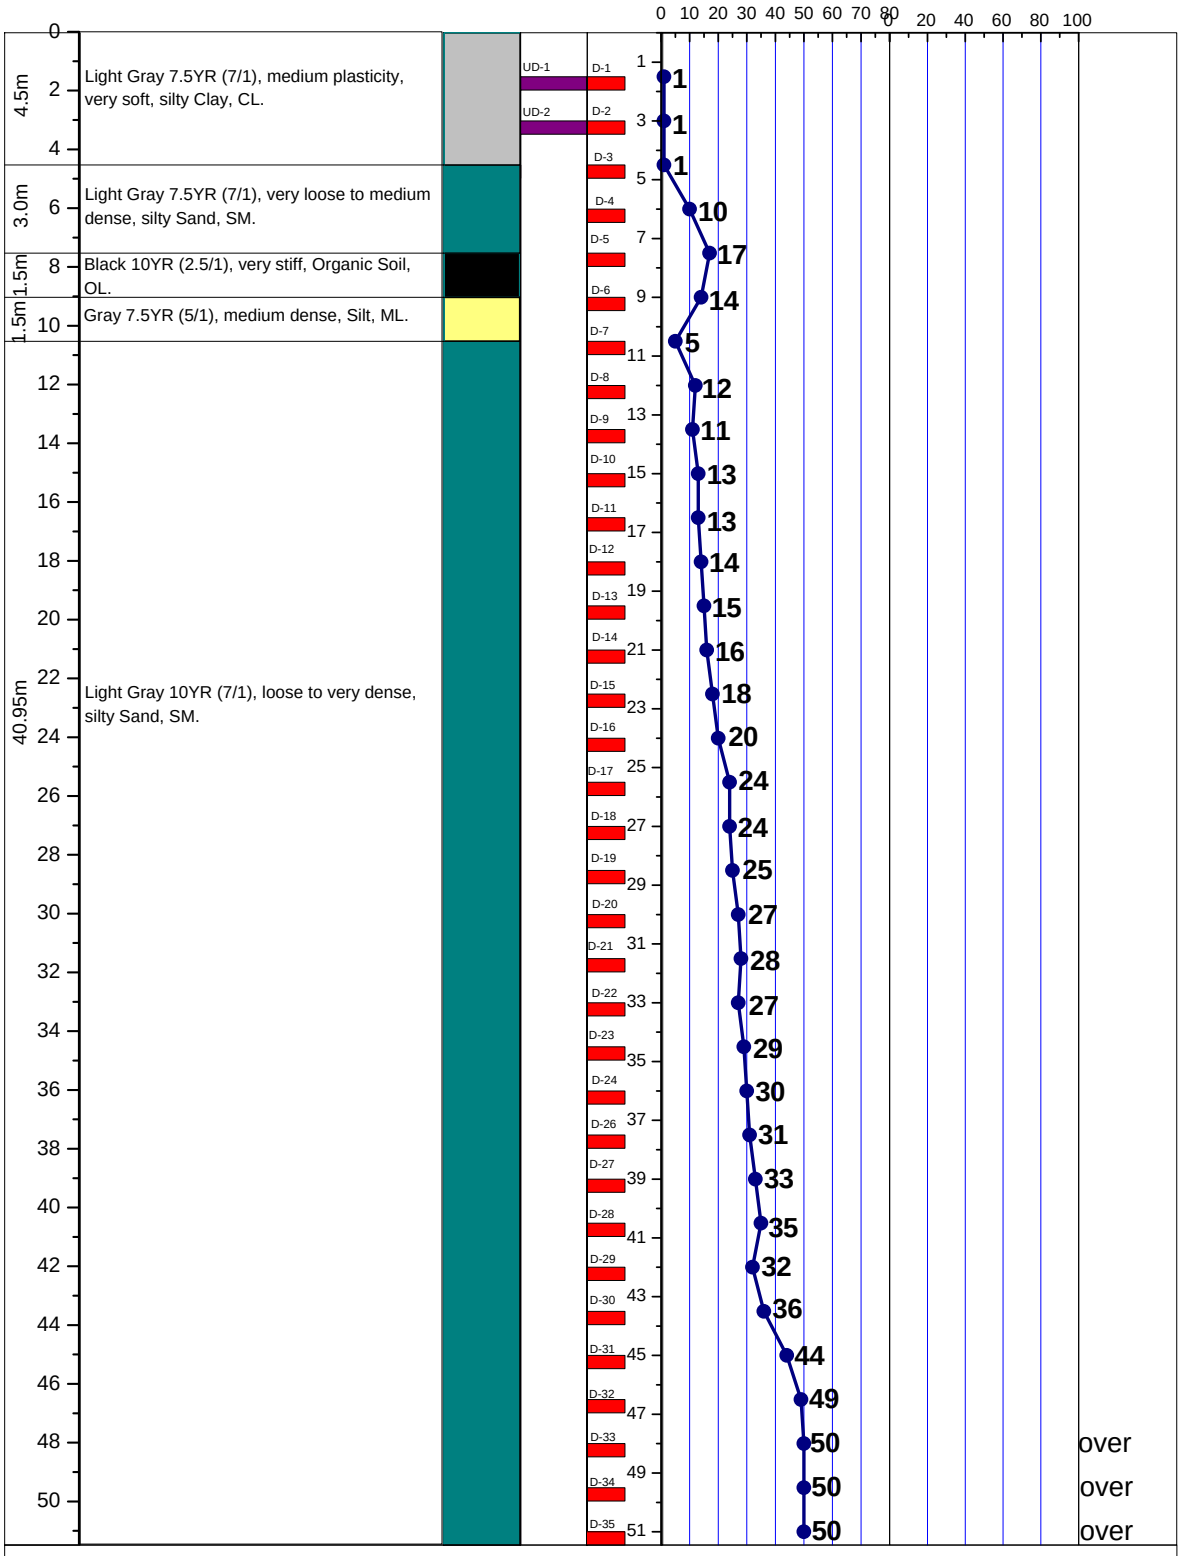


LEGEND FOR BORELOG AND GRAIN SIZE DISTRIBUTION (BASED ON 'ASTM CLASSIFICATION D-2487')

PLASTIC CLAY	SILT	PEAT/HIGHLY ORGANIC SOIL	UNDISTURBED SAMPLE
MICACEOUS FINE SAND/SILT	SAND	SHALE	DISTURBED SAMPLE

N- BLOWS DELIVERED PER FOOT BY A 140 LB HAMMER FALLING 30 INCHES

MAX^{m} PENETRATION= 50 BLOWS. AFTER 50 BLOWS PENETRATION DEPTH WERE MEASURED

A2	PROSOIL	BOREHOLE NO: BH-1	
		LOCATION : Kutubdia, Baingakata, Dhurong, Kutubdia.	
PROJECT : Telecommunication Tower.		DEPTH OF BORING : 51.0m	R. L.: 1.22m below from Road Level.
CLIENT : AXIATA (Bangladesh) Ltd.		DATE OF BORING : 03-04-2011.	G. W. T : 3.05m below from E. G. L.

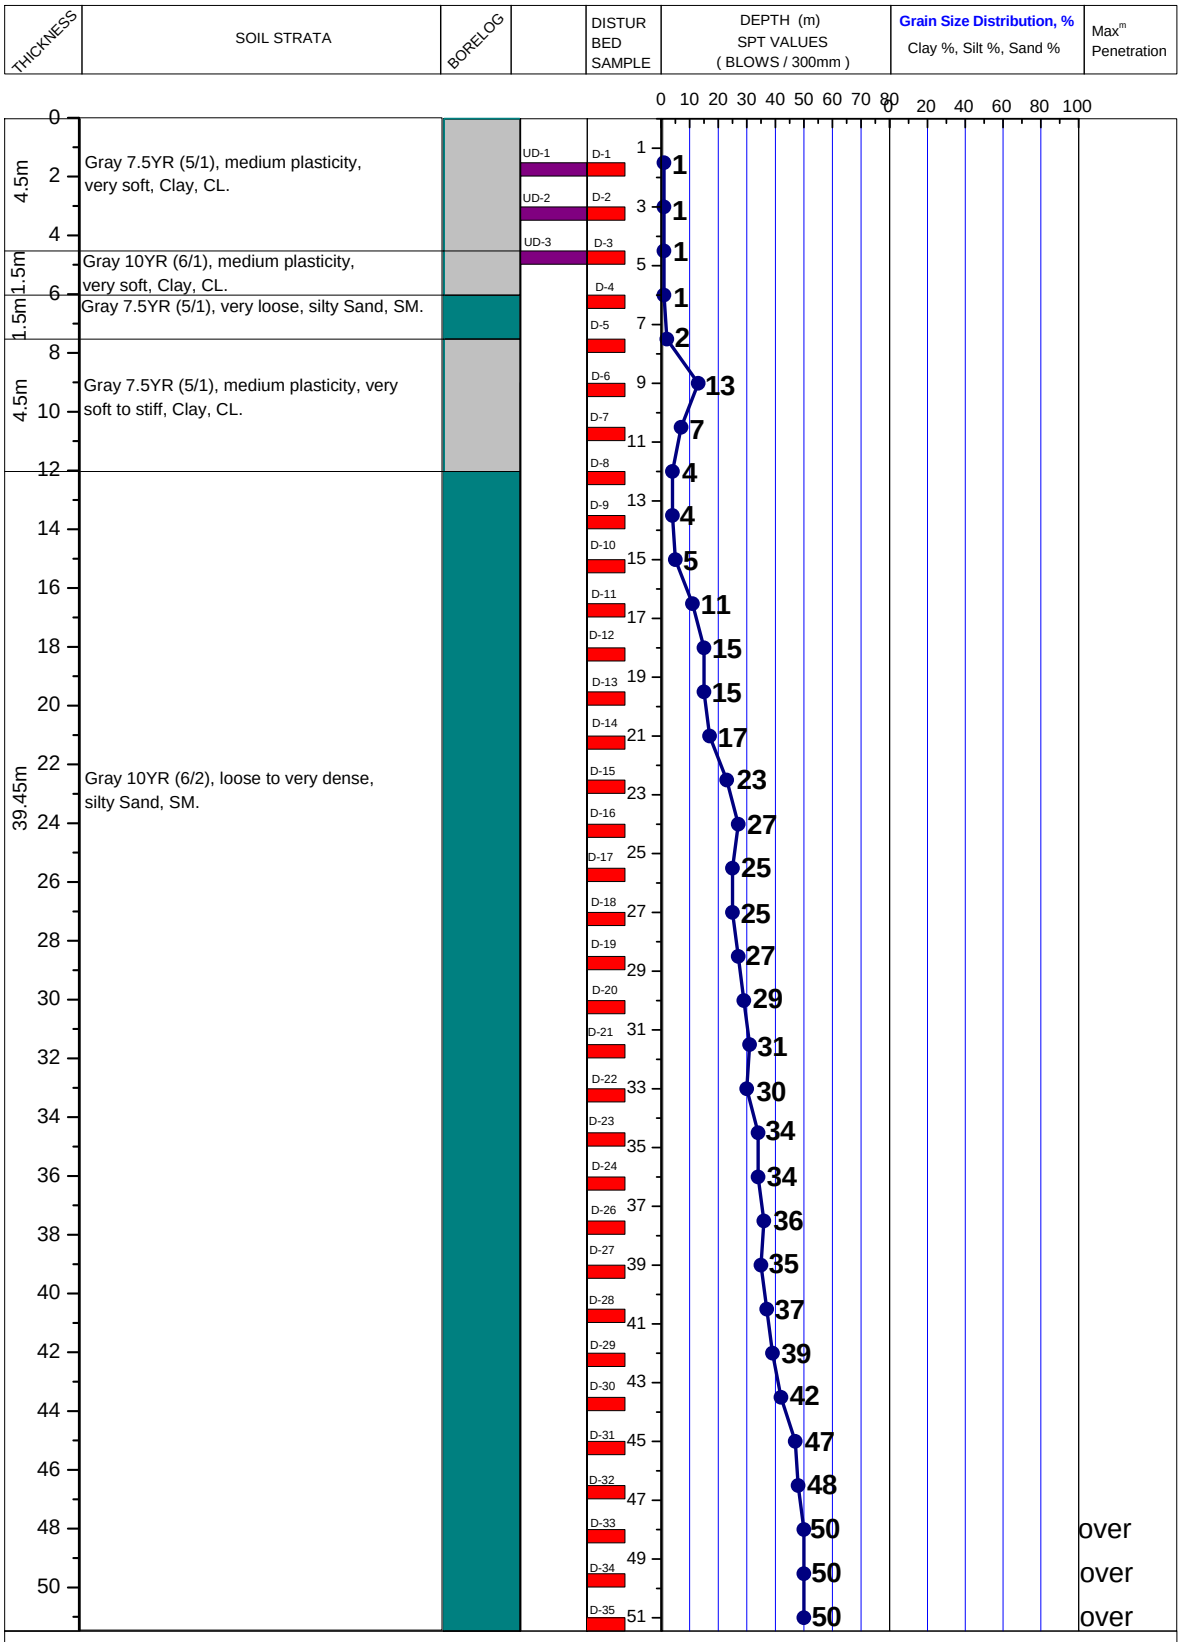


LEGEND FOR BORELOG AND GRAIN SIZE DISTRIBUTION (BASED ON 'ASTM CLASSIFICATION D-2487')

PLASTIC CLAY	SILT	PEAT/HIGHLY ORGANIC SOIL	UNDISTURBED SAMPLE
MICACEOUS FINE SAND/SILT	SAND	SHALE	DISTURBED SAMPLE

N- BLOWS DELIVERED PER FOOT BY A 140 LB HAMMER FALLING 30 INCHES

MAX^{m} PENETRATION= 50 BLOWS. AFTER 50 BLOWS PENETRATION DEPTH WERE MEASURED

A2	PROSOIL	BOREHOLE NO: BH-1	
		LOCATION : Malumghat, Chokoria, Cox's Bazar.	
PROJECT : Telecommunication Tower.		DEPTH OF BORING : 51.0m	R. L.: 0.76m below from Road Level.
CLIENT : AXIATA (Bangladesh) Ltd.		DATE OF BORING : 08-10-2010.	G. W. T : 1.52m below from E. G. L.

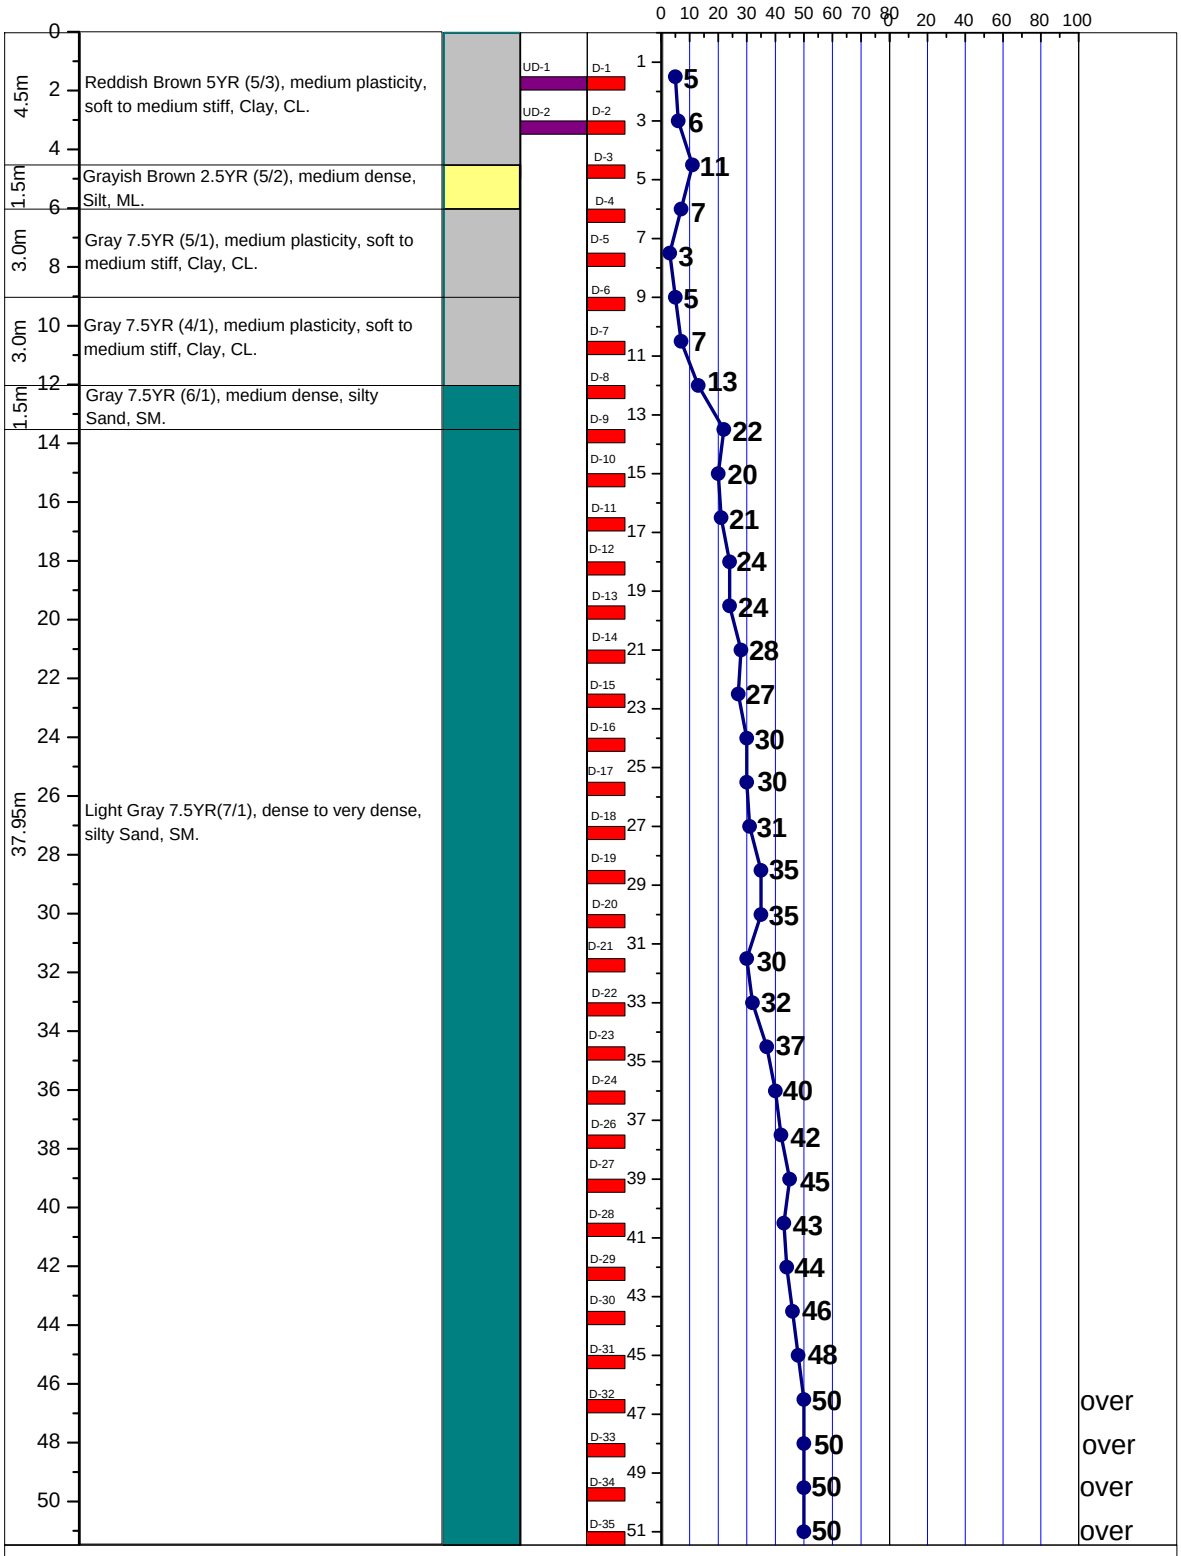


LEGEND FOR BORELOG AND GRAIN SIZE DISTRIBUTION (BASED ON 'ASTM CLASSIFICATION D-2487')

PLASTIC CLAY	SILT	PEAT/HIGHLY ORGANIC SOIL	UNDISTURBED SAMPLE
MICACEOUS FINE SAND/SILT	SAND	SHALE	DISTURBED SAMPLE

N- BLOWS DELIVERED PER FOOT BY A 140 LB HAMMER FALLING 30 INCHES

MAX^{m} PENETRATION= 50 BLOWS. AFTER 50 BLOWS PENETRATION DEPTH WERE MEASURED

A2	PROSOIL	BOREHOLE NO: BH-1	
		LOCATION : Mogdail Bazar, Moheshkhali.	
PROJECT : Telecommunication Tower.		DEPTH OF BORING : 51.0m	R. L.: On Road Level.
CLIENT : AXIATA (Bangladesh) Ltd.		DATE OF BORING : 31-03-2011.	G. W. T : 1.52m below from E. G. L.

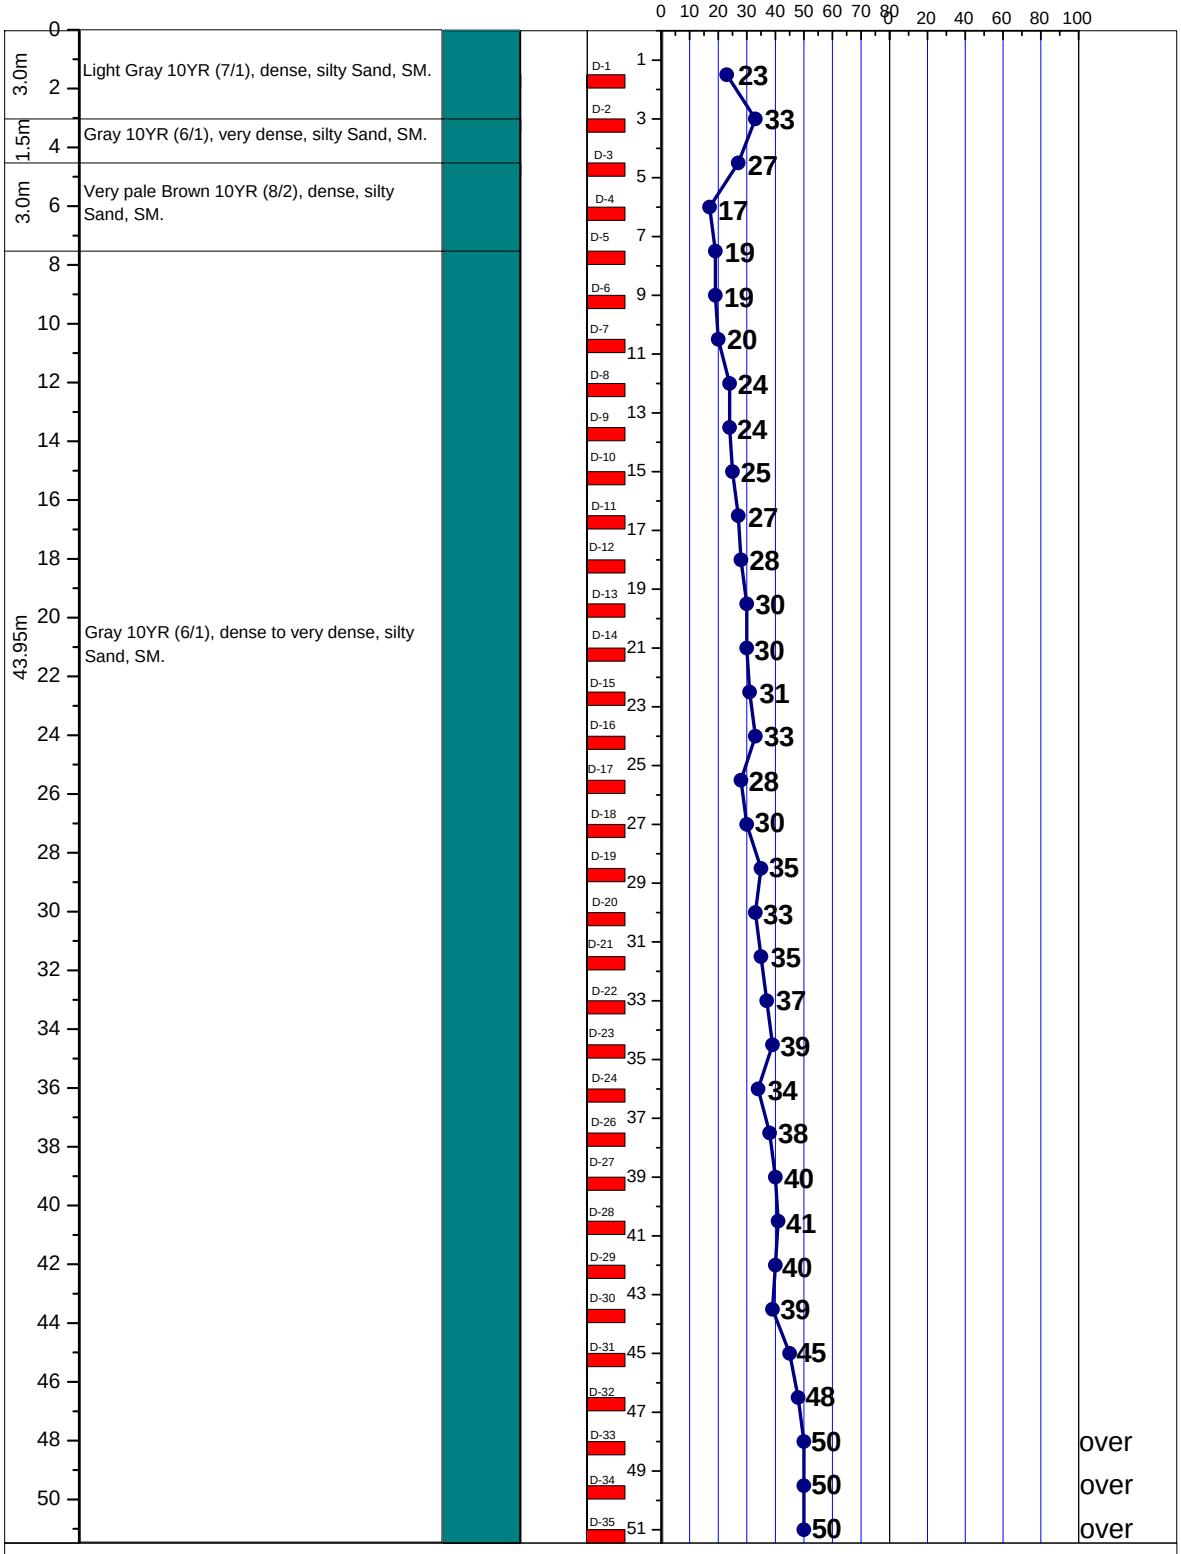


LEGEND FOR BORELOG AND GRAIN SIZE DISTRIBUTION (BASED ON 'ASTM CLASSIFICATION D-2487')

PLASTIC CLAY	SILT	PEAT/HIGHLY ORGANIC SOIL	UNDISTURBED SAMPLE
MICACEOUS FINE SAND/SILT	SAND	SHALE	DISTURBED SAMPLE

N- BLOWS DELIVERED PER FOOT BY A 140 LB HAMMER FALLING 30 INCHES

MAX^{m} PENETRATION= 50 BLOWS. AFTER 50 BLOWS PENETRATION DEPTH WERE MEASURED

A2	PROSOIL	BOREHOLE NO: BH-1	
		LOCATION : Moheshkhali 2, Ghonapara, Gorakghata, Moheshkhali.	
PROJECT : Telecommunication Tower.		DEPTH OF BORING : 51.0m	R. L.: 1.37m below from Road Level.
CLIENT : AXIATA (Bangladesh) Ltd.		DATE OF BORING : 02-04-2011.	G. W. T : 2.44m below from E. G. L.

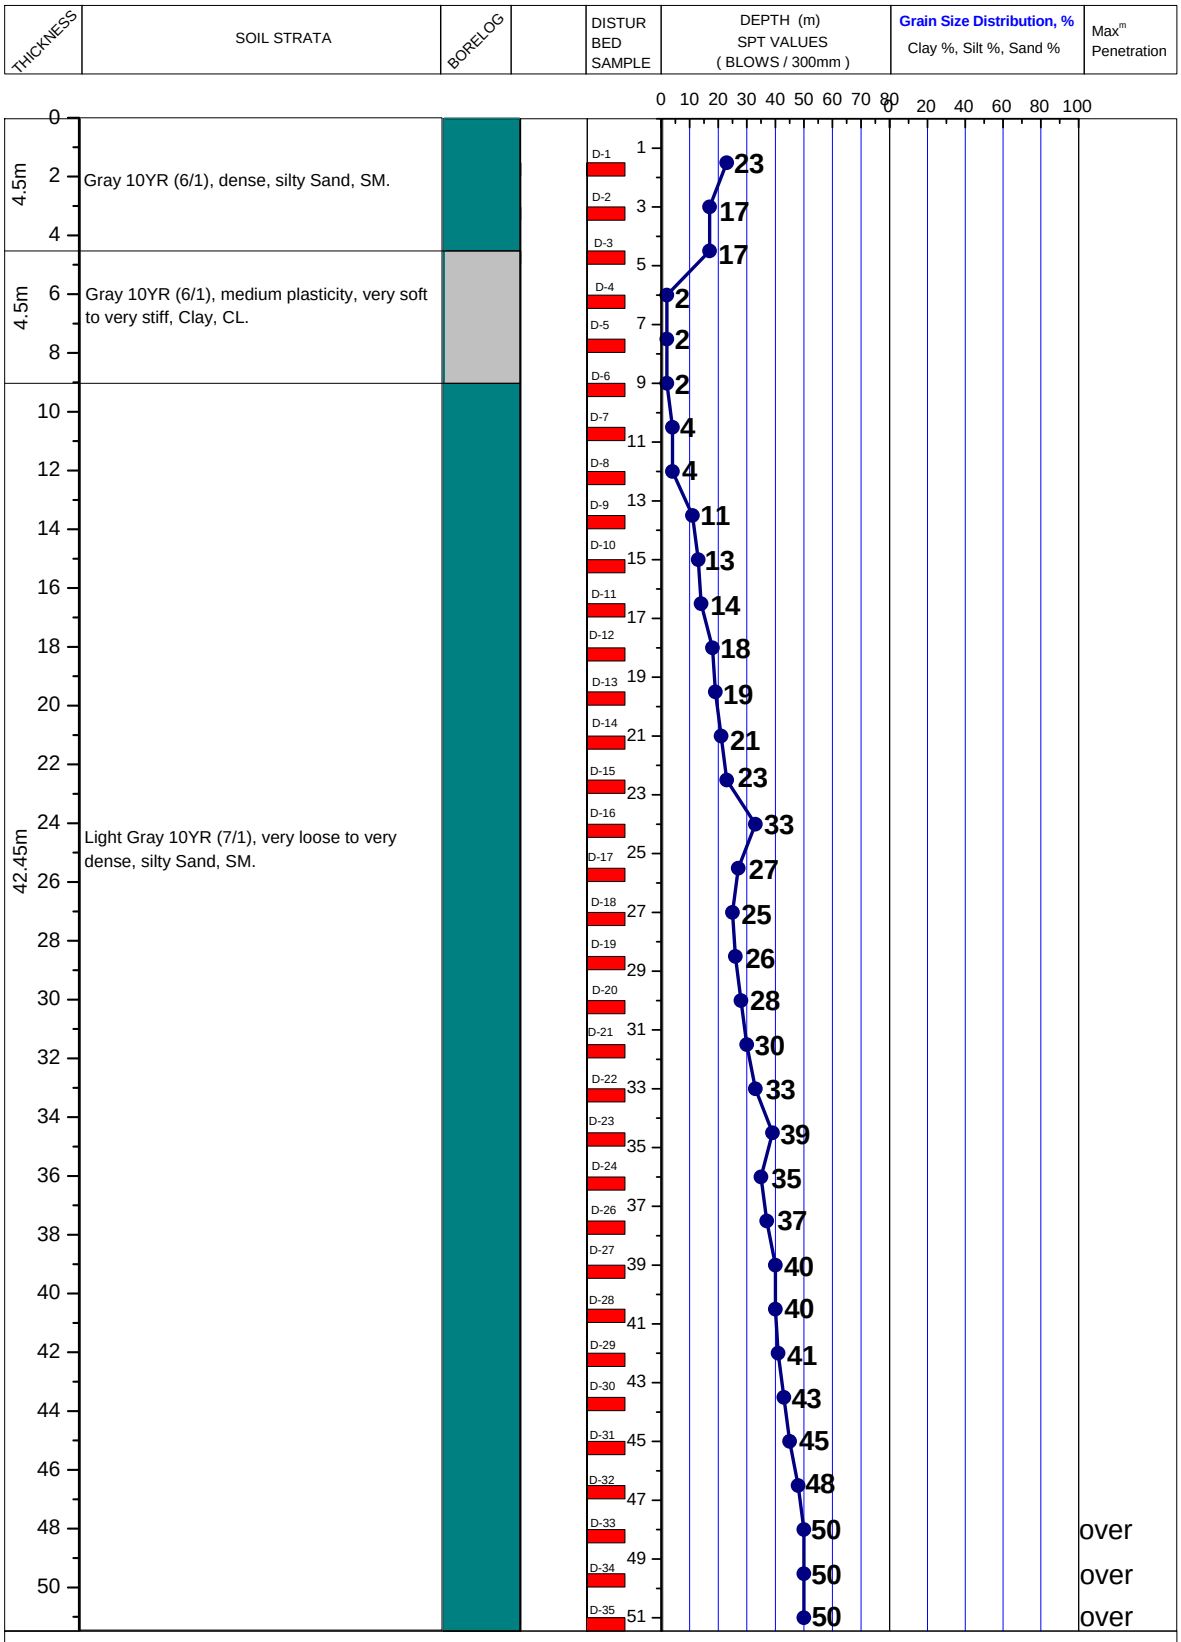


LEGEND FOR BORELOG AND GRAIN SIZE DISTRIBUTION (BASED ON 'ASTM CLASSIFICATION D-2487')

PLASTIC CLAY	SILT	PEAT/HIGHLY ORGANIC SOIL	UNDISTURBED SAMPLE
MICACEOUS FINE SAND/SILT	SAND	SHALE	DISTURBED SAMPLE

N- BLOWS DELIVERED PER FOOT BY A 140 LB HAMMER FALLING 30 INCHES

MAX^{m} PENETRATION= 50 BLOWS. AFTER 50 BLOWS PENETRATION DEPTH WERE MEASURED

A2 PROSOIL	BOREHOLE NO: BH-1	
	LOCATION : Moloyer Dokan, East Digholipalon, Ukhia, Cox's Bazar.	
PROJECT : Telecommunication Tower.	DEPTH OF BORING : 51.0m	R. L.: 1.22m below from Road Level.
CLIENT : AXIATA (Bangladesh) Ltd.	DATE OF BORING : 29-03-2011.	G. W. T : 2.13m below from E. G. L.

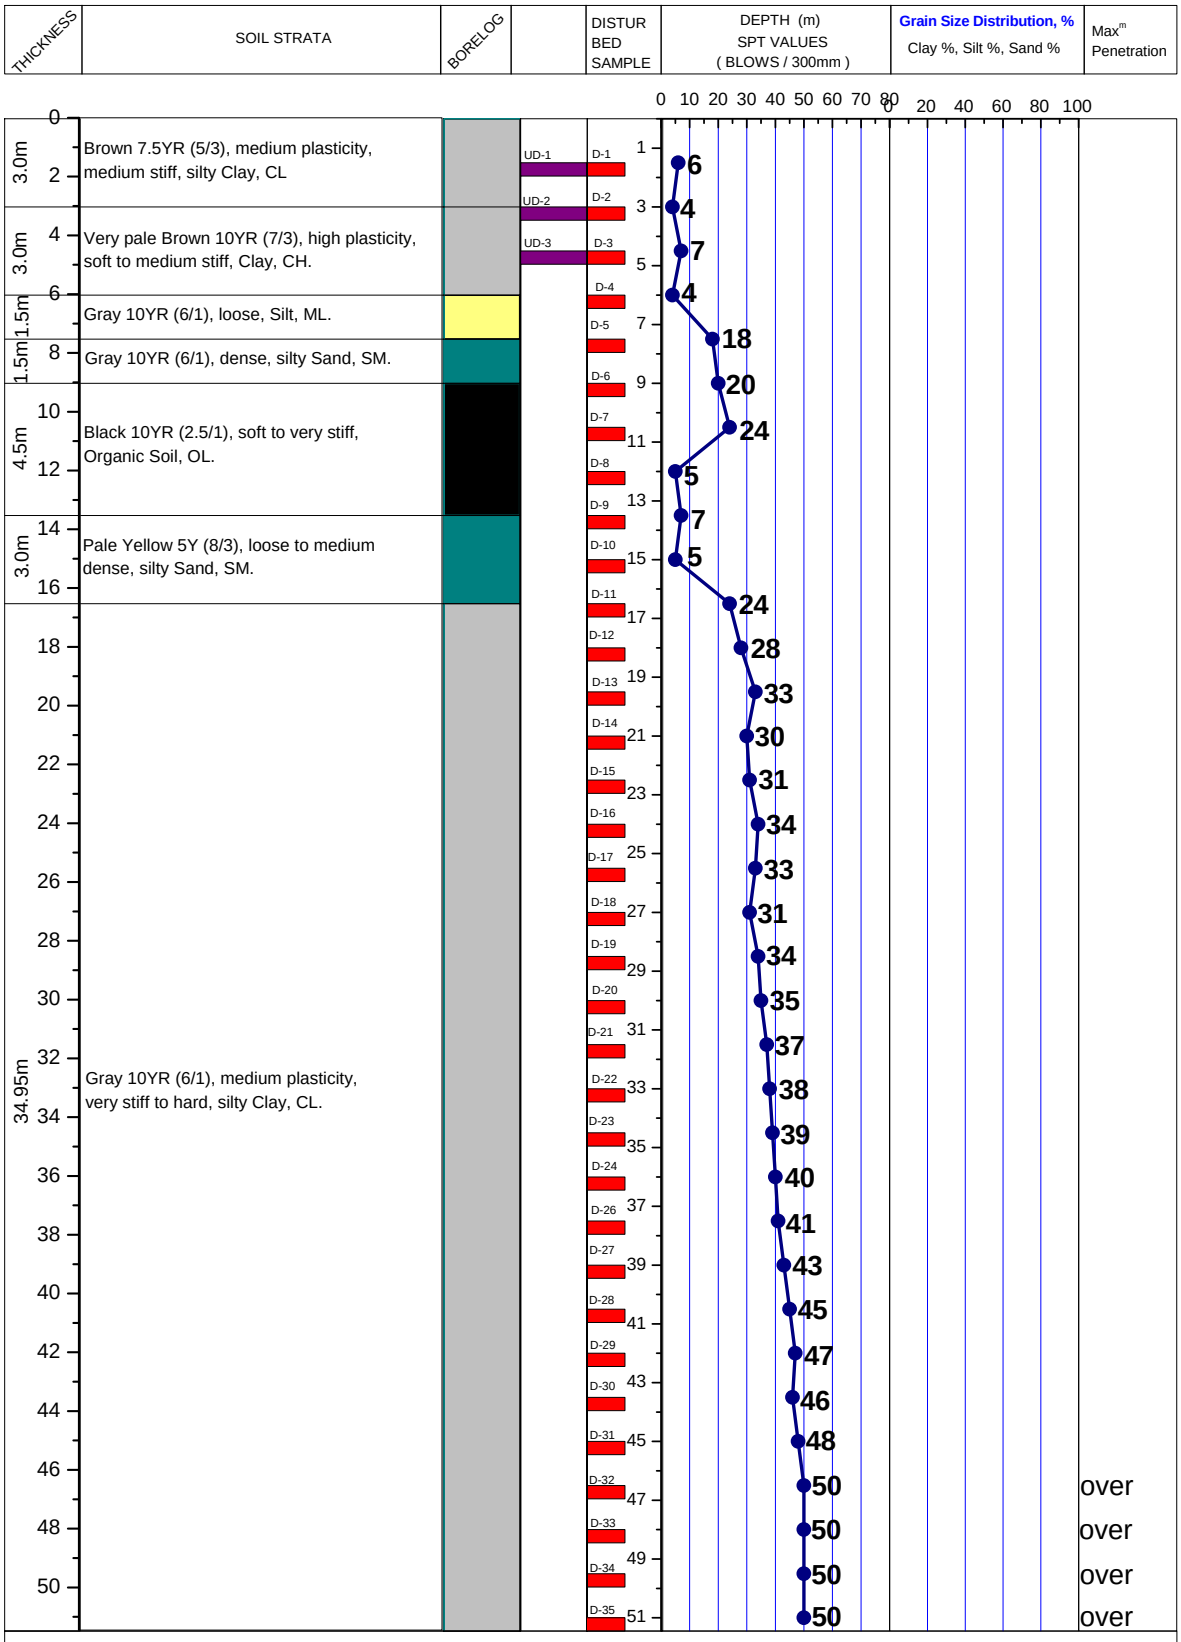


LEGEND FOR BORELOG AND GRAIN SIZE DISTRIBUTION (BASED ON 'ASTM CLASSIFICATION D-2487')

PLASTIC CLAY	SILT	PEAT/HIGHLY ORGANIC SOIL	UNDISTURBED SAMPLE
MICACEOUS FINE SAND/SILT	SAND	SHALE	DISTURBED SAMPLE

N- BLOWS DELIVERED PER FOOT BY A 140 LB HAMMER FALLING 30 INCHES

MAX^{m} PENETRATION= 50 BLOWS. AFTER 50 BLOWS PENETRATION DEPTH WERE MEASURED

A2	PROSOIL	BOREHOLE NO: BH-1	
		LOCATION : Monkhali, Chankhola, Inani, Cox's Bazar.	
PROJECT : Telecommunication Tower.		DEPTH OF BORING : 51.0m	R. L.: 1.22m below from Road Level.
CLIENT : AXIATA (Bangladesh) Ltd.		DATE OF BORING : 30-03-2011.	G. W. T : 1.83m below from E. G. L.

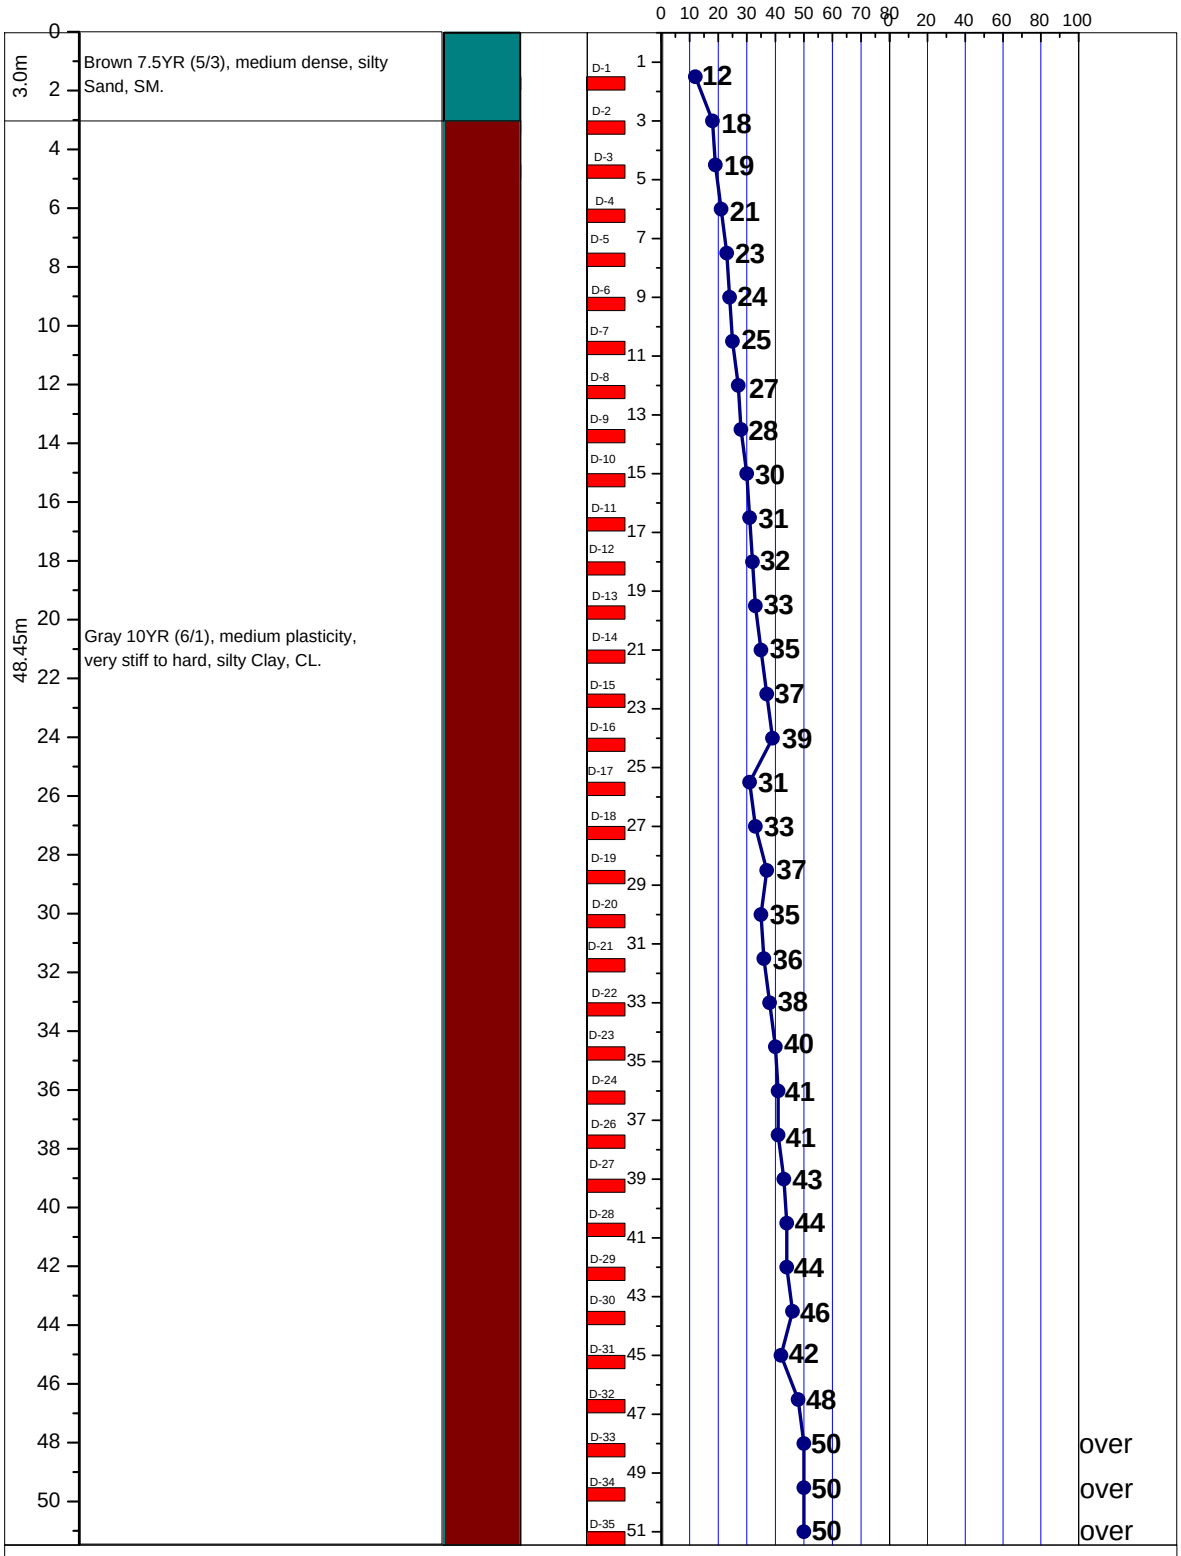


LEGEND FOR BORELOG AND GRAIN SIZE DISTRIBUTION (BASED ON 'ASTM CLASSIFICATION D-2487')

PLASTIC CLAY	SILT	PEAT/HIGHLY ORGANIC SOIL	UNDISTURBED SAMPLE
MICACEOUS FINE SAND/SILT	SAND	SHALE	DISTURBED SAMPLE

N- BLOWS DELIVERED PER FOOT BY A 140 LB HAMMER FALLING 30 INCHES

MAX^{m} PENETRATION= 50 BLOWS. AFTER 50 BLOWS PENETRATION DEPTH WERE MEASURED

A2 PROSOIL	BOREHOLE NO: BH-1	
	LOCATION : Pokkhali, Cox's Bazar.	
PROJECT : Telecommunication Tower.	DEPTH OF BORING : 51.0m	R. L.: 0.31m below from Road Level.
CLIENT : AXIATA (Bangladesh) Ltd.	DATE OF BORING : 26-09-2010.	G. W. T : 0.91m below from E. G. L.

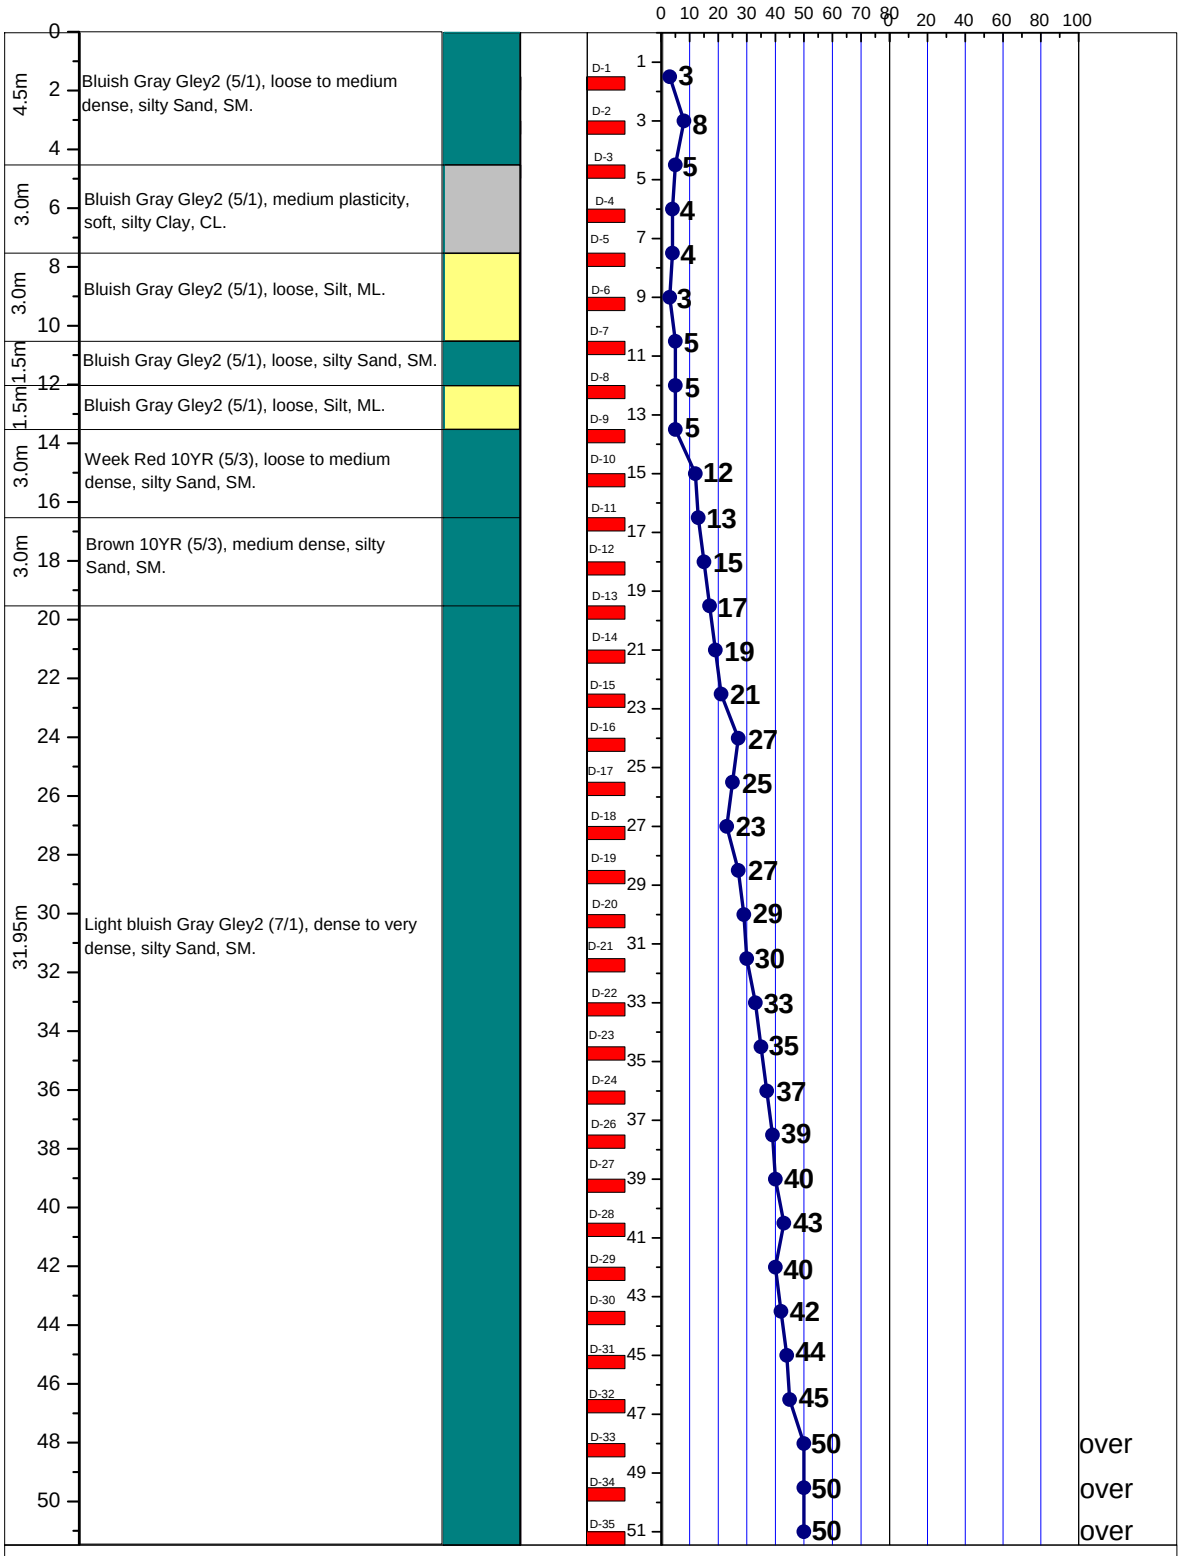


LEGEND FOR BORELOG AND GRAIN SIZE DISTRIBUTION (BASED ON 'ASTM CLASSIFICATION D-2487')

PLASTIC CLAY	SILT	PEAT/HIGHLY ORGANIC SOIL	UNDISTURBED SAMPLE
MICACEOUS FINE SAND/SILT	SAND	SHALE	DISTURBED SAMPLE

N- BLOWS DELIVERED PER FOOT BY A 140 LB HAMMER FALLING 30 INCHES

MAX^{m} PENETRATION= 50 BLOWS. AFTER 50 BLOWS PENETRATION DEPTH WERE MEASURED

A2 PROSOIL	BOREHOLE NO: BH-1	
	LOCATION : Sikdarpara, South Sikdarpara, Rajarkul, Ramu.	
PROJECT : Telecommunication Tower.	DEPTH OF BORING : 51.0m	R. L.: 1.07m below from Road Level.
CLIENT : AXIATA (Bangladesh) Ltd.	DATE OF BORING : 30-03-2011.	G. W. T : 1.52m below from E. G. L.

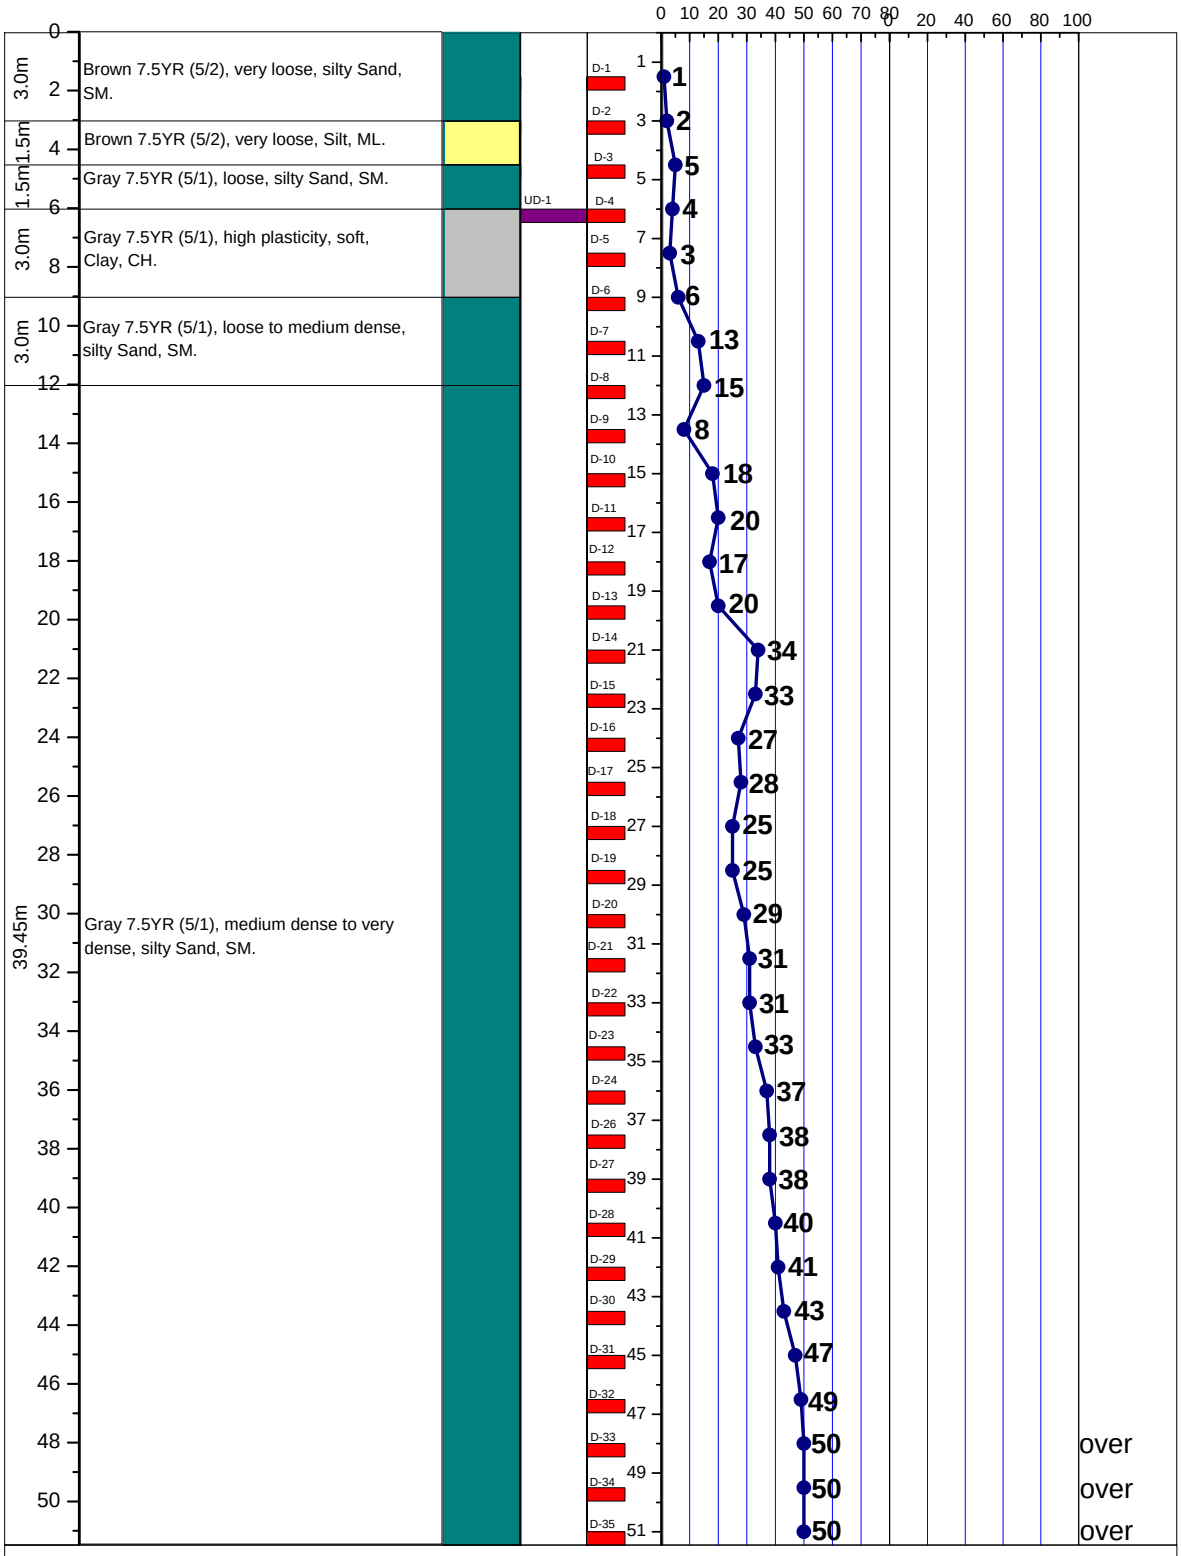


LEGEND FOR BORELOG AND GRAIN SIZE DISTRIBUTION (BASED ON 'ASTM CLASSIFICATION D-2487')

PLASTIC CLAY	SILT	PEAT/HIGHLY ORGANIC SOIL	UNDISTURBED SAMPLE
MICACEOUS FINE SAND/SILT	SAND	SHALE	DISTURBED SAMPLE

N- BLOWS DELIVERED PER FOOT BY A 140 LB HAMMER FALLING 30 INCHES

MAX^{m} PENETRATION= 50 BLOWS. AFTER 50 BLOWS PENETRATION DEPTH WERE MEASURED

A2	PROSOIL	BOREHOLE NO: BH-1	
		LOCATION : Tilapara, Kauarkhop, Ramu.	
PROJECT : Telecommunication Tower.		DEPTH OF BORING : 51.0m	R. L.: 0.46m below from Road Level.
CLIENT : AXIATA (Bangladesh) Ltd.		DATE OF BORING : 01-04-2011.	G. W. T : 2.44m below from E. G. L.

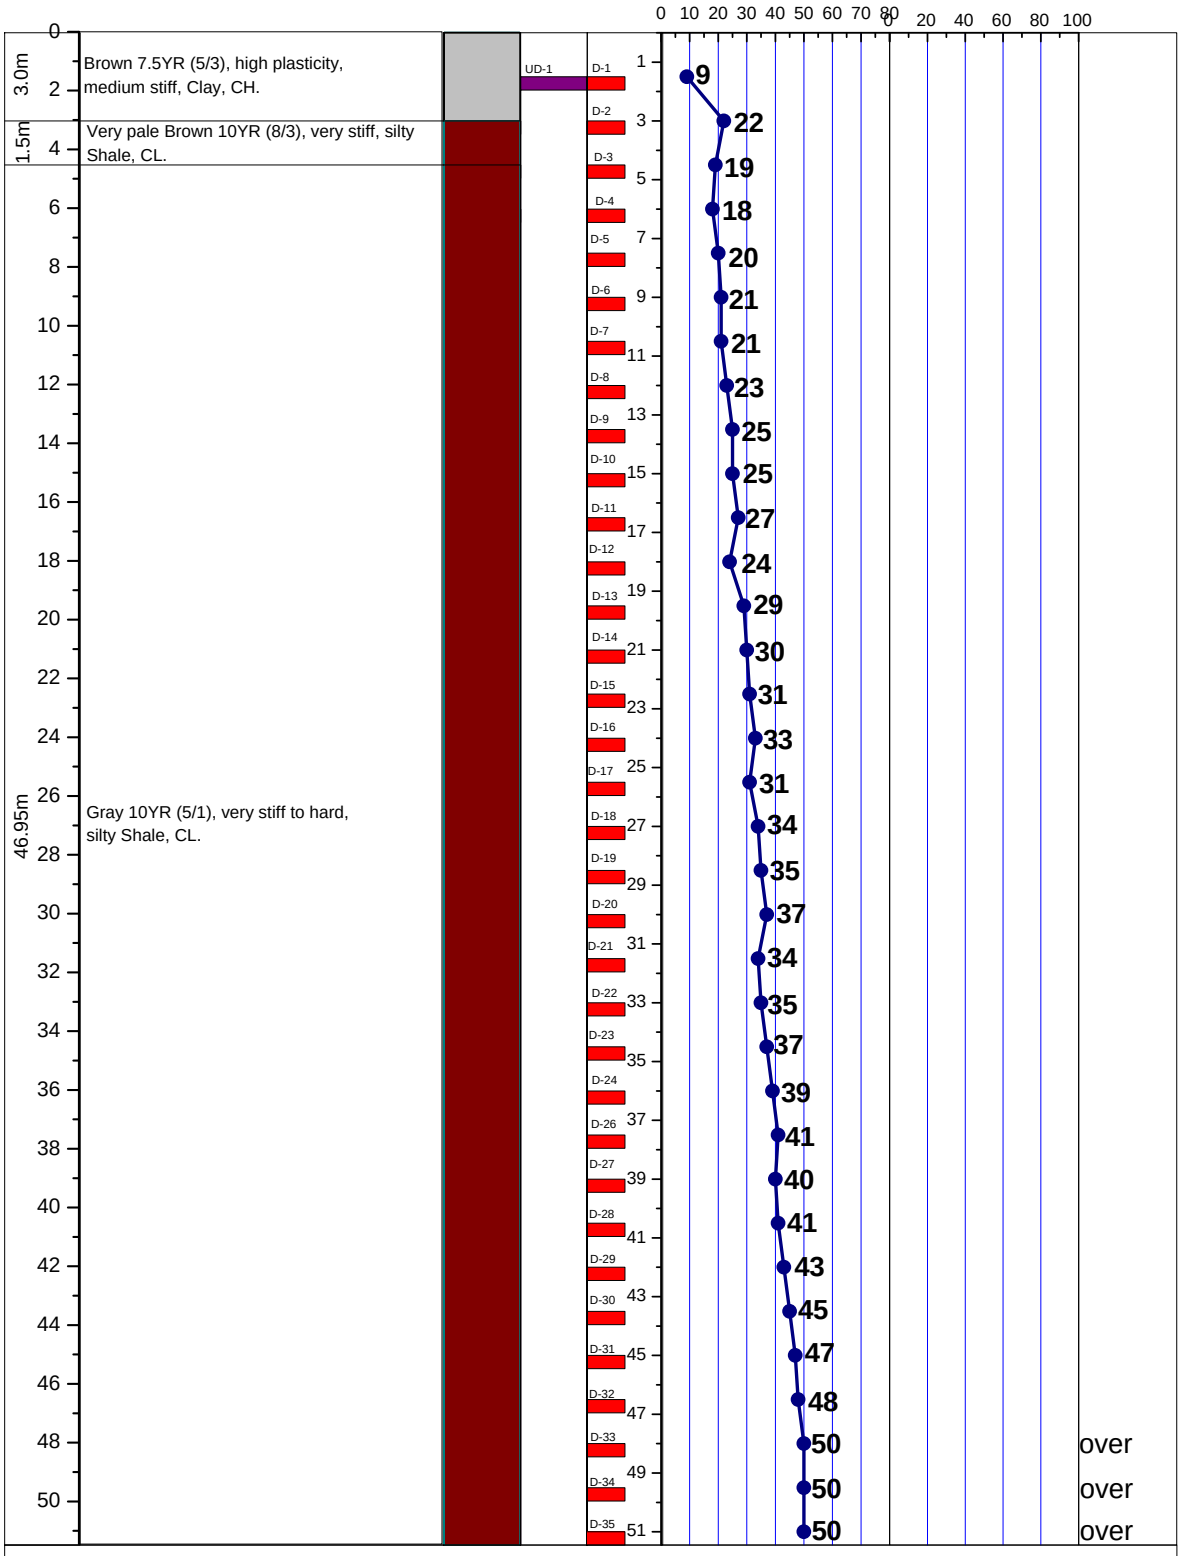


LEGEND FOR BORELOG AND GRAIN SIZE DISTRIBUTION (BASED ON 'ASTM CLASSIFICATION D-2487')

PLASTIC CLAY	SILT	PEAT/HIGHLY ORGANIC SOIL	UNDISTURBED SAMPLE
MICACEOUS FINE SAND/SILT	SAND	SHALE	DISTURBED SAMPLE

N- BLOWS DELIVERED PER FOOT BY A 140 LB HAMMER FALLING 30 INCHES

MAX^{m} PENETRATION= 50 BLOWS. AFTER 50 BLOWS PENETRATION DEPTH WERE MEASURED

A2	PROSOIL	BOREHOLE NO: BH-1	
		LOCATION : South Ledapara, Teknaf, Cox's Bazar.	
PROJECT : Telecommunication Tower.		DEPTH OF BORING : 51.0m	R. L.: 0.46m below from Road Level.
CLIENT : Warid Telecom International Ltd.		DATE OF BORING : 23-11-2010.	G. W. T : no existence of water table.

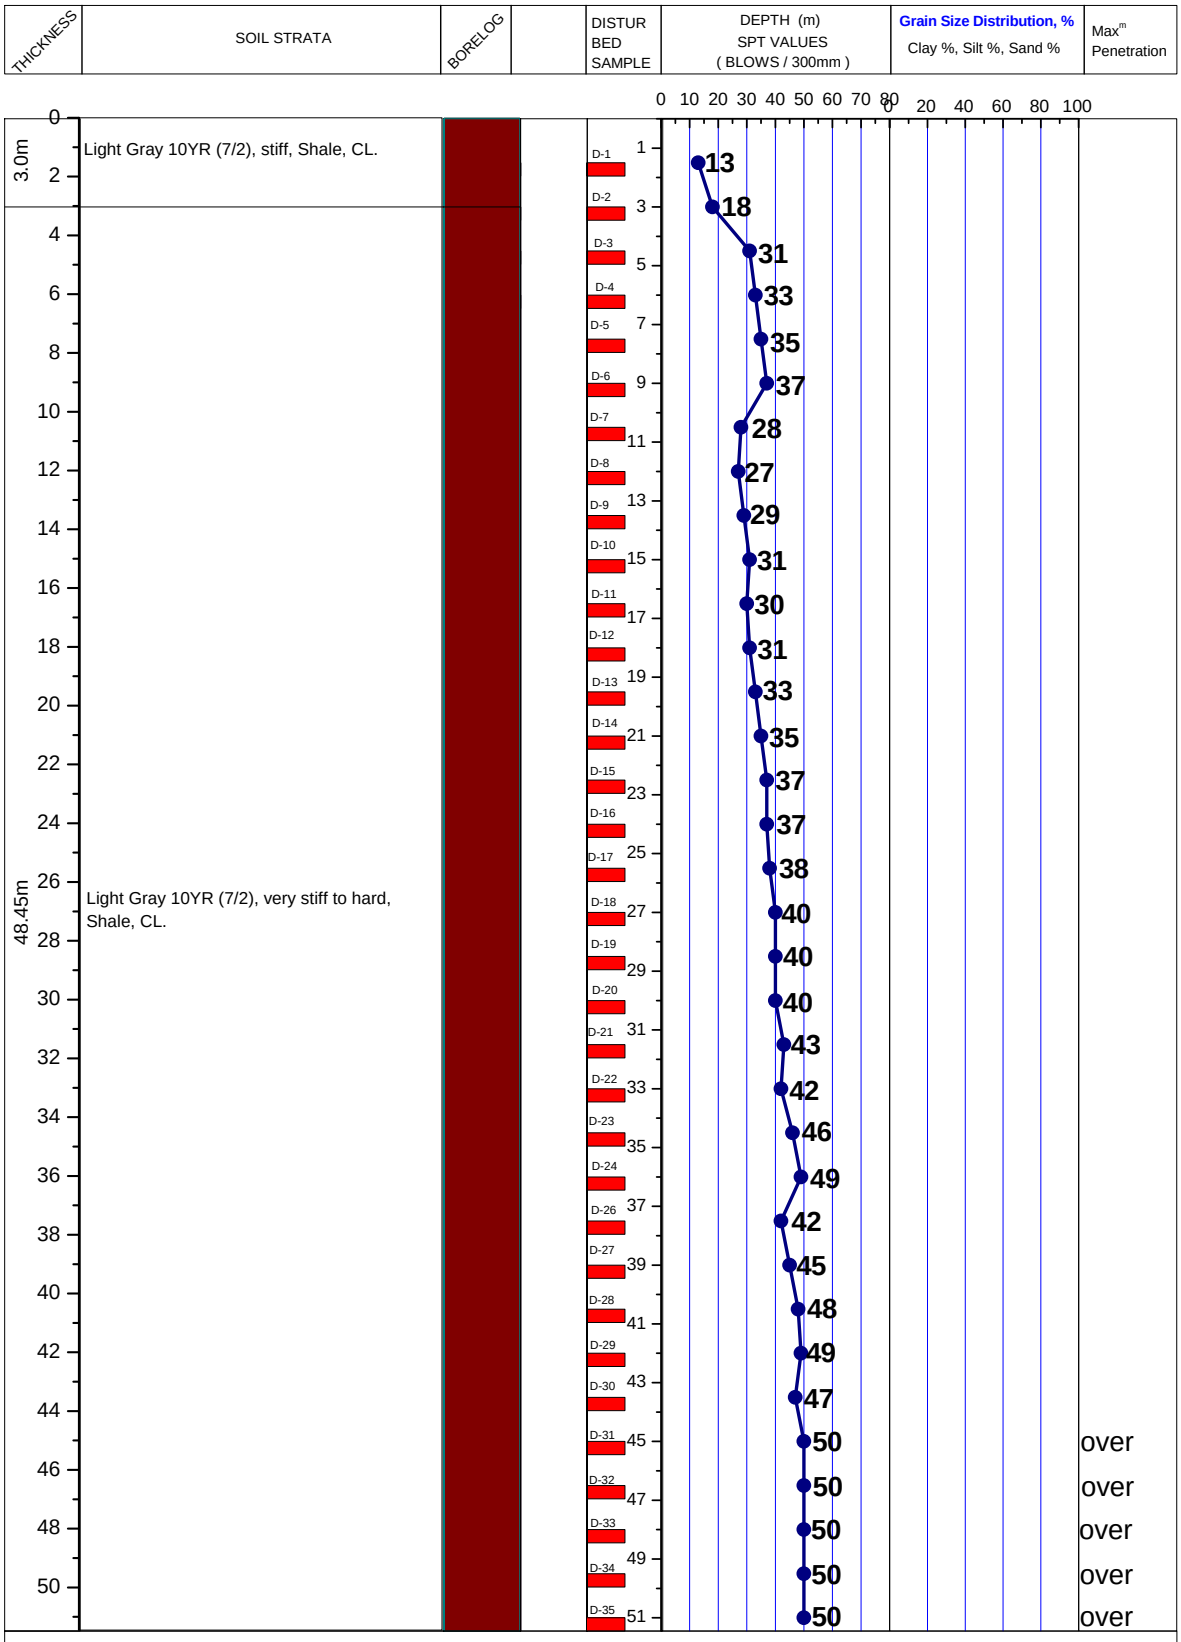


LEGEND FOR BORELOG AND GRAIN SIZE DISTRIBUTION (BASED ON 'ASTM CLASSIFICATION D-2487')

PLASTIC CLAY	SILT	PEAT/HIGHLY ORGANIC SOIL	UNDISTURBED SAMPLE
MICACEOUS FINE SAND/SILT	SAND	SHALE	DISTURBED SAMPLE

N- BLOWS DELIVERED PER FOOT BY A 140 LB HAMMER FALLING 30 INCHES

MAX^{m} PENETRATION= 50 BLOWS. AFTER 50 BLOWS PENETRATION DEPTH WERE MEASURED

A2 PROSOIL	BOREHOLE NO: BH-1	
	LOCATION : Shamlapur, Paharchara, Teknaf, Cox's Bazar.	
PROJECT : Telecommunication Tower.	DEPTH OF BORING : 51.0m	R. L.: On Road Level.
CLIENT : Warid Telecom International Ltd.	DATE OF BORING : 09-01-2011.	G. W. T : 2.44m below from E.G.L.

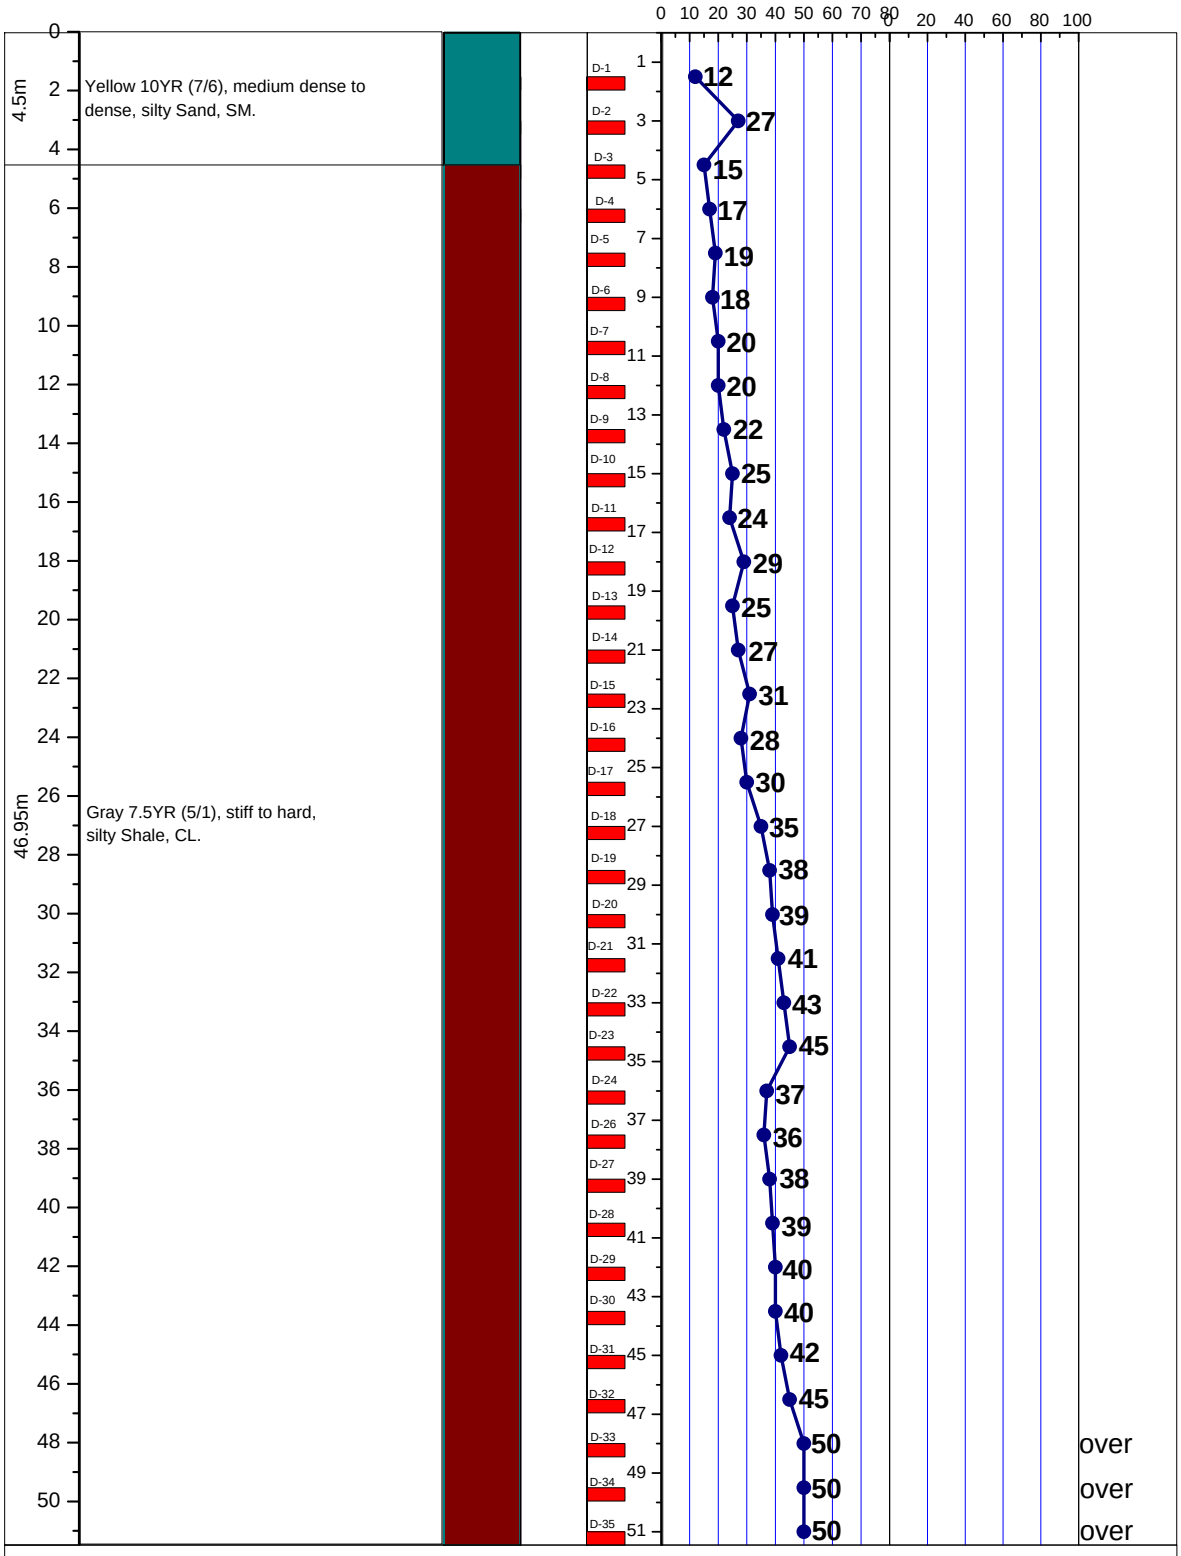


LEGEND FOR BORELOG AND GRAIN SIZE DISTRIBUTION (BASED ON 'ASTM CLASSIFICATION D-2487')

PLASTIC CLAY	SILT	PEAT/HIGHLY ORGANIC SOIL	UNDISTURBED SAMPLE
MICACEOUS FINE SAND/SILT	SAND	SHALE	DISTURBED SAMPLE

N- BLOWS DELIVERED PER FOOT BY A 140 LB HAMMER FALLING 30 INCHES

MAX^{m} PENETRATION= 50 BLOWS. AFTER 50 BLOWS PENETRATION DEPTH WERE MEASURED

A2	PROSOIL	BOREHOLE NO: BH-1	
		LOCATION : Baharchora, Teknaf, Cox's Bazar.	
PROJECT : Telecommunication Tower.		DEPTH OF BORING : 51.0m	R. L.: 0.91m below from Road Level.
CLIENT : Warid Telecom International Ltd.		DATE OF BORING : 02-08-2011.	G. W. T : 0.91m below from E.G.L.

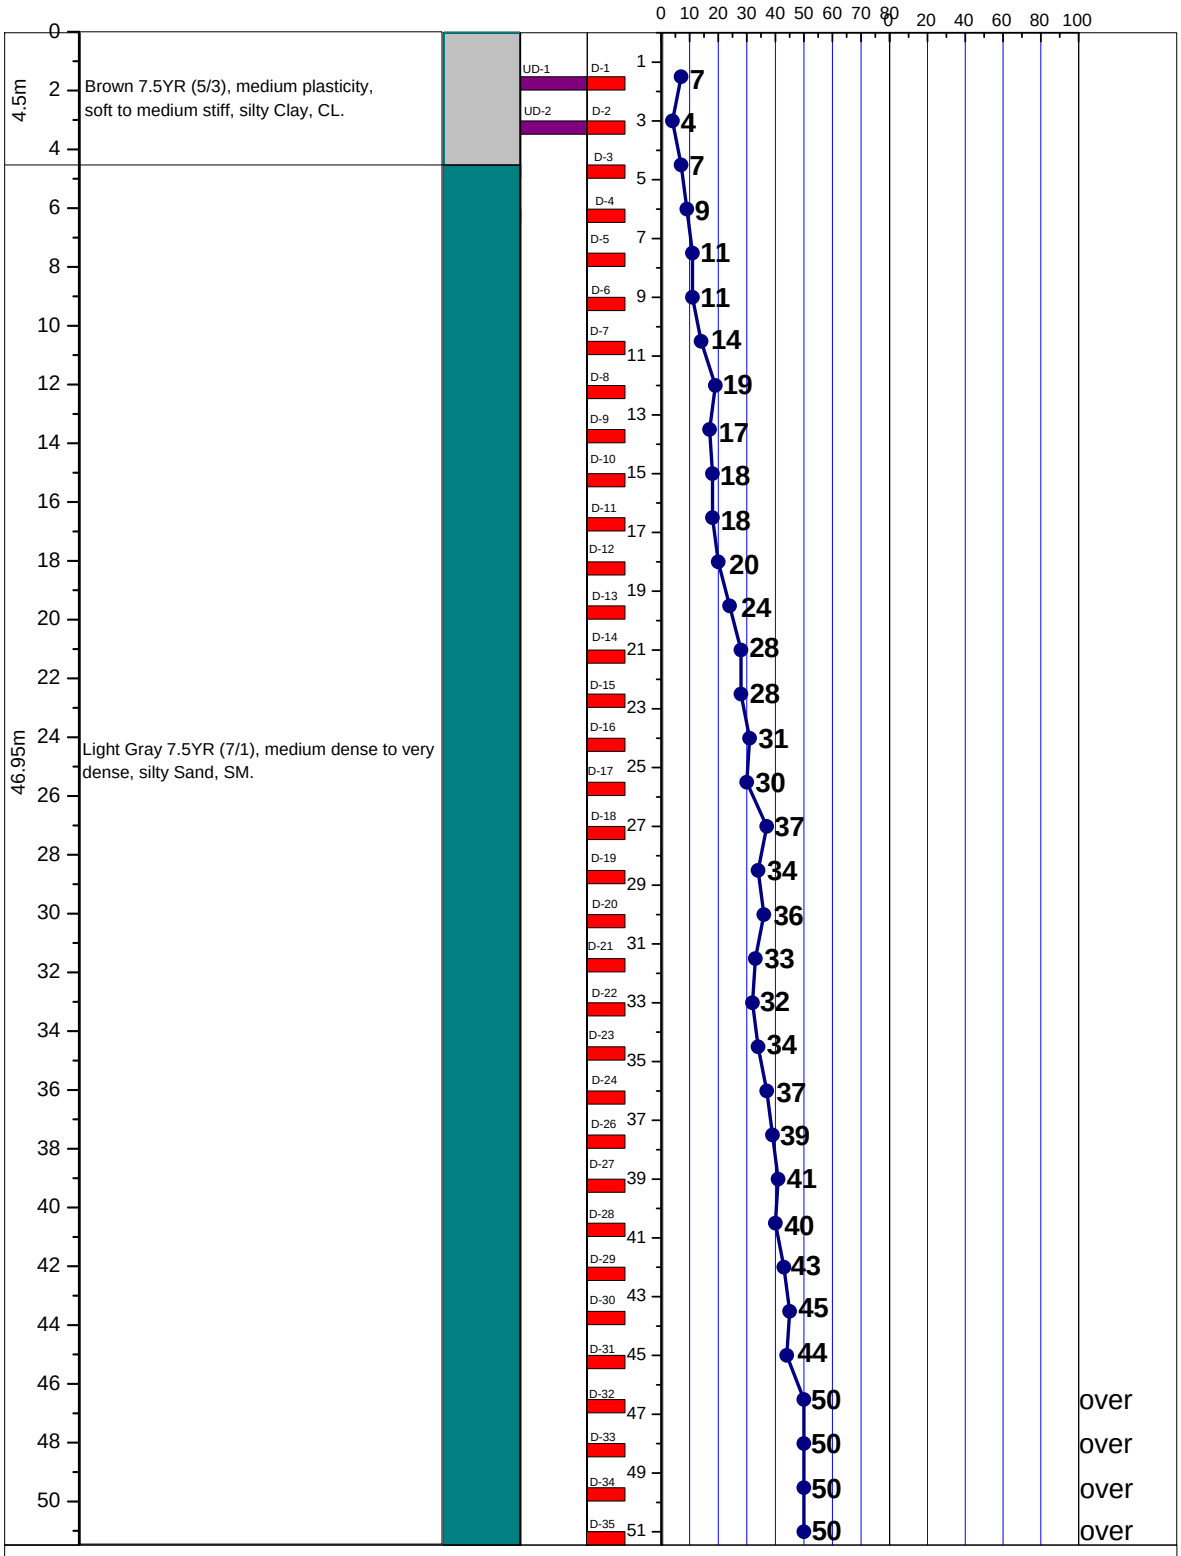


LEGEND FOR BORELOG AND GRAIN SIZE DISTRIBUTION (BASED ON 'ASTM CLASSIFICATION D-2487')

PLASTIC CLAY	SILT	PEAT/HIGHLY ORGANIC SOIL	UNDISTURBED SAMPLE
MICACEOUS FINE SAND/SILT	SAND	SHALE	DISTURBED SAMPLE

N- BLOWS DELIVERED PER FOOT BY A 140 LB HAMMER FALLING 30 INCHES

MAX^{m} PENETRATION= 50 BLOWS. AFTER 50 BLOWS PENETRATION DEPTH WERE MEASURED

A2	PROSOIL	BOREHOLE NO: BH-1	
		LOCATION : Mitha Panir Chara, Teknaf, Cox's Bazar.	
PROJECT : Telecommunication Tower.		DEPTH OF BORING : 51.0m	R. L.: On Road Level.
CLIENT : Warid Telecom International Ltd.		DATE OF BORING : 08-01-2011.	G. W. T : 0.91m below from E.G.L.

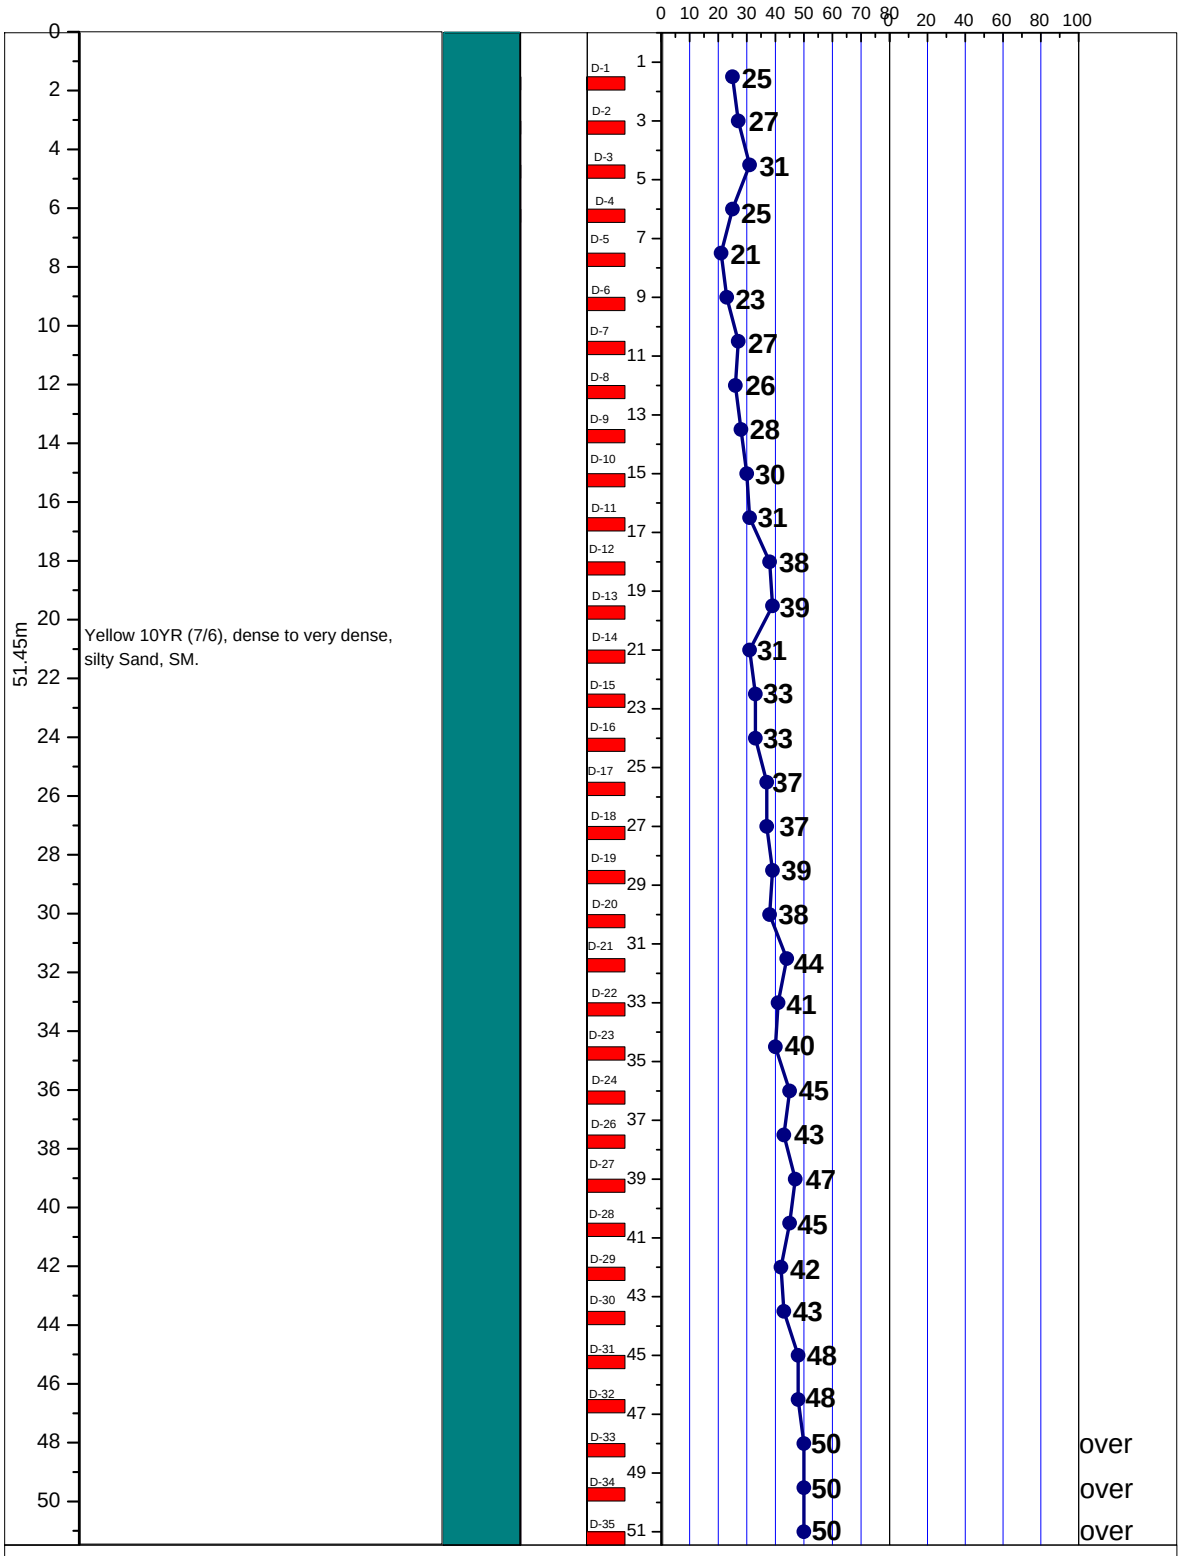


LEGEND FOR BORELOG AND GRAIN SIZE DISTRIBUTION (BASED ON 'ASTM CLASSIFICATION D-2487')

PLASTIC CLAY	SILT	PEAT/HIGHLY ORGANIC SOIL	UNDISTURBED SAMPLE
MICACEOUS FINE SAND/SILT	SAND	SHALE	DISTURBED SAMPLE

N- BLOWS DELIVERED PER FOOT BY A 140 LB HAMMER FALLING 30 INCHES

MAX^{m} PENETRATION= 50 BLOWS. AFTER 50 BLOWS PENETRATION DEPTH WERE MEASURED

A2	PROSOIL	BOREHOLE NO: BH-1	
		LOCATION : Mitha Panir Chara, Teknaf, Cox's Bazar.	
PROJECT : Telecommunication Tower.		DEPTH OF BORING : 51.0m	R. L.: 0.90m below from Road Level.
CLIENT : Warid Telecom International Ltd.		DATE OF BORING : 28-10-2011.	G. W. T : 1.52m below from E.G.L.

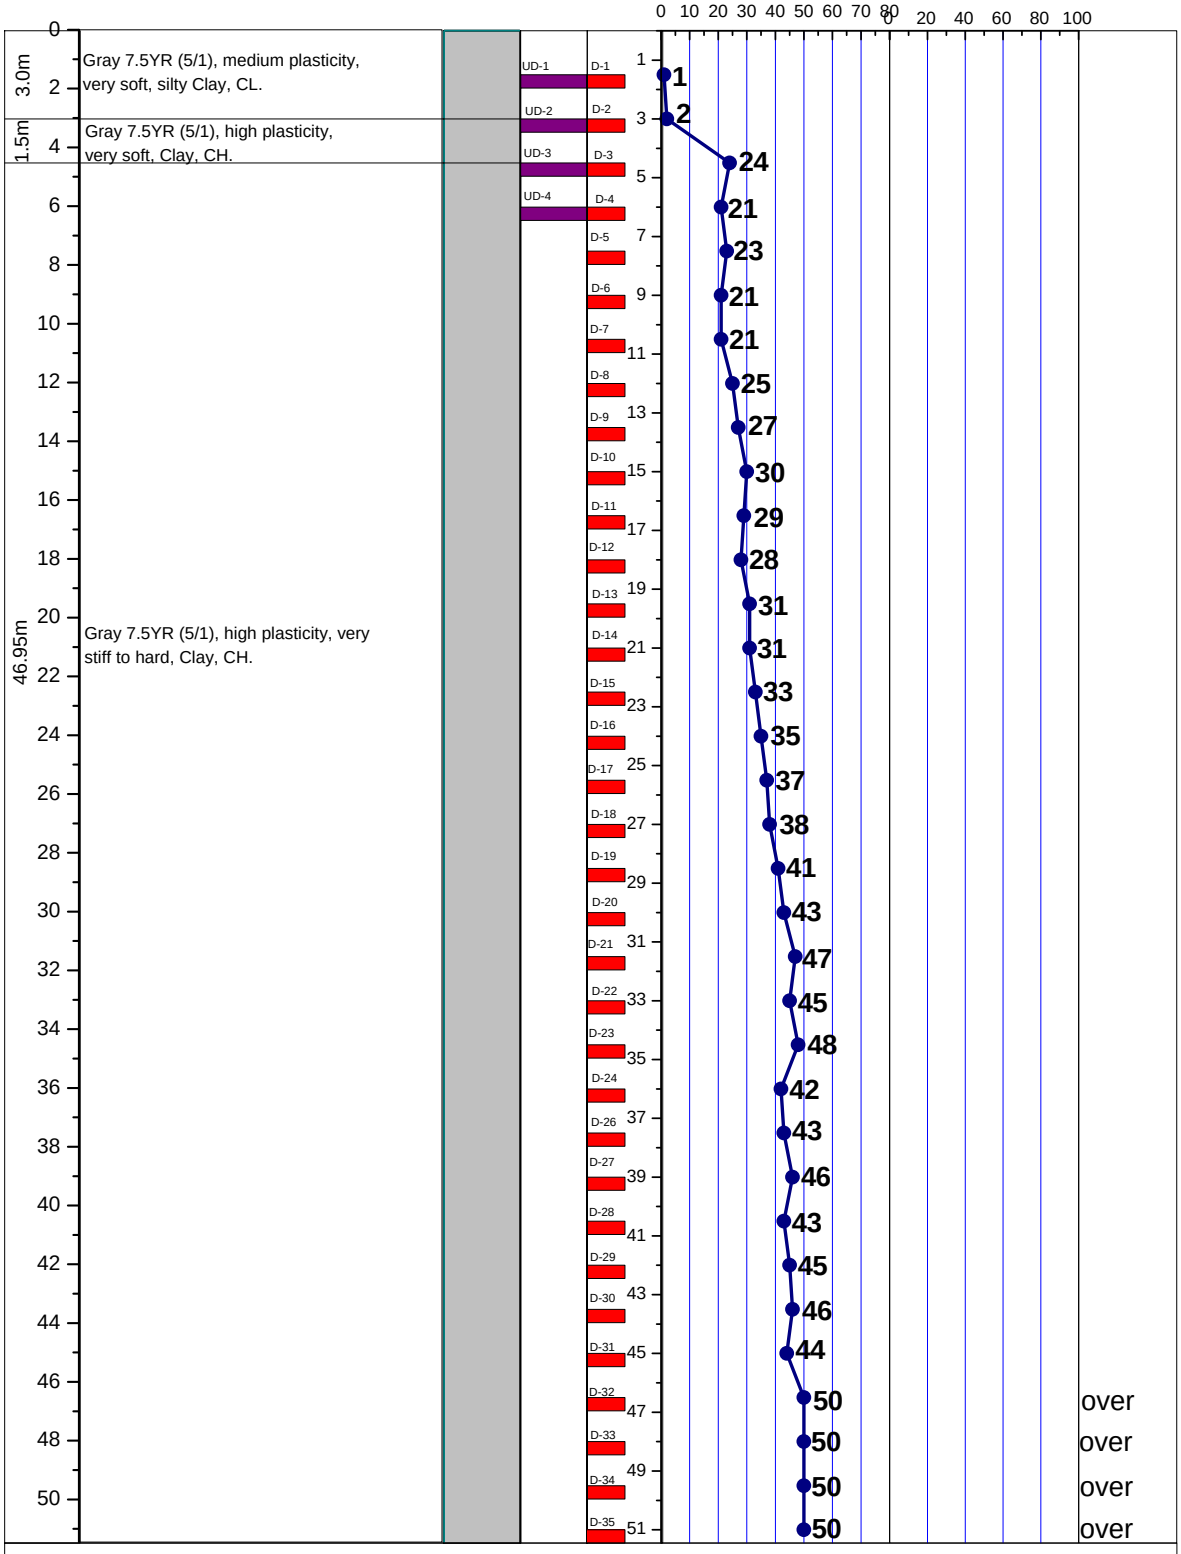


LEGEND FOR BORELOG AND GRAIN SIZE DISTRIBUTION (BASED ON 'ASTM CLASSIFICATION D-2487')

PLASTIC CLAY	SILT	PEAT/HIGHLY ORGANIC SOIL	UNDISTURBED SAMPLE
MICACEOUS FINE SAND/SILT	SAND	SHALE	DISTURBED SAMPLE

N- BLOWS DELIVERED PER FOOT BY A 140 LB HAMMER FALLING 30 INCHES

MAX^{m} PENETRATION= 50 BLOWS. AFTER 50 BLOWS PENETRATION DEPTH WERE MEASURED

A2 PROSOIL	BOREHOLE NO: BH-1	
	LOCATION : Ratna Palang, Court Bazar, Ukhai, Cox's Bazar.	
PROJECT : Telecommunication Tower.	DEPTH OF BORING : 51.0m	R. L.: 0.30m below from Road Level.
CLIENT : Warid Telecom International Ltd.	DATE OF BORING : 02-06-2011.	G. W. T : On E.G.L.

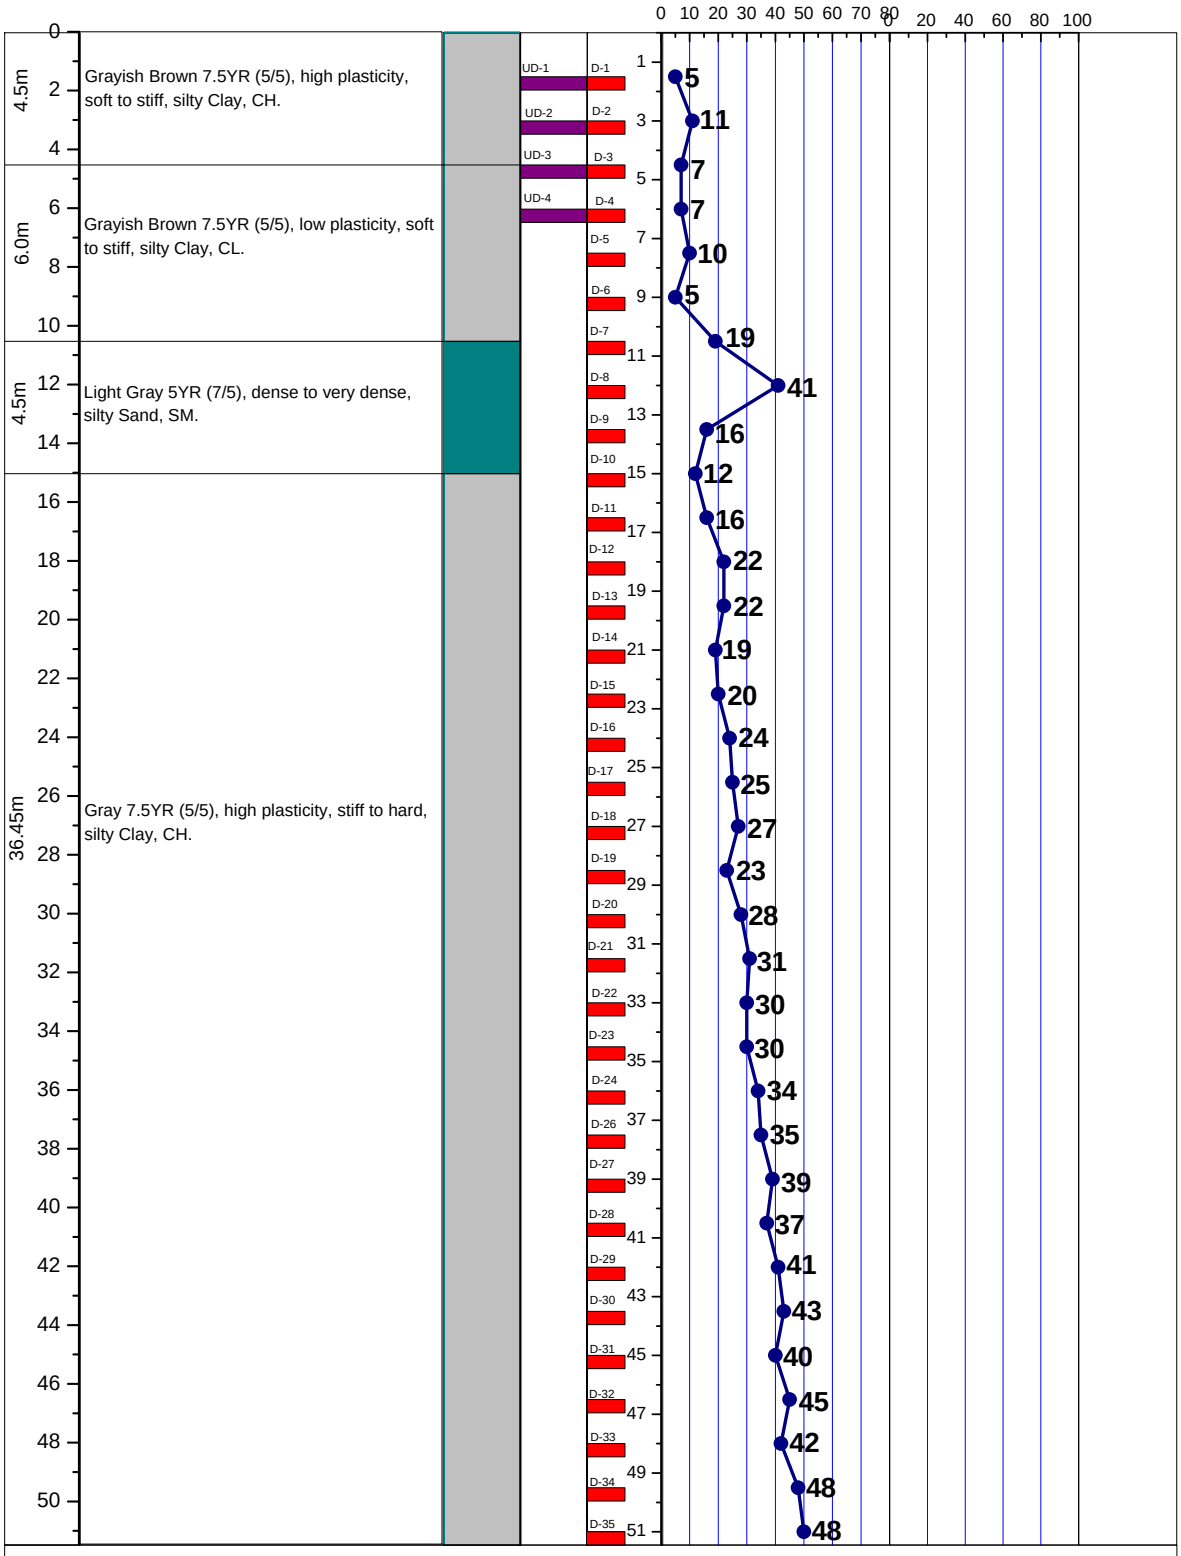


LEGEND FOR BORELOG AND GRAIN SIZE DISTRIBUTION (BASED ON 'ASTM CLASSIFICATION D-2487')

PLASTIC CLAY	SILT	PEAT/HIGHLY ORGANIC SOIL	UNDISTURBED SAMPLE
MICACEOUS FINE SAND/SILT	SAND	SHALE	DISTURBED SAMPLE

N- BLOWS DELIVERED PER FOOT BY A 140 LB HAMMER FALLING 30 INCHES

MAX^{m} PENETRATION= 50 BLOWS. AFTER 50 BLOWS PENETRATION DEPTH WERE MEASURED

A2	PROSOIL	BOREHOLE NO: BH-1	
		LOCATION : Hasherdighi (Ali Kadom Road), Fashiakandi, Chakoria, Cox's Bazar.	
PROJECT : Telecommunication Tower.		DEPTH OF BORING : 51.0m	R. L.: 1.22m below from Road Level.
CLIENT : Warid Telecom International Ltd.		DATE OF BORING : 05-05-2011.	G. W. T : 0.15m above from E.G.L.

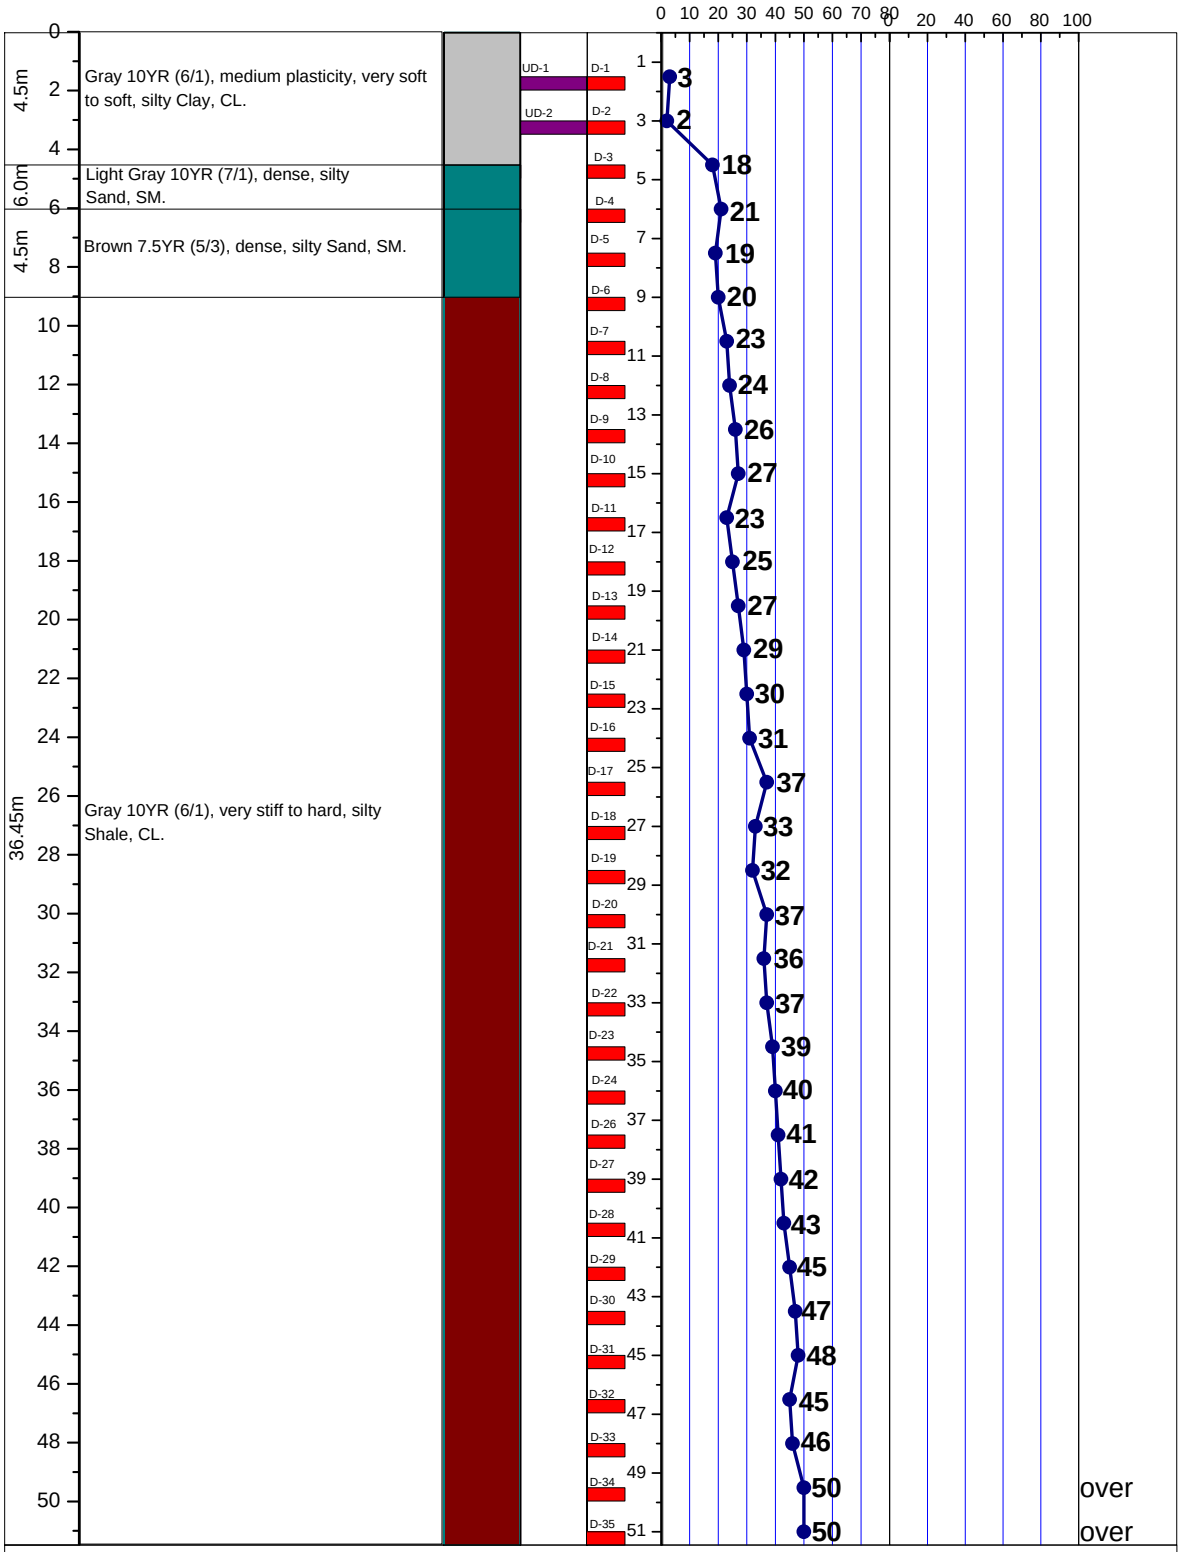


LEGEND FOR BORELOG AND GRAIN SIZE DISTRIBUTION (BASED ON 'ASTM CLASSIFICATION D-2487')

PLASTIC CLAY	SILT	PEAT/HIGHLY ORGANIC SOIL	UNDISTURBED SAMPLE
MICACEOUS FINE SAND/SILT	SAND	SHALE	DISTURBED SAMPLE

N- BLOWS DELIVERED PER FOOT BY A 140 LB HAMMER FALLING 30 INCHES

MAX^{m} PENETRATION= 50 BLOWS. AFTER 50 BLOWS PENETRATION DEPTH WERE MEASURED

A2 PROSOIL	BOREHOLE NO: BH-1	
	LOCATION : Kakara, Chakoria, Cox's bazar.	
PROJECT : Telecommunication Tower.	DEPTH OF BORING : 51.0m	R. L.: On Road Level.
CLIENT : Warid Telecom International Ltd.	DATE OF BORING : 11-09-2011.	G. W. T : 3.05m below from E.G.L.

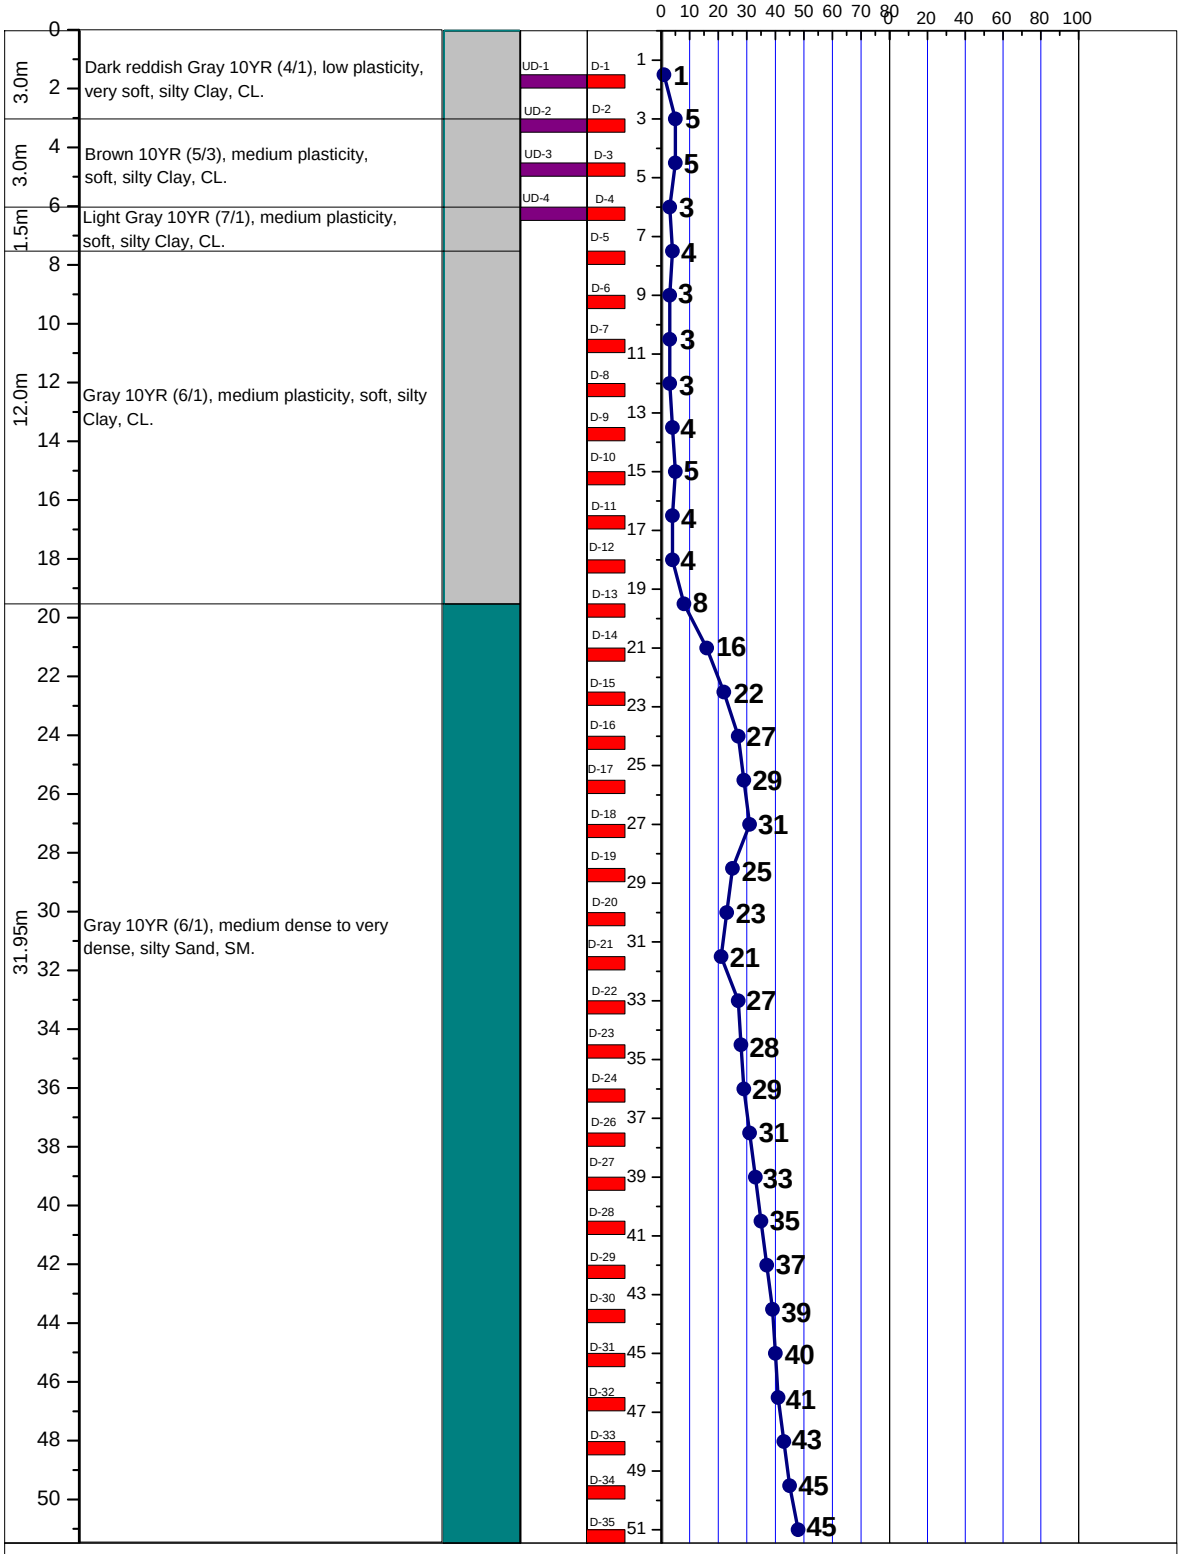


LEGEND FOR BORELOG AND GRAIN SIZE DISTRIBUTION (BASED ON 'ASTM CLASSIFICATION D-2487')

PLASTIC CLAY	SILT	PEAT/HIGHLY ORGANIC SOIL	UNDISTURBED SAMPLE
MICACEOUS FINE SAND/SILT	SAND	SHALE	DISTURBED SAMPLE

N- BLOWS DELIVERED PER FOOT BY A 140 LB HAMMER FALLING 30 INCHES

MAX^{m} PENETRATION= 50 BLOWS. AFTER 50 BLOWS PENETRATION DEPTH WERE MEASURED

A2 PROSOIL	BOREHOLE NO: BH-1	
	LOCATION : Matbor para, Kutubdia, Cox's Bazar.	
PROJECT : Telecommunication Tower.	DEPTH OF BORING : 51.0m	R. L.: 0.91m below from Road Level.
CLIENT : Warid Telecom International Ltd.	DATE OF BORING : 04-06-2011.	G. W. T : 1.83m below from E.G.L.

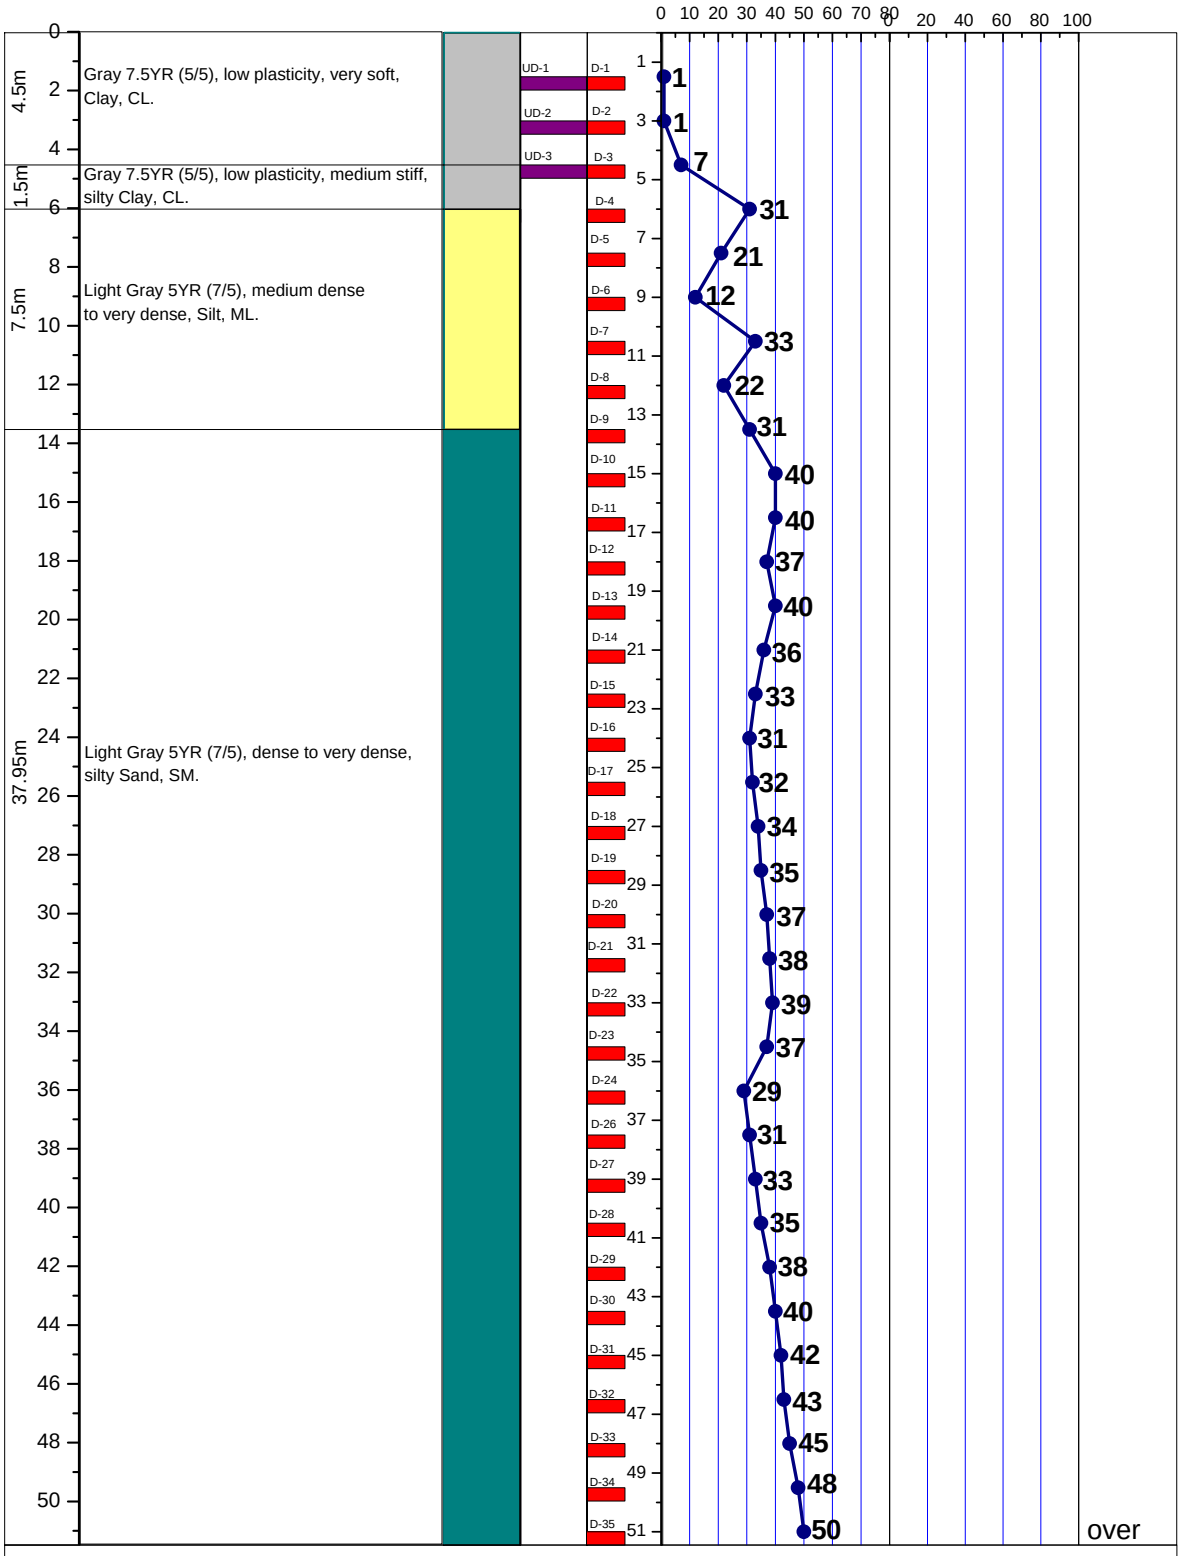


LEGEND FOR BORELOG AND GRAIN SIZE DISTRIBUTION (BASED ON 'ASTM CLASSIFICATION D-2487')

PLASTIC CLAY	SILT	PEAT/HIGHLY ORGANIC SOIL	UNDISTURBED SAMPLE
MICACEOUS FINE SAND/SILT	SAND	SHALE	DISTURBED SAMPLE

N- BLOWS DELIVERED PER FOOT BY A 140 LB HAMMER FALLING 30 INCHES

MAX^{m} PENETRATION= 50 BLOWS. AFTER 50 BLOWS PENETRATION DEPTH WERE MEASURED

A2 PROSOIL	BOREHOLE NO: BH-1	
	LOCATION : South Rajghat, Matarbari, Mohesh Khali, Cox's Bazar.	
PROJECT : Telecommunication Tower.	DEPTH OF BORING : 51.0m	R. L.: 0.91m below from Road Level.
CLIENT : Warid Telecom International Ltd.	DATE OF BORING : 07-05-2011.	G. W. T : 2.44m below from E.G.L.

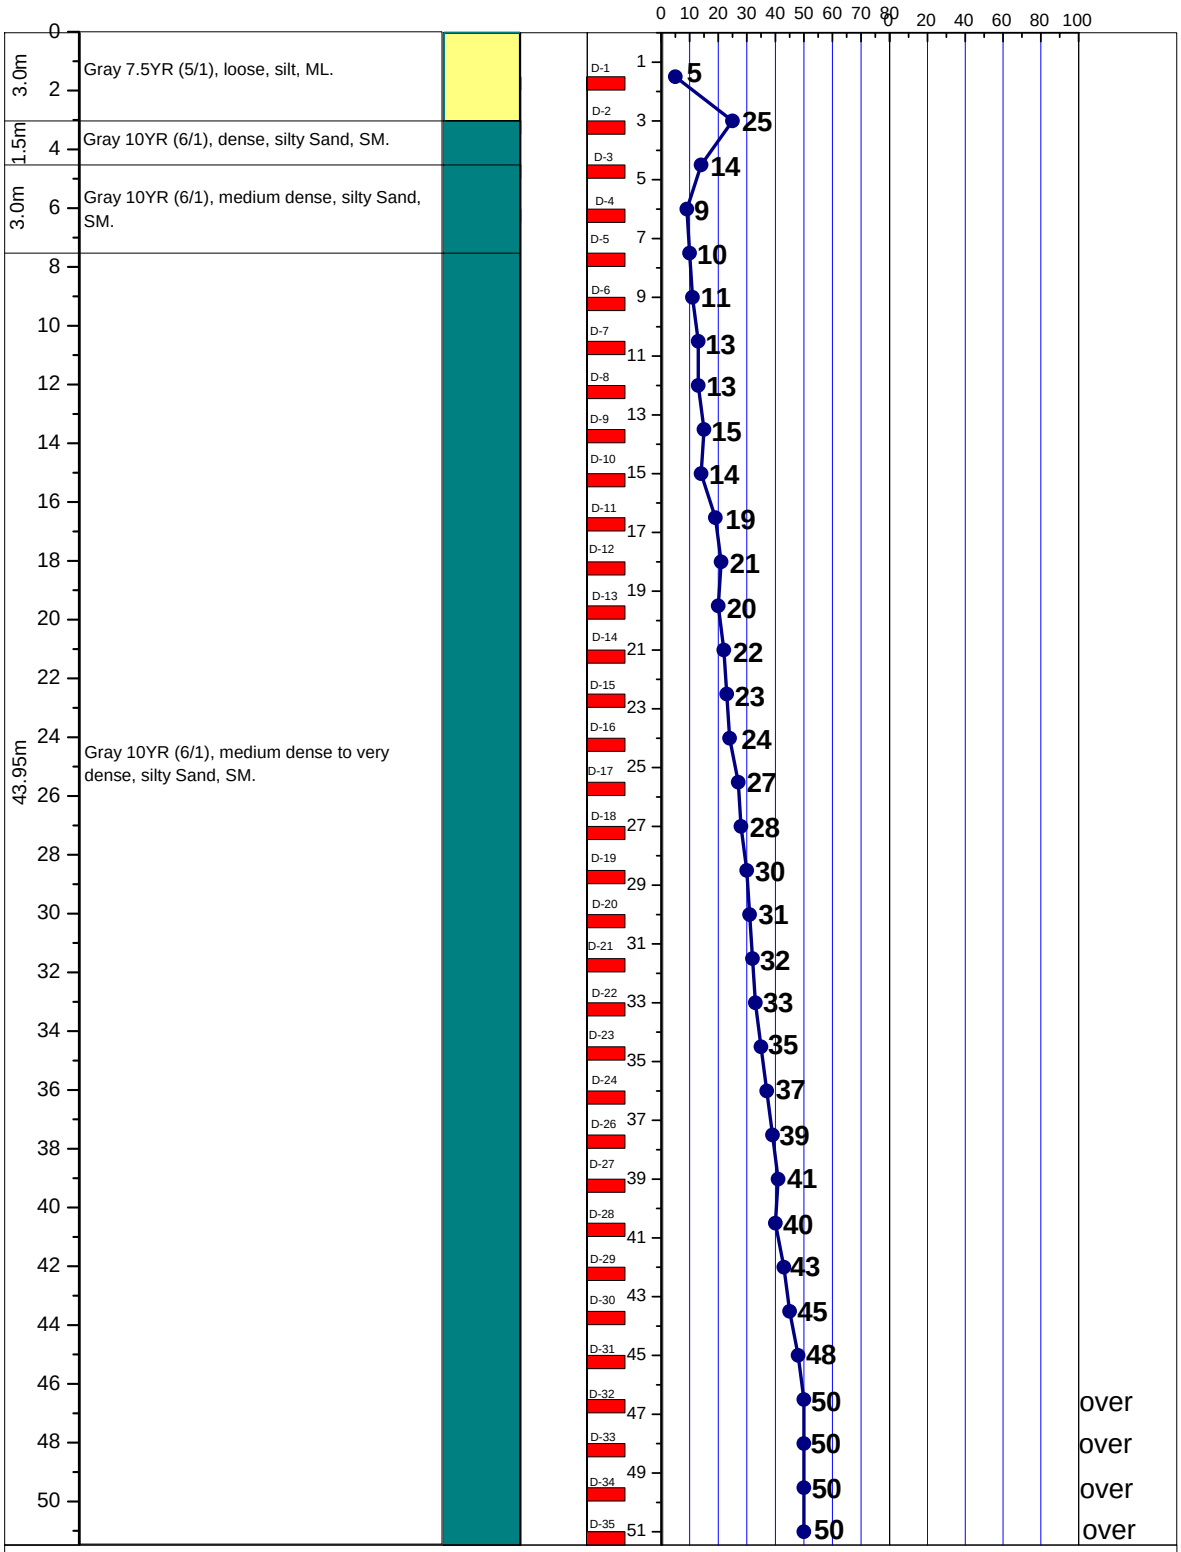


LEGEND FOR BORELOG AND GRAIN SIZE DISTRIBUTION (BASED ON 'ASTM CLASSIFICATION D-2487')

PLASTIC CLAY	SILT	PEAT/HIGHLY ORGANIC SOIL	UNDISTURBED SAMPLE
MICACEOUS FINE SAND/SILT	SAND	SHALE	DISTURBED SAMPLE

N- BLOWS DELIVERED PER FOOT BY A 140 LB HAMMER FALLING 30 INCHES

MAX^{m} PENETRATION= 50 BLOWS. AFTER 50 BLOWS PENETRATION DEPTH WERE MEASURED

A2 PROSOIL	BOREHOLE NO: BH-1	
	LOCATION : Shaplapur, Moheskhali, Cox's Bazar.	
PROJECT : Telecommunication Tower.	DEPTH OF BORING : 51.0m	R. L.: 1.07m below from Road Level.
CLIENT : Warid Telecom International Ltd.	DATE OF BORING : 05-07-2011.	G. W. T : On E.G.L.

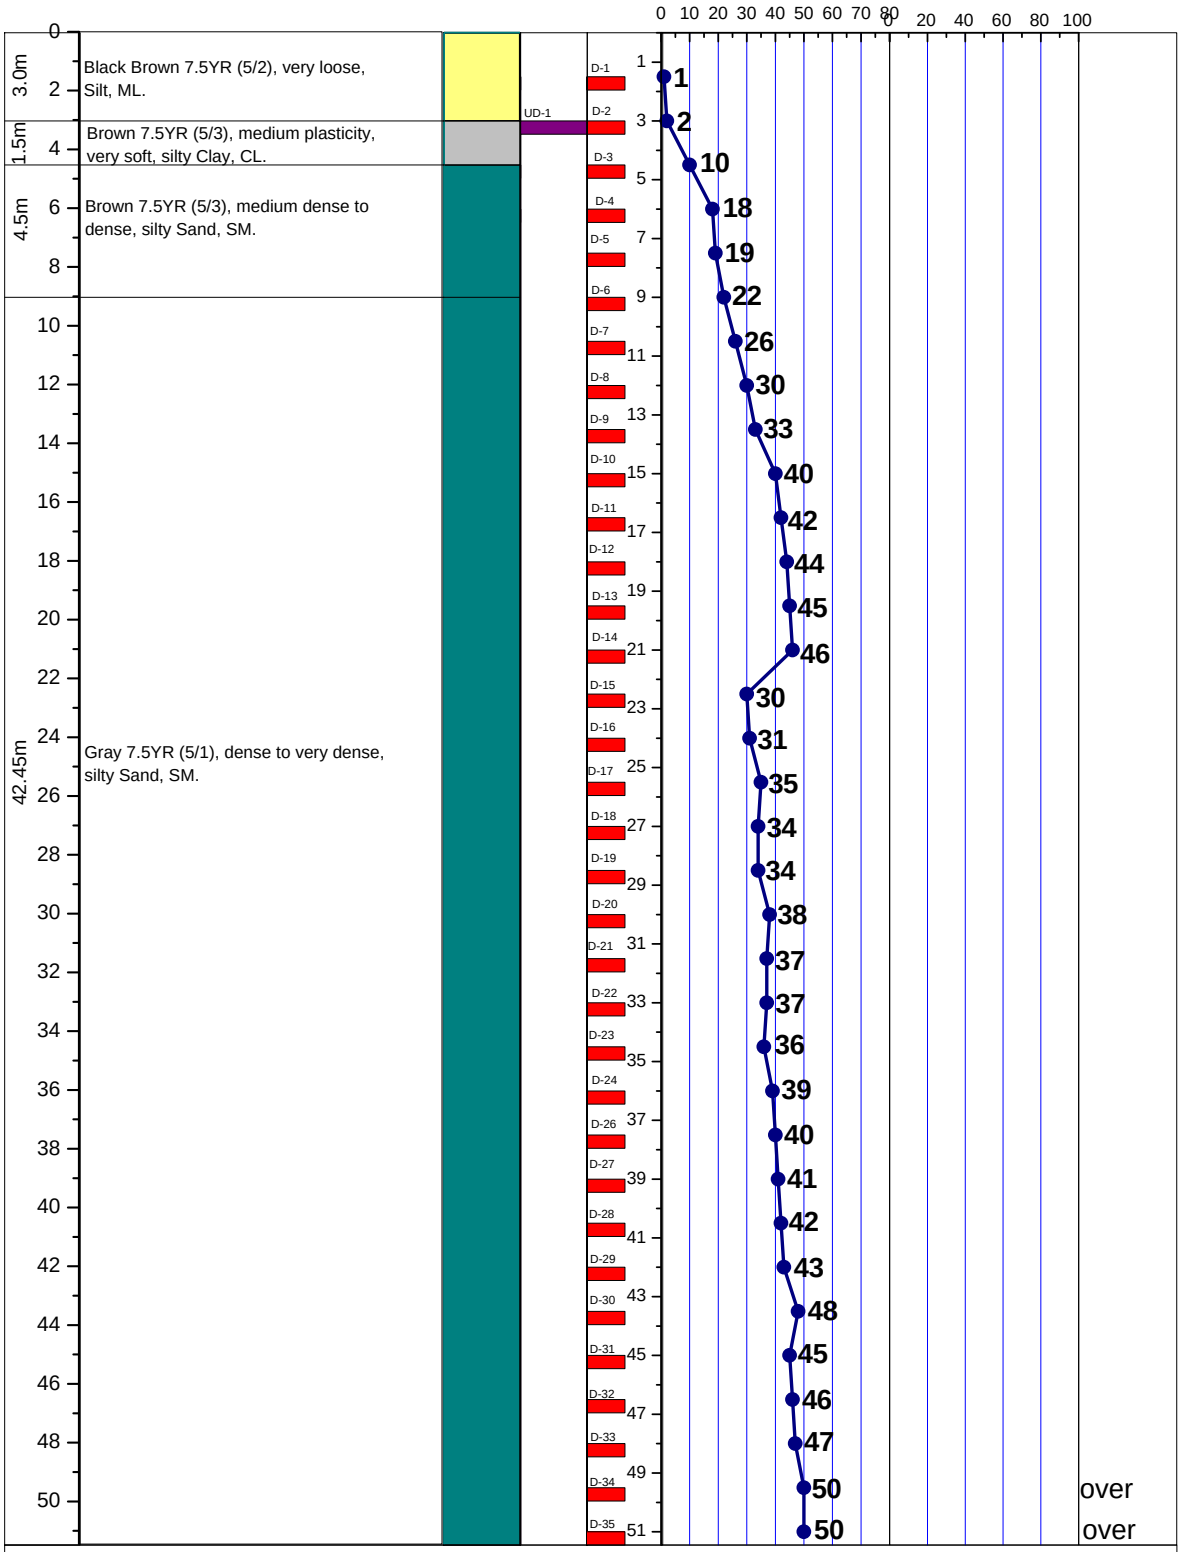

LEGEND FOR BORELOG AND GRAIN SIZE DISTRIBUTION (BASED ON 'ASTM CLASSIFICATION D-2487')

PLASTIC CLAY	SILT	PEAT/HIGHLY ORGANIC SOIL	UNDISTURBED SAMPLE
MICACEOUS FINE SAND/SILT	SAND	SHALE	DISTURBED SAMPLE

N- BLOWS DELIVERED PER FOOT BY A 140 LB HAMMER FALLING 30 INCHES

MAX^{m} PENETRATION= 50 BLOWS. AFTER 50 BLOWS PENETRATION DEPTH WERE MEASURED

A2	PROSOIL	BOREHOLE NO: BH-1	
		LOCATION : Mognama Napitardia, Pekua, Cox's Bazar.	
PROJECT : Telecommunication Tower.		DEPTH OF BORING : 51.0m	R. L.: On Road Level.
CLIENT : Warid Telecom International Ltd.		DATE OF BORING : 04-05-2011.	G. W. T : 2.74m below from E.G.L.

THICKNESS	SOIL STRATA	BORELOG	DISTURBED SAMPLE	DEPTH (m) SPT VALUES (BLOWS / 300mm)	Grain Size Distribution, % Clay %, Silt %, Sand %	Max^{m} Penetration
3.0m	Light Gray 10YR (7/1), medium plasticity, very soft, silty Clay, CL.		UD-1, UD-2, D-1, D-2	2, 2		
1.5m	Dark Gray 10YR (4/1), medium plasticity, very soft, Clay, CL.		D-3	1		
3.0m	Gray 10YR (6/1), very loose to loose, Silt, ML.		D-4, D-5	5, 16		
6.0m	Gray 10YR (6/1), dense to very dense, Silt, ML.		D-6, D-7, D-8, D-9	18, 34, 21, 19		
1.5m	Gray 10YR (6/1), dense, silty Sand, SM.		D-10	7		
6.0m	Gray 10YR (6/1), medium plasticity, medium stiff, silty Clay, CL.		D-11, D-12, D-13, D-14	6, 6, 6, 13		
30.45m	Gray 10YR (5/1), medium dense to very dense, silty Sand, SM.		D-15, D-16, D-17, D-18, D-19, D-20, D-21, D-22, D-23, D-24, D-26, D-27, D-28, D-29, D-30, D-31, D-32, D-33, D-34, D-35	14, 15, 15, 17, 16, 19, 19, 21, 23, 23, 25, 27, 27, 29, 30, 33, 35, 37, 39, 45		

LEGEND FOR BORELOG AND GRAIN SIZE DISTRIBUTION (BASED ON 'ASTM CLASSIFICATION D-2487')


PLASTIC CLAY | SILT | PEAT/HIGHLY ORGANIC SOIL | UNDISTURBED SAMPLE

MICACEOUS FINE SAND/SILT | SAND | SHALE | DISTURBED SAMPLE

N- BLOWS DELIVERED PER FOOT BY A 140 LB HAMMER FALLING 30 INCHES

MAX^{m} PENETRATION= 50 BLOWS. AFTER 50 BLOWS PENETRATION DEPTH WERE MEASURED

A2 PROSOIL	BOREHOLE NO: BH-1	
	LOCATION : Taitang Bazar, Mognama, Pekua, Cox's Bazar.	
PROJECT : Telecommunication Tower.	DEPTH OF BORING : 51.0m	R. L.: 1.22m below from Road Level.
CLIENT : Warid Telecom International Ltd.	DATE OF BORING : 03-05-2011.	G. W. T : 0.46m below from E.G.L.

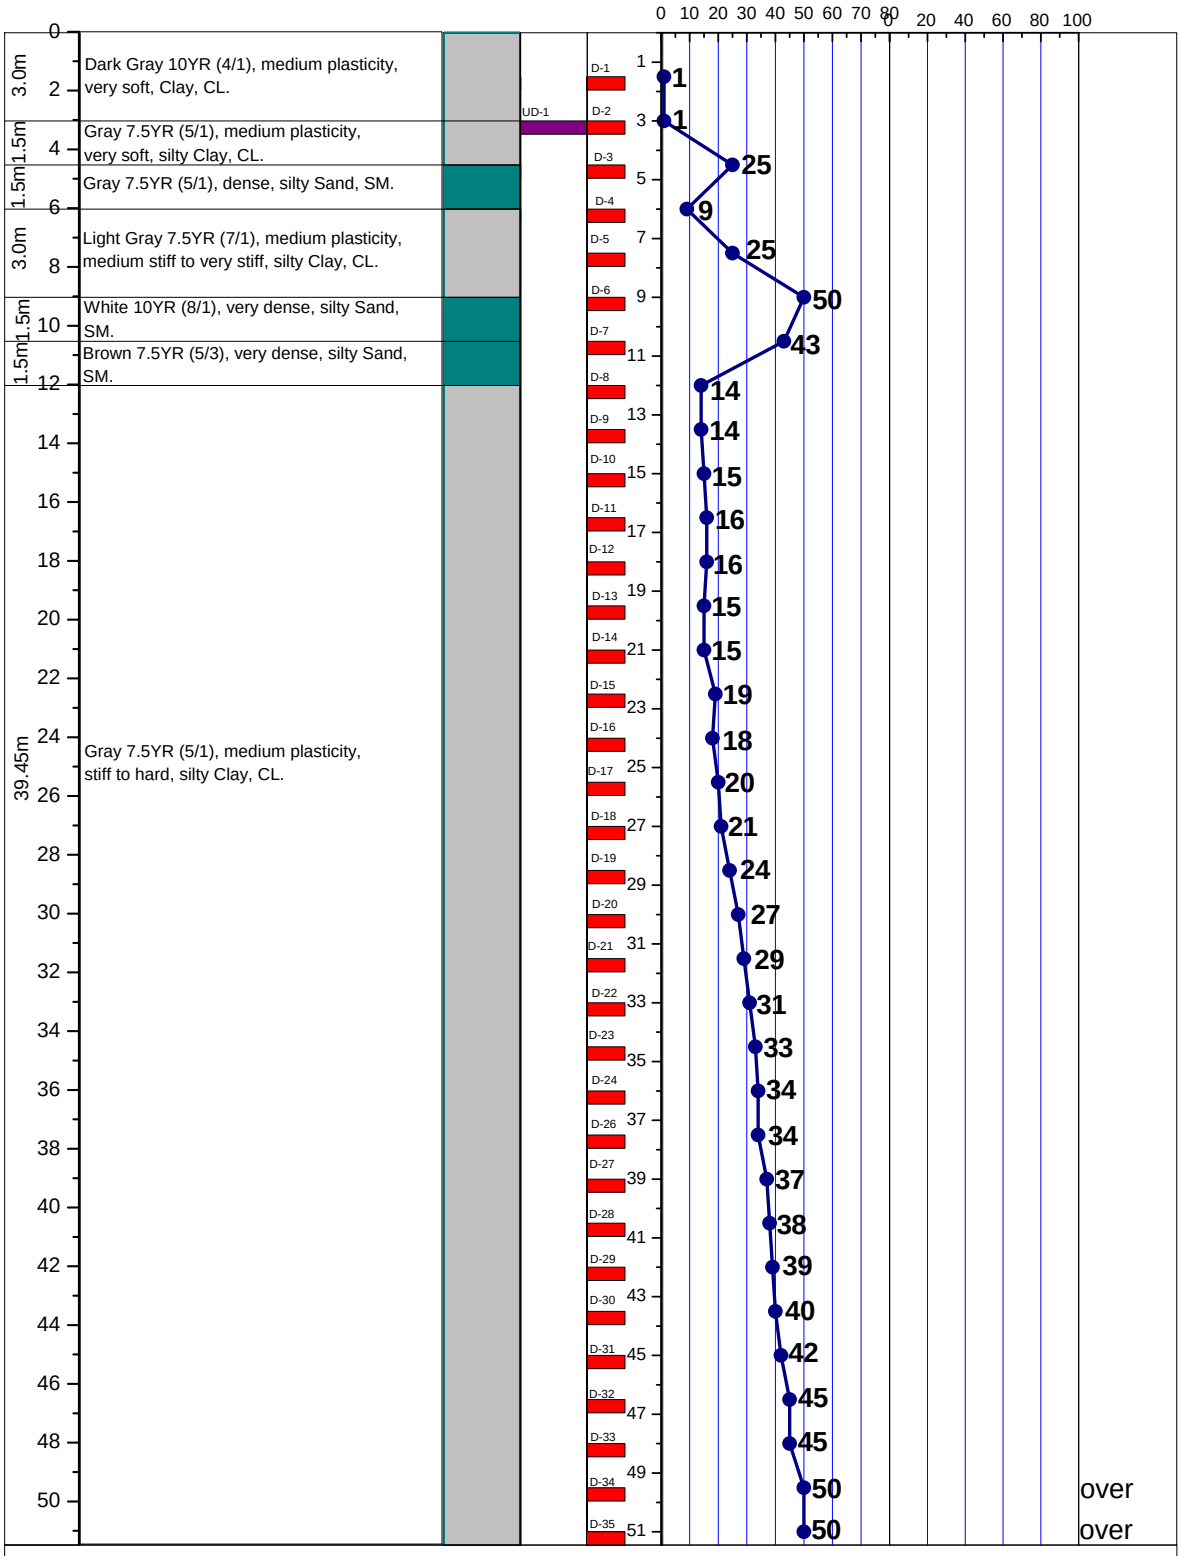


LEGEND FOR BORELOG AND GRAIN SIZE DISTRIBUTION (BASED ON 'ASTM CLASSIFICATION D-2487')

PLASTIC CLAY	SILT	PEAT/HIGHLY ORGANIC SOIL	UNDISTURBED SAMPLE
MICACEOUS FINE SAND/SILT	SAND	SHALE	DISTURBED SAMPLE

N- BLOWS DELIVERED PER FOOT BY A 140 LB HAMMER FALLING 30 INCHES

MAX^{m} PENETRATION= 50 BLOWS. AFTER 50 BLOWS PENETRATION DEPTH WERE MEASURED

A2 PROSOIL	BOREHOLE NO: BH-1	
	LOCATION : Eidgor, Bodormukham, Ramu, Cox's Bazar.	
PROJECT : Telecommunication Tower.	DEPTH OF BORING : 51.0m	R. L.: 1.52m below from Road Level.
CLIENT : Warid Telecom International Ltd.	DATE OF BORING : 15-05-2011.	G. W. T : 3.66m below from E.G.L.

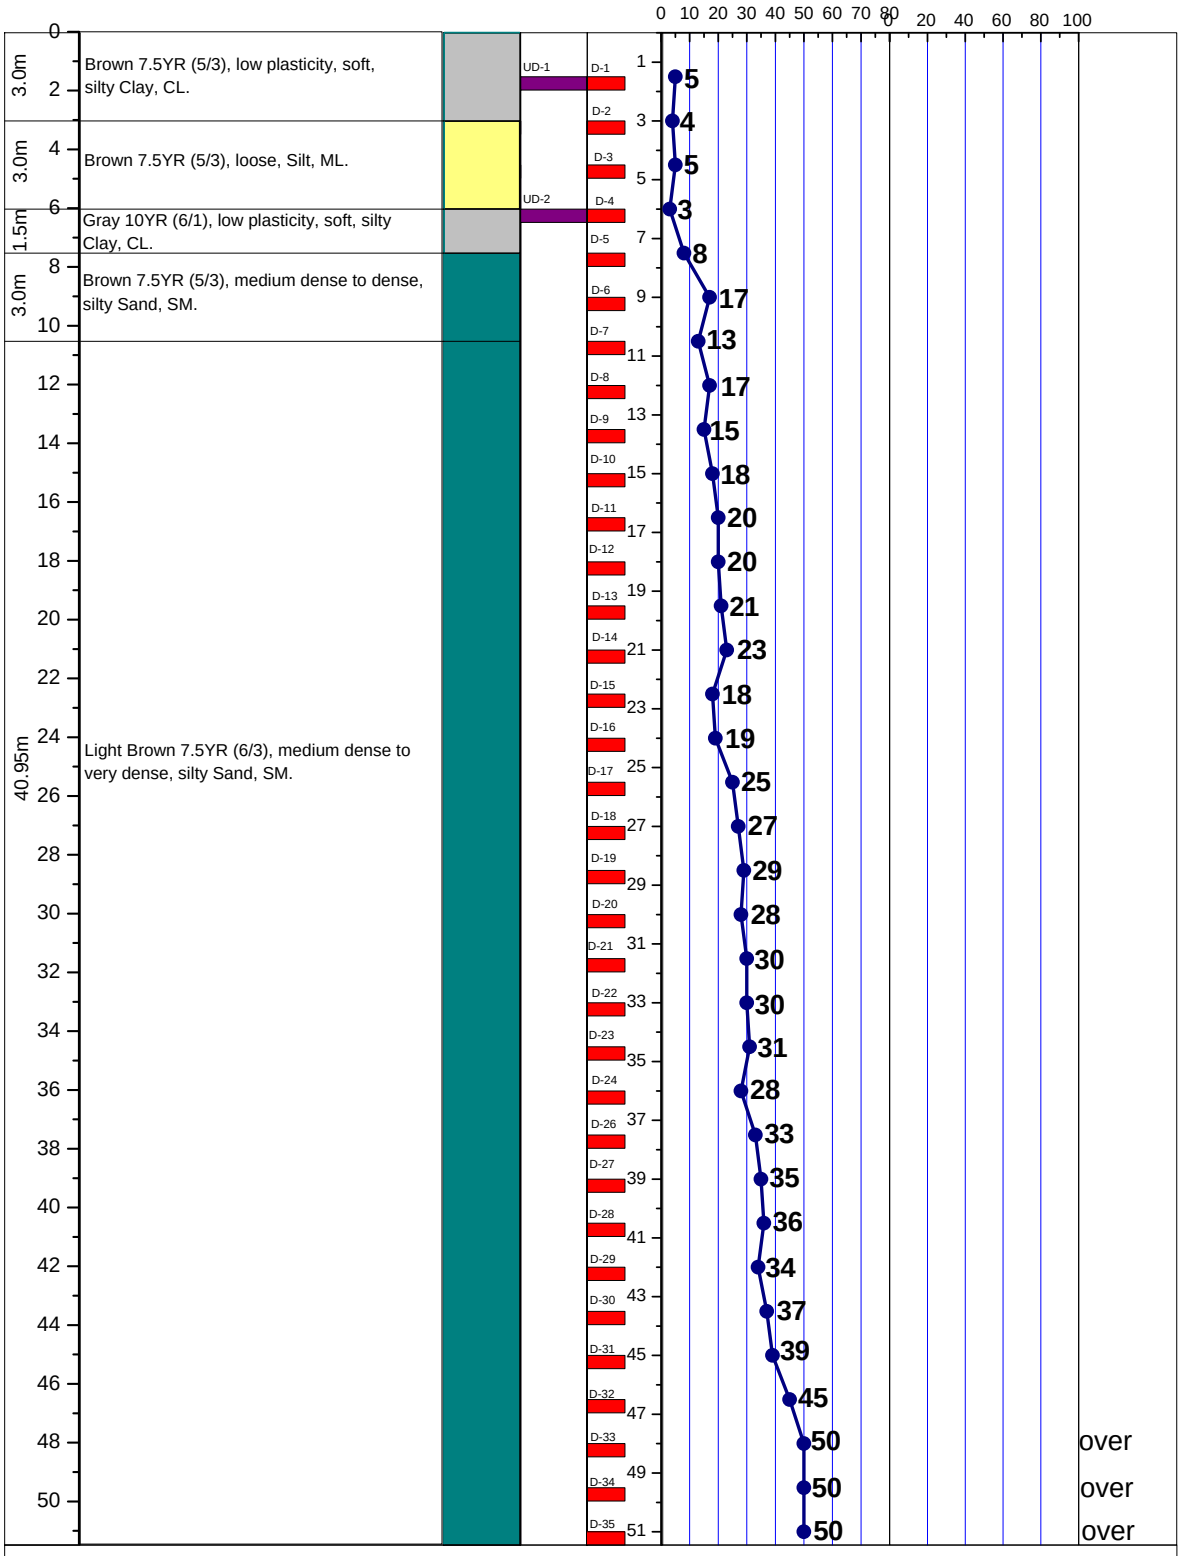


LEGEND FOR BORELOG AND GRAIN SIZE DISTRIBUTION (BASED ON 'ASTM CLASSIFICATION D-2487')

PLASTIC CLAY	SILT	PEAT/HIGHLY ORGANIC SOIL	UNDISTURBED SAMPLE
MICACEOUS FINE SAND/SILT	SAND	SHALE	DISTURBED SAMPLE

N- BLOWS DELIVERED PER FOOT BY A 140 LB HAMMER FALLING 30 INCHES

MAX^{m} PENETRATION= 50 BLOWS. AFTER 50 BLOWS PENETRATION DEPTH WERE MEASURED

A2 PROSOIL	BOREHOLE NO: BH-1	
	LOCATION : Ramkut, Ramu, Cox's Bazar.	
PROJECT : Telecommunication Tower.	DEPTH OF BORING : 51.0m	R. L.: 1.22m below from Road Level.
CLIENT : Warid Telecom International Ltd.	DATE OF BORING : 25-04-2011.	G. W. T : 0.91m below from E.G.L.

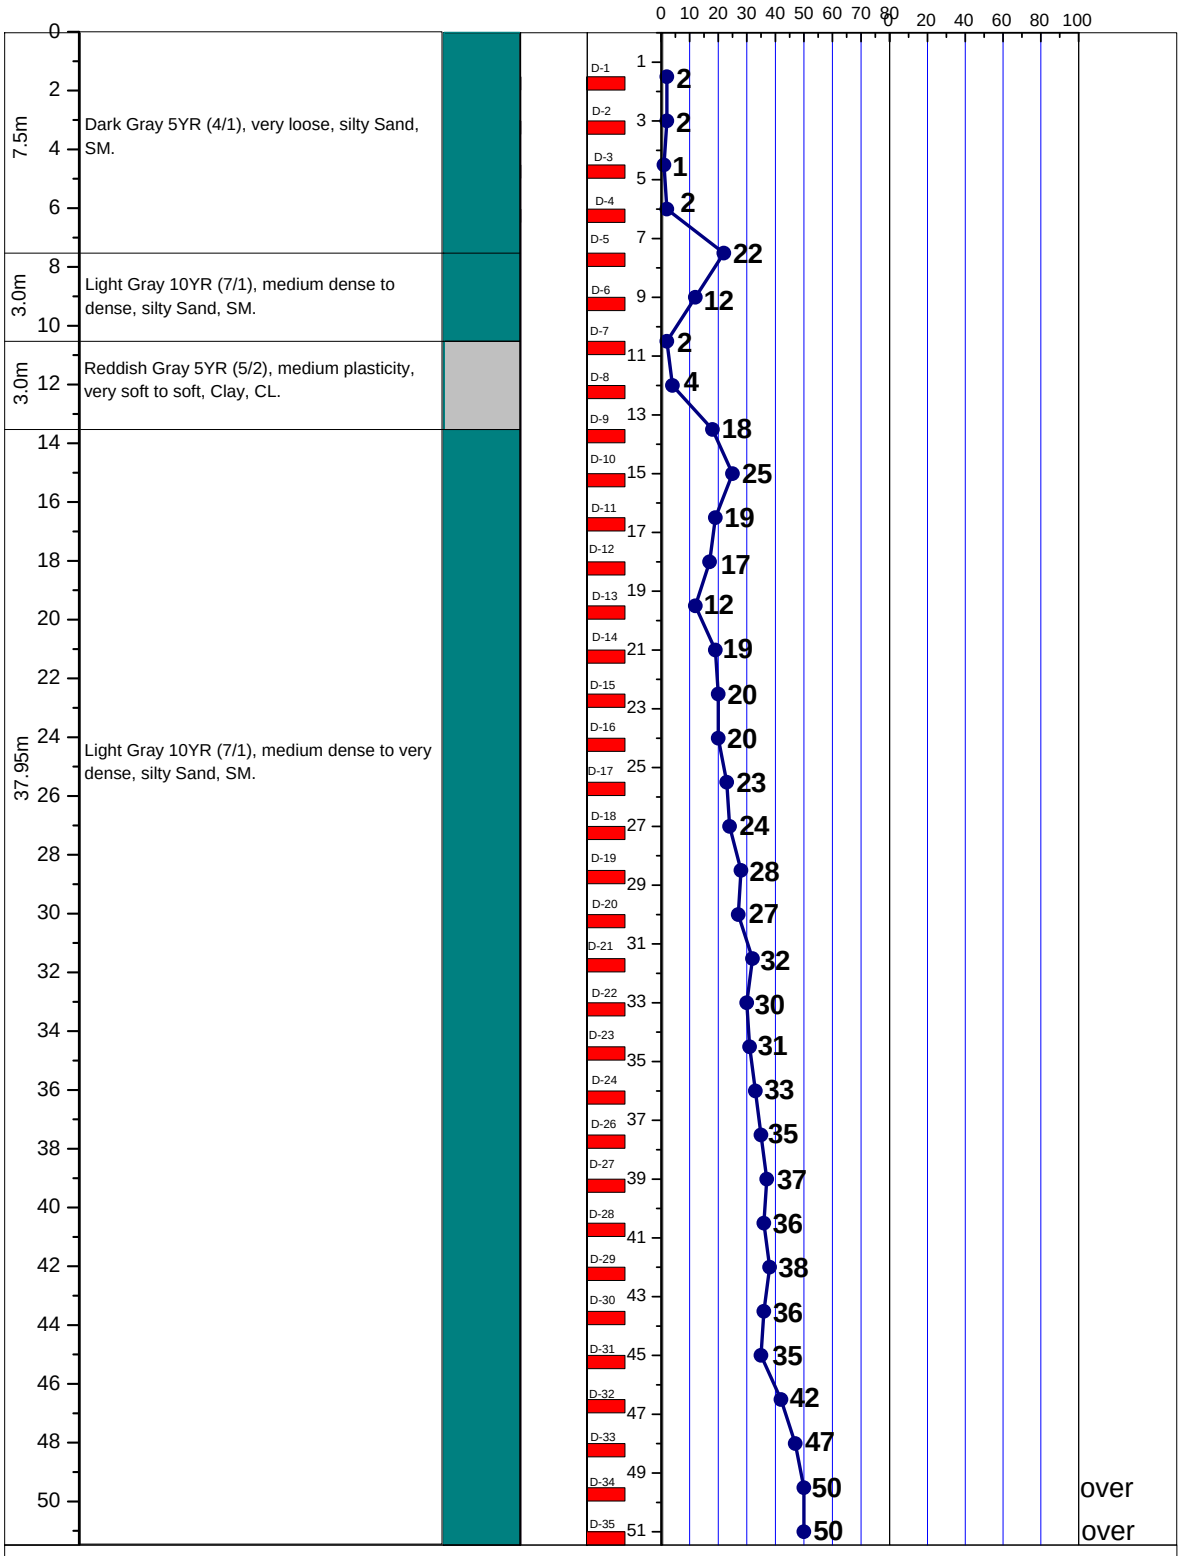


LEGEND FOR BORELOG AND GRAIN SIZE DISTRIBUTION (BASED ON 'ASTM CLASSIFICATION D-2487')

PLASTIC CLAY	SILT	PEAT/HIGHLY ORGANIC SOIL	UNDISTURBED SAMPLE
MICACEOUS FINE SAND/SILT	SAND	SHALE	DISTURBED SAMPLE

N- BLOWS DELIVERED PER FOOT BY A 140 LB HAMMER FALLING 30 INCHES

MAX^{m} PENETRATION= 50 BLOWS. AFTER 50 BLOWS PENETRATION DEPTH WERE MEASURED

A2 PROSOIL	BOREHOLE NO: BH-1	
	LOCATION : Kharulia, Munsirbil, Cox's Bazar.	
PROJECT : Telecommunication Tower.	DEPTH OF BORING : 51.0m	R. L.: On Road Level.
CLIENT : Warid Telecom International Ltd.	DATE OF BORING : 10-01-2011.	G. W. T : 1.83m below from E.G.L.

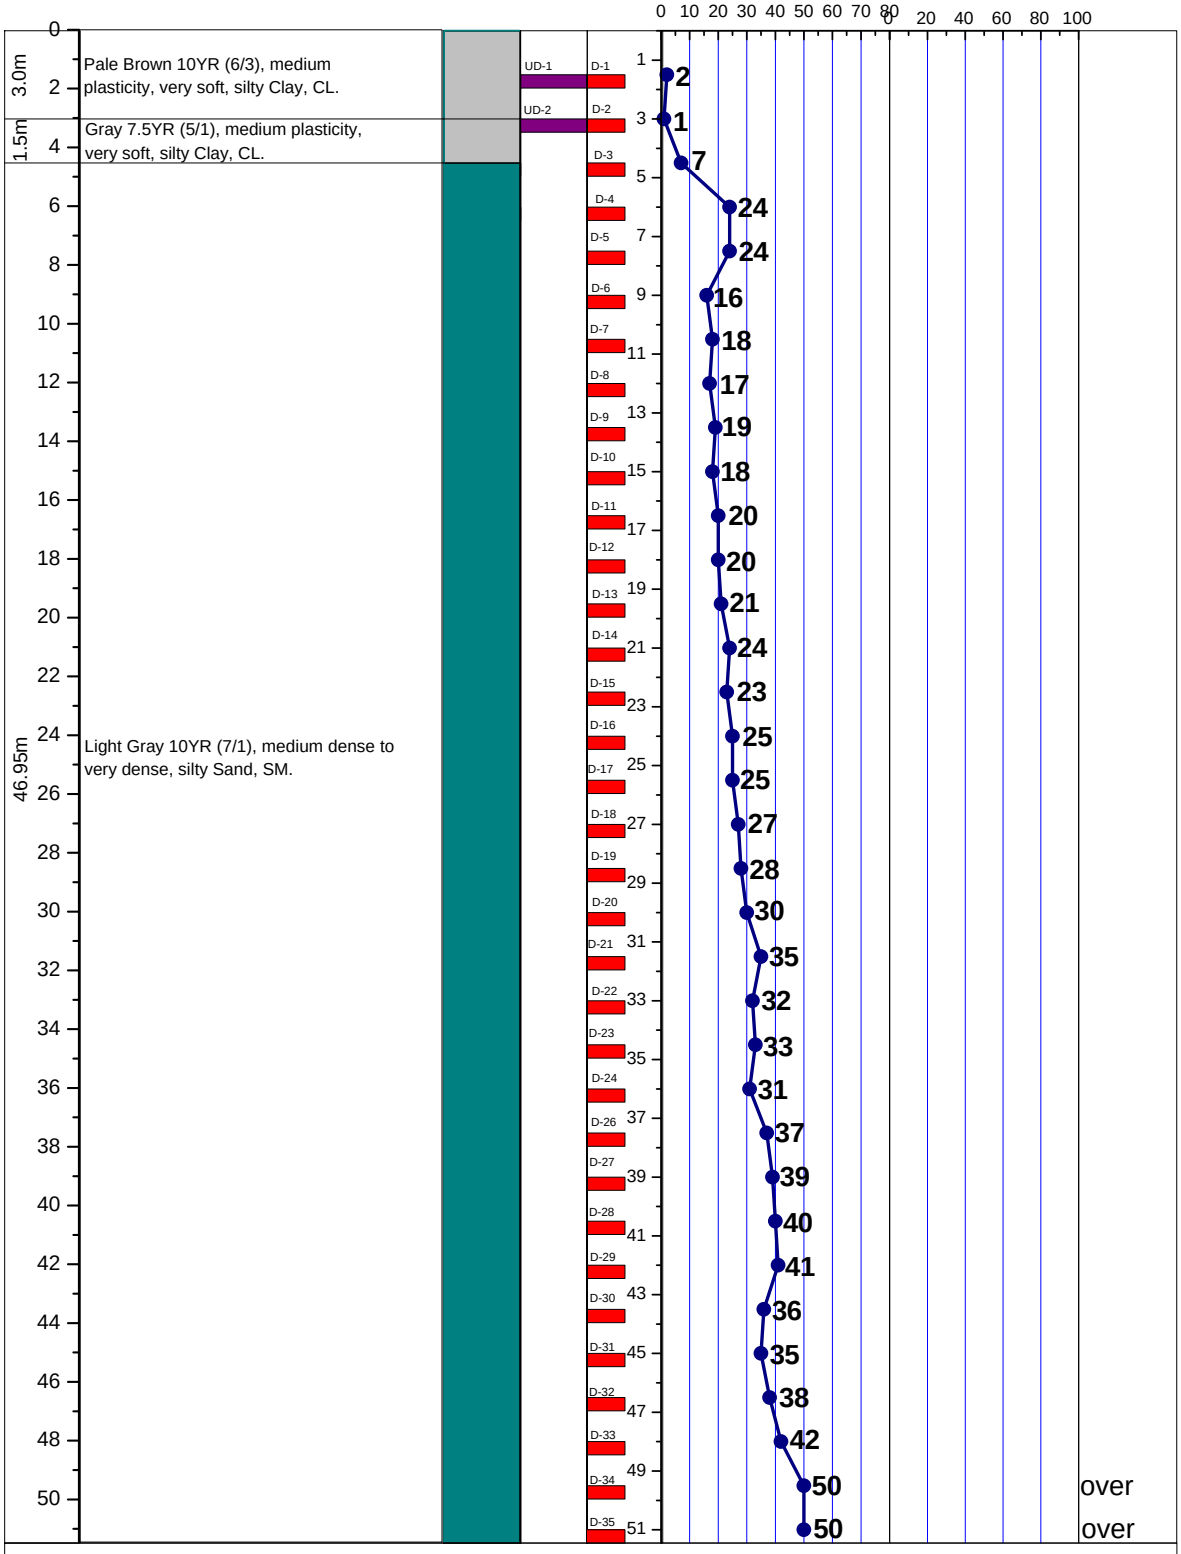


LEGEND FOR BORELOG AND GRAIN SIZE DISTRIBUTION (BASED ON 'ASTM CLASSIFICATION D-2487')

PLASTIC CLAY	SILT	PEAT/HIGHLY ORGANIC SOIL	UNDISTURBED SAMPLE
MICACEOUS FINE SAND/SILT	SAND	SHALE	DISTURBED SAMPLE

N- BLOWS DELIVERED PER FOOT BY A 140 LB HAMMER FALLING 30 INCHES

MAX^{m} PENETRATION= 50 BLOWS. AFTER 50 BLOWS PENETRATION DEPTH WERE MEASURED

A2	PROSOIL	BOREHOLE NO: BH-1	
		LOCATION : South Nidaniya, Inani, Ukhia, Cox's Bazar.	
PROJECT : Telecommunication Tower.		DEPTH OF BORING : 51.0m	R. L.: On Road Level.
CLIENT : Warid Telecom International Ltd.		DATE OF BORING : 04-06-2011.	G. W. T : 0.31m below from E.G.L.

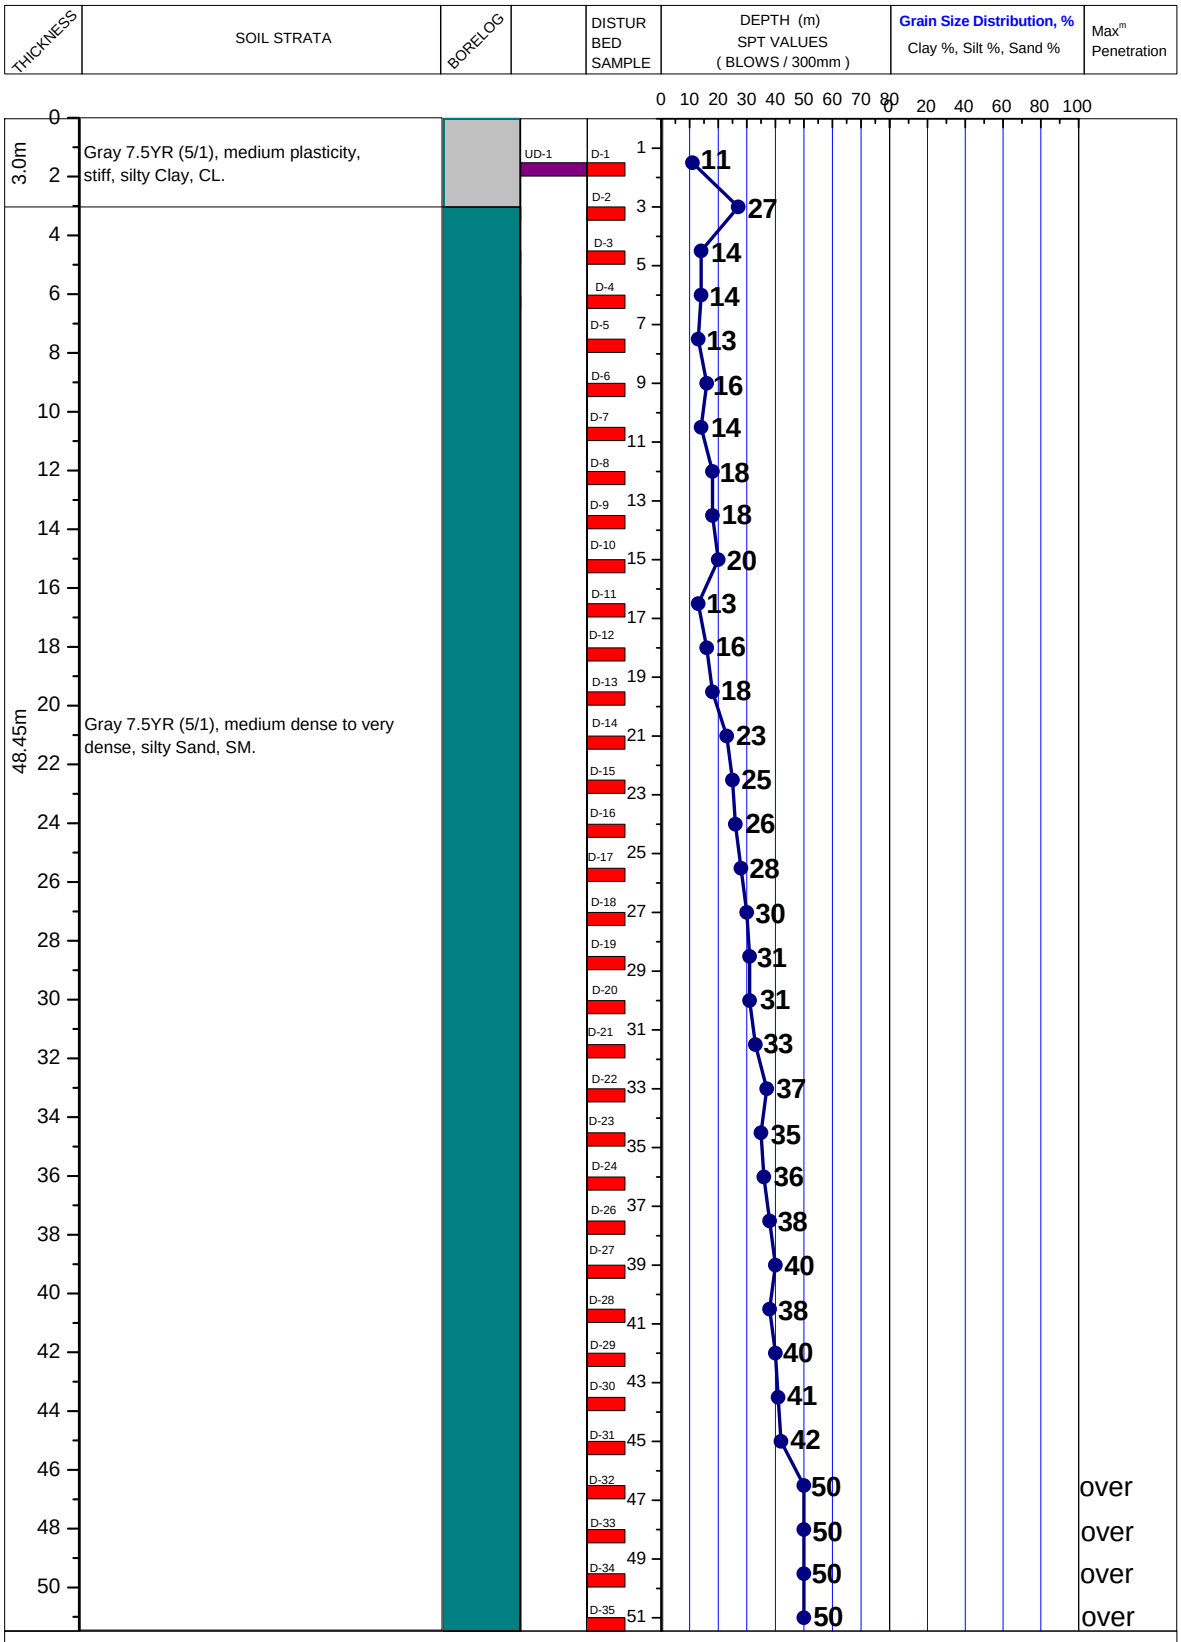


LEGEND FOR BORELOG AND GRAIN SIZE DISTRIBUTION (BASED ON 'ASTM CLASSIFICATION D-2487')

PLASTIC CLAY	SILT	PEAT/HIGHLY ORGANIC SOIL	UNDISTURBED SAMPLE
MICACEOUS FINE SAND/SILT	SAND	SHALE	DISTURBED SAMPLE

N- BLOWS DELIVERED PER FOOT BY A 140 LB HAMMER FALLING 30 INCHES

MAX^{m} PENETRATION= 50 BLOWS. AFTER 50 BLOWS PENETRATION DEPTH WERE MEASURED

A2	PROSOIL	BOREHOLE NO: BH-1	
		LOCATION : Nalbanai, Morcha, Ukhia, Cox's Bazar.	
PROJECT : Telecommunication Tower.		DEPTH OF BORING : 51.0m	R. L.: 0.61m below from Road Level.
CLIENT : Warid Telecom International Ltd.		DATE OF BORING : 01-06-2011.	G. W. T : On E.G.L.

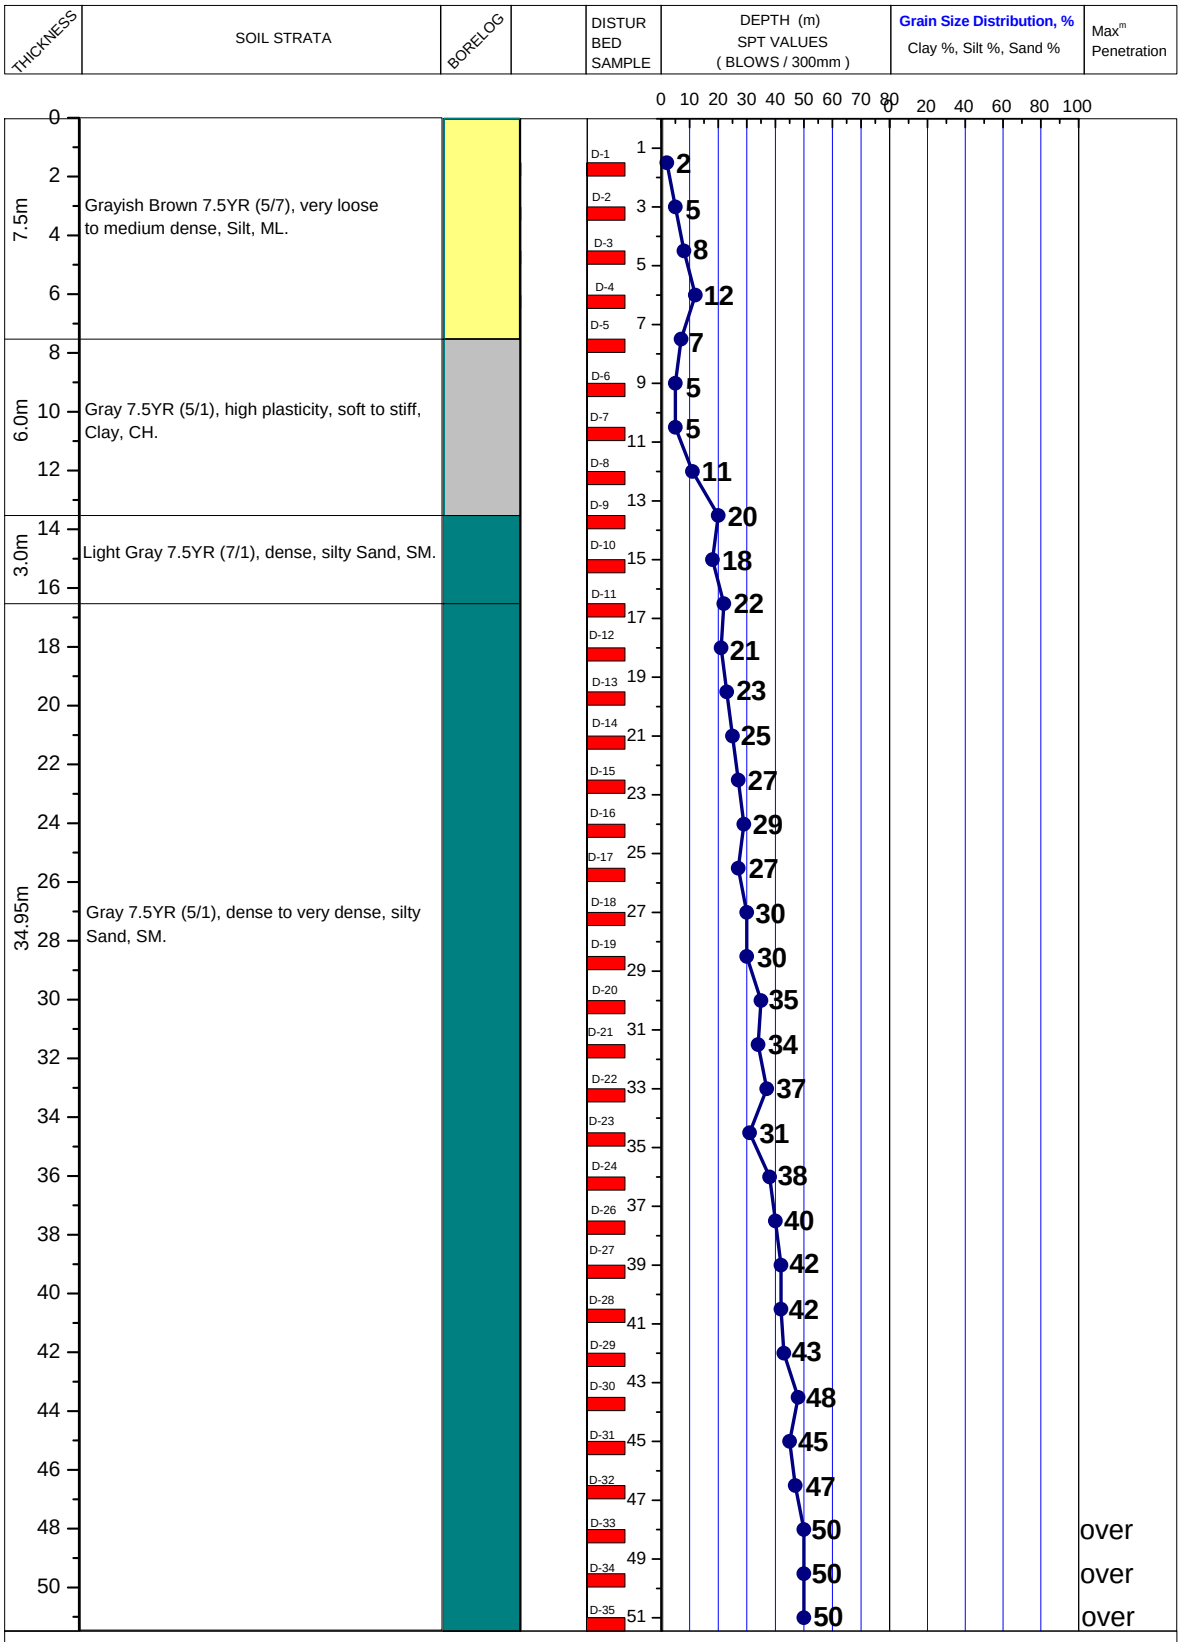


LEGEND FOR BORELOG AND GRAIN SIZE DISTRIBUTION (BASED ON 'ASTM CLASSIFICATION D-2487')

PLASTIC CLAY	SILT	PEAT/HIGHLY ORGANIC SOIL	UNDISTURBED SAMPLE
MICACEOUS FINE SAND/SILT	SAND	SHALE	DISTURBED SAMPLE

N- BLOWS DELIVERED PER FOOT BY A 140 LB HAMMER FALLING 30 INCHES

MAX^{m} PENETRATION= 50 BLOWS. AFTER 50 BLOWS PENETRATION DEPTH WERE MEASURED

A2	PROSOIL	BOREHOLE NO: BH-1	
		LOCATION : East KawarKhup, Ramu, Cox's Bazar.	
PROJECT : Telecommunication Tower.		DEPTH OF BORING : 51.0m	R. L.: 1.22m below from Road Level.
CLIENT : Warid Telecom International Ltd.		DATE OF BORING : 06-05-2011.	G. W. T : 2.13m below from E.G.L.

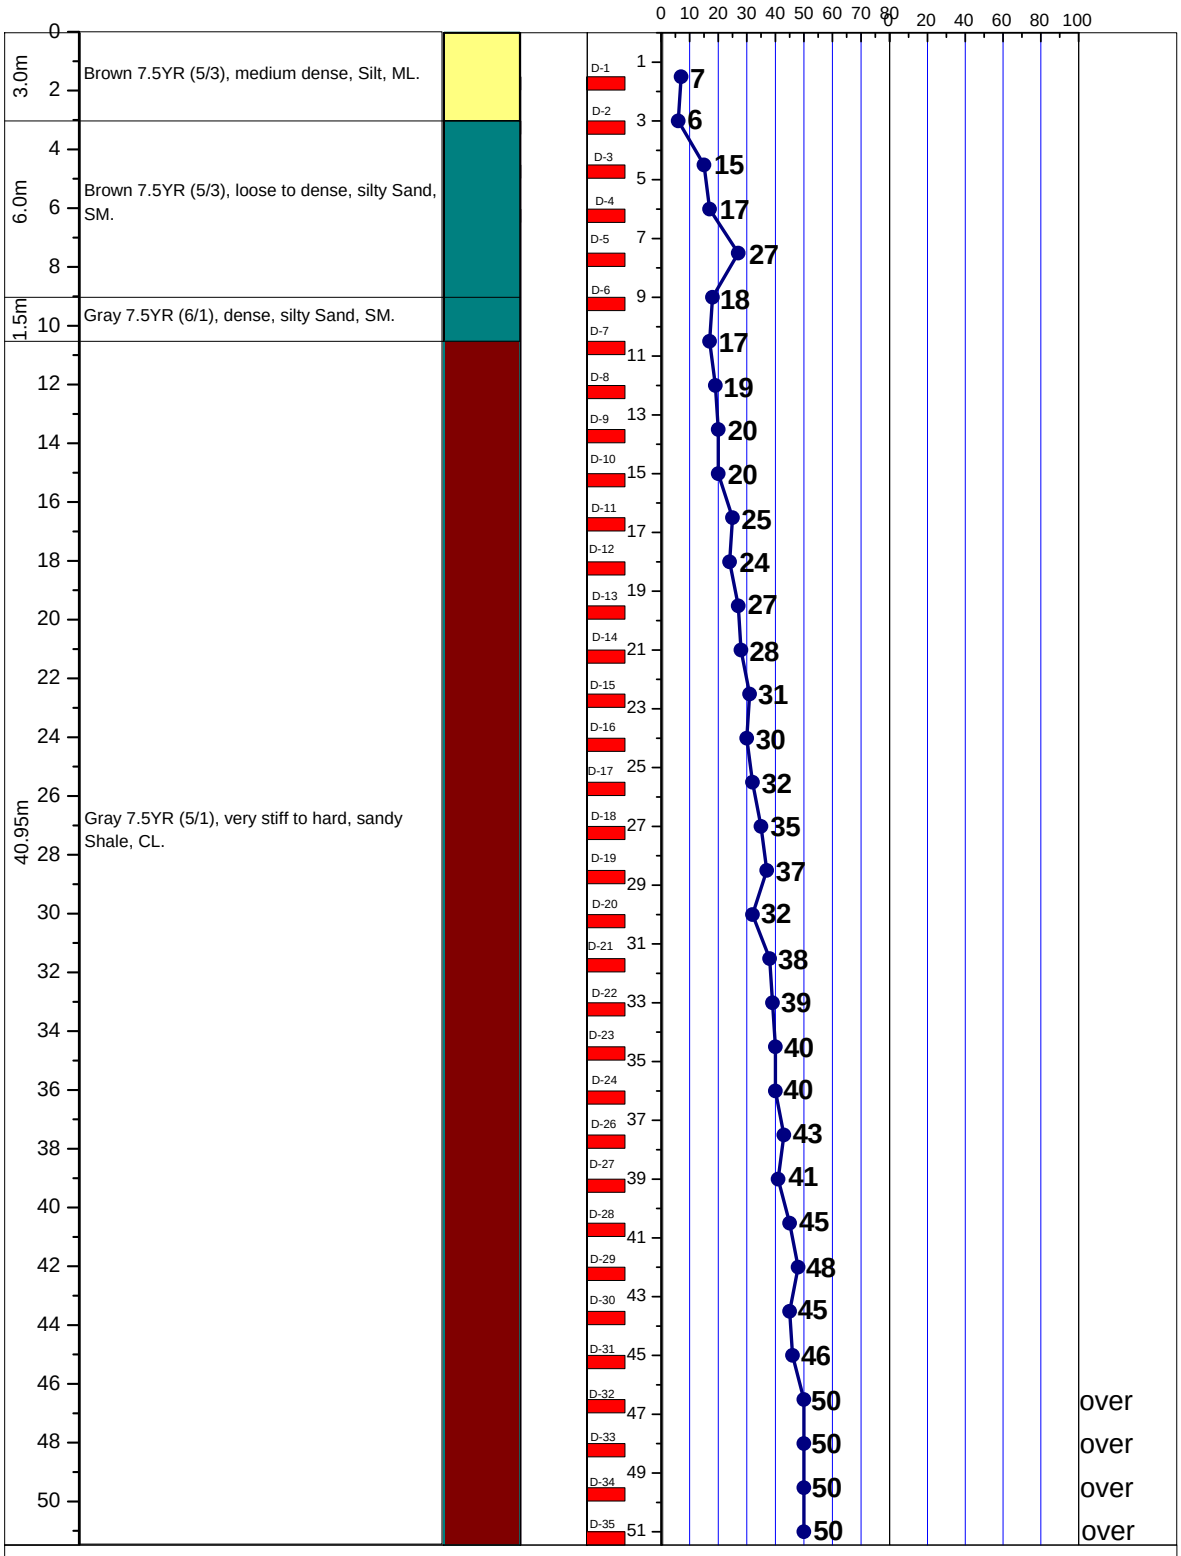

LEGEND FOR BORELOG AND GRAIN SIZE DISTRIBUTION (BASED ON 'ASTM CLASSIFICATION D-2487')

PLASTIC CLAY	SILT	PEAT/HIGHLY ORGANIC SOIL	UNDISTURBED SAMPLE
MICACEOUS FINE SAND/SILT	SAND	SHALE	DISTURBED SAMPLE

N- BLOWS DELIVERED PER FOOT BY A 140 LB HAMMER FALLING 30 INCHES

MAX^{m} PENETRATION= 50 BLOWS. AFTER 50 BLOWS PENETRATION DEPTH WERE MEASURED