A2	PROSOIL	BOREHOLE NO: BH-1	
		LOCATION : Bogachari Purbo Para, Nanyarchar Road, Nanyarchar, Rangamati.	
PROJECT : Telecommunication Tower.		DEPTH OF BORING : 10.95m	R. L.: 6.10m above from Road Level.
CLIENT : BANGLADESH TELEGRAPH & TELEPHONE BOARD.		DATE OF BORING: 27-11-2011.	G. W. T : Too low to measure.

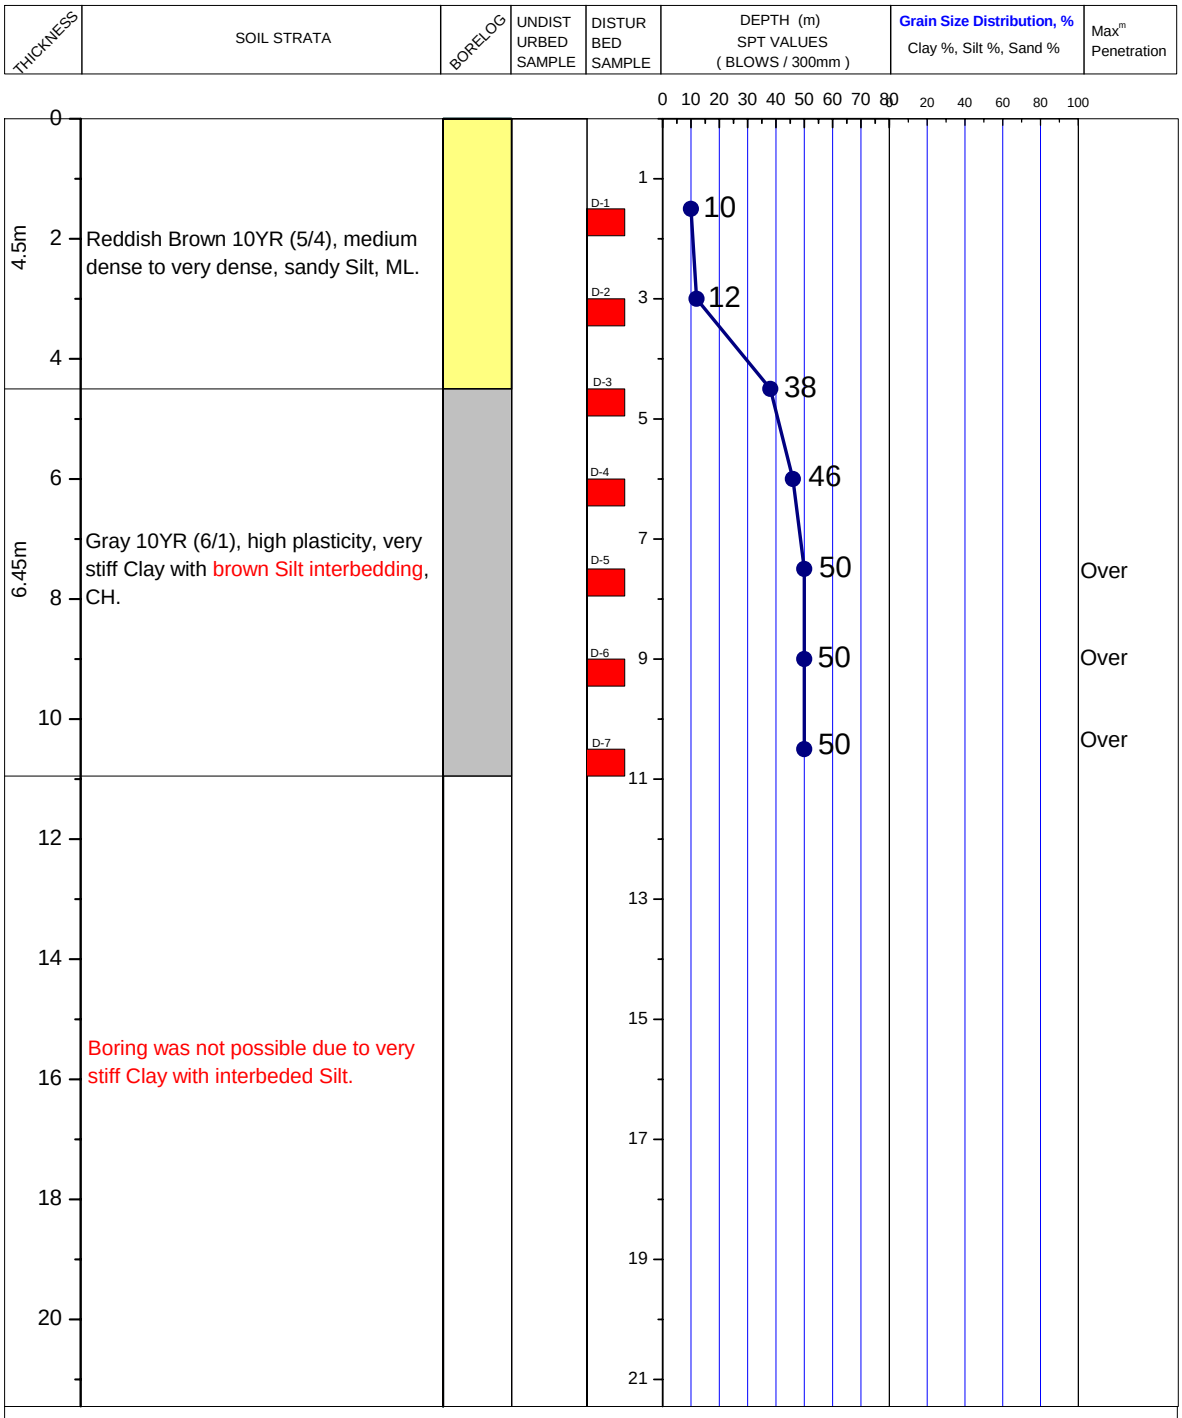

LEGEND FOR BORELOG AND GRAIN SIZE DISTRIBUTION (BASED ON 'ASTM CLASSIFICATION D-2487')

PLASTIC CLAY	SAND	SHALE	UNDISTURBED SAMPLE
MICACEOUS FINE SAND/SILT	SILT	PEAT/HIGHLY ORGANIC SOIL	DISTURBED SAMPLE

N- BLOWS DELIVERED PER FOOT BY A 140 LB HAMMER FALLING 30 INCHES

MAX^{m} PENETRATION= 50 BLOWS

AFTER 50 BLOWS PENETRATION DEPTH WERE MEASURED