| A2 | PROSOIL | BOREHOLE NO: BH-1 | |
|---|---|---|---|
| | | LOCATION: Vill: Belgharia, P. O: Muroil, P. S: Kahaloo, Dist: Bogra. | |
| PROJECT : Telecommunication Tower. | | DEPTH OF BORING: 13.5m | R. L.: 1.37m below from Road Level. |
| CLIENT : Grameenphone Ltd. | | DATE OF BORING: 01-03-2015. | B. W. T : 3.04m below from E. G. L. |

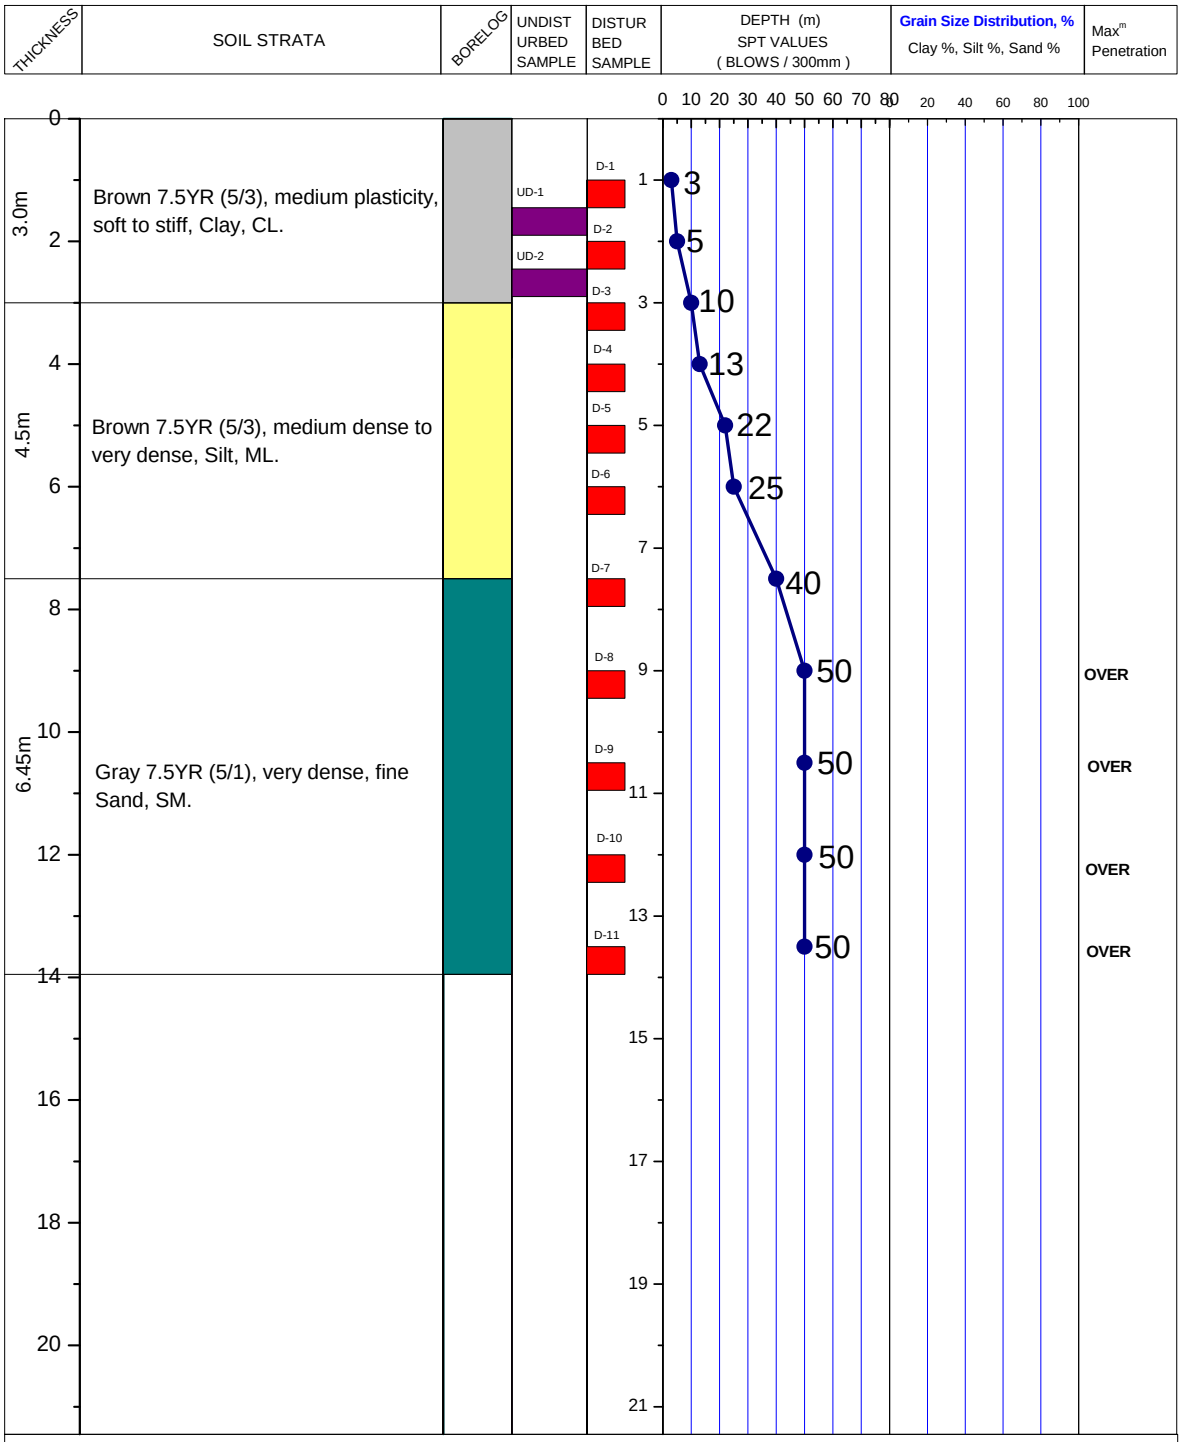


LEGEND FOR BORELOG AND GRAIN SIZE DISTRIBUTION (BASED ON 'ASTM CLASSIFICATION D-2487')

PLASTIC CLAY | SHALE | SILT | SAND

PEAT/HIGHLY ORGANIC SOIL | MICACEOUS FINE SAND/SILT | UNDISTURBED SAMPLE | DISTURBED SAMPLE

N- BLOWS DELIVERED PER FOOT BY A 140 LB HAMMER FALLING 30 INCHES

MAX$^{m}$ PENETRATION= 50 BLOWS

AFTER 50 BLOWS PENETRATION DEPTH WERE MEASURED