
A2	PROSOIL	BOREHOLE NO: A1	Easting: 238048	Northing: 2606344
		LOCATION : Kunder Bazar (CH.5+512) Road (Z-8004)		CHAINAGE: 5+512 km
PROJECT : Kunder Bazar Bridge, Munshiganj.		DEPTH OF BORING : 45.0m		R. L. : 6.12m
CLIENT : ROADS & HIGHWAYS DEPARTMENT.		DATE OF BORING : 16-12-2020 to 18-12-2020		B. W. T : 2.35m below from E. G. L.

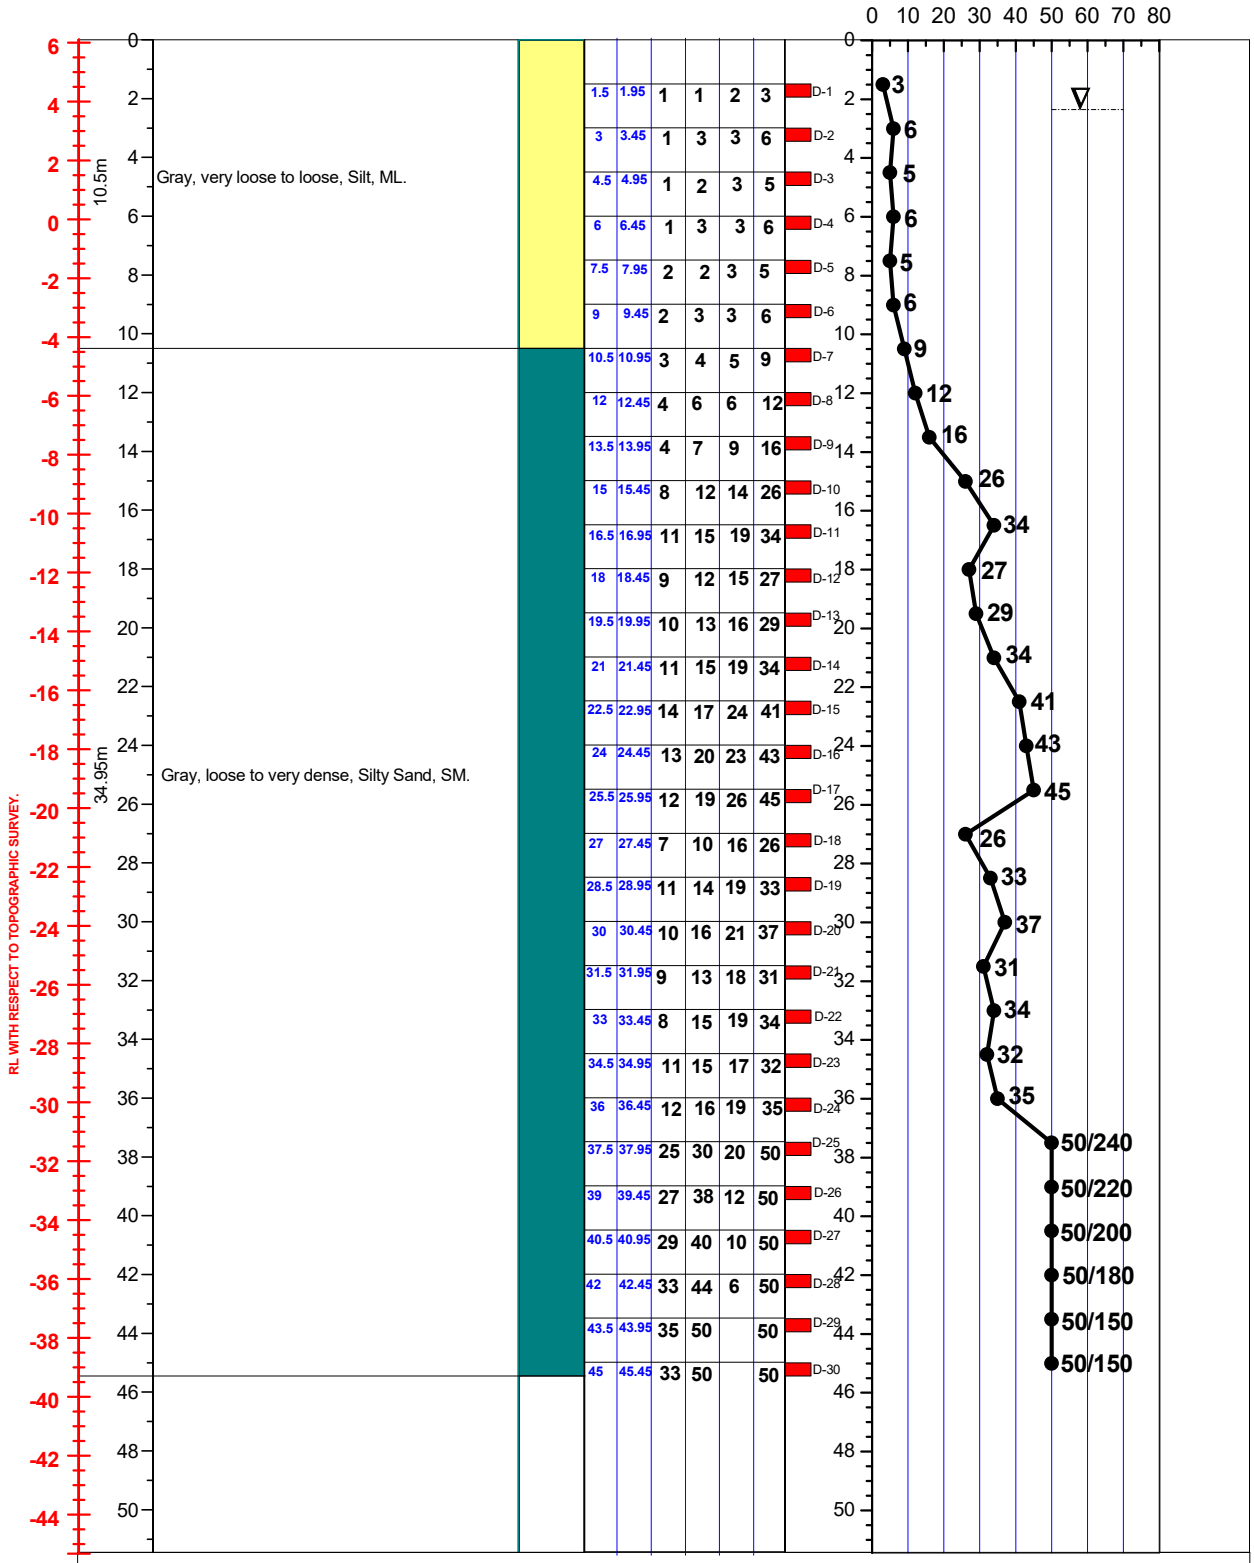


LEGEND FOR BOREHOLE AND GRAIN SIZE DISTRIBUTION (BASED ON 'ASTM CLASSIFICATION D-2487')

PLASTIC CLAY	SILT	PEAT/HIGHLY ORGANIC SOIL	UNDISTURBED SAMPLE
MICACEOUS FINE SAND/SILT	SAND	SHALE	DISTURBED SAMPLE

N- BLOWS DELIVERED PER FOOT BY A 140 LB HAMMER FALLING 30 INCHES

MAX^m PENETRATION= 50 BLOWS. AFTER 50 BLOWS PENETRATION DEPTH WERE MEASURED

A2	PROSOIL	BOREHOLE NO: P1	Easting: 237992	Northing: 2606370
		LOCATION : Kunder Bazar (CH.5+512) Road (Z-8004)		CHAINAGE: 5+572 km
PROJECT : Kunder Bazar Bridge, Munshiganj.		DEPTH OF BORING : 45.0m		R. L. : 2.10m
CLIENT : ROADS & HIGHWAYS DEPARTMENT.		DATE OF BORING : 23-12-2020 to 26-12-2020		B. W. T : 5.02m above from E. G. L.

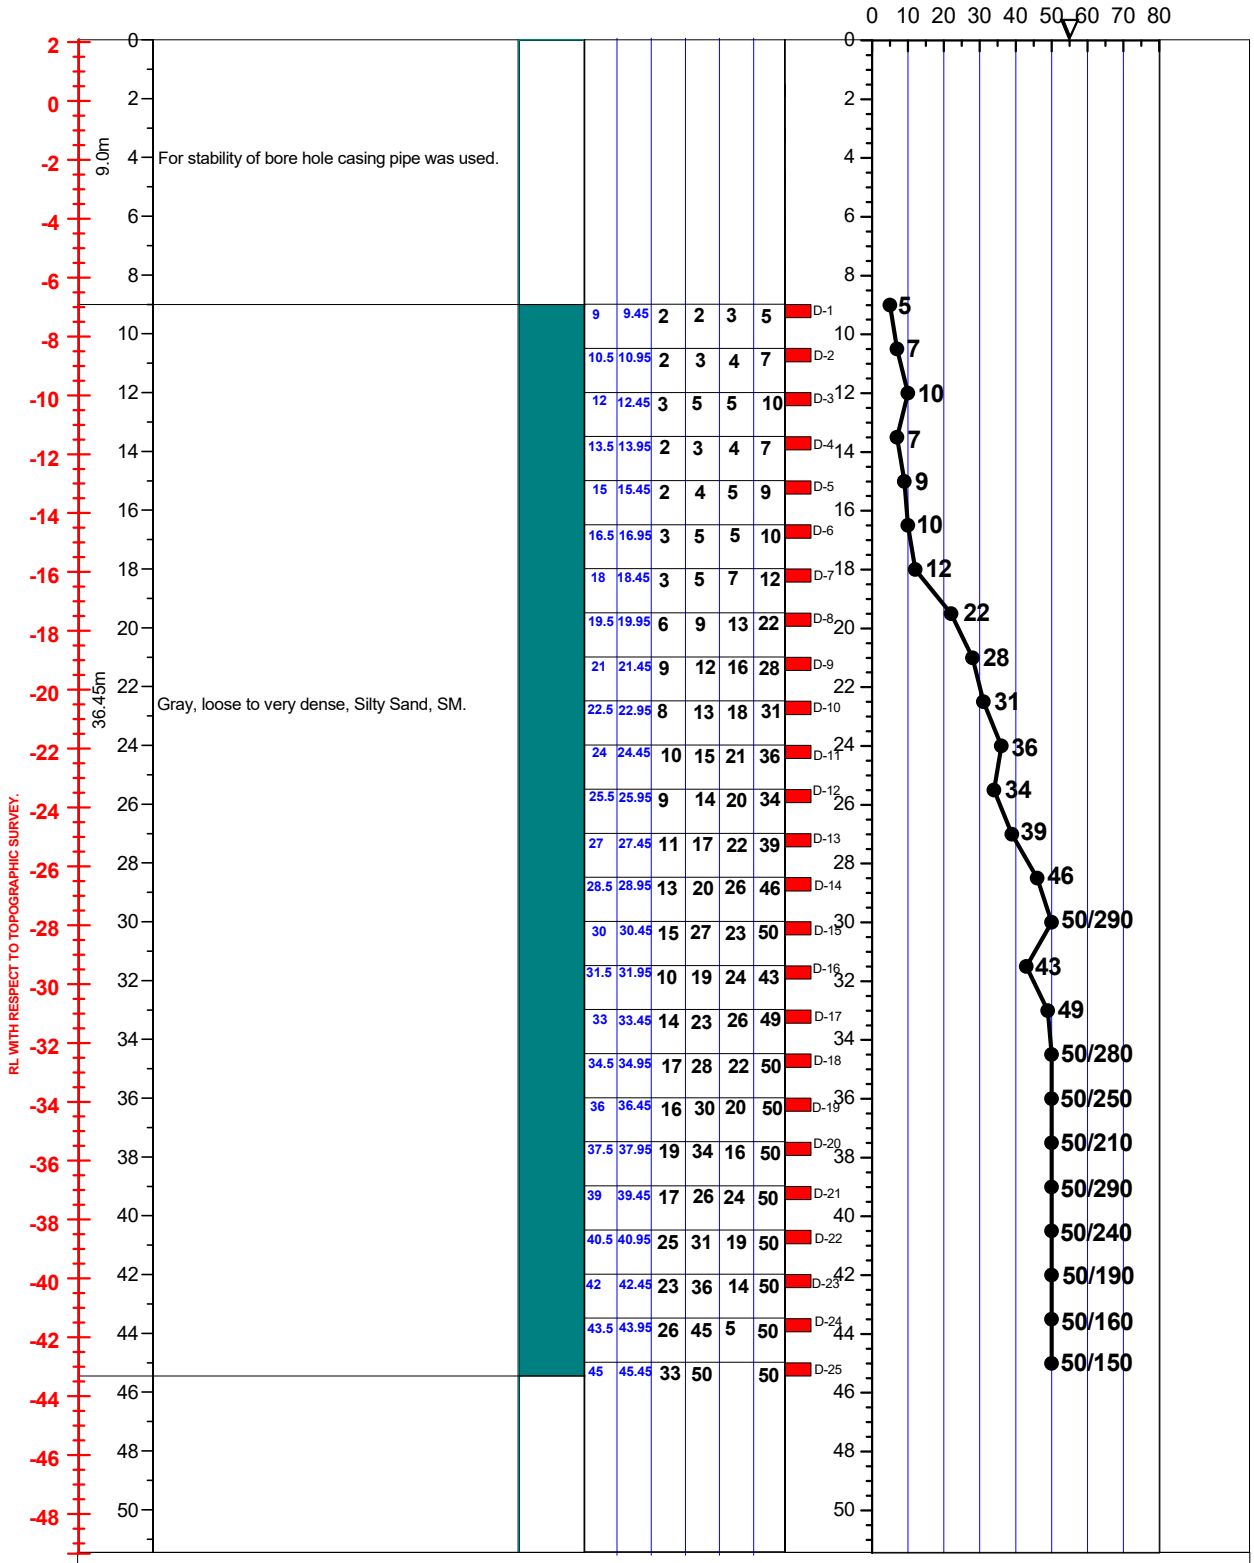


LEGEND FOR BORELOG AND GRAIN SIZE DISTRIBUTION (BASED ON 'ASTM CLASSIFICATION D-2487')

PLASTIC CLAY	SILT	PEAT/HIGHLY ORGANIC SOIL	UNDISTURBED SAMPLE
MICACEOUS FINE SAND/SILT	SAND	SHALE	DISTURBED SAMPLE

N- BLOWS DELIVERED PER FOOT BY A 140 LB HAMMER FALLING 30 INCHES

MAX^m PENETRATION= 50 BLOWS. AFTER 50 BLOWS PENETRATION DEPTH WERE MEASURED

A2	PROSOIL	BOREHOLE NO: P2	Easting: 238037	Northing: 2606353
		LOCATION : Kunder Bazar (CH.5+512) Road (Z-8004)		CHAINAGE: 5+542 km
PROJECT : Kunder Bazar Bridge, Munshiganj.		DEPTH OF BORING : 46.5m		R. L. : 1.10m
CLIENT : ROADS & HIGHWAYS DEPARTMENT.		DATE OF BORING : 26-12-2020 to 29-12-2020		B. W. T : 2.59m above from E. G. L.

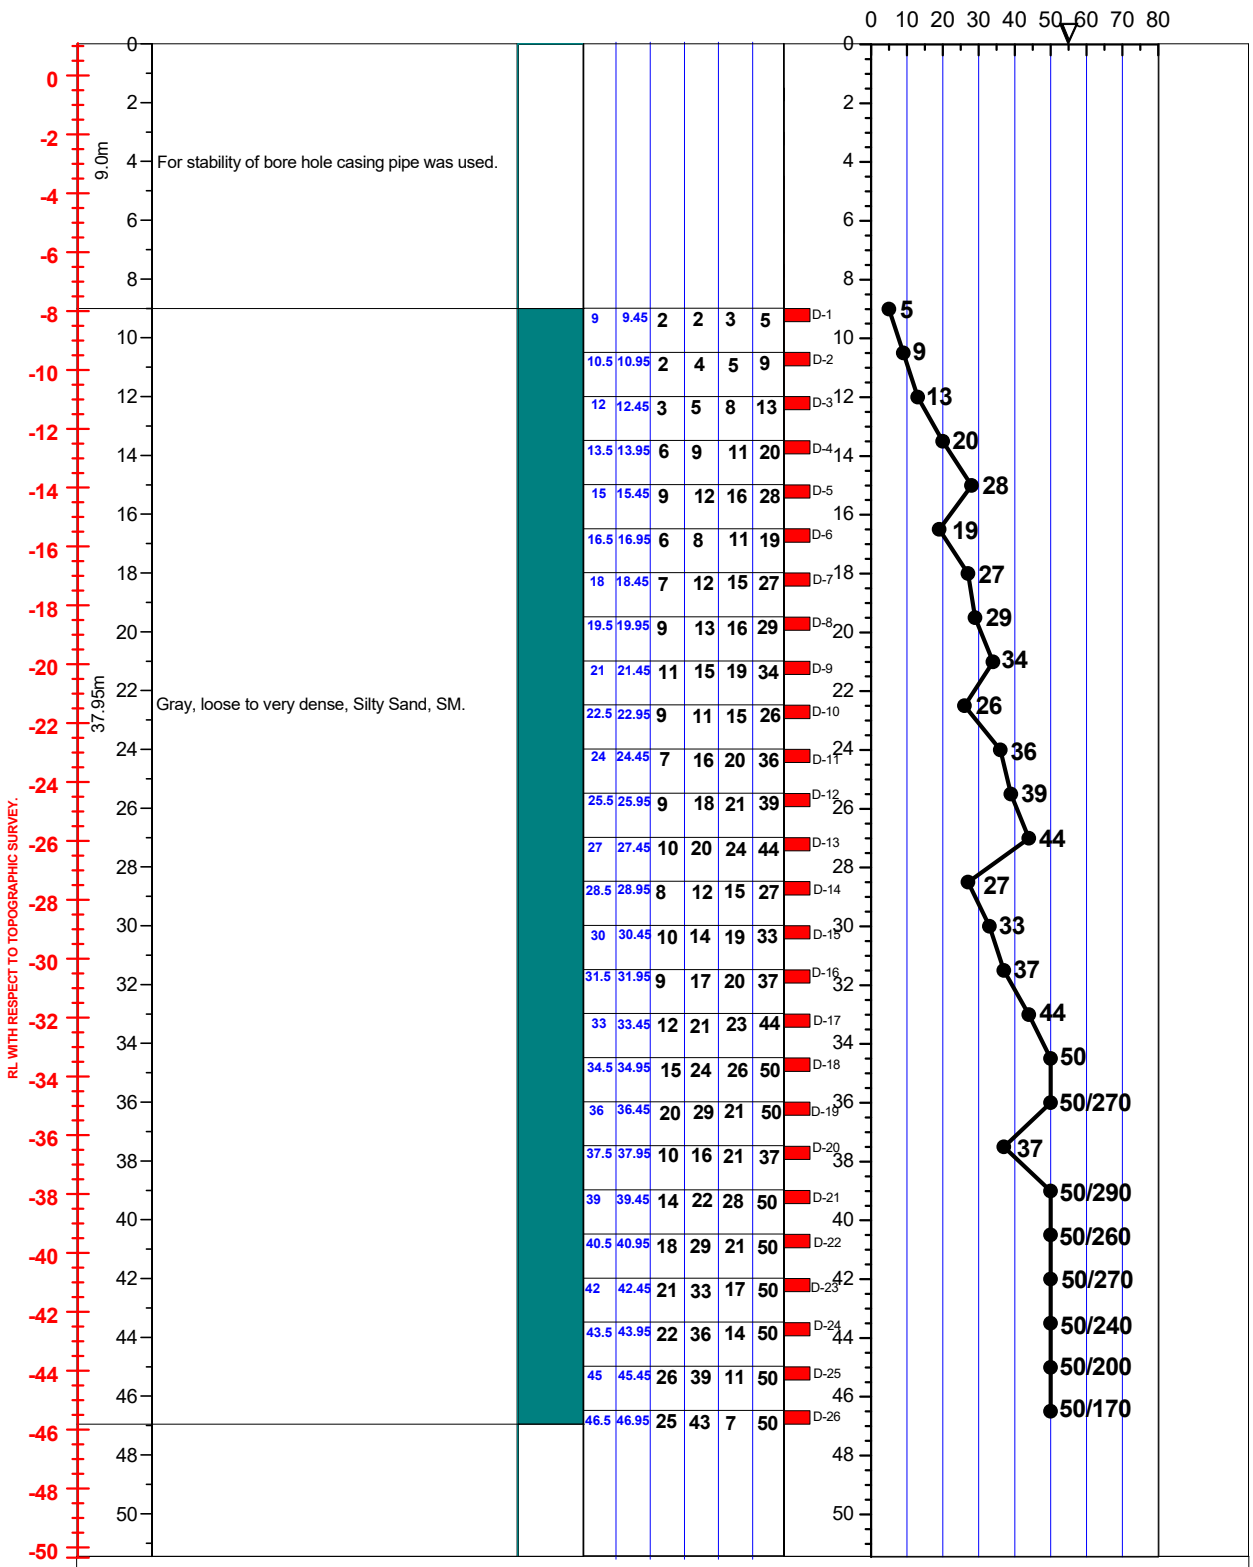


LEGEND FOR BOREHOLE AND GRAIN SIZE DISTRIBUTION (BASED ON 'ASTM CLASSIFICATION D-2487')

PLASTIC CLAY	SILT	PEAT/HIGHLY ORGANIC SOIL	UNDISTURBED SAMPLE
MICACEOUS FINE SAND/SILT	SAND	SHALE	DISTURBED SAMPLE

N- BLOWS DELIVERED PER FOOT BY A 140 LB HAMMER FALLING 30 INCHES

MAX^m PENETRATION= 50 BLOWS. AFTER 50 BLOWS PENETRATION DEPTH WERE MEASURED

A2	PROSOIL	BOREHOLE NO: A2	Easting: 237970	Northing: 2606377
		LOCATION : Kunder Bazar (CH.5+512) Road (Z-8004)		CHAINAGE: 5+604 km
PROJECT : Kunder Bazar Bridge, Munshiganj.		DEPTH OF BORING : 45.0m		R. L. : 8.84m
CLIENT : ROADS & HIGHWAYS DEPARTMENT.		DATE OF BORING : 19-12-2020 to 21-12-2020		B. W. T : 2.39m below from E. G. L.

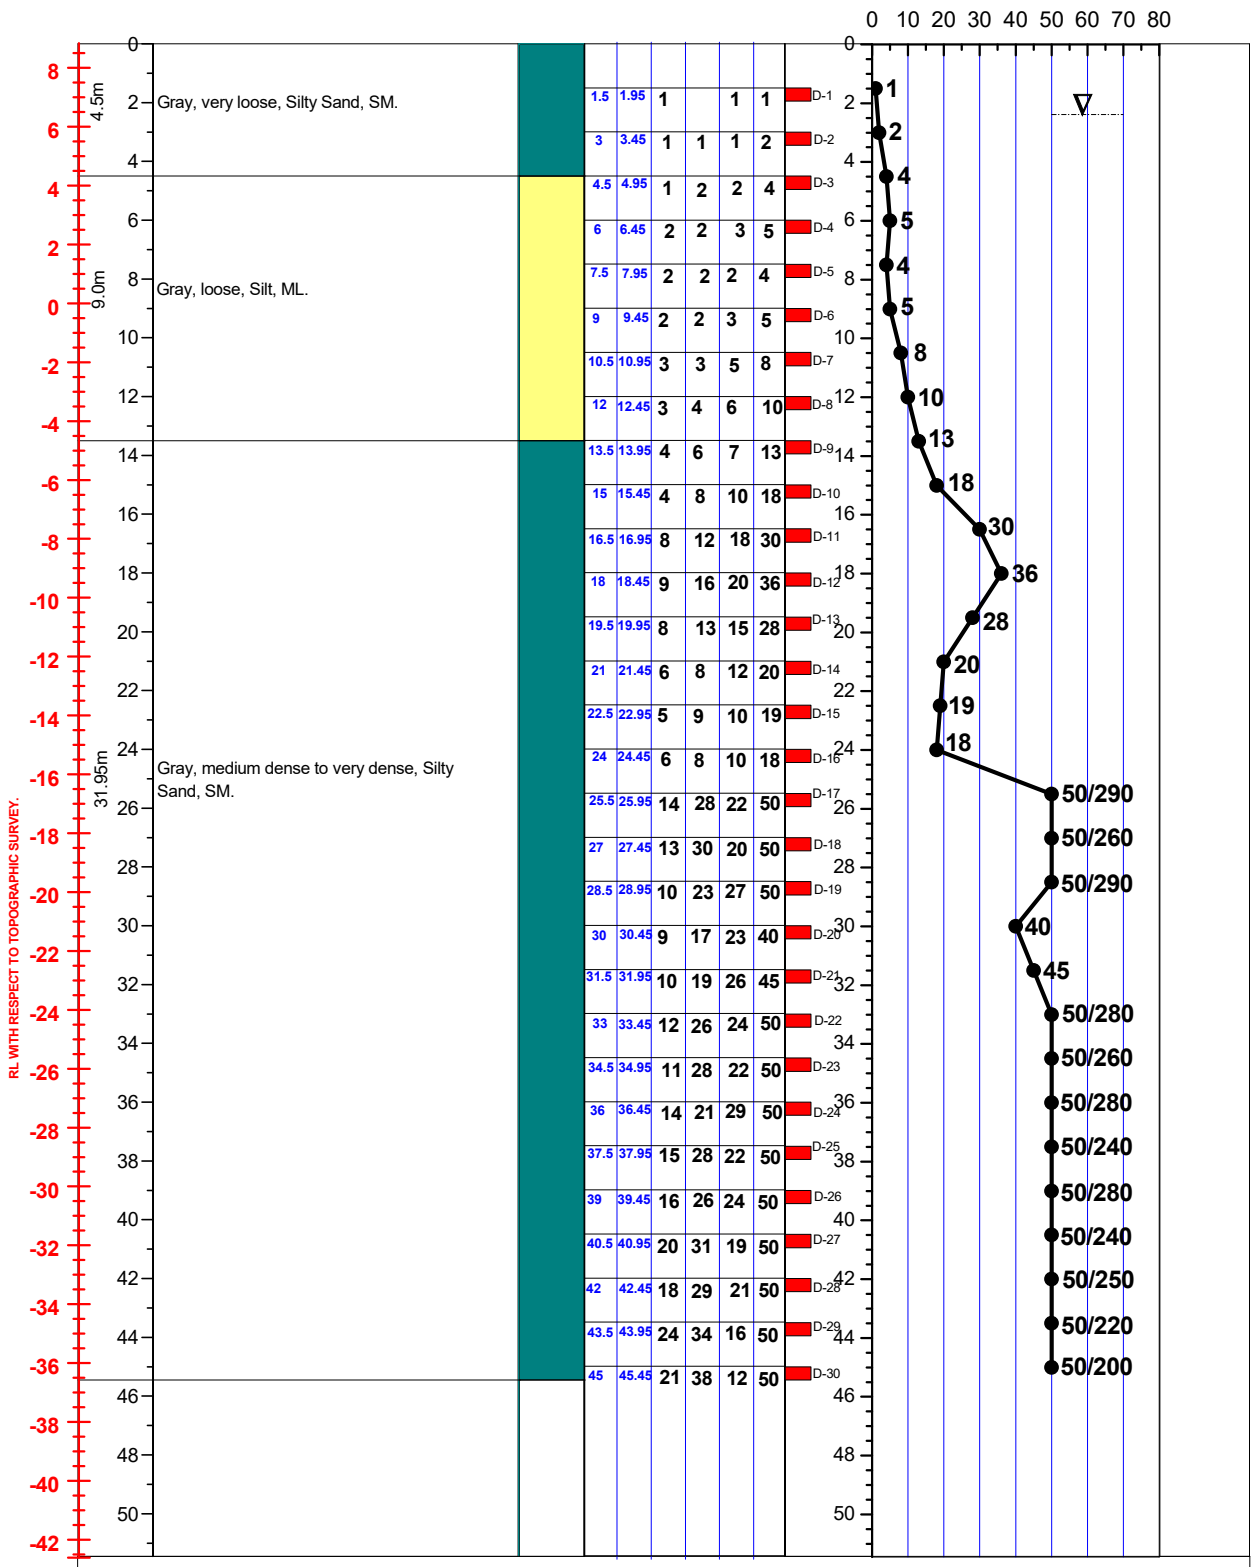

LEGEND FOR BOREHOLE AND GRAIN SIZE DISTRIBUTION (BASED ON 'ASTM CLASSIFICATION D-2487')

PLASTIC CLAY	SILT	PEAT/HIGHLY ORGANIC SOIL	UNDISTURBED SAMPLE
MICACEOUS FINE SAND/SILT	SAND	SHALE	DISTURBED SAMPLE

N- BLOWS DELIVERED PER FOOT BY A 140 LB HAMMER FALLING 30 INCHES

MAX^m PENETRATION= 50 BLOWS. AFTER 50 BLOWS PENETRATION DEPTH WERE MEASURED