| A2 | PROSOIL | BOREHOLE NO: BH-1 | |
|---|---|---|---|
| | | LOCATION : Chainage 1+252 of Karidandi-Bancharampur-Jibongonj Bazar Road, B.Baria. | |
| PROJECT : Proposed 55.0m PC Girder Bridge. | | DEPTH OF BORING : 42.0m | Chainage: 1+267.6<br>R. L. : 0.39 |
| CLIENT : Road Division, B.Baria. | | DATE OF BORING : 01-02-2011. | G. W. T : 0.61m below from E.G.L. |

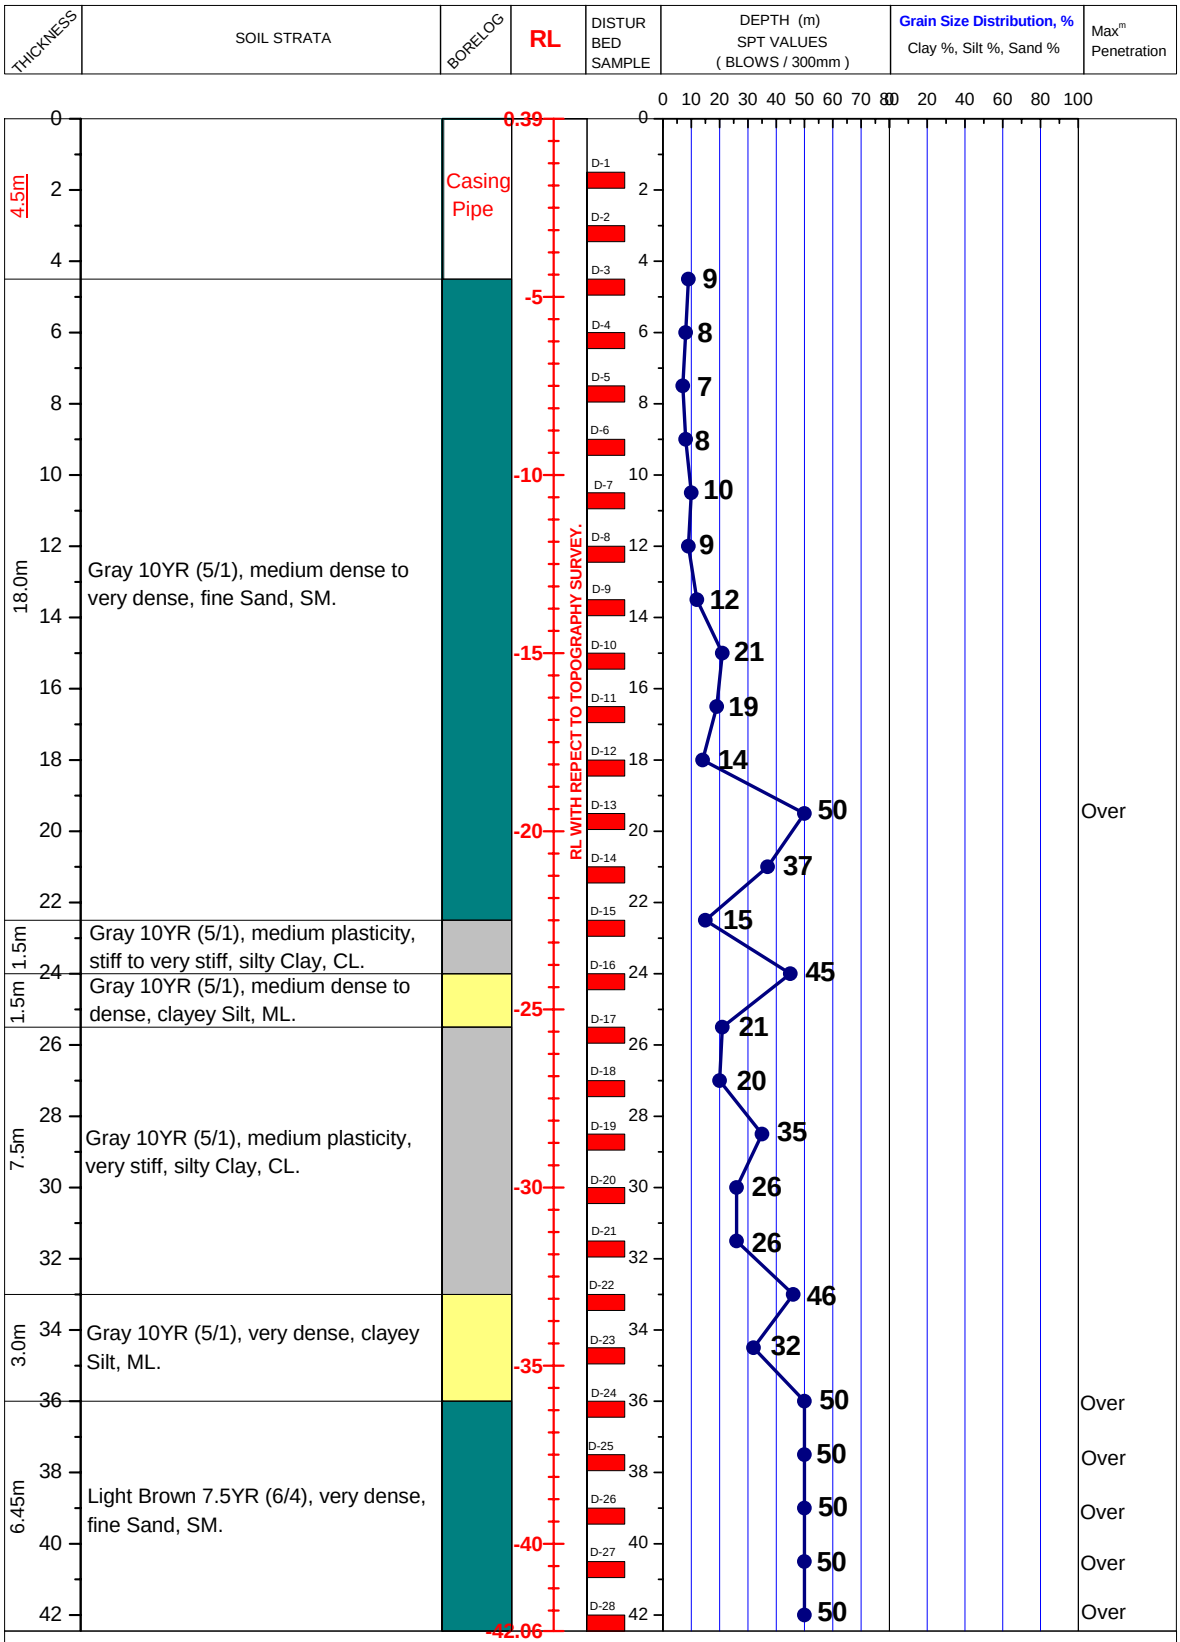


LEGEND FOR BORELOG AND GRAIN SIZE DISTRIBUTION (BASED ON 'ASTM CLASSIFICATION D-2487')

| | | | |
|---|---|---|---|
| PLASTIC CLAY | SILT | PEAT/HIGHLY ORGANIC SOIL | UNDISTURBED SAMPLE |
| MICACEOUS FINE SAND/SILT | SAND | SHALE | DISTURBED SAMPLE |

N- BLOWS DELIVERED PER FOOT BY A 140 LB HAMMER FALLING 30 INCHES

MAX$^{m}$ PENETRATION= 50 BLOWS. AFTER 50 BLOWS PENETRATION DEPTH WERE MEASURED