A2	PROSOIL	BOREHOLE NO: BH-1	
		LOCATION: Kagojpukur, Benapol, Jessore.	
PROJECT : Telecommunication Tower.		DEPTH OF BORING: 18.0m	R. L.: 0.91m below from Road Level.
CLIENT : Orascom Telecom Bangladesh Limited.		DATE OF BORING : 28-06-2010.	G. W. T : 1.83m below from E. G. L.

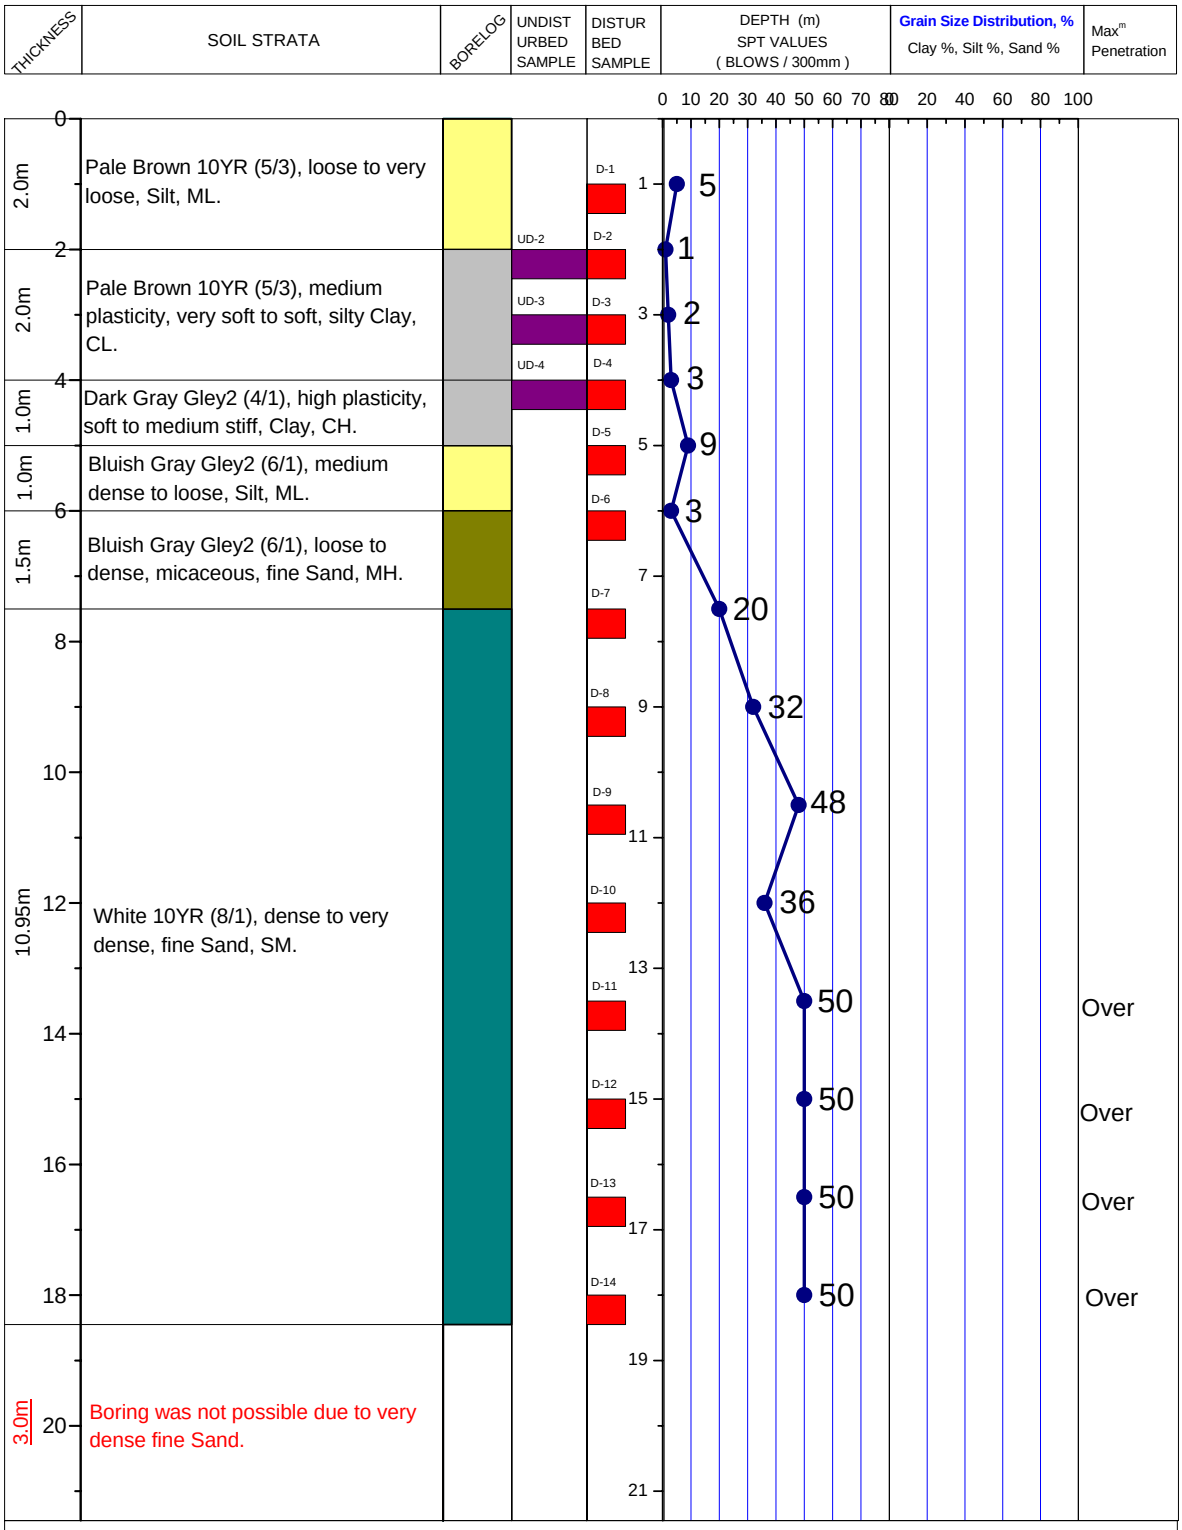

LEGEND FOR BORELOG AND GRAIN SIZE DISTRIBUTION (BASED ON 'ASTM CLASSIFICATION D-2487')

PLASTIC CLAY	SAND	SILT	SHALE
PEAT/HIGHLY ORGANIC SOIL	MICACEOUS FINE SAND/SILT	UNDISTURBED SAMPLE	DISTURBED SAMPLE

N- BLOWS DELIVERED PER FOOT BY A 140 LB HAMMER FALLING 30 INCHES

MAX^{m} PENETRATION= 50 BLOWS

AFTER 50 BLOWS PENETRATION DEPTH WERE MEASURED