| | | |
|---|---|---|
| **A2 PROSOIL** | BOREHOLE NO: BH-1 | |
| | LOCATION: Silimpur, Sakhipur, Tangail. | |
| **PROJECT : Telecommunication Tower.** | DEPTH OF BORING: 21.0m | R. L.: 0.20m below from Road Level. |
| **CLIENT : Grameenphone Ltd.** | DATE OF BORING: 14-10-2011. | G. W. T : 2.13m below from E. G. L. |

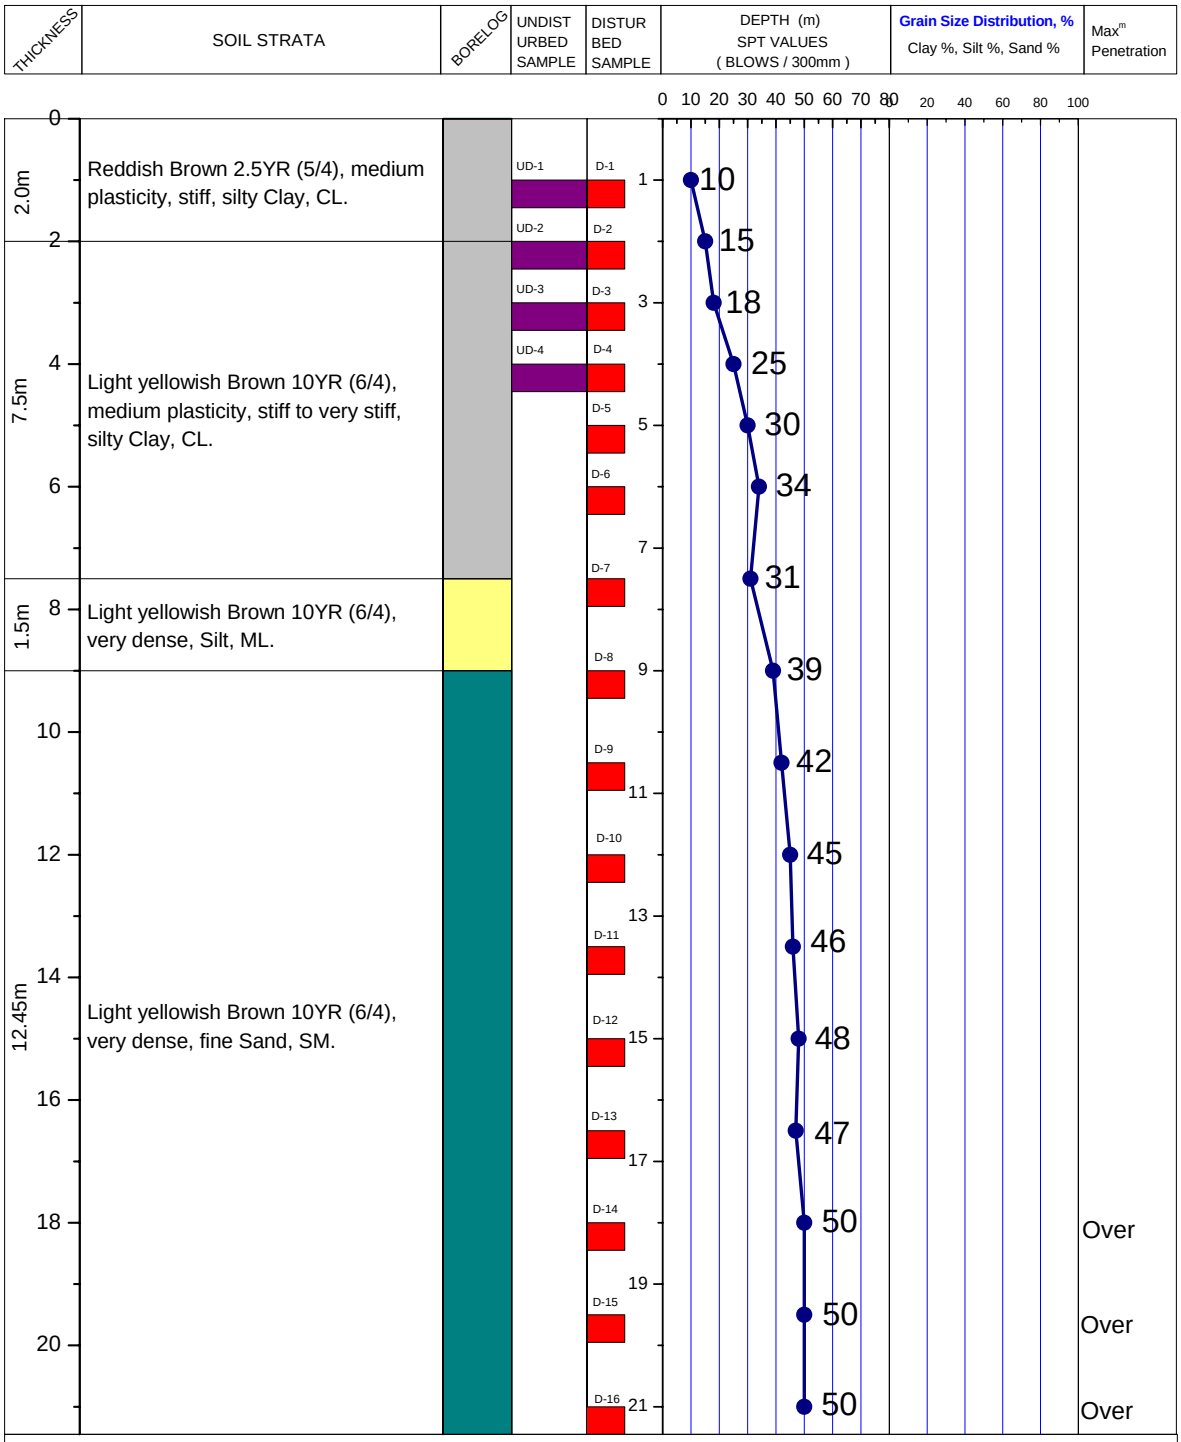


LEGEND FOR BORELOG AND GRAIN SIZE DISTRIBUTION (BASED ON 'ASTM CLASSIFICATION D-2487')

PLASTIC CLAY | SHALE | SILT | SAND

PEAT/HIGHLY ORGANIC SOIL | MICACEOUS FINE SAND/SILT | UNDISTURBED SAMPLE | DISTURBED SAMPLE

N- BLOWS DELIVERED PER FOOT BY A 140 LB HAMMER FALLING 30 INCHES

MAX$^{m}$ PENETRATION= 50 BLOWS

AFTER 50 BLOWS PENETRATION DEPTH WERE MEASURED