A2	PROSOIL	BOREHOLE NO: BH-1	
		LOCATION : Plot #04, Road #05, Block #K, Baridhara, Dhaka.	
PROJECT : Proposed (Nine Storied+1B) Building.		DEPTH OF BORING : 18.0m	R. L.: 0.15m below from Road Level.
CLIENT : Concord Real Estate & Development Ltd.		DATE OF BORING : 23-02-2010.	G. W. T : 1.52m below from E. G. L.

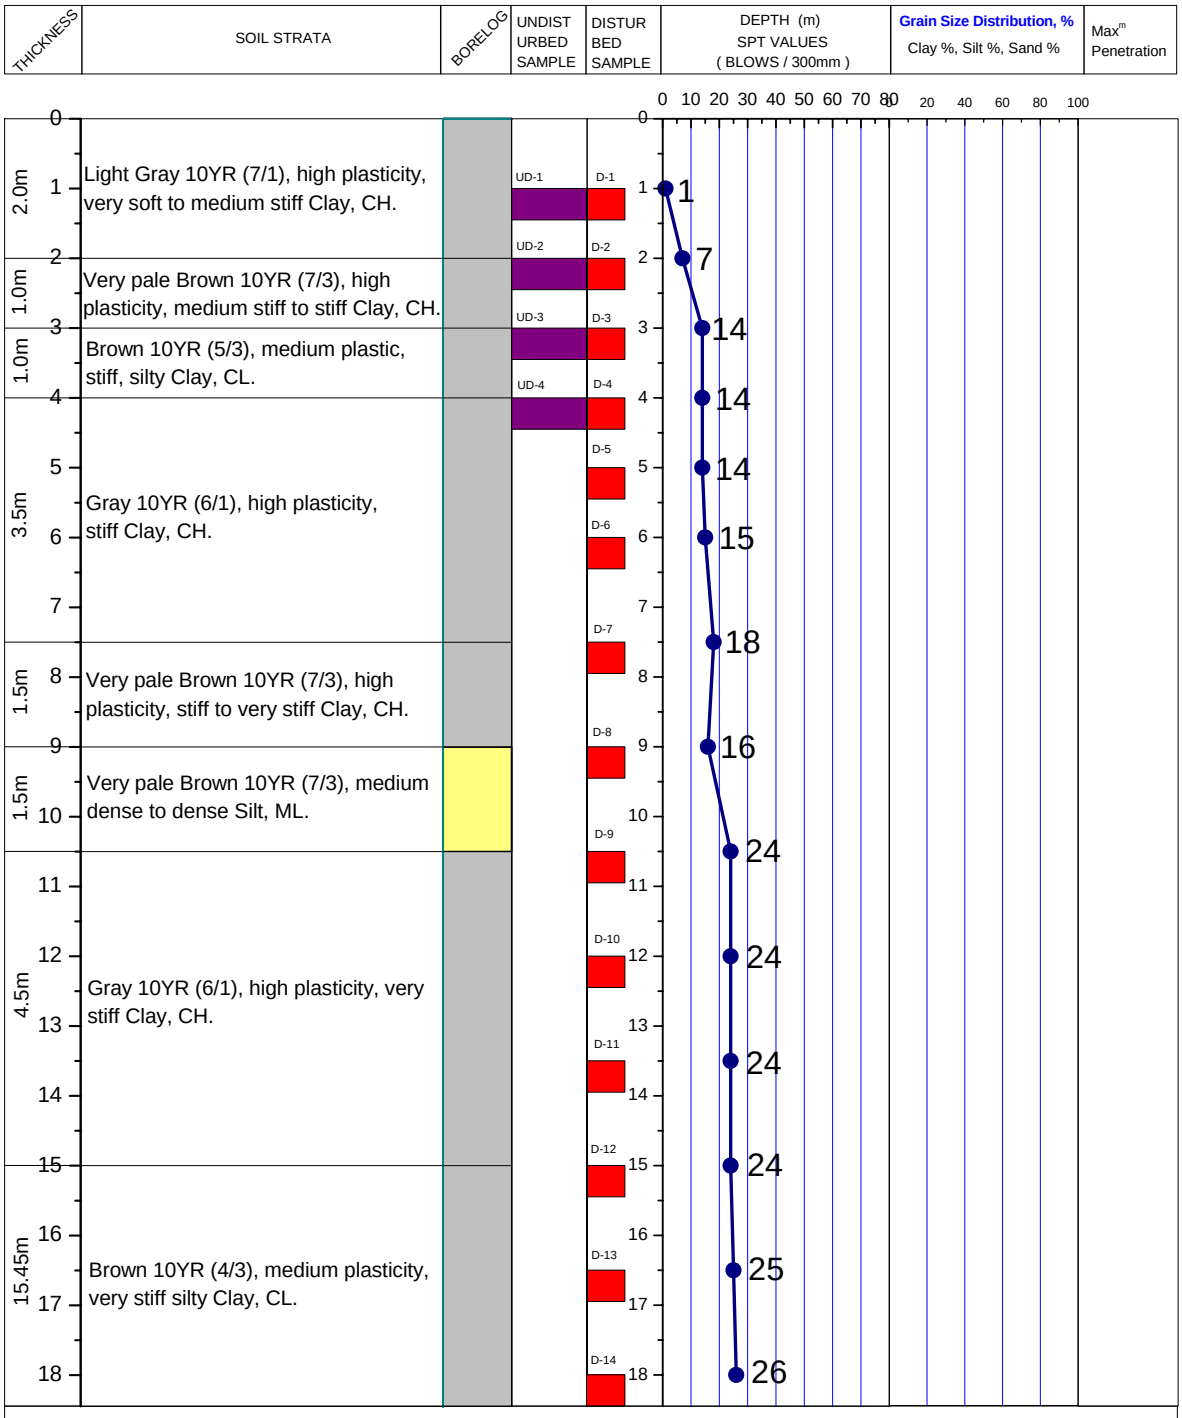

LEGEND FOR BORELOG AND GRAIN SIZE DISTRIBUTION (BASED ON 'ASTM CLASSIFICATION D-2487')

PLASTIC CLAY | SAND | SILT | SHALE

PEAT/HIGHLY ORGANIC SOIL | MICACEOUS FINE SAND/SILT | UNDISTURBED SAMPLE | DISTURBED SAMPLE

N- BLOWS DELIVERED PER FOOT BY A 140 LB HAMMER FALLING 30 INCHES

MAX^{m} PENETRATION= 50 BLOWS

AFTER 50 BLOWS PENETRATION DEPTH WERE MEASURED