A2	PROSOIL	BOREHOLE NO: BH-1	
		LOCATION : 6th km (University Gate) On Sylhet-Sunamgonj Road.	
PROJECT : Proposed Foot Over Bridge.		DEPTH OF BORING : 24.0m	Chainage: 5+000 R. L. : 11.71
CLIENT : Road Division, Sylhet.		DATE OF BORING : 25-02-2010.	G. W. T : 1.52m below from E.G.L.

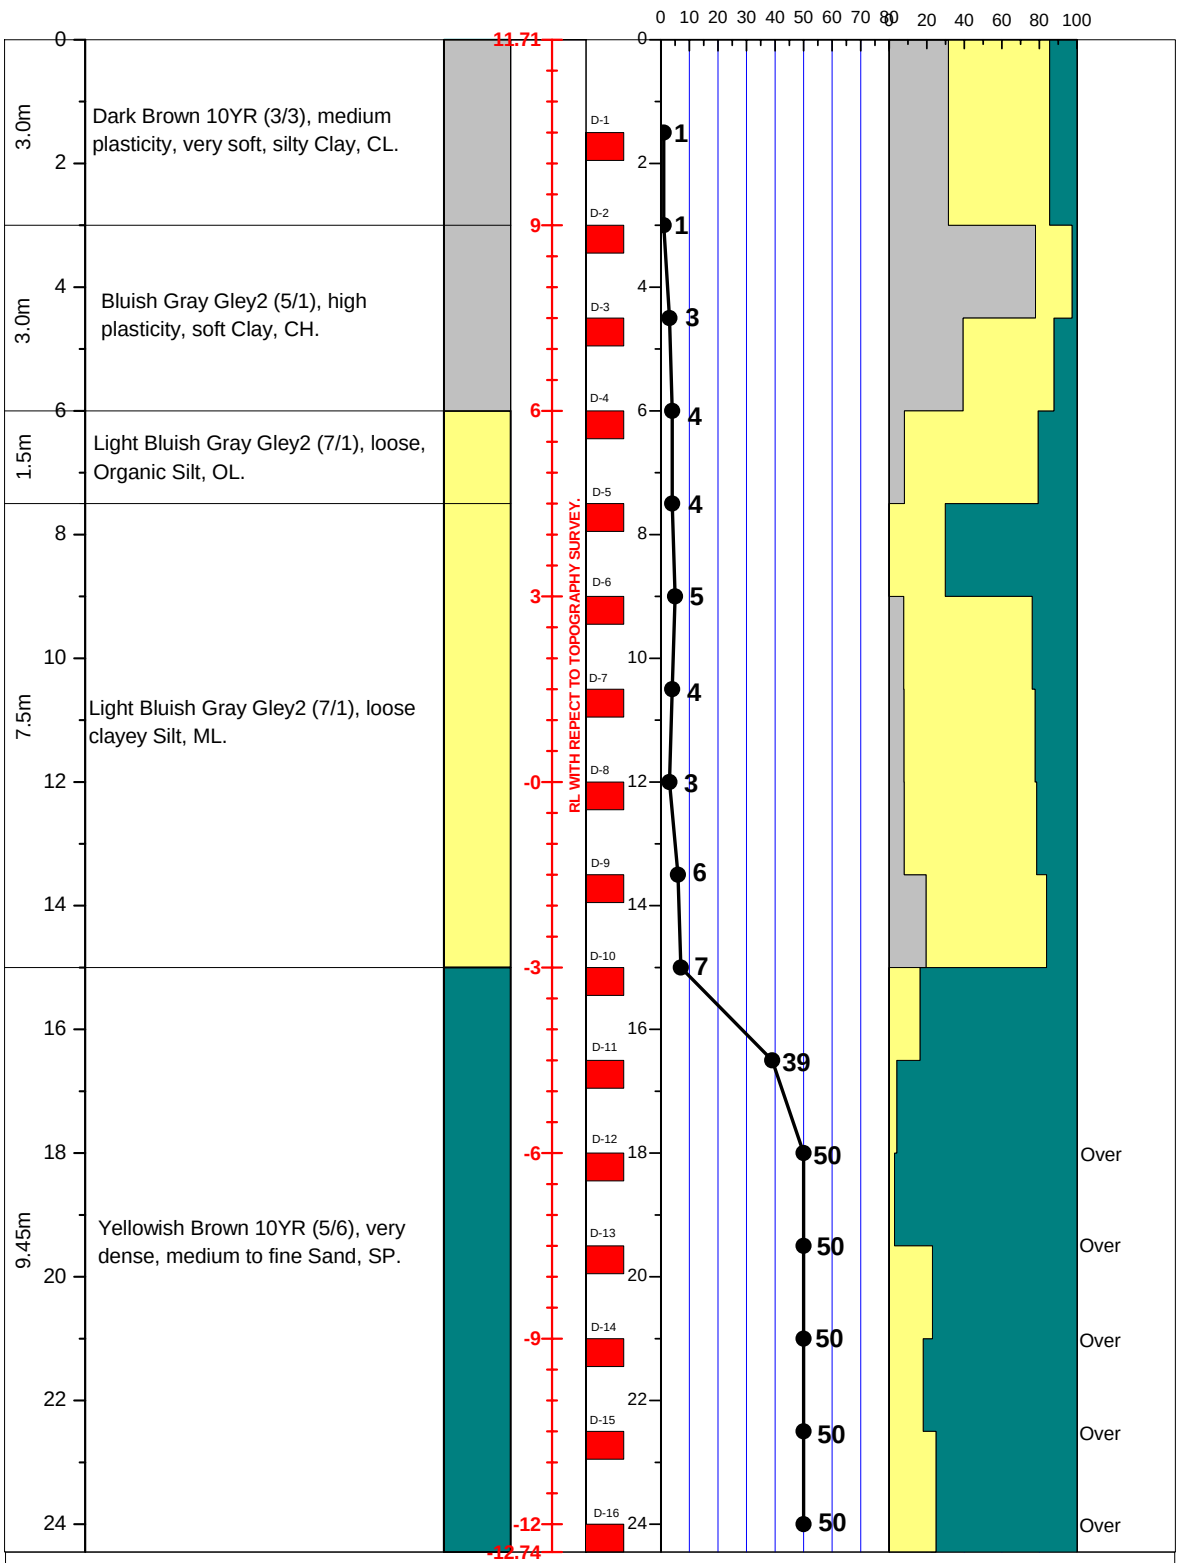

LEGEND FOR BORELOG AND GRAIN SIZE DISTRIBUTION (BASED ON 'ASTM CLASSIFICATION D-2487')

PLASTIC CLAY	SILT	PEAT/HIGHLY ORGANIC SOIL	UNDISTURBED SAMPLE
MICACEOUS FINE SAND/SILT	SAND	SHALE	DISTURBED SAMPLE

N- BLOWS DELIVERED PER FOOT BY A 140 LB HAMMER FALLING 30 INCHES

MAX^m PENETRATION= 50 BLOWS. AFTER 50 BLOWS PENETRATION DEPTH WERE MEASURED