A2	PROSOIL	BOREHOLE NO: BH-1	
		LOCATION : 40th km Of Pirojpur-Gopalgonj Road, Gopalgonj.	
PROJECT :Contruction Of Incomplete Sheikh Lutfar Rahman Bridge (Patgati Brige) Over The River Madhumoti.		DEPTH OF BORING : 54.0m	Chainage: 18+540.228 R. L. : -17.17m
CLIENT : Road Division, Gopalgonj.		DATE OF BORING : 16-01-2012.	G. W. T : 4.26m above from E.G.L.

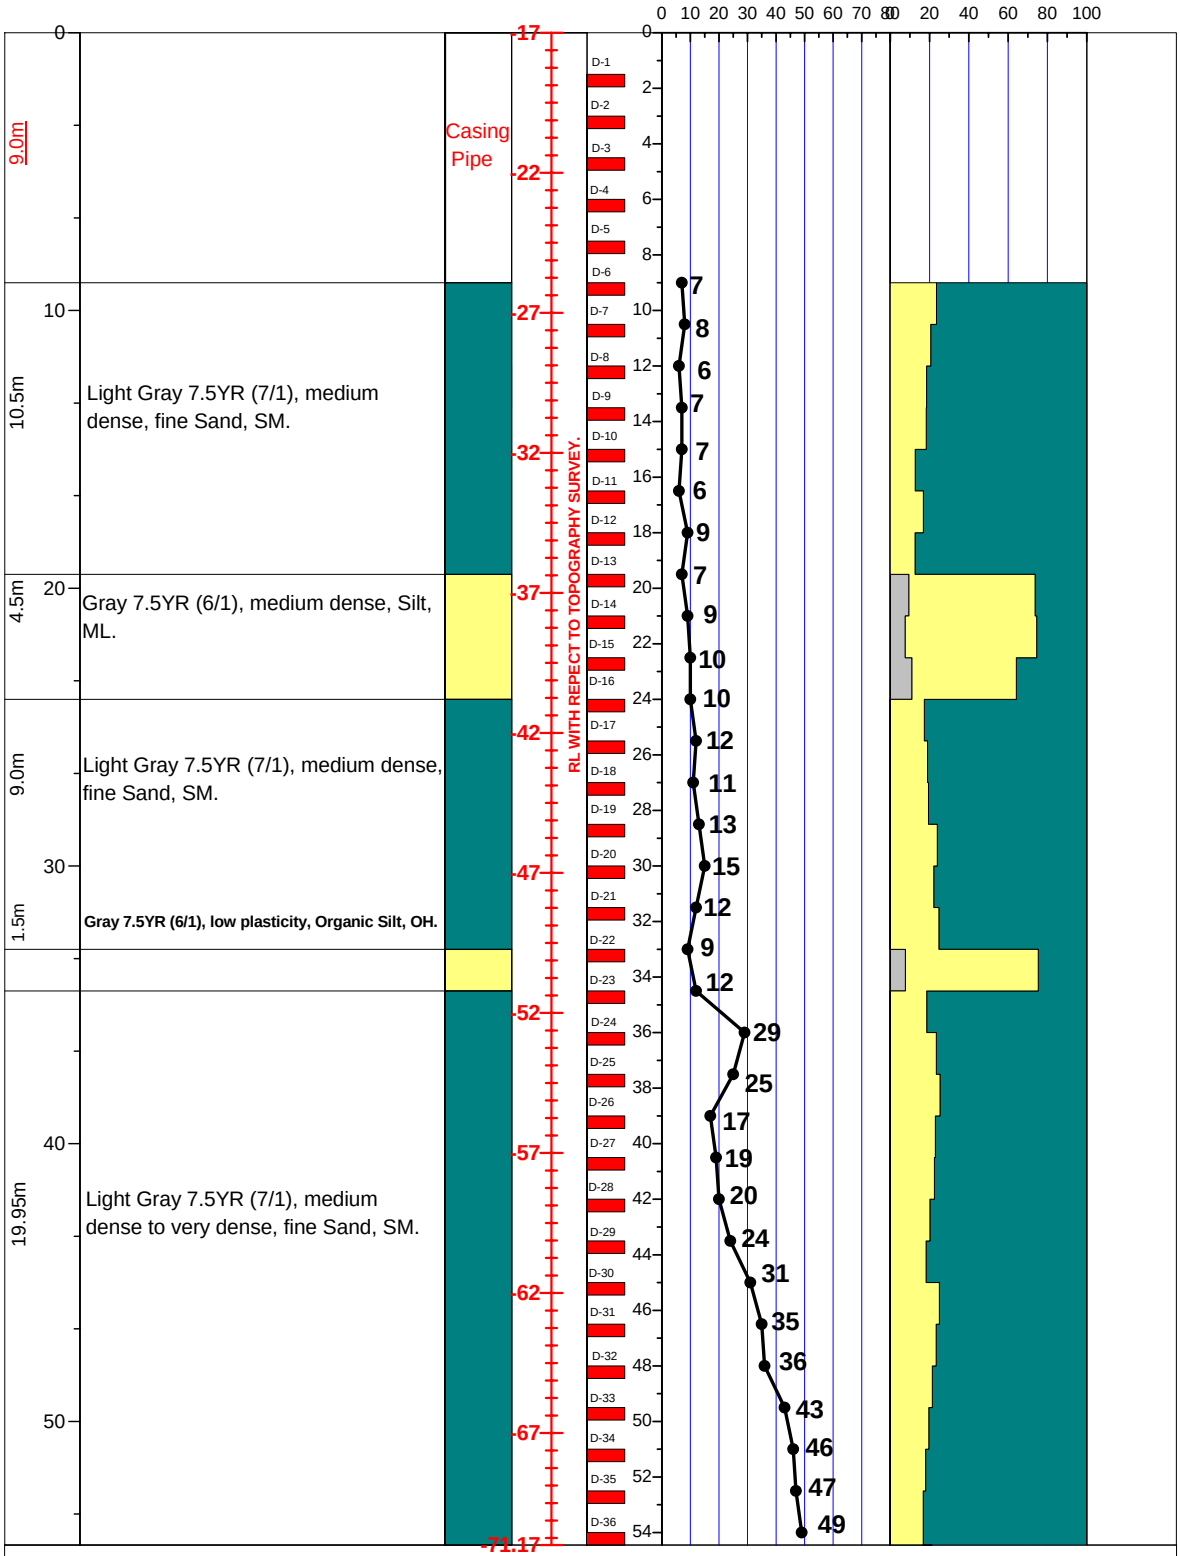

LEGEND FOR BOREHOLE AND GRAIN SIZE DISTRIBUTION (BASED ON 'ASTM CLASSIFICATION D-2487')

PLASTIC CLAY	SILT	PEAT/HIGHLY ORGANIC SOIL	UNDISTURBED SAMPLE
MICACEOUS FINE SAND/SILT	SAND	SHALE	DISTURBED SAMPLE

N- BLOWS DELIVERED PER FOOT BY A 140 LB HAMMER FALLING 30 INCHES

MAX^m PENETRATION= 50 BLOWS. AFTER 50 BLOWS PENETRATION DEPTH WERE MEASURED