A2	PROSOIL	BOREHOLE NO: BH-1	
		LOCATION : Langalbandh-Naduria Ghat Road, Rajbari.	
PROJECT : Proposed 719.74m (33.54m×16+45.0m×2+80.0m) Long P.C. Girder Bridge Over "Gorai River".		DEPTH OF BORING : 45.0m	Chainage: 5+241.5 R. L. : 17.2
CLIENT : Road Division, Rajbari.		DATE OF BORING : 07-06-2012.	G. W. T : 1.83m below from E.G.L.

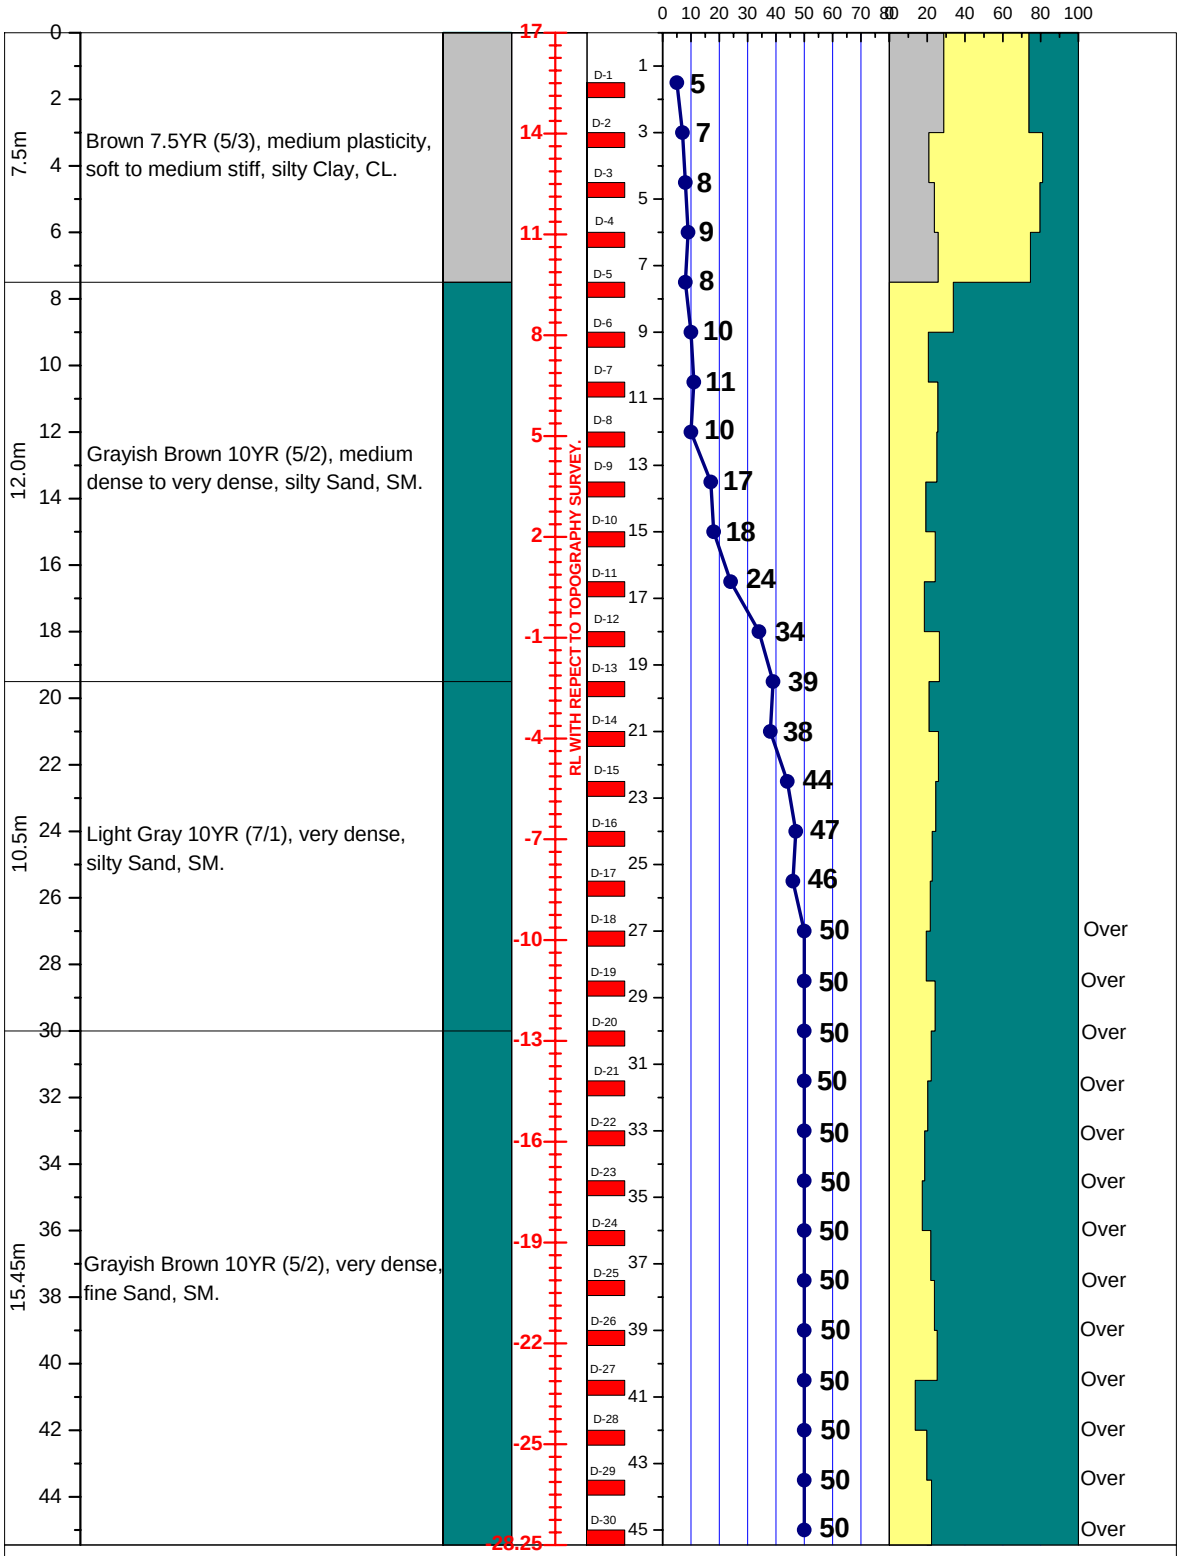

LEGEND FOR BORELOG AND GRAIN SIZE DISTRIBUTION (BASED ON 'ASTM CLASSIFICATION D-2487')

PLASTIC CLAY	SILT	PEAT/HIGHLY ORGANIC SOIL	UNDISTURBED SAMPLE
MICACEOUS FINE SAND/SILT	SAND	SHALE	DISTURBED SAMPLE

N- BLOWS DELIVERED PER FOOT BY A 140 LB HAMMER FALLING 30 INCHES

MAX^{m} PENETRATION= 50 BLOWS. AFTER 50 BLOWS PENETRATION DEPTH WERE MEASURED