A2 PROSOIL	BOREHOLE NO: BH-1	
	LOCATION : 73rd km Chainage 72+600 on Charkhai-Sheola-Beanibazar -Baroigram Road, Sylhet.	
PROJECT : Proposed Bridge At 73rd km.	DEPTH OF BORING : 42.0m	Chainage: 72+615 R. L. : 13.75
CLIENT : Road Division, Sylhet.	DATE OF BORING : 23-12-2010.	G. W. T : 3.05m below from E.G.L.

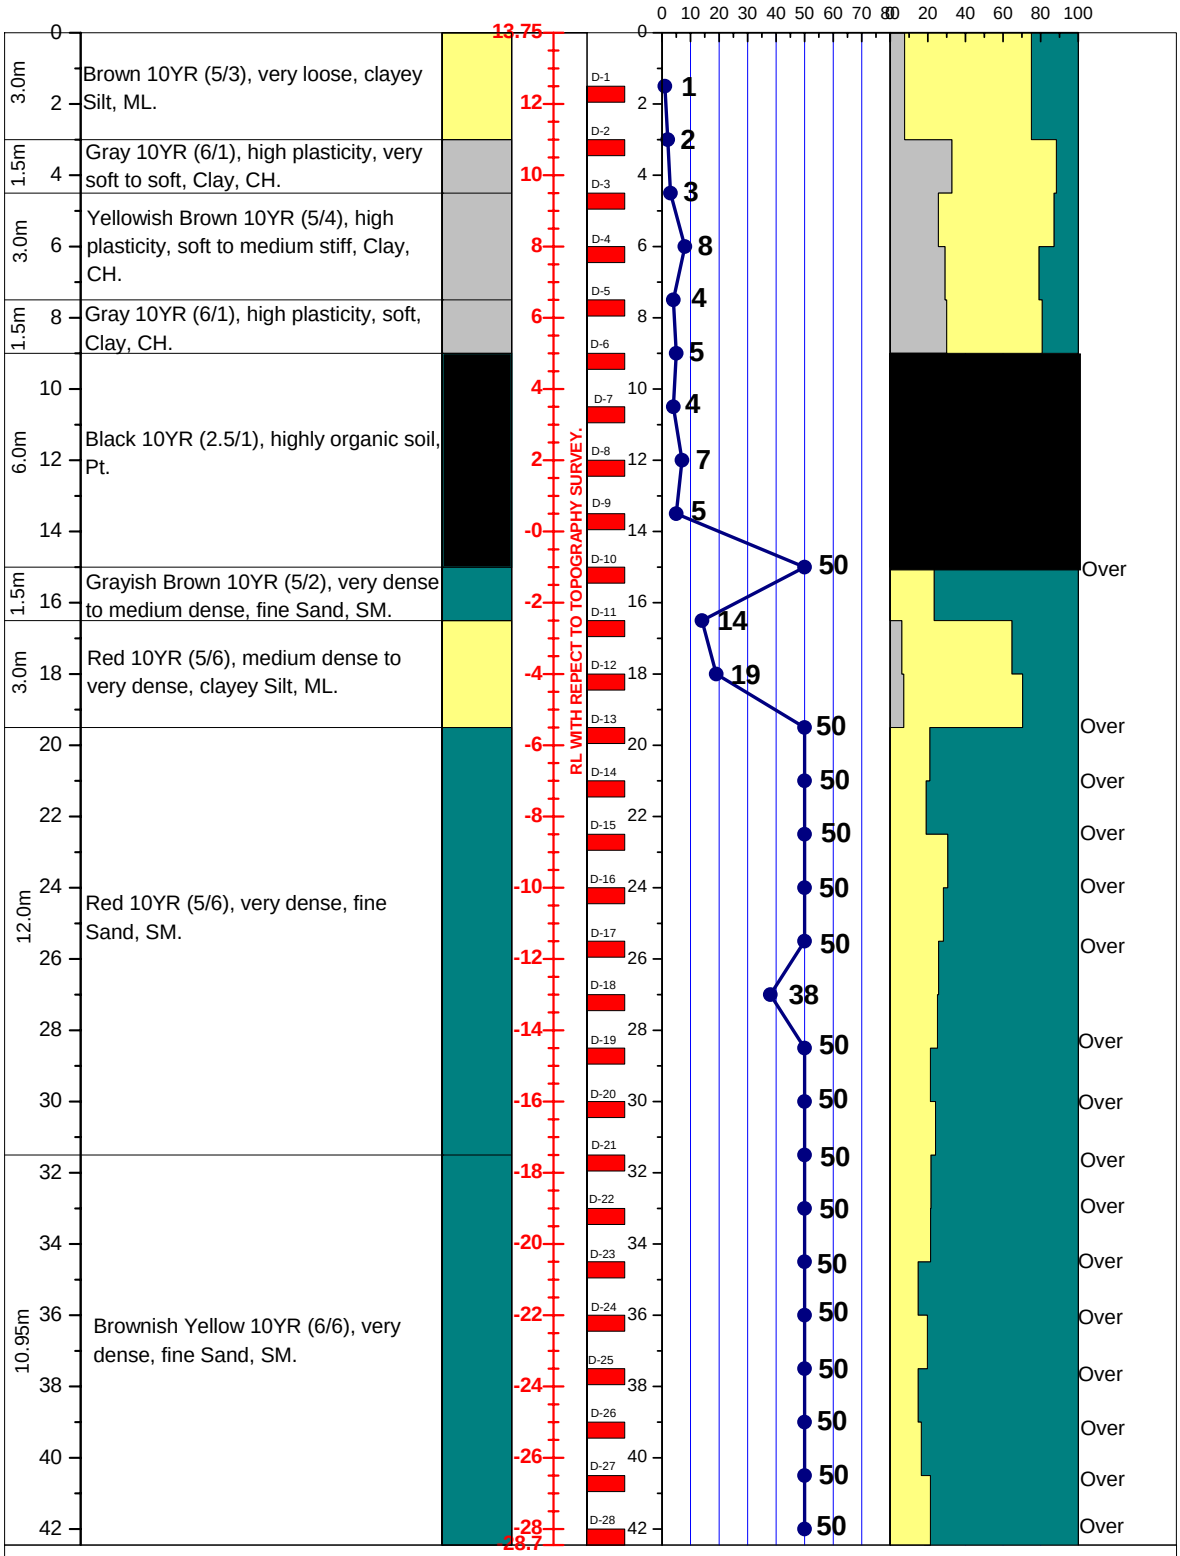

LEGEND FOR BORELOG AND GRAIN SIZE DISTRIBUTION (BASED ON 'ASTM CLASSIFICATION D-2487')

PLASTIC CLAY	SILT	PEAT/HIGHLY ORGANIC SOIL	UNDISTURBED SAMPLE
MICACEOUS FINE SAND/SILT	SAND	SHALE	DISTURBED SAMPLE

N- BLOWS DELIVERED PER FOOT BY A 140 LB HAMMER FALLING 30 INCHES

MAX^m PENETRATION= 50 BLOWS. AFTER 50 BLOWS PENETRATION DEPTH WERE MEASURED