A2	PROSOIL	BOREHOLE NO: BH-1	
		LOCATION : Vill+Post: Satkhamair,Union: Bormee,Upozilla: Sreepur, Zilla: Gazipur.	
PROJECT : PPS Plastic Pipe Industries Ltd.		DEPTH OF BORING : 18.0m	R. L.: 0.91m below from Road Level.
CLIENT : Shaila Sabrin.		DATE OF BORING: 24-02-2014.	B. W. T : 0.31m below from E.G.L.

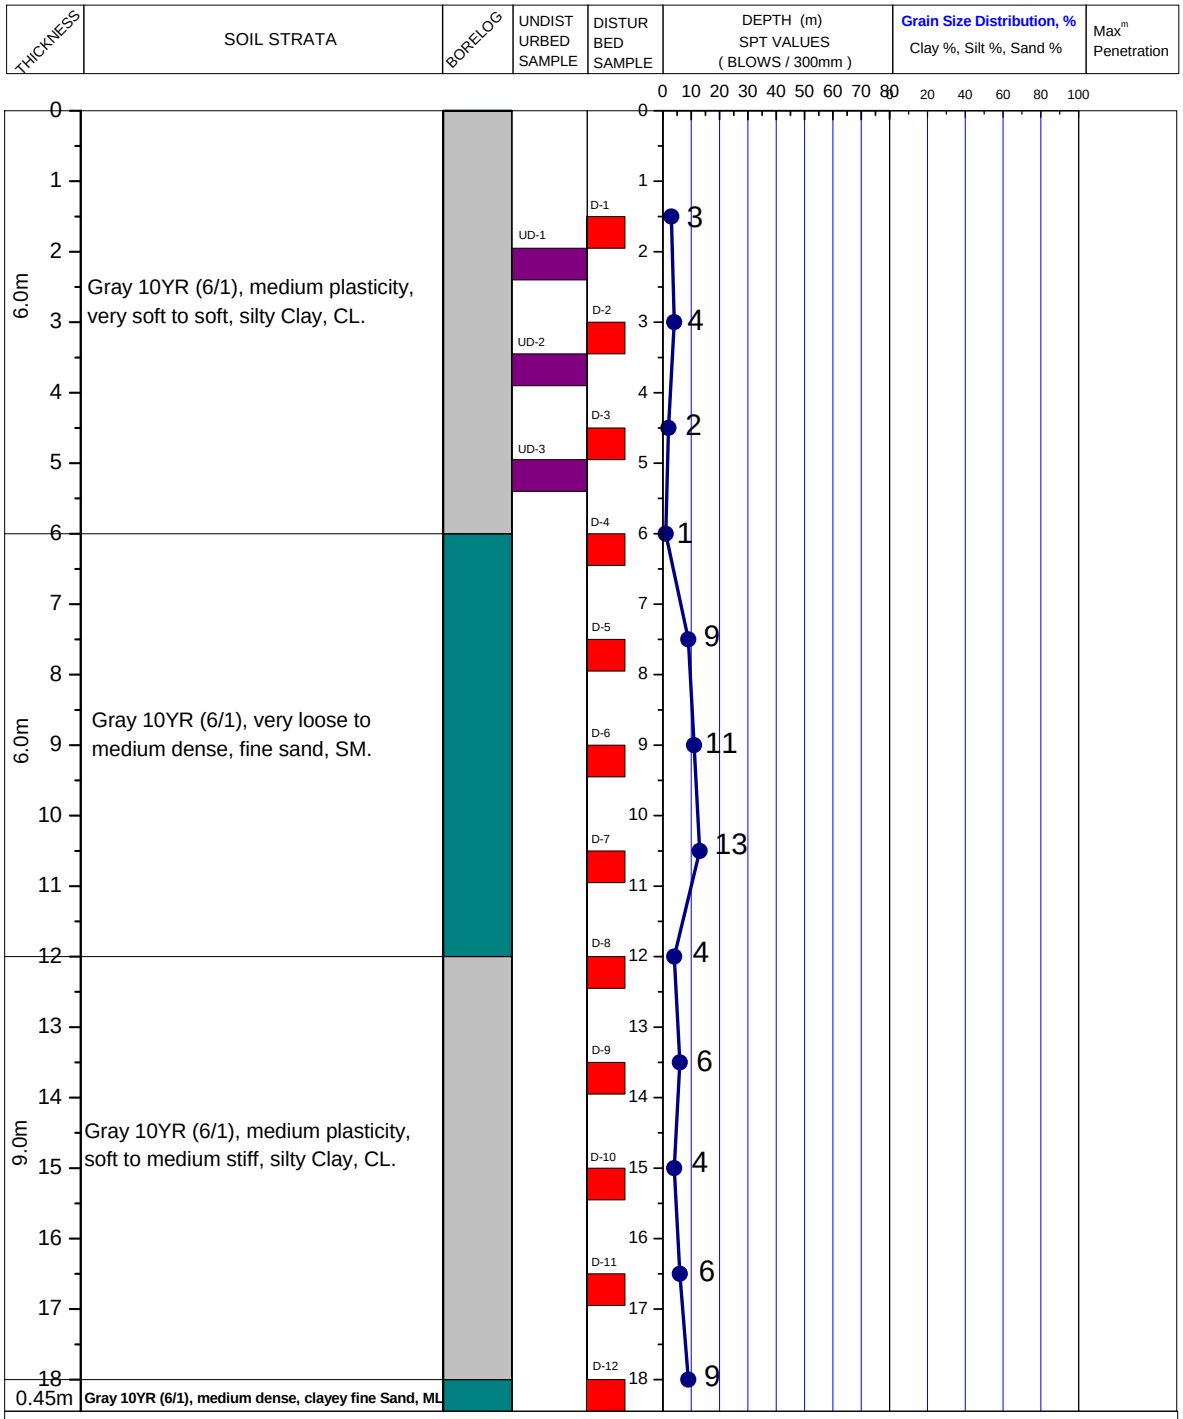

LEGEND FOR BORELOG AND GRAIN SIZE DISTRIBUTION (BASED ON 'ASTM CLASSIFICATION D-2487')

PLASTIC CLAY	SAND	SHALE	UNDISTURBED SAMPLE
MICACEOUS FINE SAND/SILT	SILT	PEAT/HIGHLY ORGANIC SOIL	DISTURBED SAMPLE

N- BLOWS DELIVERED PER FOOT BY A 140 LB HAMMER FALLING 30 INCHES

MAX^{m} PENETRATION= 50 BLOWS

AFTER 50 BLOWS PENETRATION DEPTH WERE MEASURED