A2	PROSOIL	BOREHOLE NO: BH-1	
		LOCATION : 4th Km (Gap No. 4/1) On Birishiri-Bijoypur Land Port Road, Netrakona.	
PROJECT : Proposed 15.96m (1×15.25m) Long R.C.C. Girder Madhupara Bridge At 4th Km (Gap No. 4/1).		DEPTH OF BORING : 51.0m	Chainage: 3+552.625 R. L. : 15.8
CLIENT : Road Division, Netrakona.		DATE OF BORING : 27-01-2013.	G. W. T : 1.83m below from E.G.L.

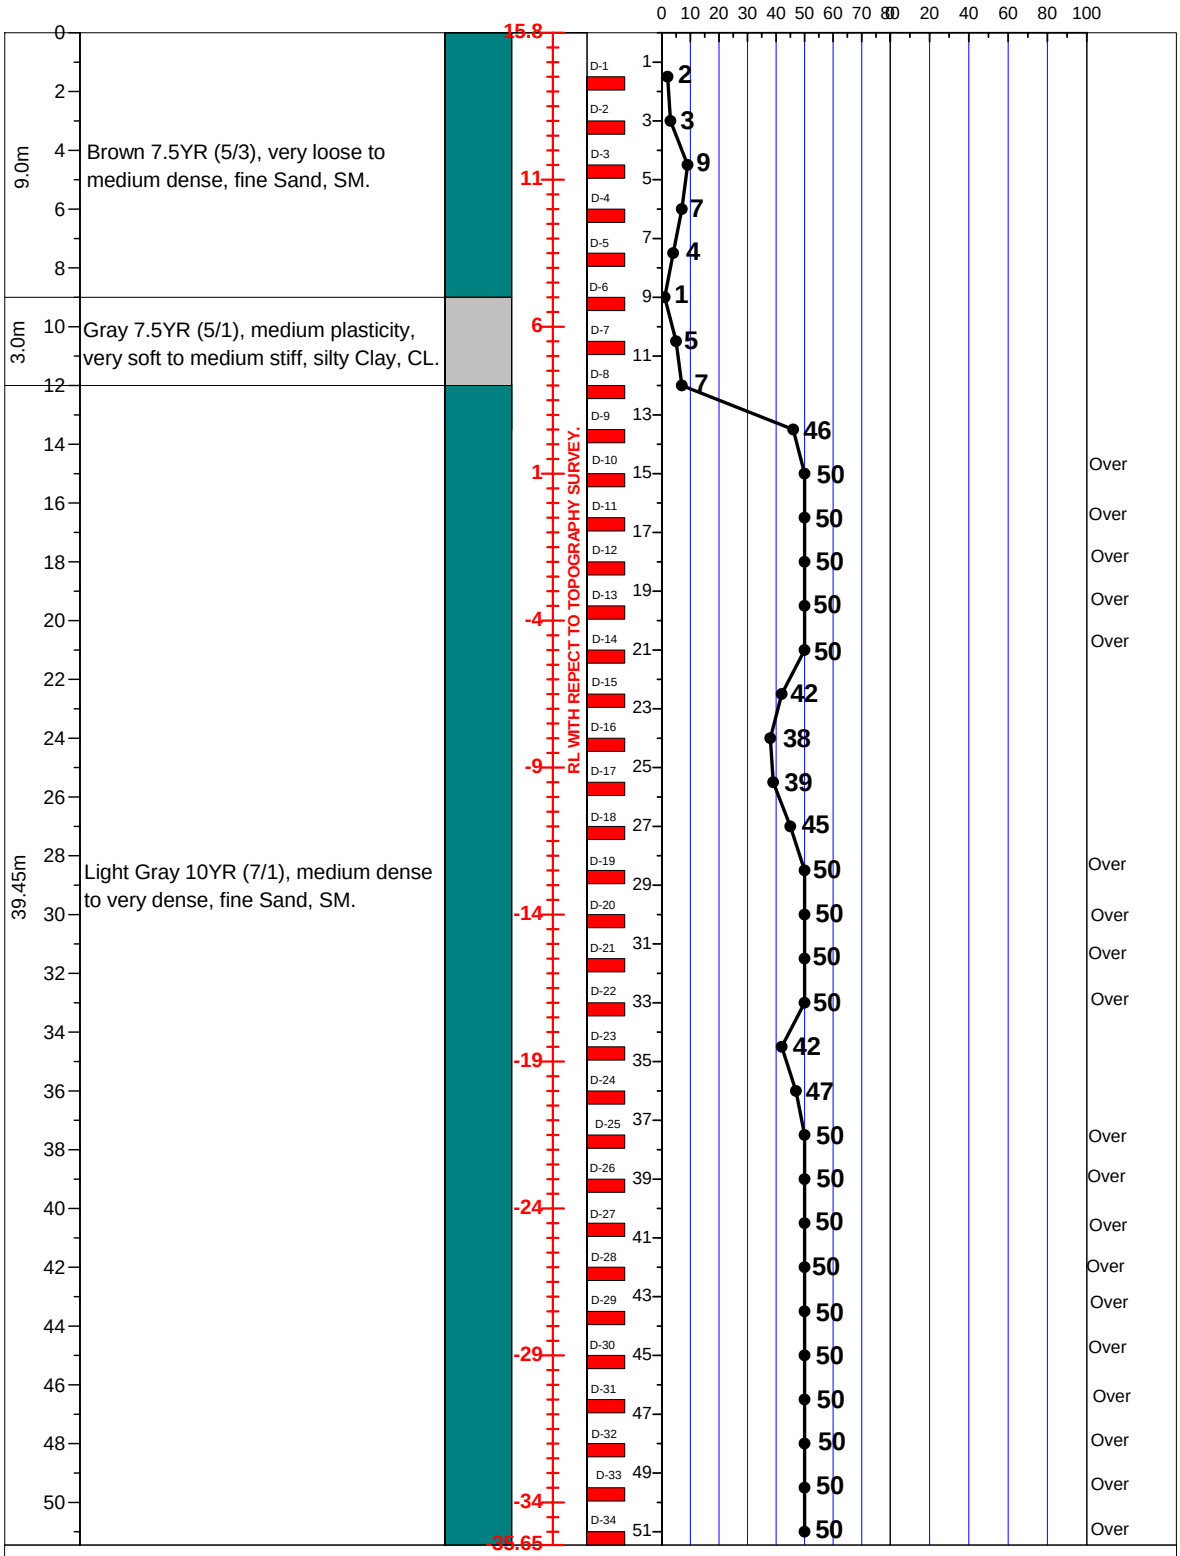

LEGEND FOR BOREHOLE AND GRAIN SIZE DISTRIBUTION (BASED ON 'ASTM CLASSIFICATION D-2487')

PLASTIC CLAY | SILT | PEAT/HIGHLY ORGANIC SOIL | UNDISTURBED SAMPLE

MICACEOUS FINE SAND/SILT | SAND | SHALE | DISTURBED SAMPLE

N- BLOWS DELIVERED PER FOOT BY A 140 LB HAMMER FALLING 30 INCHES

MAX^m PENETRATION= 50 BLOWS. AFTER 50 BLOWS PENETRATION DEPTH WERE MEASURED