
A2	PROSOIL	Borehole No: 03	Easting: 239748	Northing: 2738712
		Location: Kewatkhali		Borehole Depth: 97.5m
Name of Project: Kewatkhali Bridge Project.		Type of Drill Rig: Hydraulic Rotary Drilling.		R. L. : 9.816m
CLIENT: Roads & Highways Department, Mymensingh.		Date of Boring: 30-03-2022 to 06-04-2022		B. W. T : 6.5m below from E. G. L.

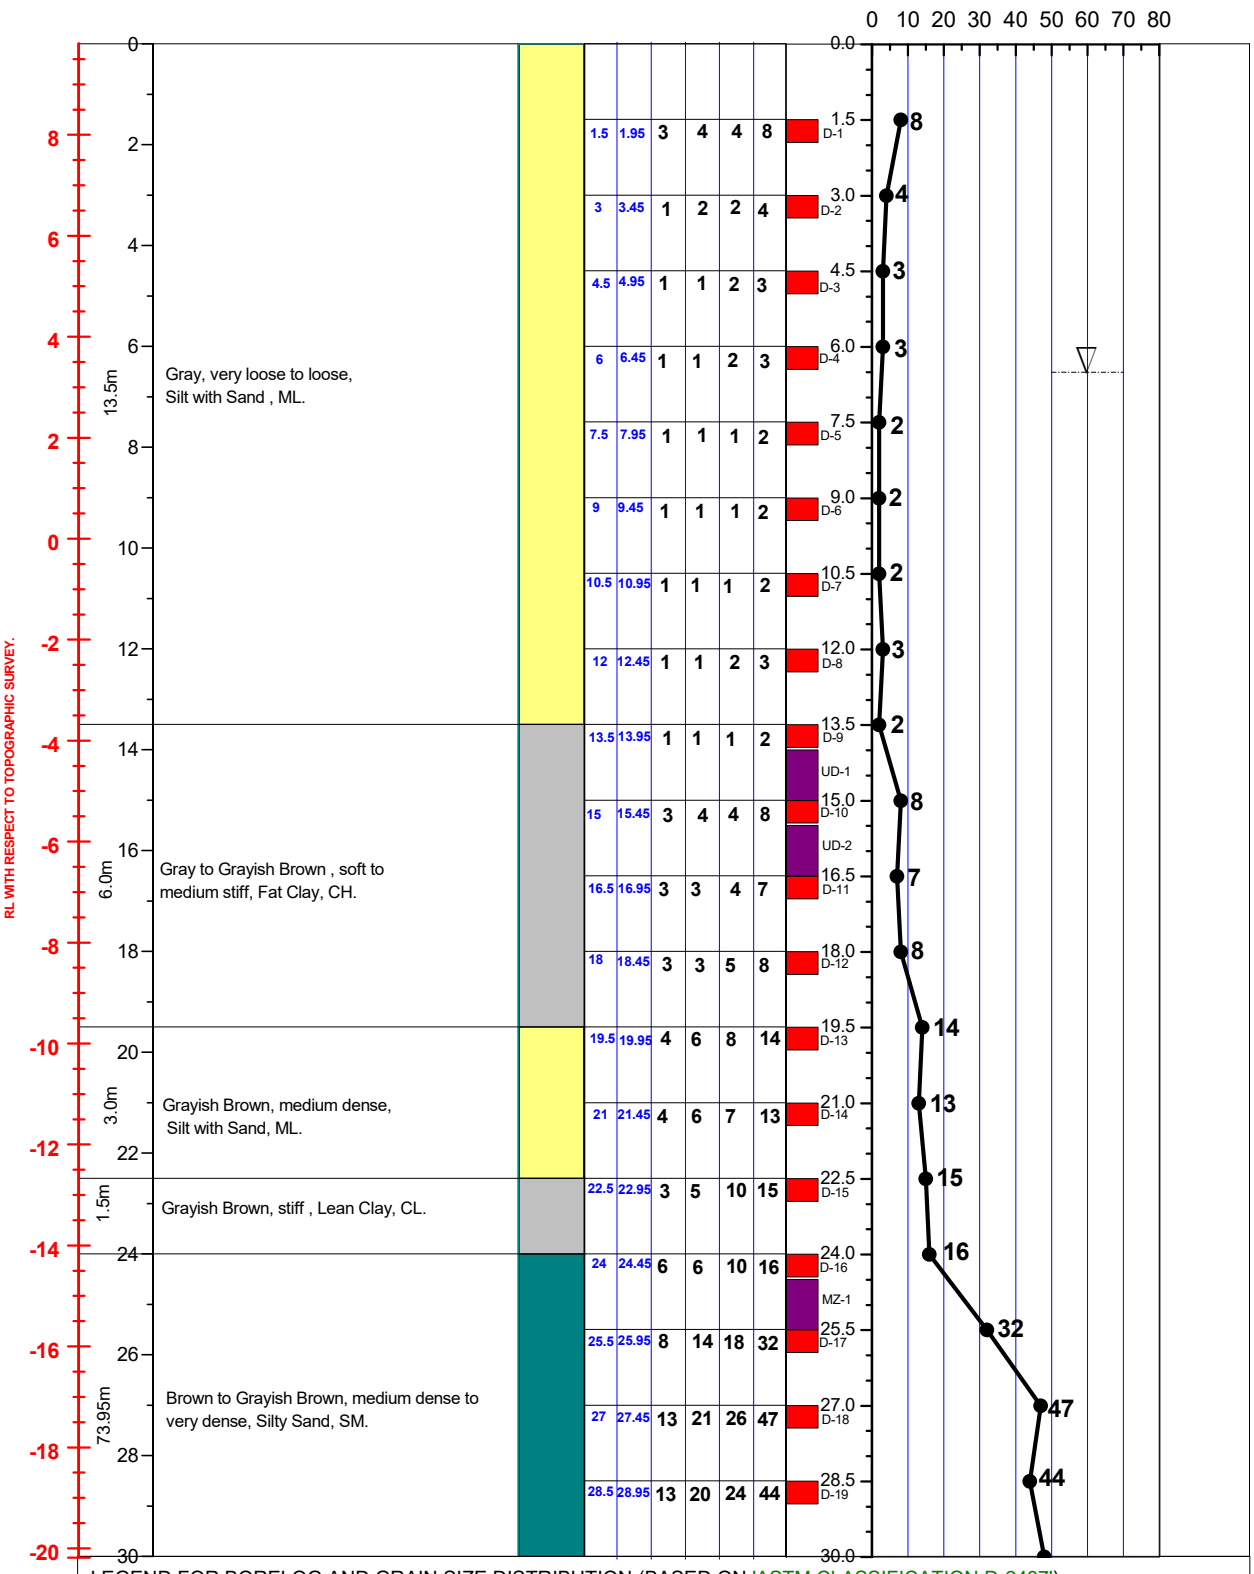

LEGEND FOR BORELOG AND GRAIN SIZE DISTRIBUTION (BASED ON 'ASTM CLASSIFICATION D-2487')

PLASTIC CLAY	SILT	PEAT/HIGHLY ORGANIC SOIL	UNDISTURBED SAMPLE
MICACEOUS FINE SAND/SILT	SAND	SHALE	DISTURBED SAMPLE

N- BLOWS DELIVERED PER FOOT BY A 140 LB HAMMER FALLING 30 INCHES

MAX^{m} PENETRATION= 50 BLOWS. AFTER 50 BLOWS PENETRATION DEPTH WERE MEASURED