
A2	PROSOIL	BOREHOLE NO: 01	
		LOCATION : Narail sadar.	
PROJECT : Construction of 1.05 lakh MT capacity new food godowns.		DEPTH OF BORING : 21.0m	R. L. : 0.30m
CLIENT : Government of the peoples republic of bangladesh office of the director.		DATE OF BORING : 05-03-2018	B. W. T : 2.44m below from E. G. L.

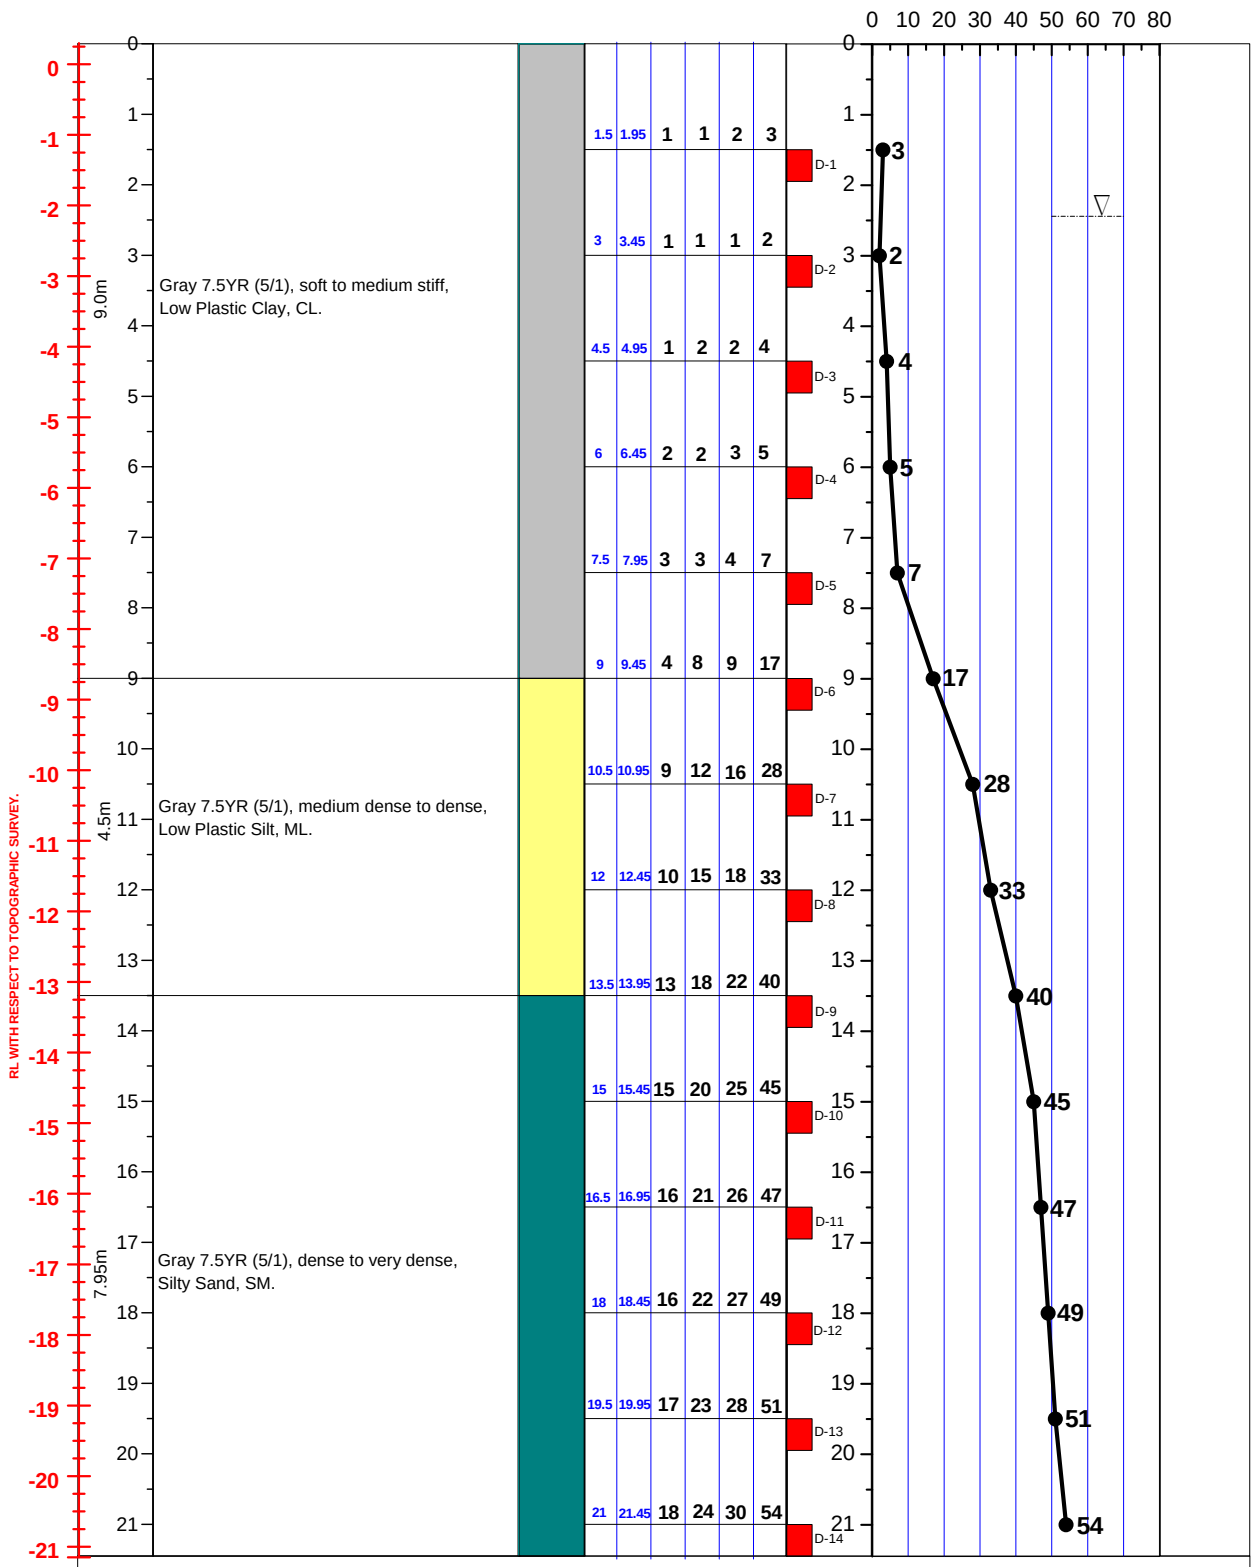

LEGEND FOR BORELOG AND GRAIN SIZE DISTRIBUTION (BASED ON 'ASTM CLASSIFICATION D-2487')

PLASTIC CLAY	SILT	PEAT/HIGHLY ORGANIC SOIL	UNDISTURBED SAMPLE
MICACEOUS FINE SAND/SILT	SAND	SHALE	DISTURBED SAMPLE

N- BLOWS DELIVERED PER FOOT BY A 140 LB HAMMER FALLING 30 INCHES

MAX^m PENETRATION= 50 BLOWS. AFTER 50 BLOWS PENETRATION DEPTH WERE MEASURED