A2	PROSOIL	BOREHOLE NO: BH-1	
		LOCATION : Dhara Bashail, Kotalipara, Gopalgonj.	
PROJECT : Proposed Six (6) Storied Building.		DEPTH OF BORING : 18.0m	R. L.: 0.45m below from Road Level.
CLIENT : Mr. David Barikdar.		DATE OF BORING : 22-01-2010	G. W. T : 1.82m below from E. G. L.

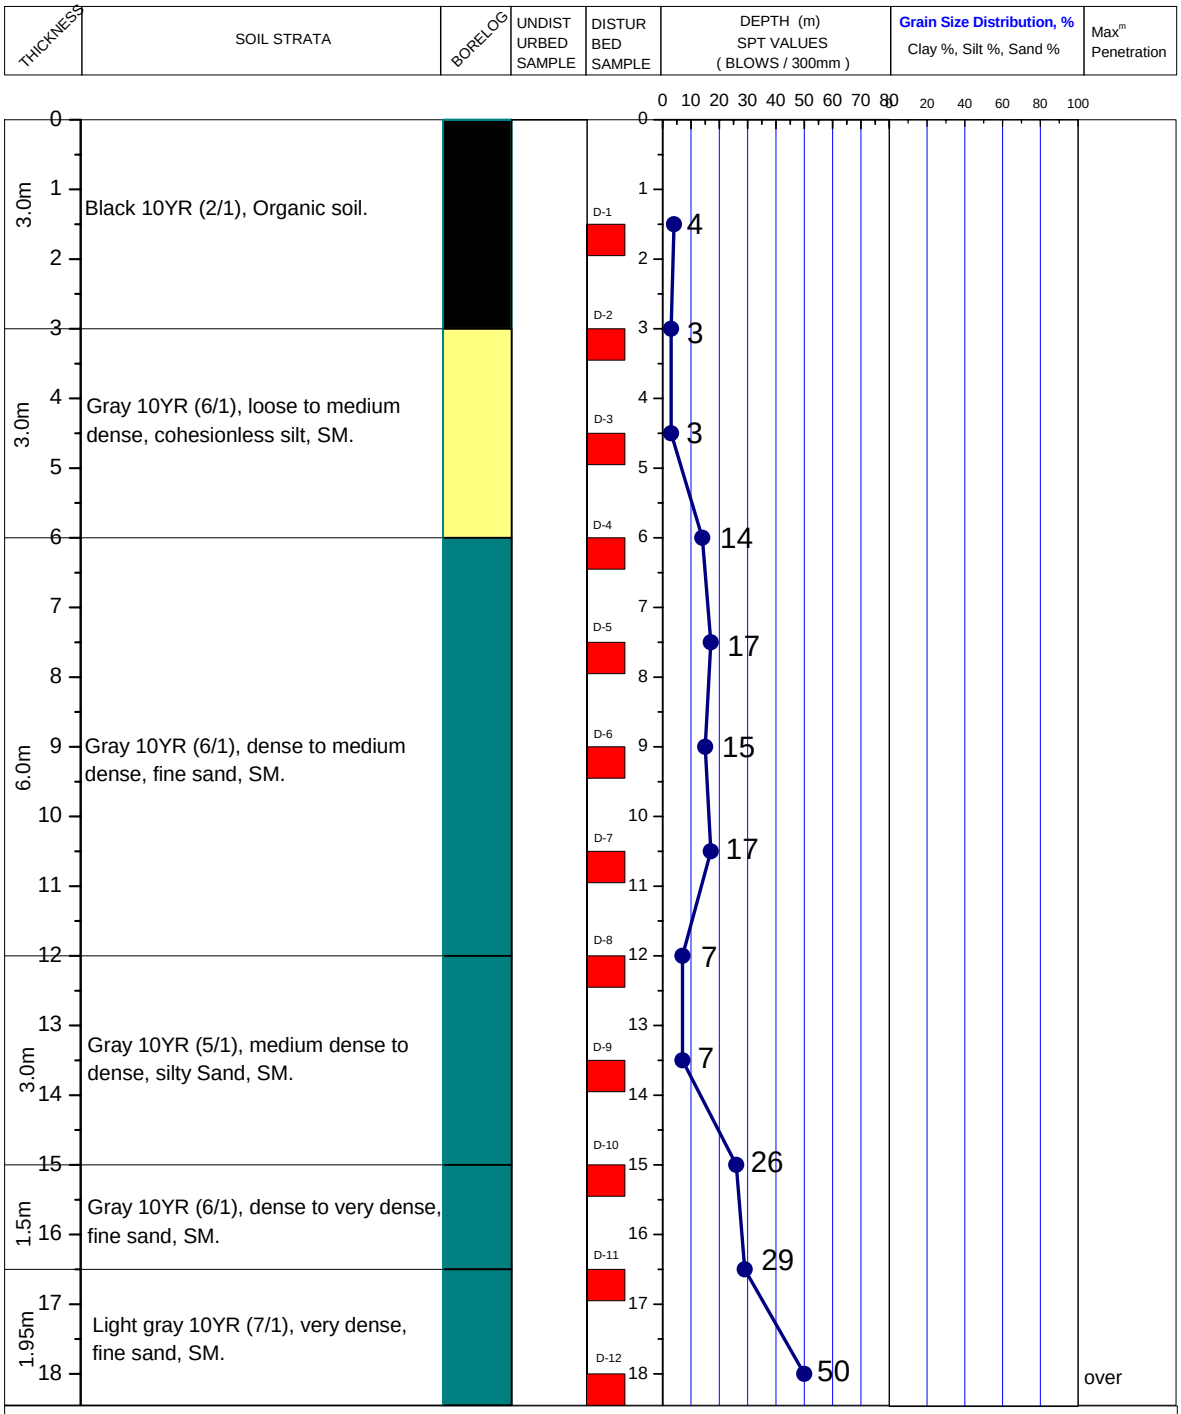

LEGEND FOR BORELOG AND GRAIN SIZE DISTRIBUTION

PLASTIC SILTY CLAY	NON PLASTIC SILT	ORGANIC	UNDISTURBED SAMPLE
LOW PLASTIC CLAYEY SILT	SAND	SHALE	DISTURBED SAMPLE

N- BLOWS DELIVERED PER FOOT BY A 140 LB HAMMER FALLING 30 INCHES

MAX^{m} PENETRATION= 50 BLOWS

AFTER 50 BLOWS PENETRATION DEPTH WERE MEASURED