A2	PROSOIL	BOREHOLE NO: BH-1	
		LOCATION : Chikondi Police Fari, Shariatpur.	
PROJECT : Chikondi Police Fari, Shariatpur		DEPTH OF BORING : 30.0m	R. L.: 2.13m below from Road Level.
CLIENT : PWD.		DATE OF BORING: 15-12-2014.	B. W. T : 0.91m below from E.G.L.

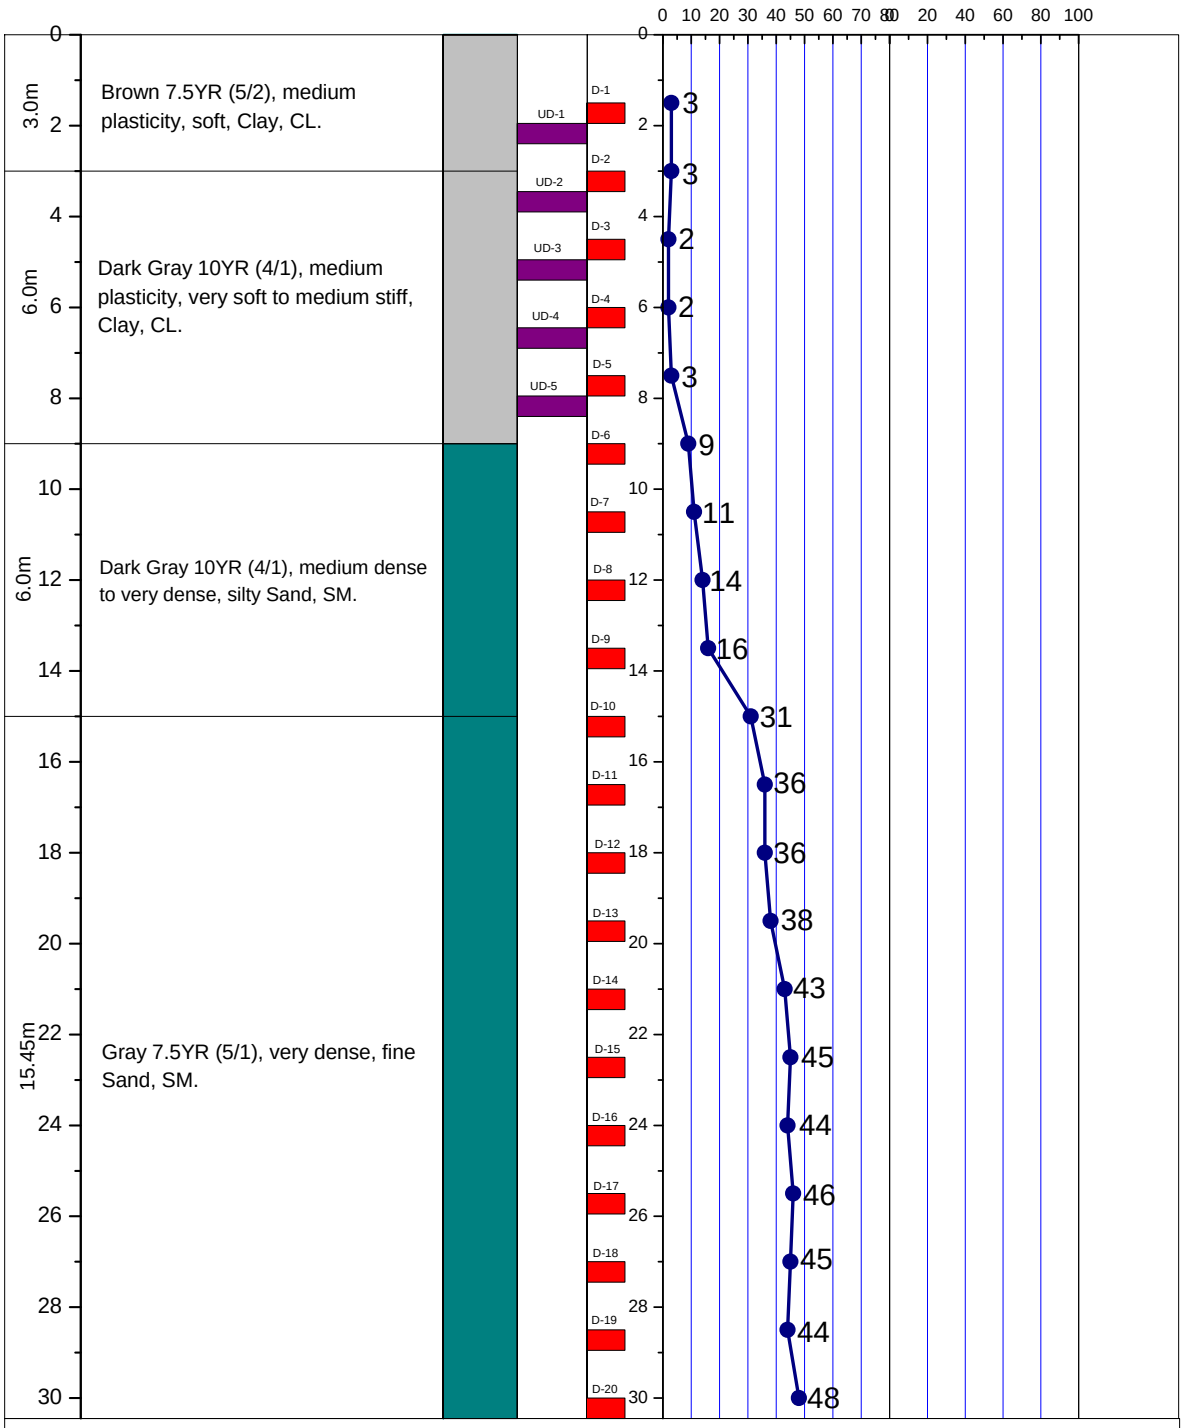

LEGEND FOR BORELOG AND GRAIN SIZE DISTRIBUTION (BASED ON 'ASTM CLASSIFICATION D-2487')

PLASTIC CLAY	SILT	SHALE	UNDISTURBED SAMPLE
MICACEOUS FINE SAND/SILT	SAND	PEAT/HIGHLY ORGANIC SOIL	DISTURBED SAMPLE

N- BLOWS DELIVERED PER FOOT BY A 140 LB HAMMER FALLING 30 INCHES

MAX^{m} PENETRATION= 50 BLOWS
AFTER 50 BLOWS PENETRATION DEPTH WERE MEASURED