A2	PROSOIL	BOREHOLE NO: BH-1	
		LOCATION : Chorpukuria Bazar, Niamotpur, Naogaon.	
PROJECT : Telecommunication Tower.		DEPTH OF BORING : 15.0m	R. L.: Road Level.
CLIENT : Grameenphone Ltd.		DATE OF BORING : 10-06-2009.	G. W. T : 1.21m below from E. G. L.

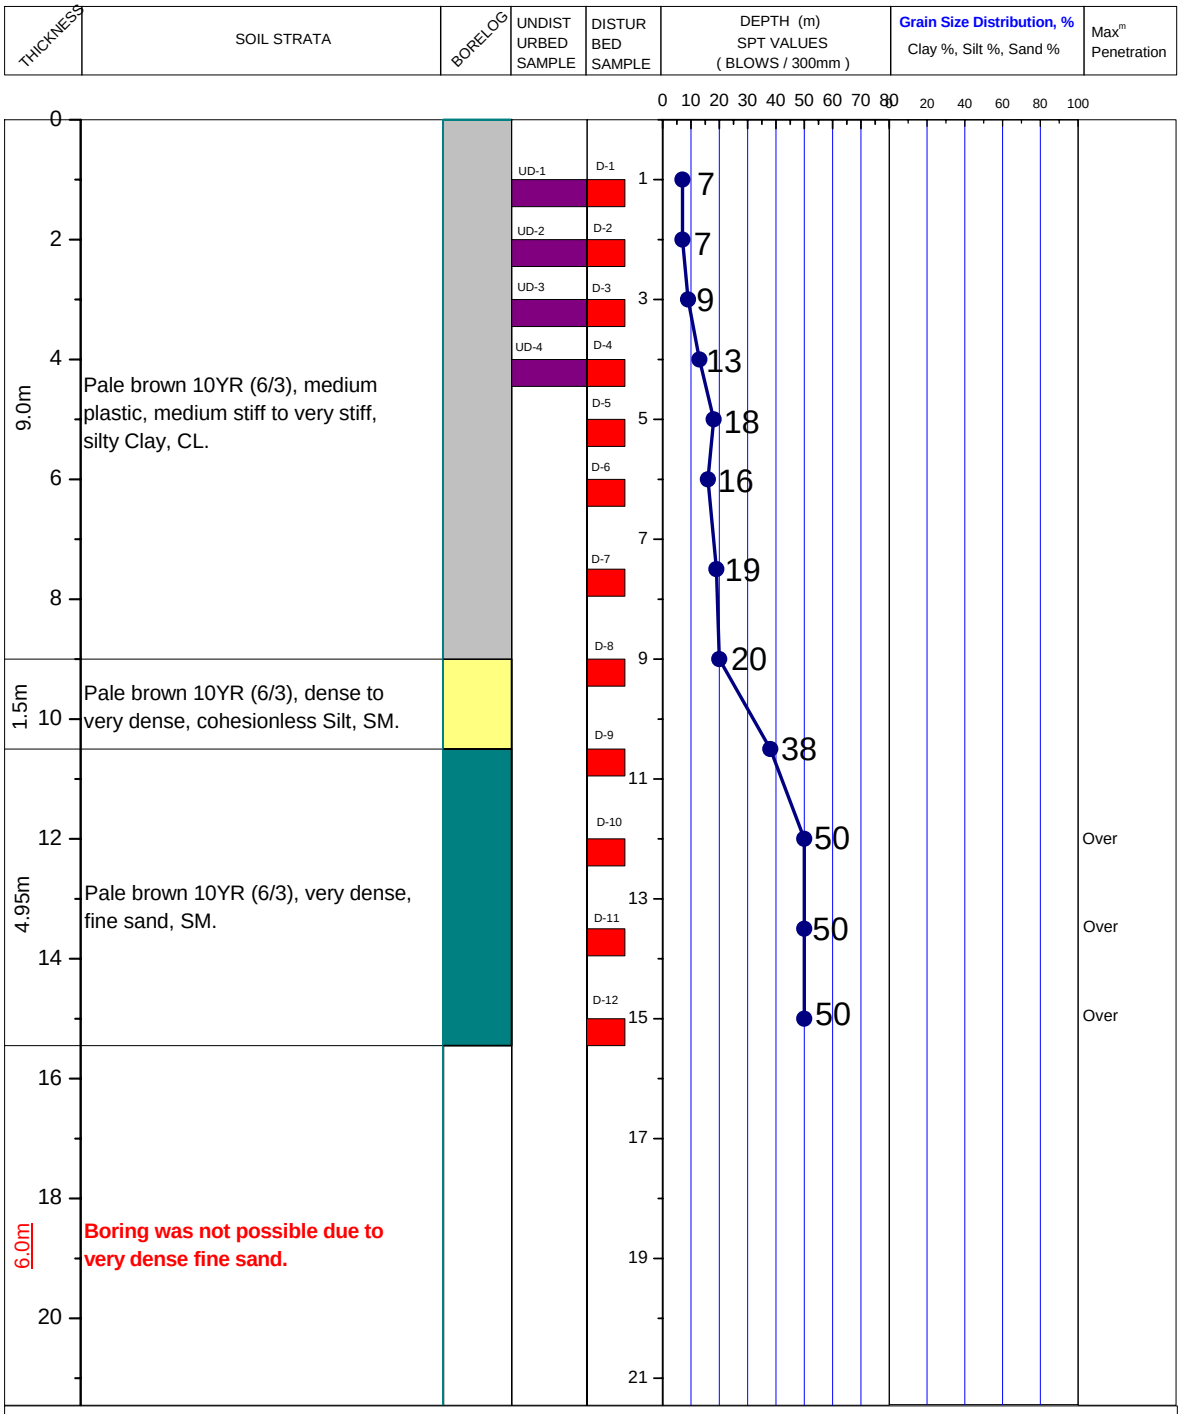

LEGEND FOR BORELOG AND GRAIN SIZE DISTRIBUTION

PLASTIC SILTY CLAY

LOW PLASTIC CLAYEY SILT

NON PLASTIC SILT

SAND

ORGANIC

UNDISTURBED SAMPLE

DISTURBED SAMPLE

SHALE

N- BLOWS DELIVERED PER FOOT BY A 140 LB HAMMER FALLING 30 INCHES

MAX^{m} PENETRATION= 50 BLOWS

AFTER 50 BLOWS PENETRATION DEPTH WERE MEASURED