A2 PROSOIL	BOREHOLE NO: BH-1	
	LOCATION : Goawainghat, Sylhet.	
PROJECT : Telecommunication Tower.	DEPTH OF BORING : 21.0m	R. L.: 2.0m below from Road Level.
CLIENT : Grameen phone Ltd.	DATE OF BORING : 04-01-2005	G. W. T : 2.44m below from E. G. L.

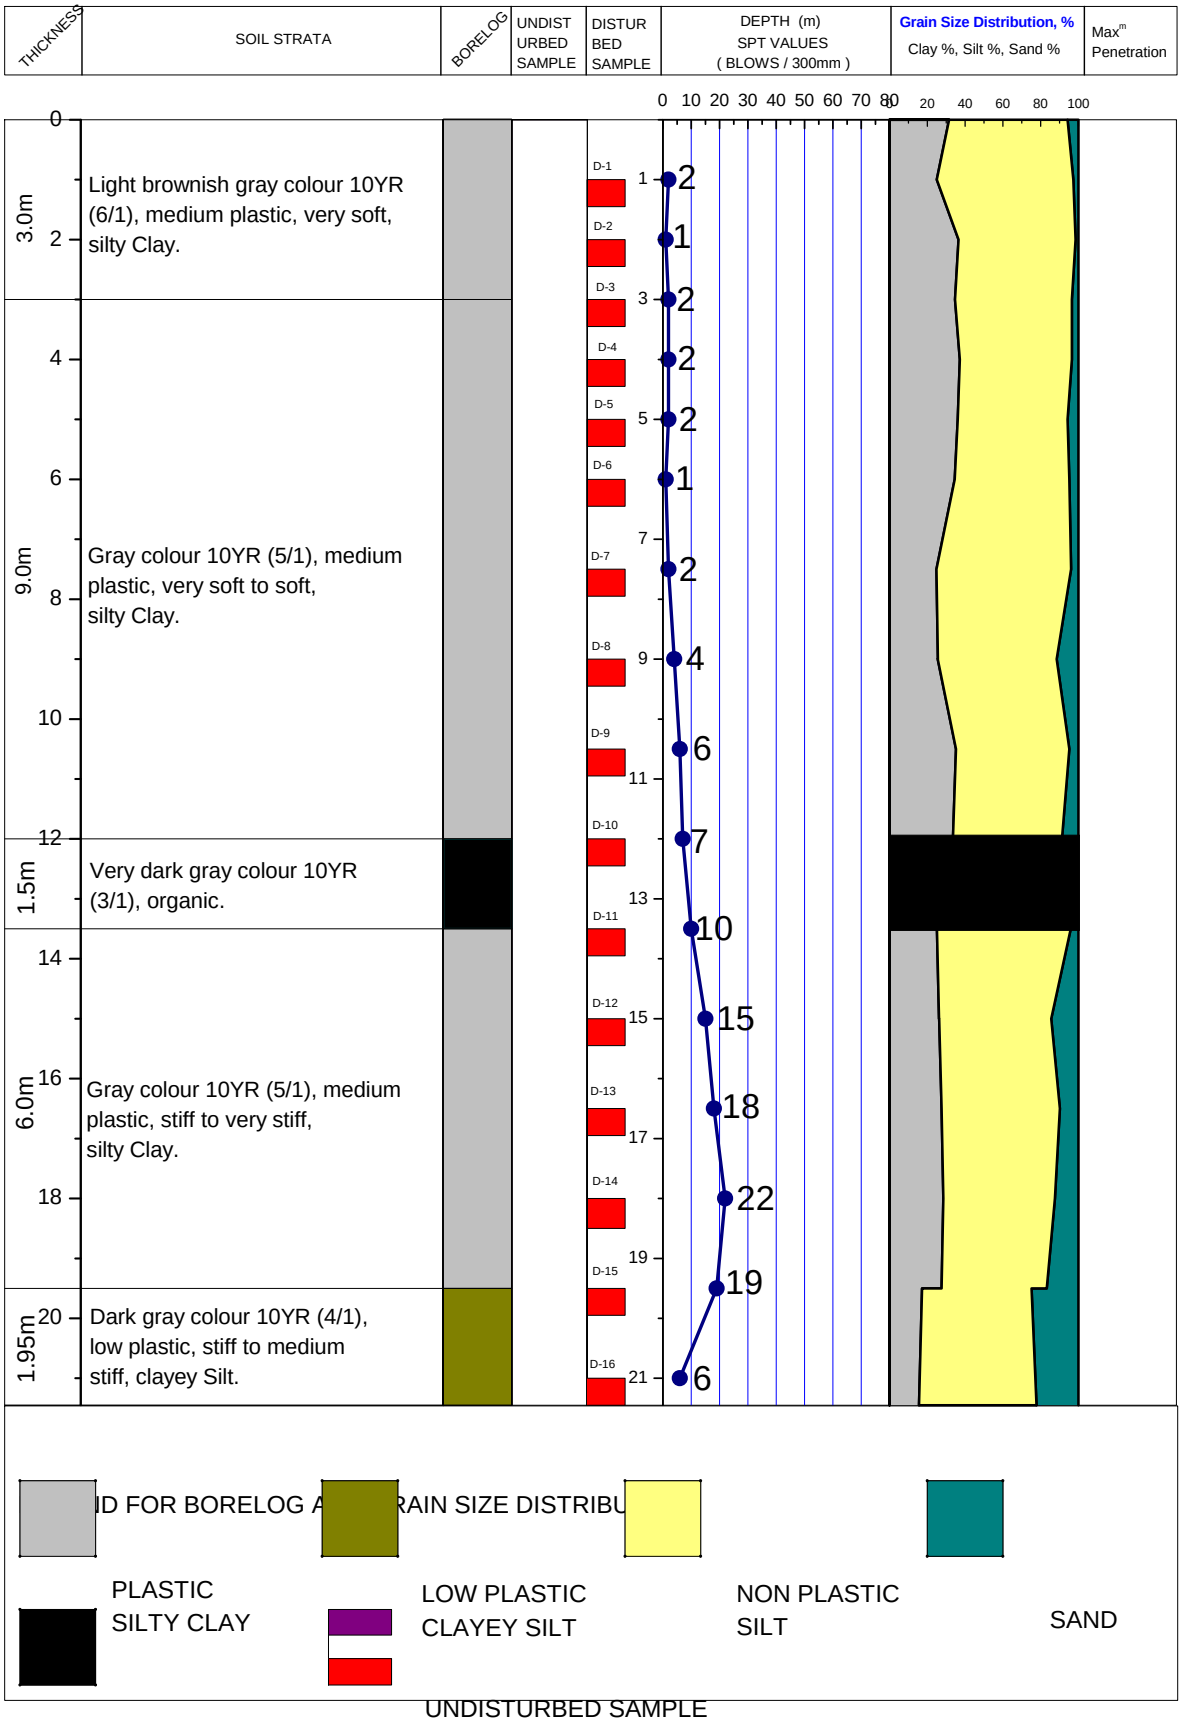

N- BLOWS DELIVERED PER FOOT BY A 140 LB HAMMER FALLING 30 INCHES

MAX^{m} PENETRATION= 50 BLOWS

AFTER 50 BLOWS PENETRATION DEPTH WERE MEASURED