A2 PROSOIL	BOREHOLE NO: BH-1	
	LOCATION : Comilla Railway Station, Comilla.	
PROJECT : Telecommunication Tower	DEPTH OF BORING : 20.0m	R. L.: 0.0m from Road Level
CLIENT : GrameenPhone Ltd.	DATE OF BORING : 5-06-2004	G. W. T : 0.31m below from E. G. L.

THICKNESS	SOIL STRATA	BORELOG	SAMPLE	DEPTH (m)	SPT VALUES (BLOWS / 300mm)	Grain Size Distribution, % Clay %, Silt %, Sand %	Max^{m} Penetration

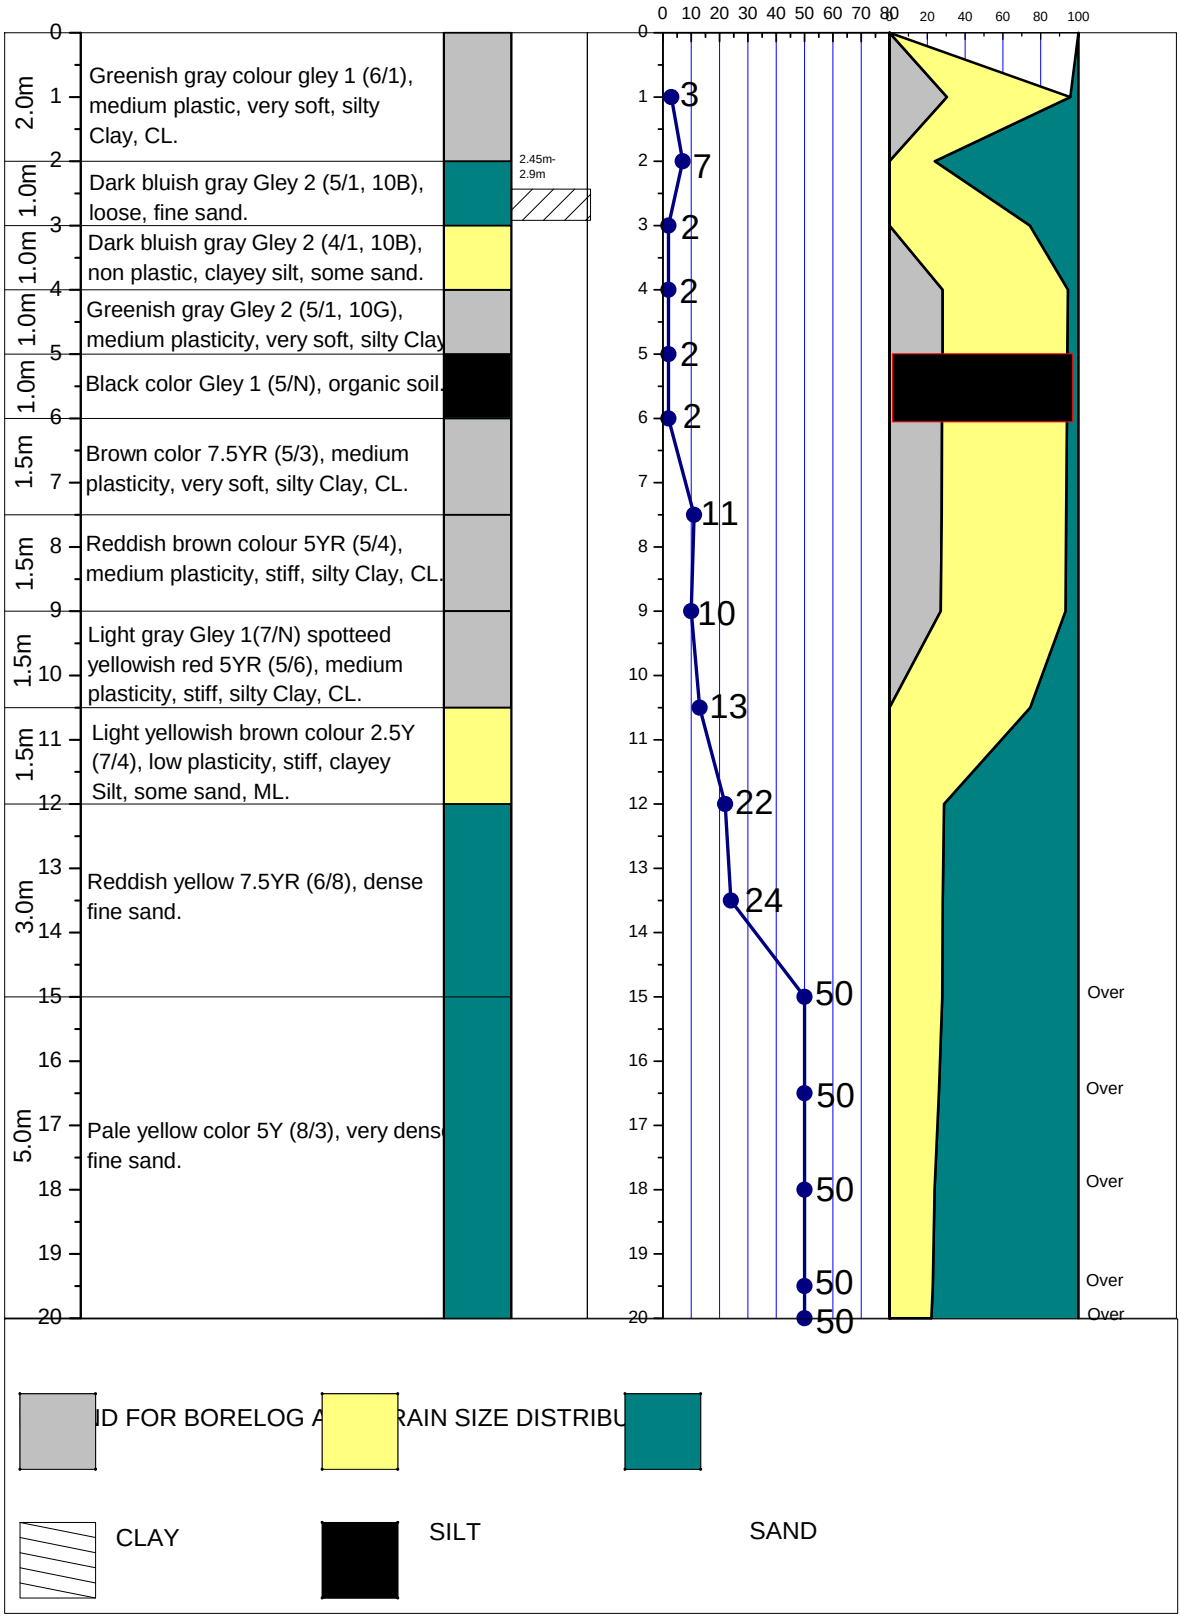

UNDISTURBED ORGANIC

N- BLOWS DELIVERED PER FOOT BY A 140 LB HAMMER FALLING 30 INCHES

MAX^{m} PENETRATION= 50 BLOWS

AFTER 50 BLOWS PENETRATION DEPTH WERE MEASURED