A2	PROSOIL	BOREHOLE NO: BH-1	
		LOCATION: Amlabo, Vulta, Rupganj, Narayanganj.	
PROJECT : Telecommunication Tower.		DEPTH OF BORING : 36.0m	R. L.: 3.05m below from Road Level.
CLIENT : AXIATA (Bangladesh) Ltd.		DATE OF BORING: 25-02-2011.	G. W. T : 3.96m below from E. G. L.

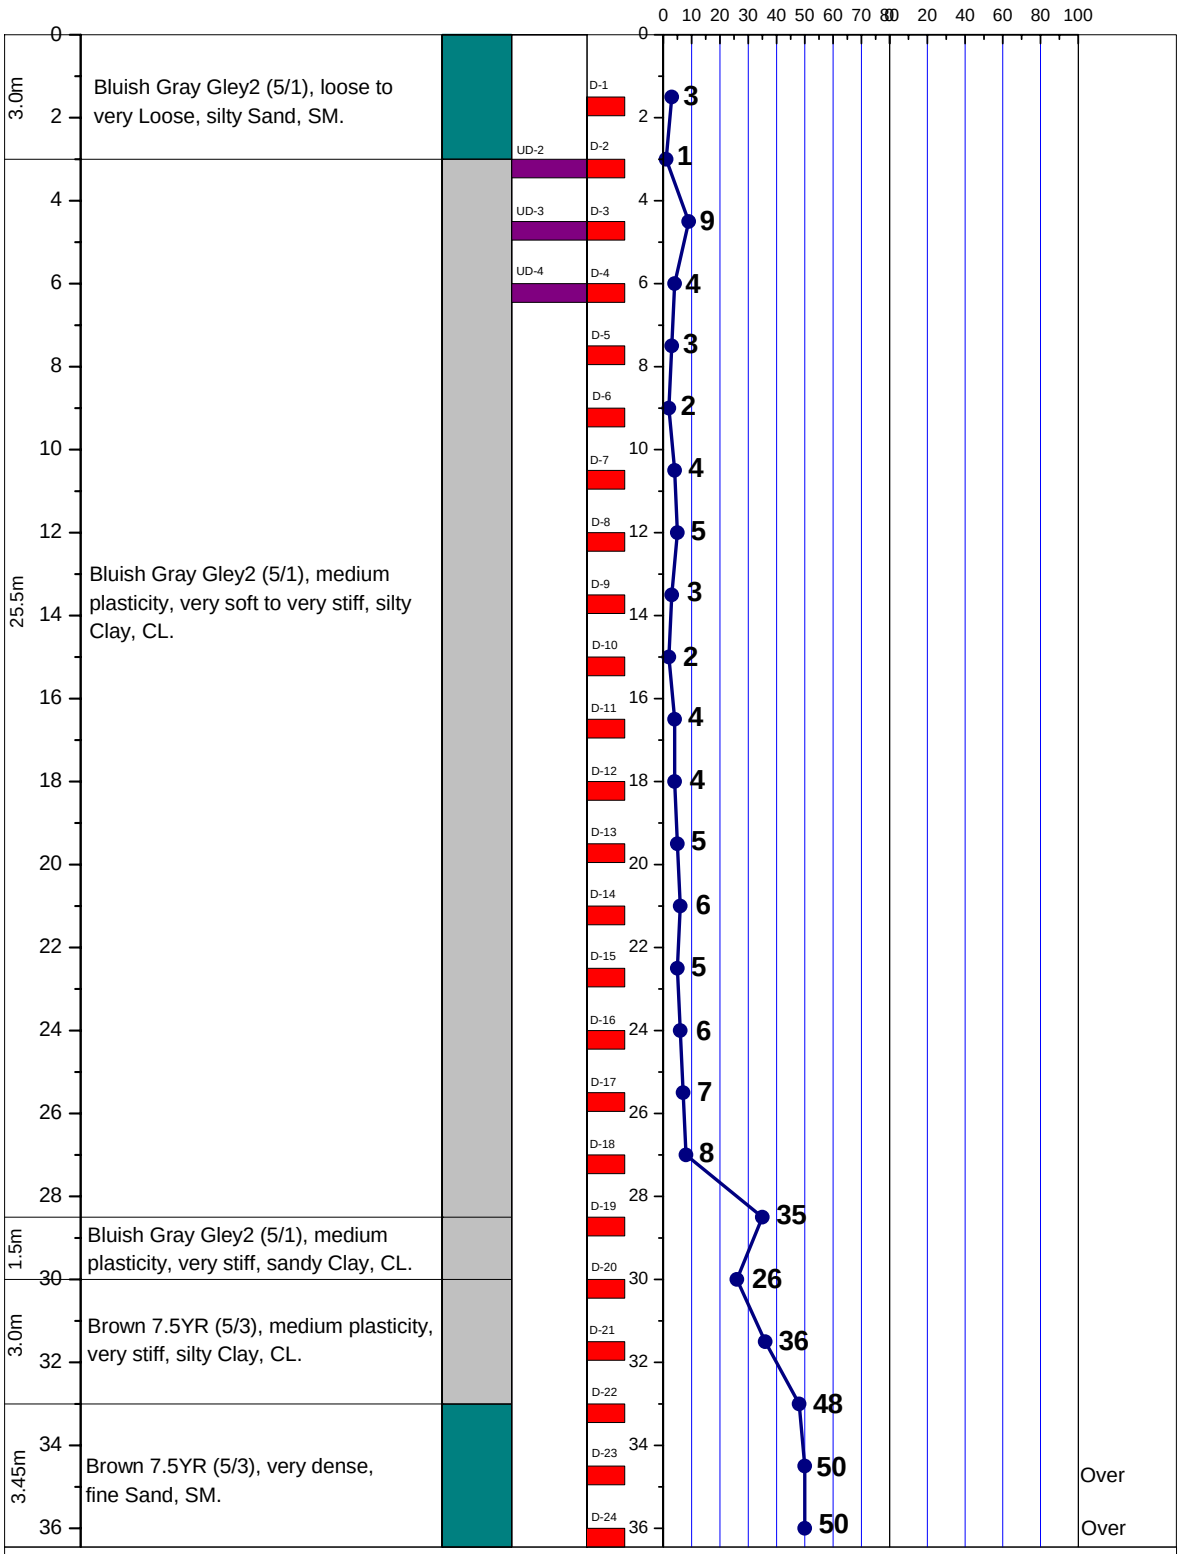

LEGEND FOR BORELOG AND GRAIN SIZE DISTRIBUTION (BASED ON 'ASTM CLASSIFICATION D-2487')

PLASTIC CLAY	SILT	PEAT/HIGHLY ORGANIC SOIL	UNDISTURBED SAMPLE
MICACEOUS FINE SAND/SILT	SAND	SHALE	DISTURBED SAMPLE

N- BLOWS DELIVERED PER FOOT BY A 140 LB HAMMER FALLING 30 INCHES

MAX^{m} PENETRATION= 50 BLOWS. AFTER 50 BLOWS PENETRATION DEPTH WERE MEASURED