A2	PROSOIL	BOREHOLE NO: BH-1	
		LOCATION : 72nd km Chainage 71+200 on Charkhai-Sheola-Beanibazar -Baroigram Road, Sylhet.	
PROJECT : Proposed Bridge At 72nd km.		DEPTH OF BORING : 42.0m	Chainage: 71+200 R. L. : 10.88
CLIENT : Road Division, Sylhet.		DATE OF BORING : 21-12-2010.	G. W. T : 0.61m below from E.G.L.

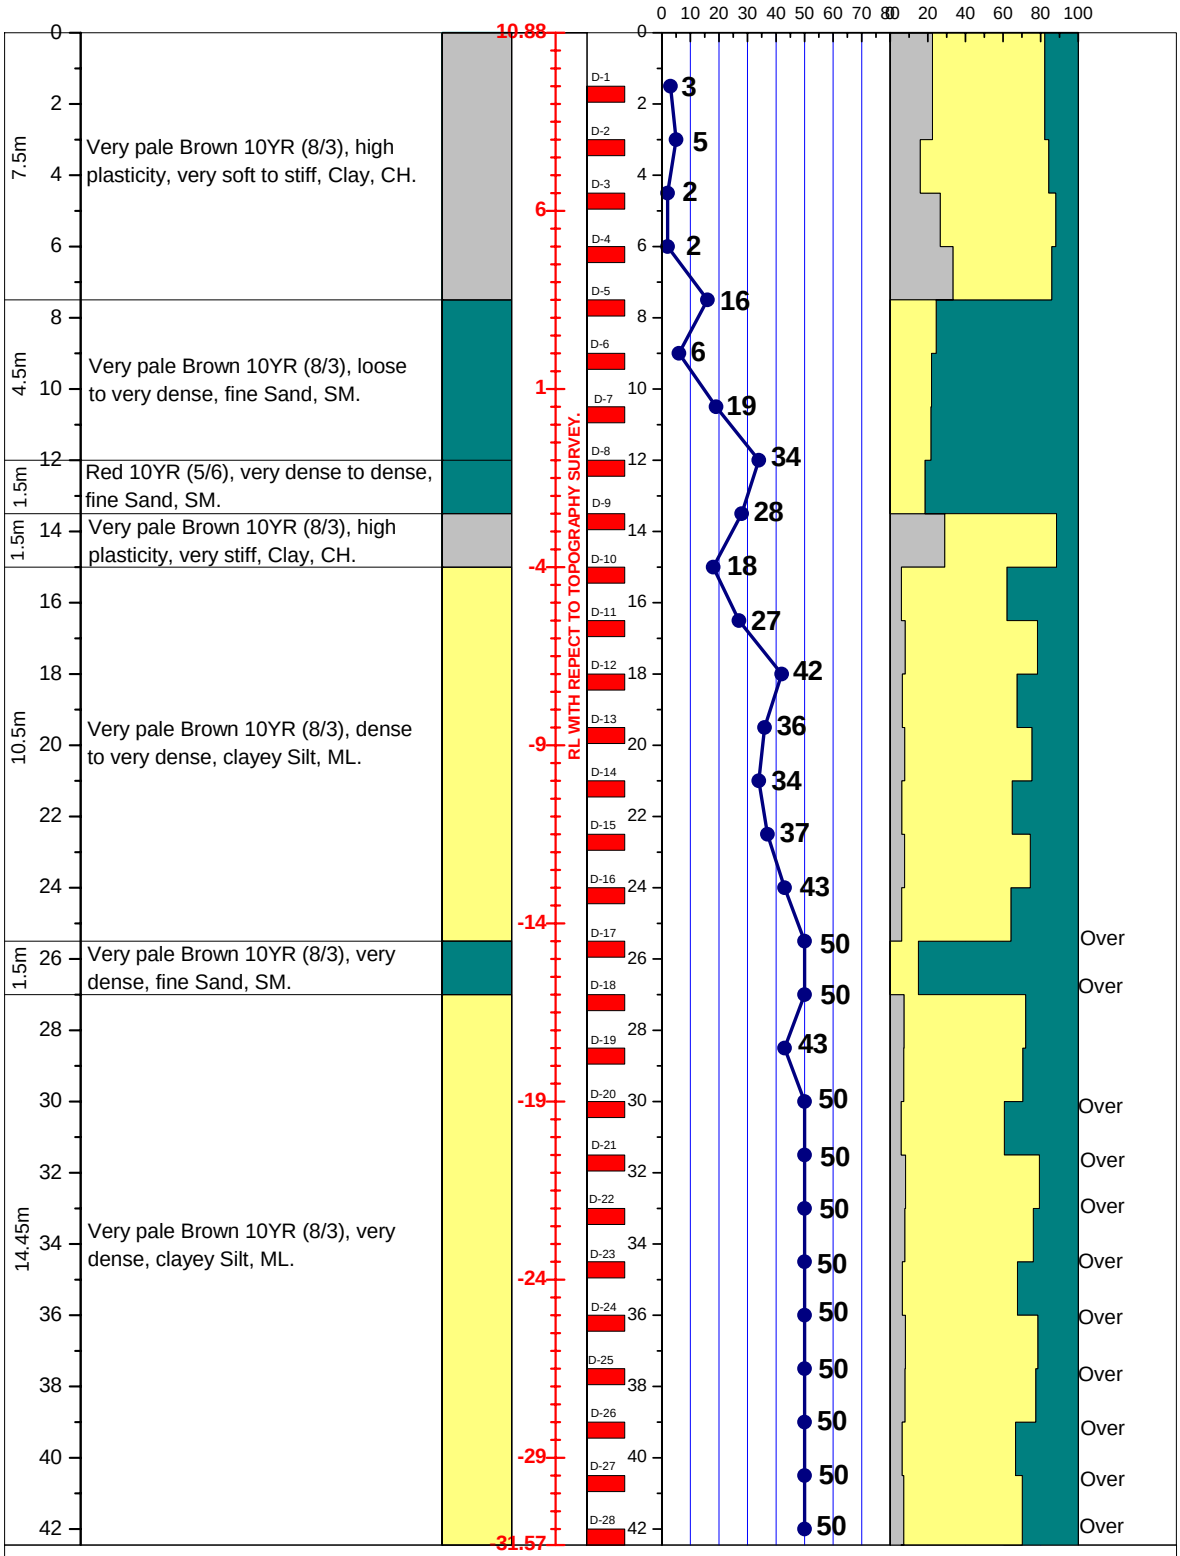

LEGEND FOR BORELOG AND GRAIN SIZE DISTRIBUTION (BASED ON 'ASTM CLASSIFICATION D-2487')

PLASTIC CLAY	SILT	PEAT/HIGHLY ORGANIC SOIL	UNDISTURBED SAMPLE
MICACEOUS FINE SAND/SILT	SAND	SHALE	DISTURBED SAMPLE

N- BLOWS DELIVERED PER FOOT BY A 140 LB HAMMER FALLING 30 INCHES

MAX^m PENETRATION= 50 BLOWS. AFTER 50 BLOWS PENETRATION DEPTH WERE MEASURED