A2	PROSOIL	BOREHOLE NO: BH-2	
		LOCATION : House #32, Road #14/A, Dhanmondi R/A, Dhaka.	
PROJECT : The Grand Residence.		DEPTH OF BORING: 9.0m	R. L.: On Road Level.
CLIENT : Building Technology & Ideas Ltd.		DATE OF BORING: 24-07-2010.	G. W. T : 1.52m below from E.G.L.

THICKNESS	SOIL STRATA	BORELOG	UNDISTURBED SAMPLE	DISTURBED SAMPLE	DEPTH (m) SPT VALUES (BLOWS / 300mm)	Grain Size Distribution, % Clay %, Silt %, Sand %	Max^m Penetration
2.0m	Grayish Brown 10YR (5/2), medium plasticity, very soft, silty Clay, CL.		UD-1	D-1	1		
			UD-2	D-2	1		
4.0m	Bluish Gray Gley2 (5/1), medium plasticity, very soft to medium stiff, silty Clay, CL.		UD-3	D-3	1		
			UD-4	D-4	7		
				D-5	8		
2.0m	Bluish Gray Gley2 (5/1), loose to dense, Silt, ML.			D-6	6		
				D-7	10		
1.45m	Light yellowish Brown 10YR (6/4), dense to very dense, fine Sand, SM.			D-8	20		
				D-9	18		

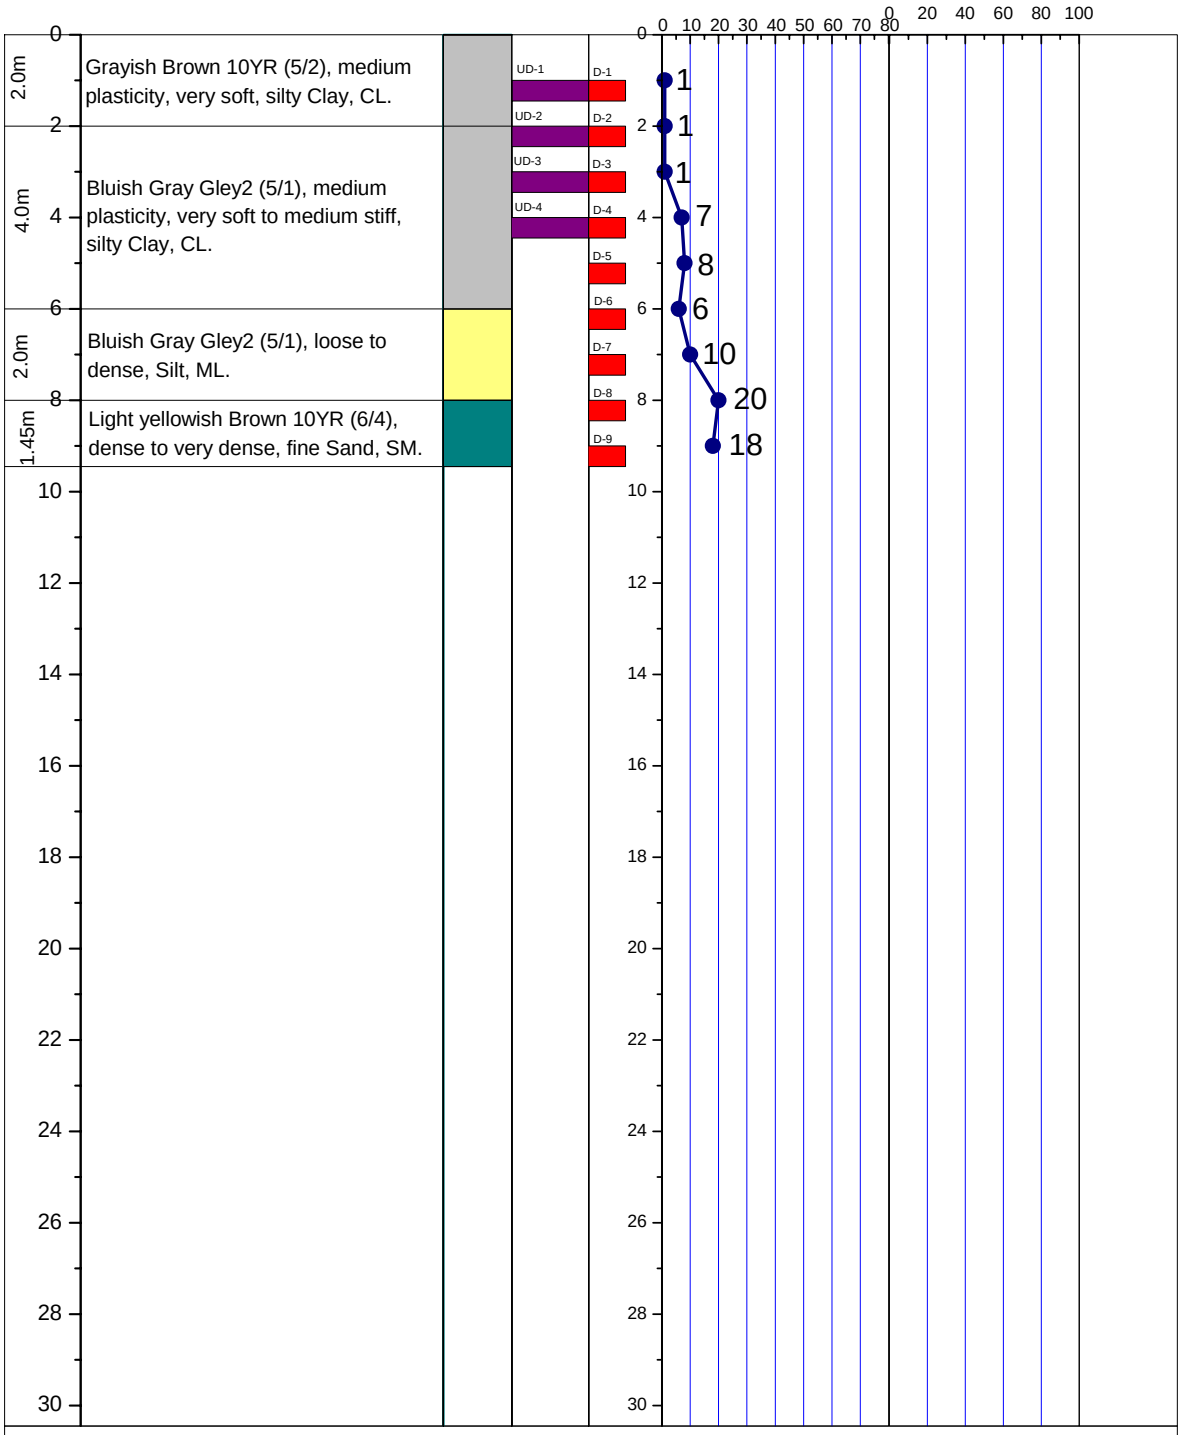

LEGEND FOR BORELOG AND GRAIN SIZE DISTRIBUTION (BASED ON 'ASTM CLASSIFICATION D-2487')

PLASTIC CLAY | SAND | SILT | SHALE

PEAT/HIGHLY ORGANIC SOIL | MICACEOUS FINE SAND/SILT | UNDISTURBED SAMPLE | DISTURBED SAMPLE

N- BLOWS DELIVERED PER FOOT BY A 140 LB HAMMER FALLING 30 INCHES

MAX^m PENETRATION= 50 BLOWS

AFTER 50 BLOWS PENETRATION DEPTH WERE MEASURED