A2	PROSOIL	BOREHOLE NO: BH-1	
		LOCATION : Bridge At Fatehpur Over River Of Niamotpur-Tahirpur Road, Sunamgonj.	
PROJECT : Proposed 134.608m (3X48.78m) Long P.C. Girder Bridge.		DEPTH OF BORING : 70.5m	**Chainage: 18+997** **R. L. : 3.27**
CLIENT : BUET.		DATE OF BORING : 20-04-2012.	G. W. T : 10.67m above from E.G.L.

THICKNESS	SOIL STRATA	BORELOG	RL	DISTURBED SAMPLE	DEPTH (m) SPT VALUES (BLOWS / 300mm)	Grain Size Distribution, % Clay %, Silt %, Sand %	Max^{m} Penetration

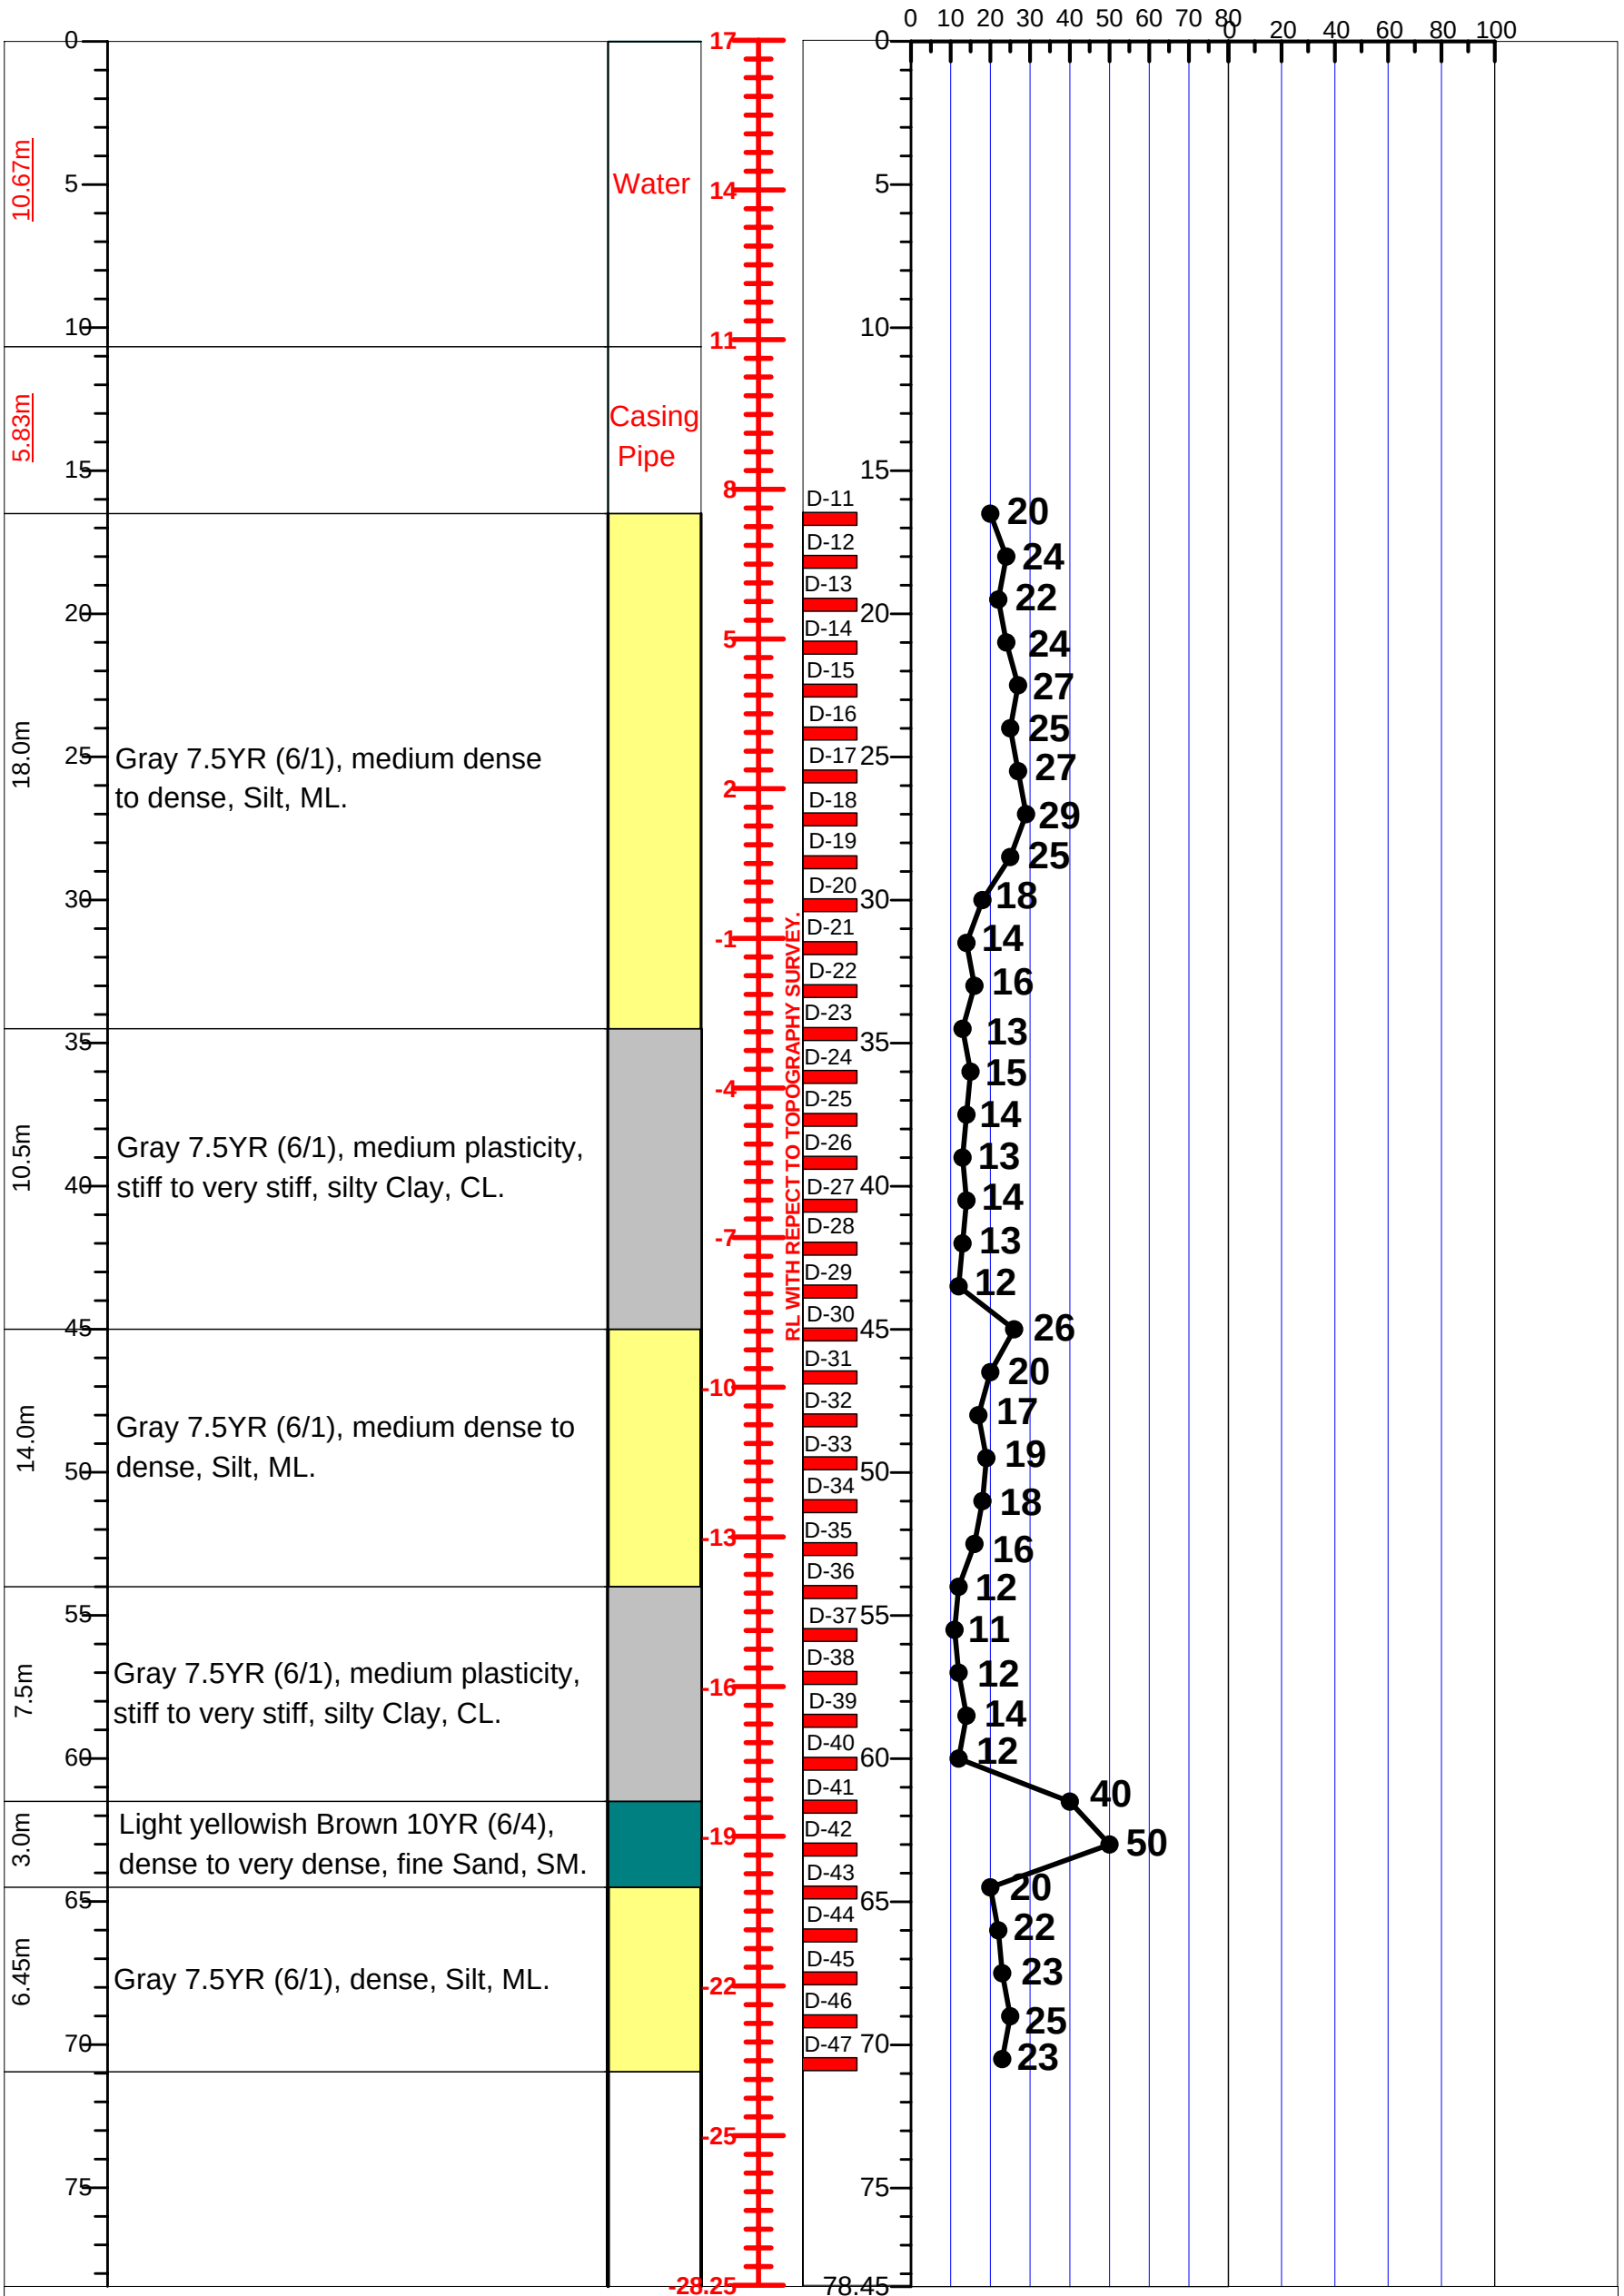

LEGEND FOR BORELOG AND GRAIN SIZE DISTRIBUTION (BASED ON 'ASTM CLASSIFICATION D-2487')

PLASTIC CLAY	SILT	PEAT/HIGHLY ORGANIC SOIL	UNDISTURBED SAMPLE
MICACEOUS FINE SAND/SILT	SAND	SHALE	DISTURBED SAMPLE

N- BLOWS DELIVERED PER FOOT BY A 140 LB HAMMER FALLING 30 INCHES

MAX^{m} PENETRATION= 50 BLOWS. AFTER 50 BLOWS PENETRATION DEPTH WERE MEASURED

A2	PROSOIL	BOREHOLE NO: BH-2	
		LOCATION : Bridge At Fatehpur Over River Of Niamotpur-Tahirpur Road, Sunamgonj.	
PROJECT : Proposed 134.608m (3X48.78m) Long P.C. Girder Bridge.		DEPTH OF BORING : 78.0m	**Chainage: 18+997** **R. L. : 3.27**
CLIENT : BUET.		DATE OF BORING : 16-04-2012.	G. W. T : 16.77m above from E.G.L.

THICKNESS	SOIL STRATA	BORELOG	RL	DISTURBED SAMPLE	DEPTH (m) SPT VALUES (BLOWS / 300mm)	Grain Size Distribution, % Clay %, Silt %, Sand %	Max^{m} Penetration

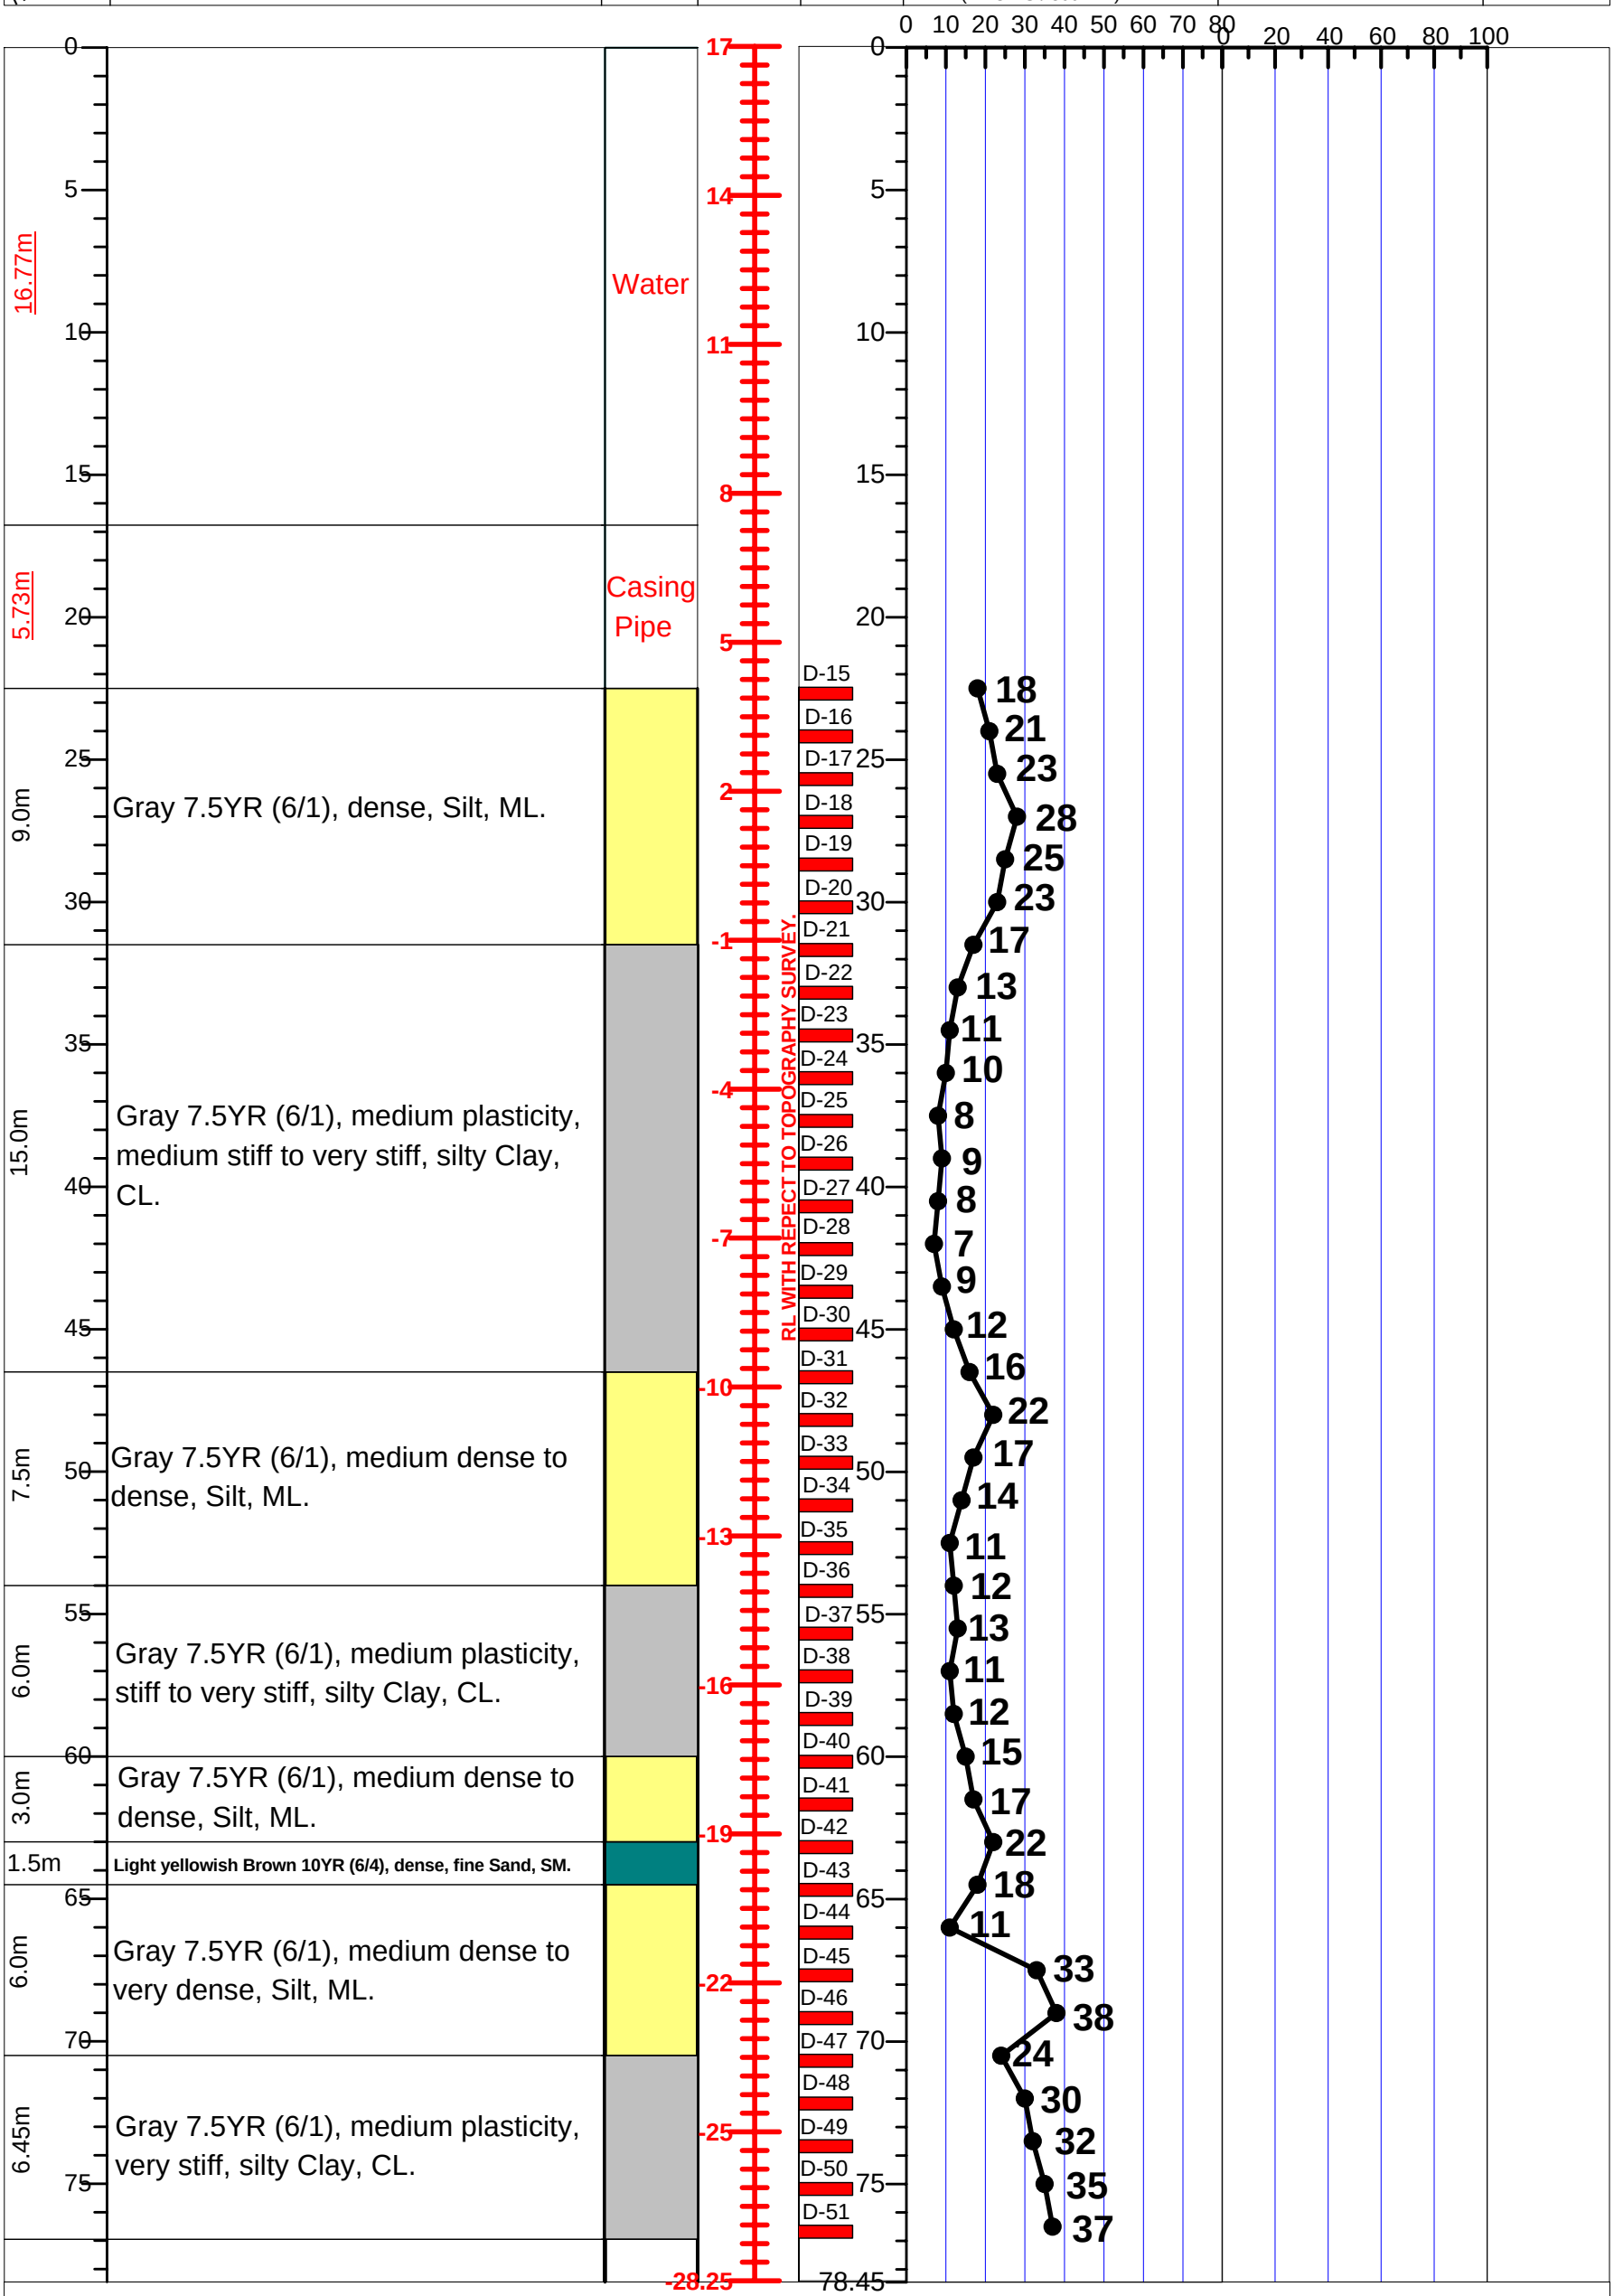

LEGEND FOR BORELOG AND GRAIN SIZE DISTRIBUTION (BASED ON 'ASTM CLASSIFICATION D-2487')

PLASTIC CLAY	SILT	PEAT/HIGHLY ORGANIC SOIL	UNDISTURBED SAMPLE
MICACEOUS FINE SAND/SILT	SAND	SHALE	DISTURBED SAMPLE

N- BLOWS DELIVERED PER FOOT BY A 140 LB HAMMER FALLING 30 INCHES

MAX^{m} PENETRATION= 50 BLOWS. AFTER 50 BLOWS PENETRATION DEPTH WERE MEASURED