
A2 PROSOIL	BOREHOLE NO: BH-1	
	LOCATION : Chainage 5th km on Airport Gate-Bada Ghat Road, Sylhet.	
PROJECT : Proposed Puti Khal Bridge.	DEPTH OF BORING : 40.95m	**Chainage: 5+064** **R. L. : 7.7**
CLIENT : Road Division, Sylhet.	DATE OF BORING : 13-02-2010.	G. W. T : 6.5m below from E.G.L.

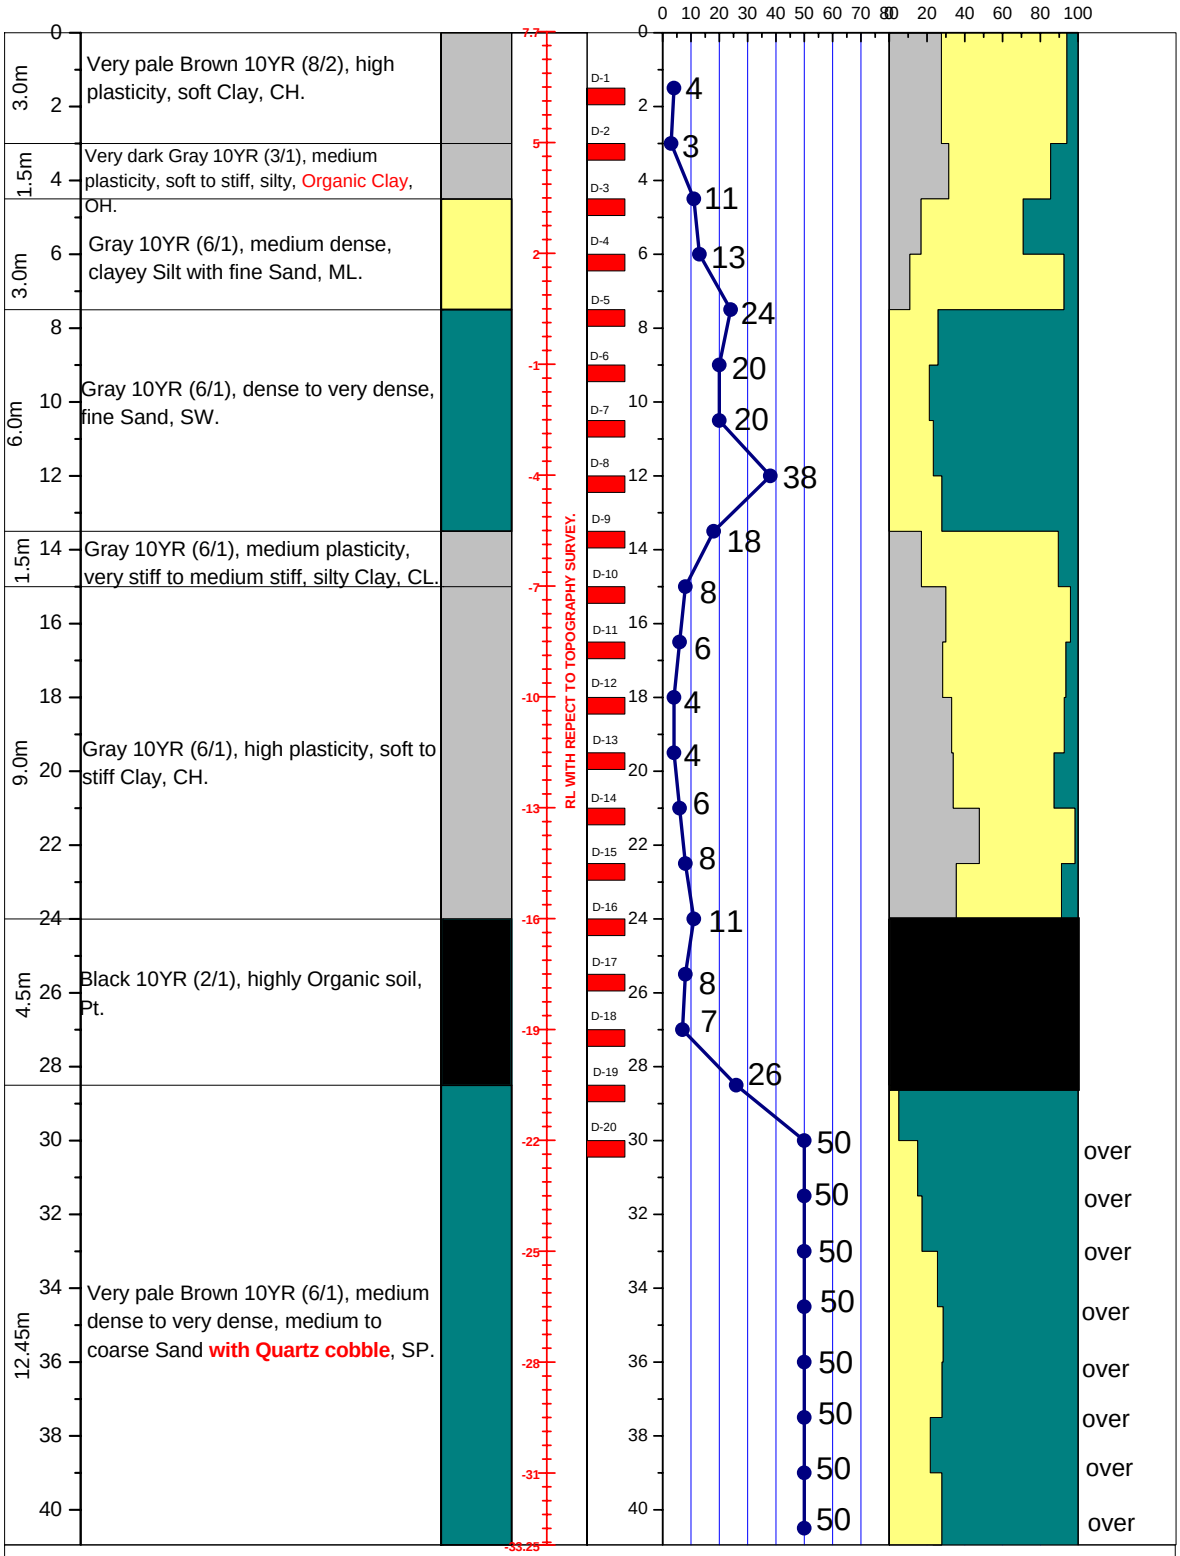

LEGEND FOR BORELOG AND GRAIN SIZE DISTRIBUTION (BASED ON 'ASTM CLASSIFICATION D-2487')

PLASTIC CLAY | SILT | PEAT/HIGHLY ORGANIC SOIL | DISTURBED SAMPLE

MICACEOUS FINE SAND/SILT | SAND | SHALE | UNDISTURBED SAMPLE

N- BLOWS DELIVERED PER FOOT BY A 140 LB HAMMER FALLING 30 INCHES

MAX^m PENETRATION= 50 BLOWS. AFTER 50 BLOWS PENETRATION DEPTH WERE MEASURED