A2	PROSOIL	BOREHOLE NO: BH-1
		LOCATION: VILL: KAPNA MERUAKHOLA, P. O: ROTARGOAN, P. S: BISHWAMBARPUR, DIST: SUNAMGANJ.
PROJECT : Telecommunication Tower.		DEPTH OF BORING: 21.0m
CLIENT : AXIATA (Bangladesh) Ltd.		DATE OF BORING: 06-02-2015.

R. L.: 0.15m above from Road Level.
B. W. T : 0.15m below from E. G. L.

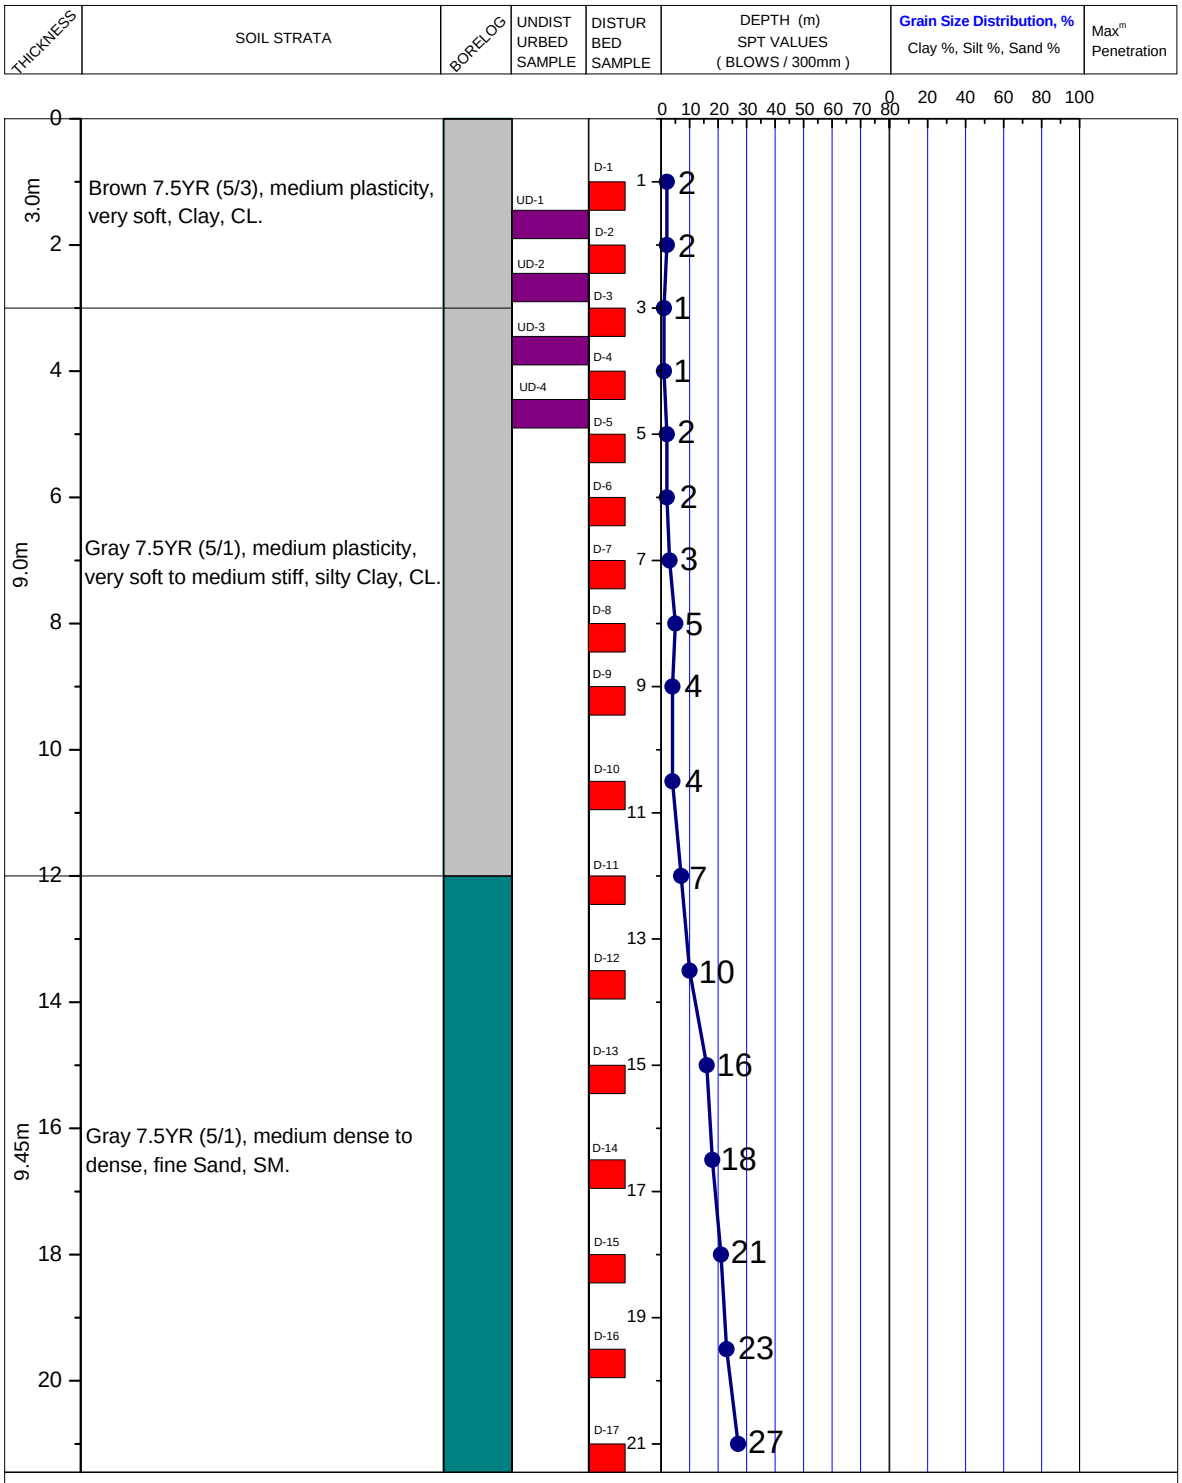

LEGEND FOR BORELOG AND GRAIN SIZE DISTRIBUTION (BASED ON 'ASTM CLASSIFICATION D-2487')

PLASTIC CLAY | SAND | SILT | SHALE

PEAT/HIGHLY ORGANIC SOIL | MICACEOUS FINE SAND/SILT | UNDISTURBED SAMPLE | DISTURBED SAMPLE

N- BLOWS DELIVERED PER FOOT BY A 140 LB HAMMER FALLING 30 INCHES

MAX^m PENETRATION= 50 BLOWS

AFTER 50 BLOWS PENETRATION DEPTH WERE MEASURED

XB

PROSOIL FOUNDATION CONSULTANT DHAKA-1205 68/B, INDIRA ROAD

Md. Shamsul Islam

(Engr. Md. Shamsul Islam)
B. Sc. Engg. (Civil, BUET),
M. Engg. (Geotech), MCSD, FIEB, CCPE
Chief Executive
Prosoil Foundation Consultant