A2	PROSOIL	BOREHOLE NO: BH-1	
		LOCATION : Chainage 1+400Km of Jatrabari-Demra-Tarabo Kachpur Road (Tarabo Kachpur Portion), Narayangonj.	
PROJECT : Proposed Bridge At 2nd km Gap No (2/1).		DEPTH OF BORING : 42.0m	Chainage: 1+409 R. L. : 2.6
CLIENT : Road Division, Narayangonj.		DATE OF BORING : 11-04-2011.	G. W. T : 4.57m below from E.G.L.

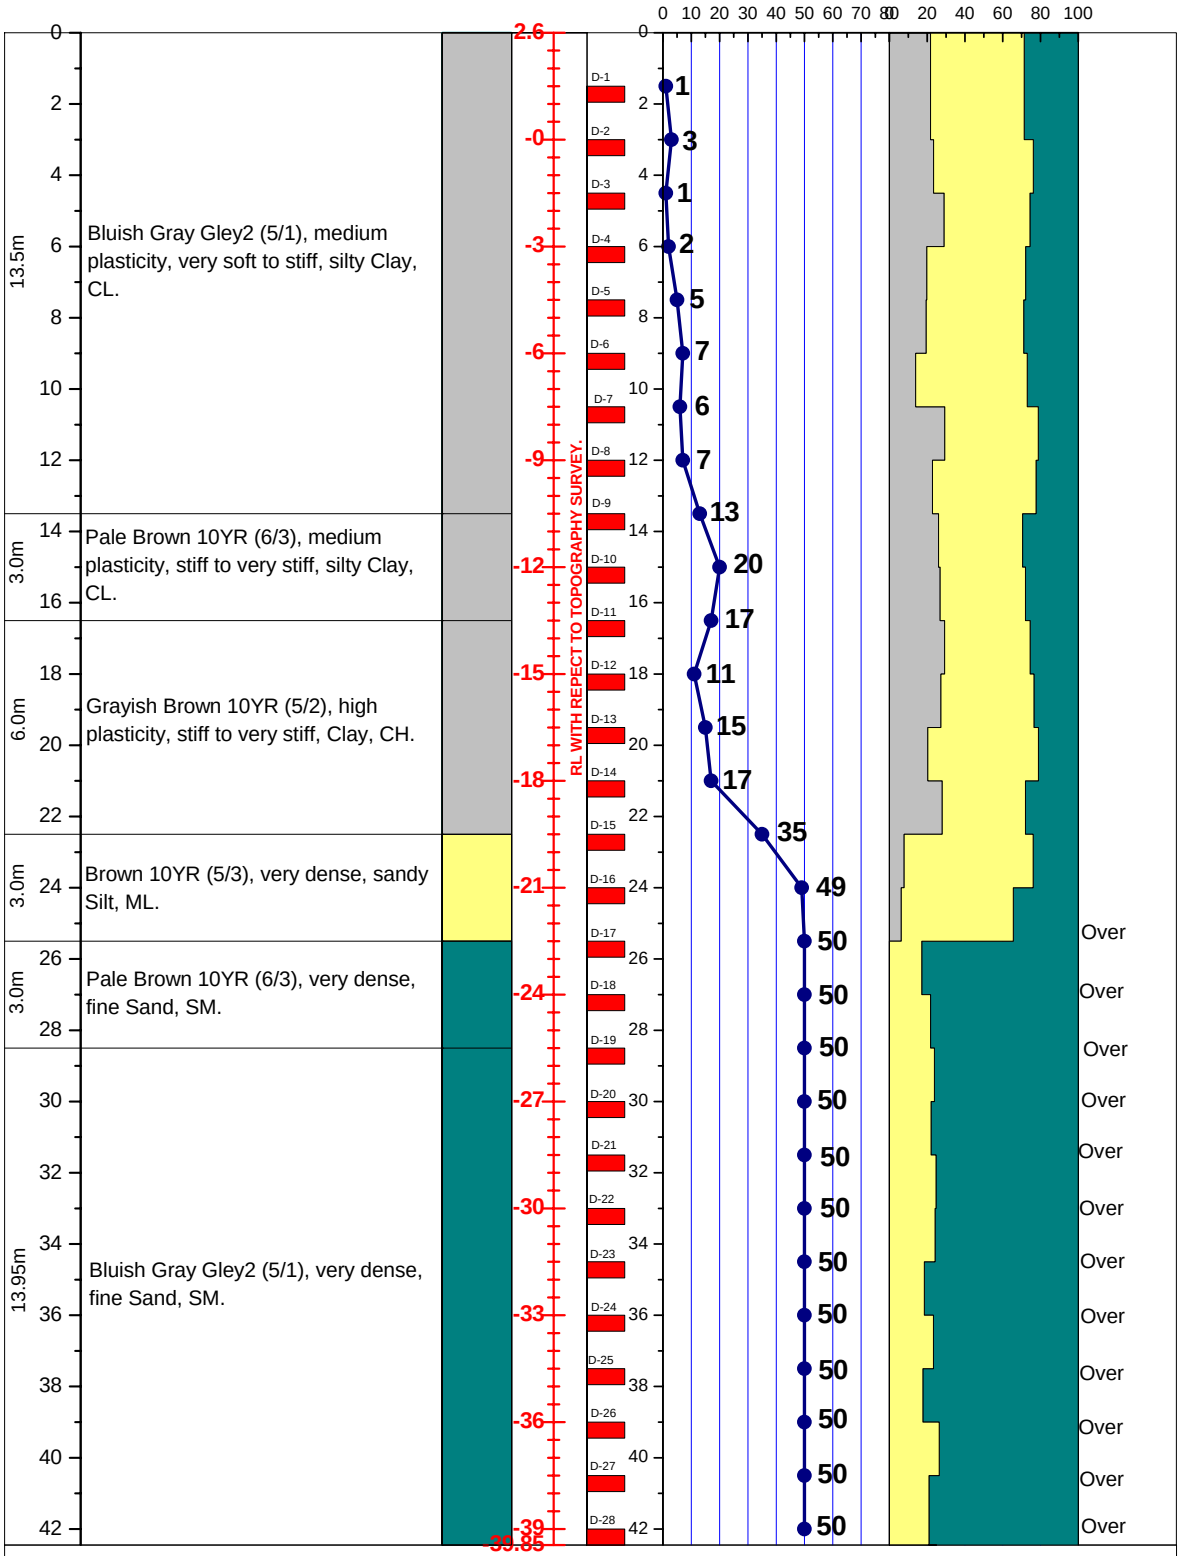

LEGEND FOR BORELOG AND GRAIN SIZE DISTRIBUTION (BASED ON 'ASTM CLASSIFICATION D-2487')

PLASTIC CLAY	SILT	PEAT/HIGHLY ORGANIC SOIL	UNDISTURBED SAMPLE
MICACEOUS FINE SAND/SILT	SAND	SHALE	DISTURBED SAMPLE

N- BLOWS DELIVERED PER FOOT BY A 140 LB HAMMER FALLING 30 INCHES

MAX^m PENETRATION= 50 BLOWS. AFTER 50 BLOWS PENETRATION DEPTH WERE MEASURED