A2 PROSOIL	BOREHOLE NO: BH-1	
	LOCATION : Sheowratoli Bazar- Massimnagar Fery Ghat Road, Narsingdhi.	
PROJECT : Proposed Bridge Over branch of Meghna.	DEPTH OF BORING : 33.0m	Chainage: 27.0m R. L. : 18.03m
CLIENT : Executive Engineer, LGED, Narsingdhi.	DATE OF BORING: 21-07-2012.	G. W. T : 1.83m above from E.G.L.

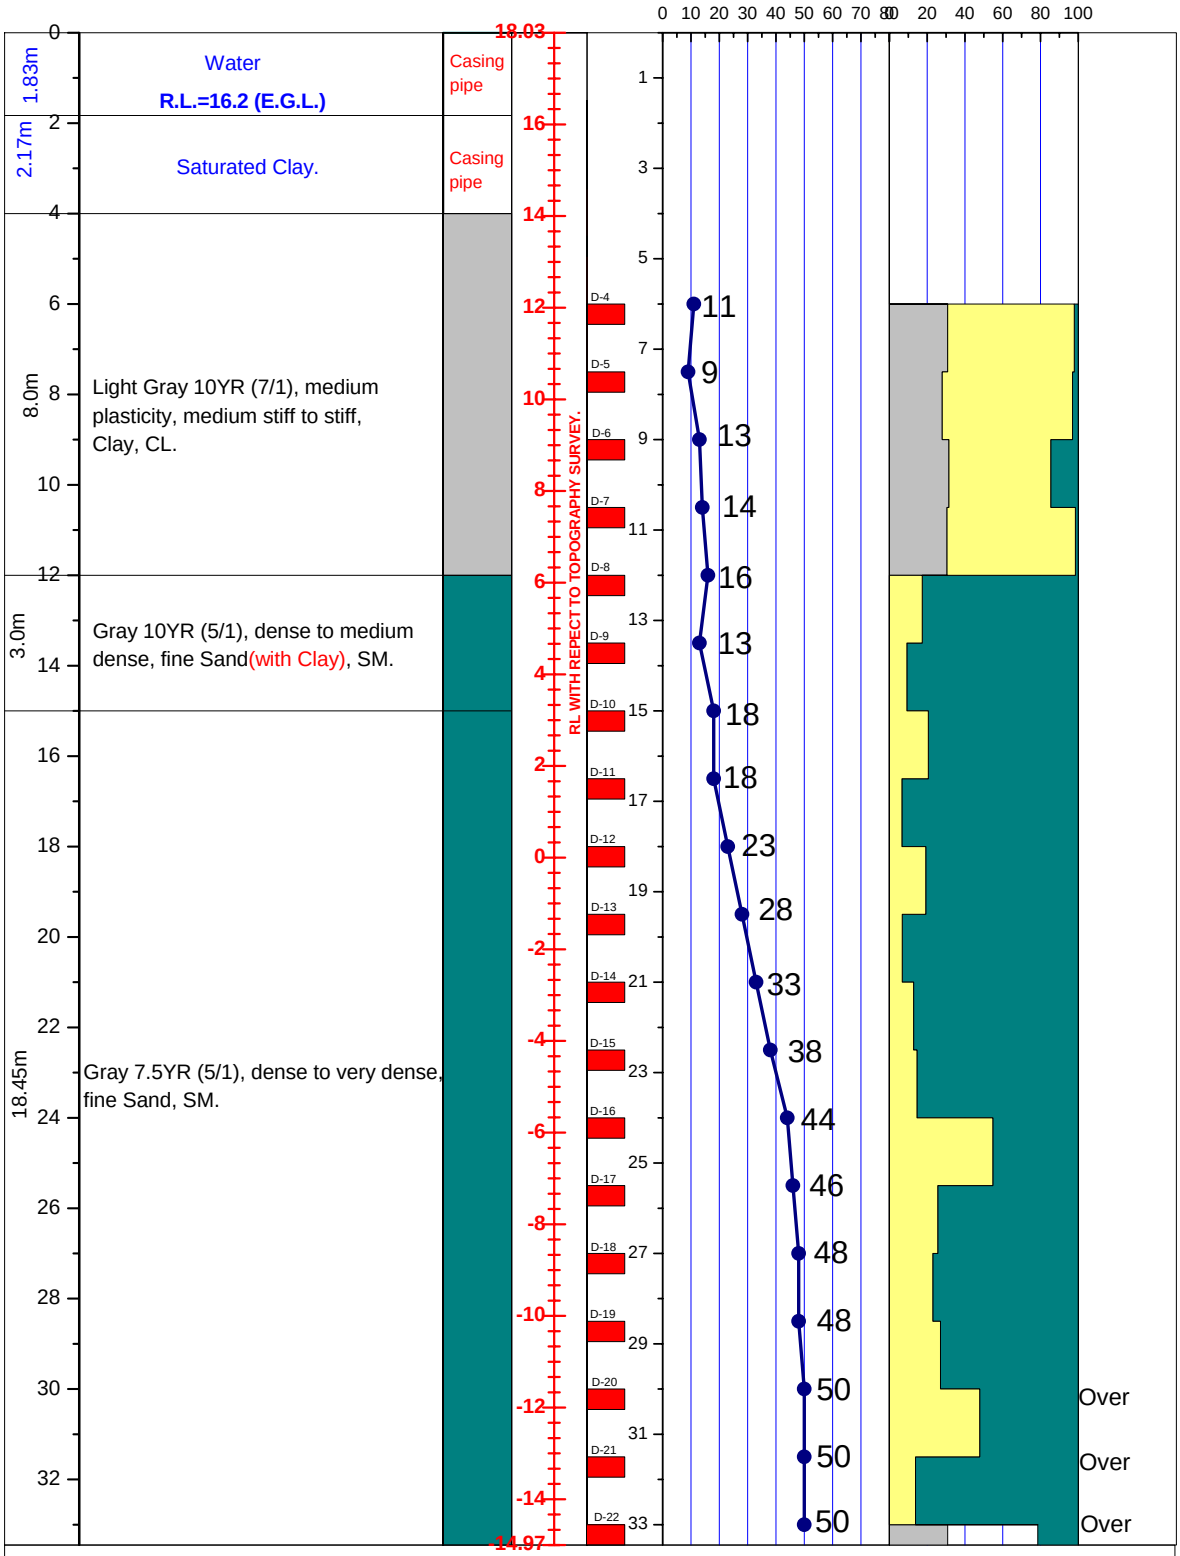

LEGEND FOR BORELOG AND GRAIN SIZE DISTRIBUTION (BASED ON 'ASTM CLASSIFICATION D-2487')

PLASTIC CLAY	SILT	PEAT/HIGHLY ORGANIC SOIL	UNDISTURBED SAMPLE
MICACEOUS FINE SAND/SILT	SAND	SHALE	DISTURBED SAMPLE

N- BLOWS DELIVERED PER FOOT BY A 140 LB HAMMER FALLING 30 INCHES

MAX^m PENETRATION= 50 BLOWS. AFTER 50 BLOWS PENETRATION DEPTH WERE MEASURED