| A2 PROSOIL | BOREHOLE NO: BH-1 | |
|---|---|---|
| | LOCATION : LRP Ch. 0.744 Km (Zindabazar Point) on Sylhet-Salutikor-Companygonj-Bholagonj (Sylhet Town Portion) Road. | |
| PROJECT : Construction of Proposed Bridge. | DEPTH OF BORING : 22.5m | R. L.: Road Level. |
| CLIENT : Road Division, Sylhet. | DATE OF BORING : 18-10-2009. | G. W. T : 3.70m below from E.G.L. |

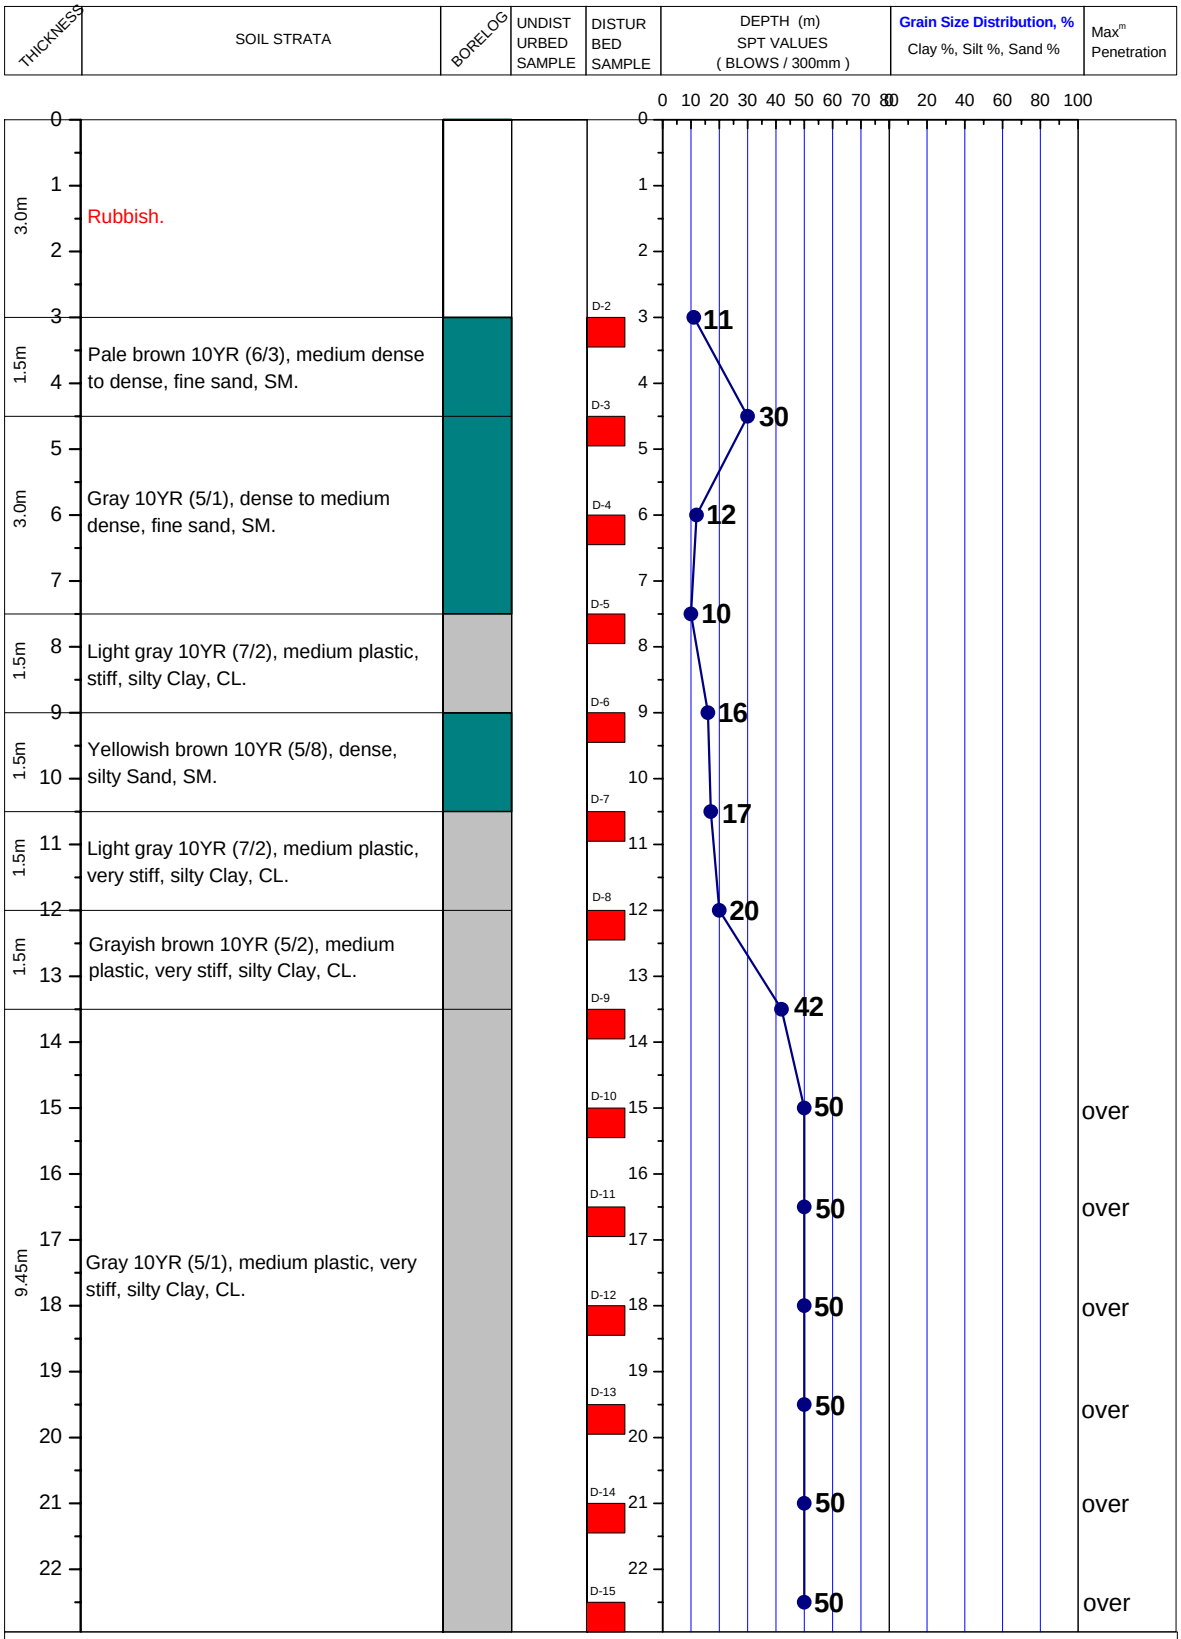


LEGEND FOR BORELOG AND GRAIN SIZE DISTRIBUTION

| | | | |
|---|---|---|---|
| PLASTIC SILTY CLAY | NON PLASTIC SILT | ORGANIC | UNDISTURBED SAMPLE |
| LOW PLASTIC CLAYEY SILT | SAND | SHALE | DISTURBED SAMPLE |

N- BLOWS DELIVERED PER FOOT BY A 140 LB HAMMER FALLING 30 INCHES

MAX$^{m}$ PENETRATION= 50 BLOWS. AFTER 50 BLOWS PENETRATION DEPTH WERE MEASURED