A2 PROSOIL	BOREHOLE NO: BH-1	
	LOCATION : **Chainage 15+246.6 km on Darbost-Kanaight-Shahbag Road, Sylhet.**	
PROJECT : Proposed Bridge at 16th km from Chainage 15+246.6 km to 15+277.6 km.	DEPTH OF BORING : 45.0m	**Chainage: 15+249.6** **R. L. : 8.09**
CLIENT : Road Division, Sylhet.	DATE OF BORING: 23-02-2010.	G. W. T : 1.83m below from E.G.L.

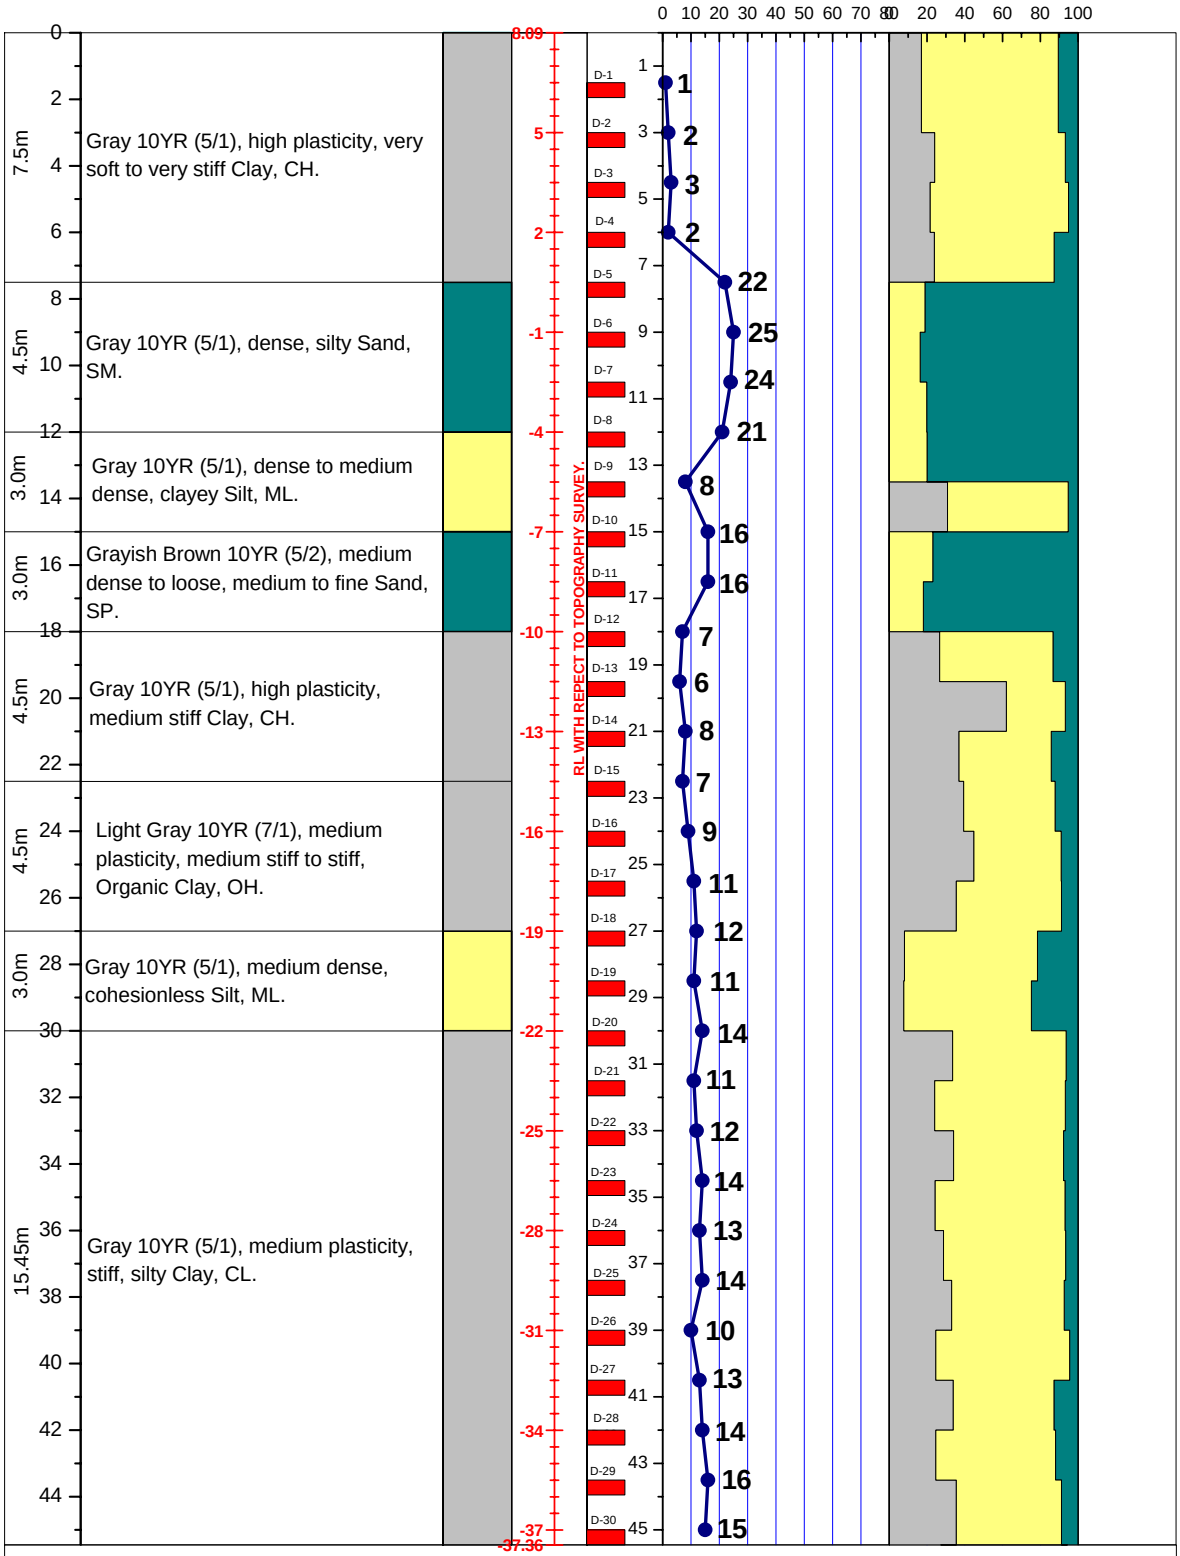

LEGEND FOR BORELOG AND GRAIN SIZE DISTRIBUTION (BASED ON 'ASTM CLASSIFICATION D-2487')

PLASTIC CLAY	SILT	PEAT/HIGHLY ORGANIC SOIL	UNDISTURBED SAMPLE
MICACEOUS FINE SAND/SILT	SAND	SHALE	DISTURBED SAMPLE

N- BLOWS DELIVERED PER FOOT BY A 140 LB HAMMER FALLING 30 INCHES

MAX^m PENETRATION= 50 BLOWS. AFTER 50 BLOWS PENETRATION DEPTH WERE MEASURED