A2	PROSOIL	BOREHOLE NO: BH-1	
		LOCATION : **Chainage 11+600km on Baburhat-Matlab-Pennai Road Chandpur.**	
PROJECT : Proposed Bridge at 12th km (Gap 12/1).		DEPTH OF BORING : 42.0m	**Chainage: 11+600** **R. L. : 4.885**
CLIENT : Road Division, Chandpur.		DATE OF BORING : 18-06-2010.	G. W. T : 3.96m below from E.G.L.

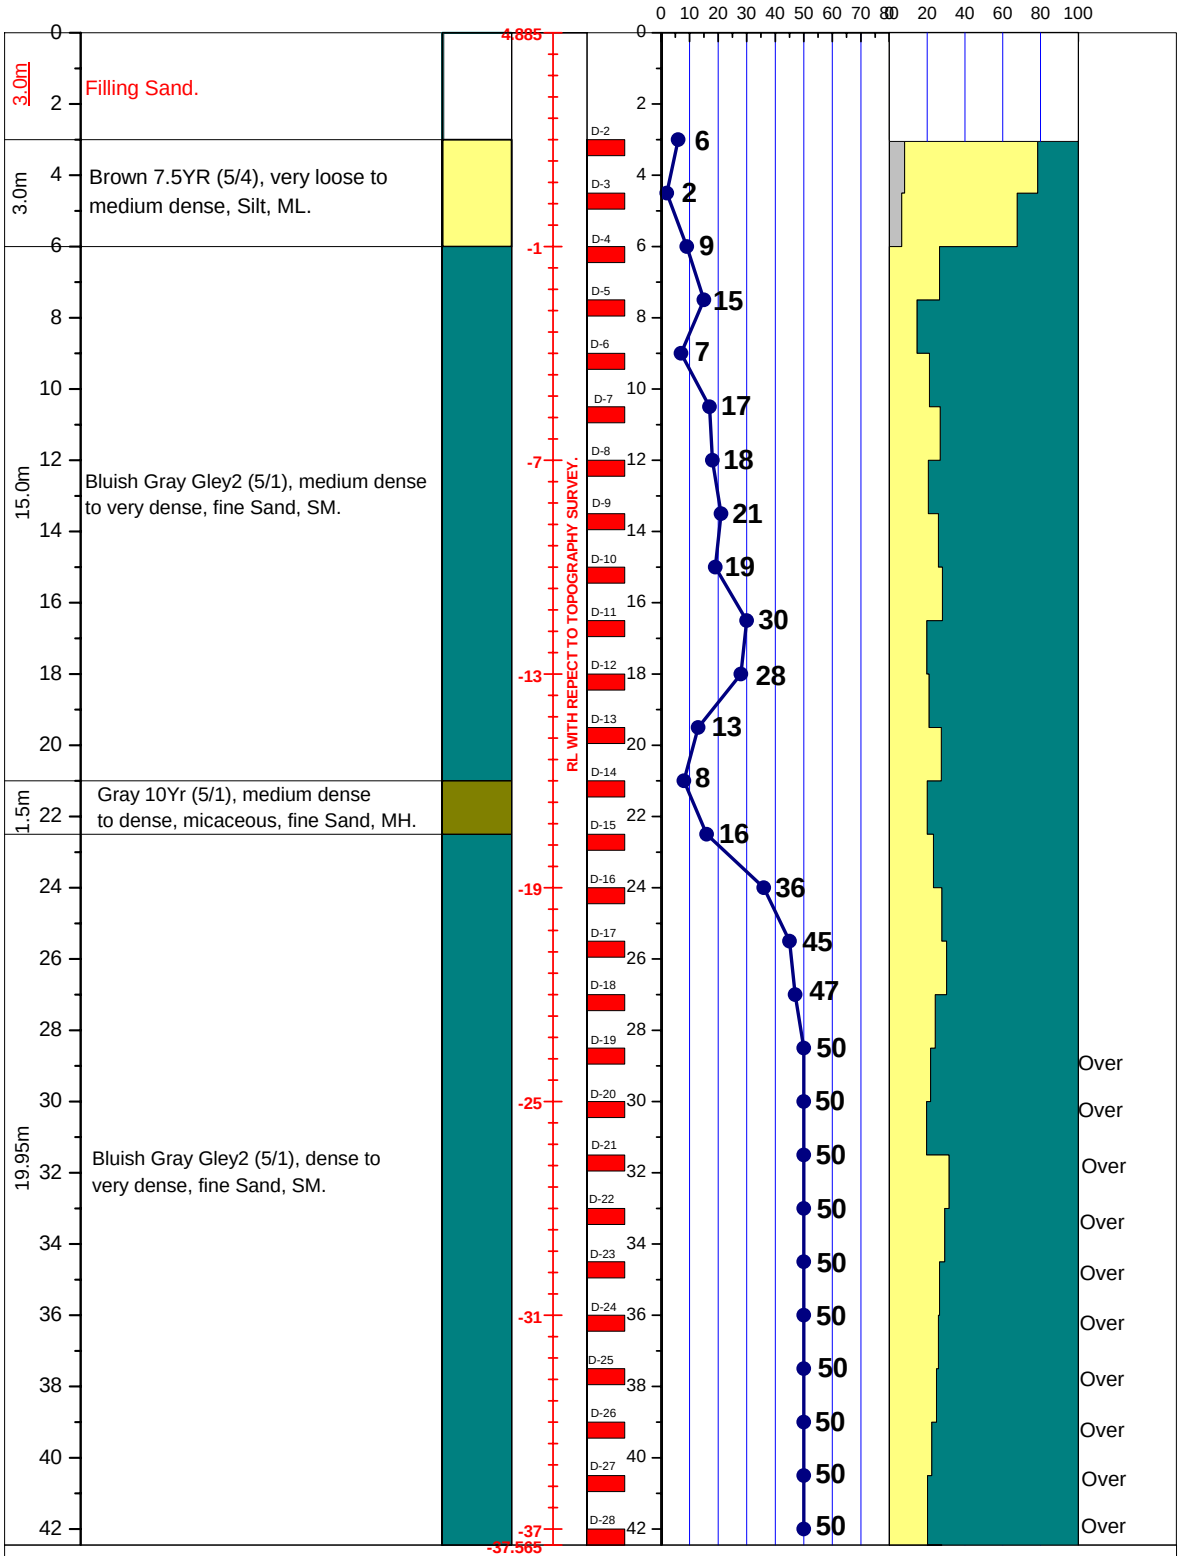

LEGEND FOR BORELOG AND GRAIN SIZE DISTRIBUTION (BASED ON 'ASTM CLASSIFICATION D-2487')

PLASTIC CLAY	SILT	PEAT/HIGHLY ORGANIC SOIL	UNDISTURBED SAMPLE
MICACEOUS FINE SAND/SILT	SAND	SHALE	DISTURBED SAMPLE

N- BLOWS DELIVERED PER FOOT BY A 140 LB HAMMER FALLING 30 INCHES

MAX^m PENETRATION= 50 BLOWS. AFTER 50 BLOWS PENETRATION DEPTH WERE MEASURED