A2 PROSOIL	BOREHOLE NO: BH-1	
	LOCATION : 24th km of Gap no. (24/1) of Sarail-Nasirngar-Lakhai Road.	
PROJECT : Construction of Proposed Bridge.	DEPTH OF BORING : 42.0m	R. L. : 4.12. Chainage: 23+379
CLIENT : Road Division, B.Baria.	DATE OF BORING : 02-11-2010.	G. W. T : 1.22m below from E.G.L.

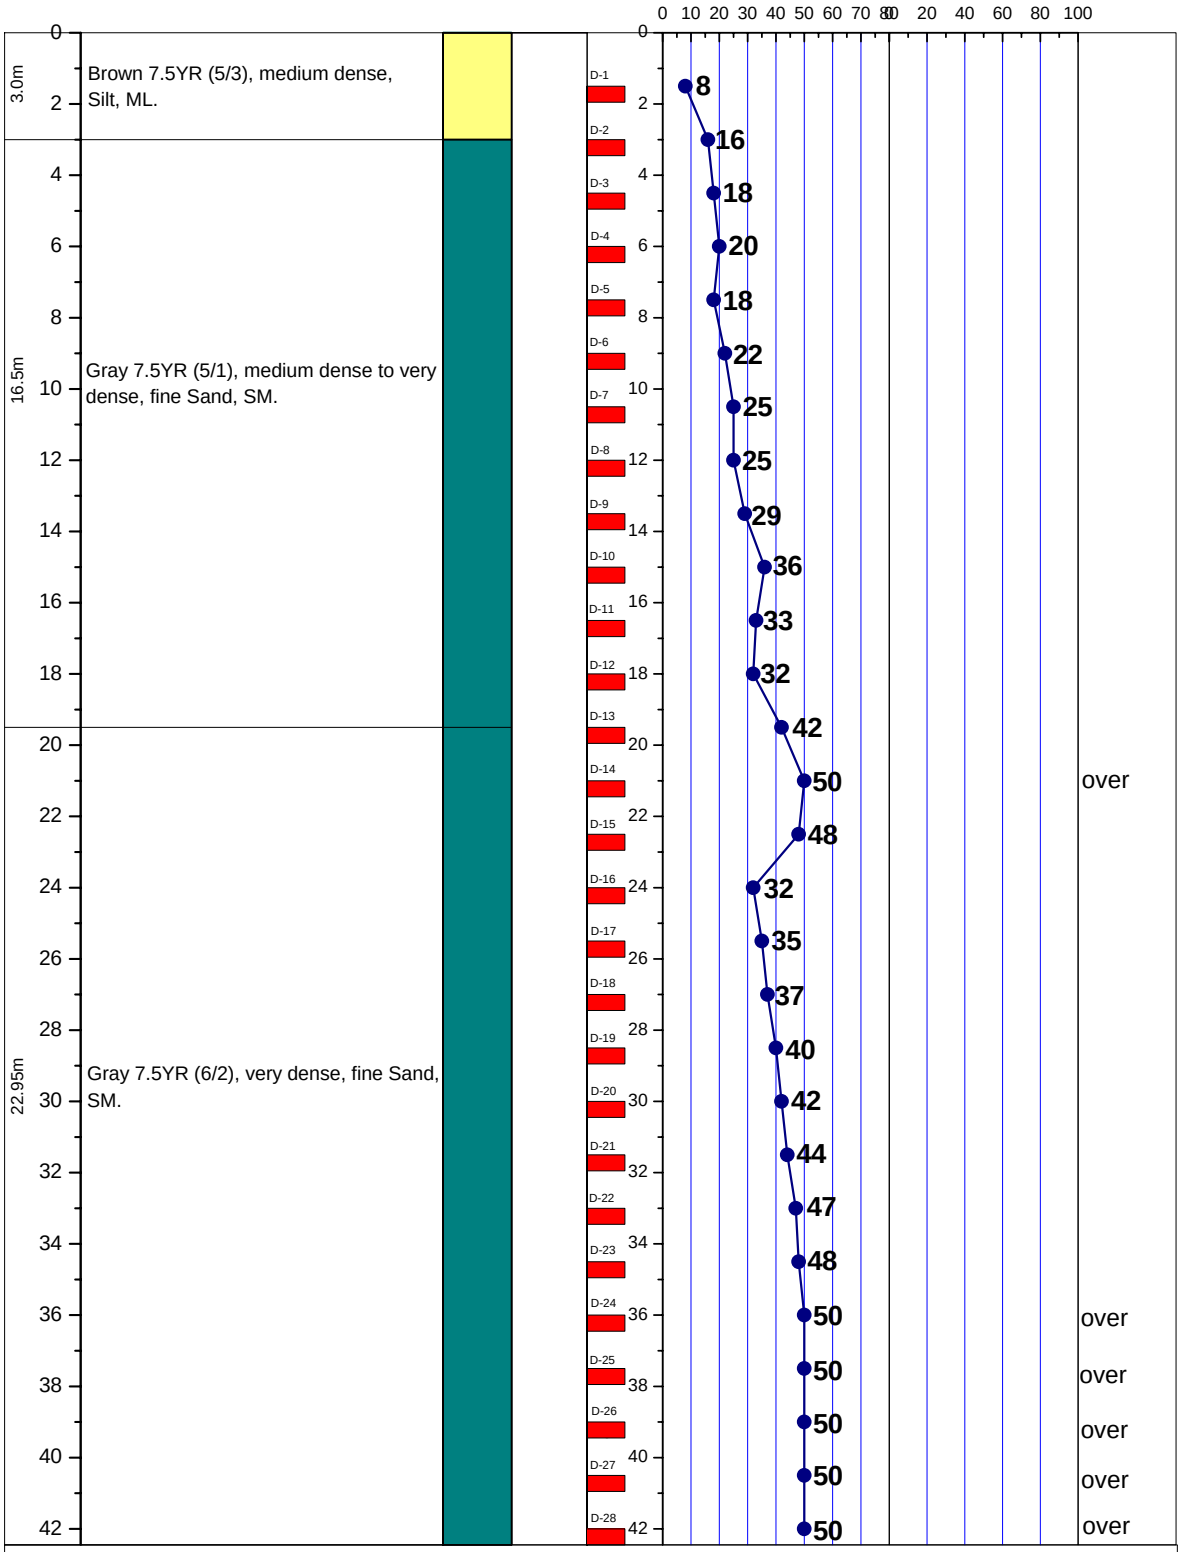

LEGEND FOR BORELOG AND GRAIN SIZE DISTRIBUTION

PLASTIC SILTY CLAY	NON PLASTIC SILT	ORGANIC	DISTURBED SAMPLE
LOW PLASTIC CLAYEY SILT	SAND	SHALE	UNDISTURBED SAMPLE

N- BLOWS DELIVERED PER FOOT BY A 140 LB HAMMER FALLING 30 INCHES

MAX^m PENETRATION= 50 BLOWS. AFTER 50 BLOWS PENETRATION DEPTH WERE MEASURED