A2	PROSOIL	BOREHOLE NO: BH-1	
		LOCATION : Alokbali Union, Narsingdi Sadar, Narsingdi.	
PROJECT : Proposed Union Parishad Complex Bhaban.		DEPTH OF BORING : 25.5m	R. L. : 0.51m below from Road Level.
CLIENT : Upazilla Engineer (LGED), Narsingdi Sadar, Narsingdi.		DATE OF BORING : 15-07-2011.	G. W. T : 0.46m below from E.G.L.

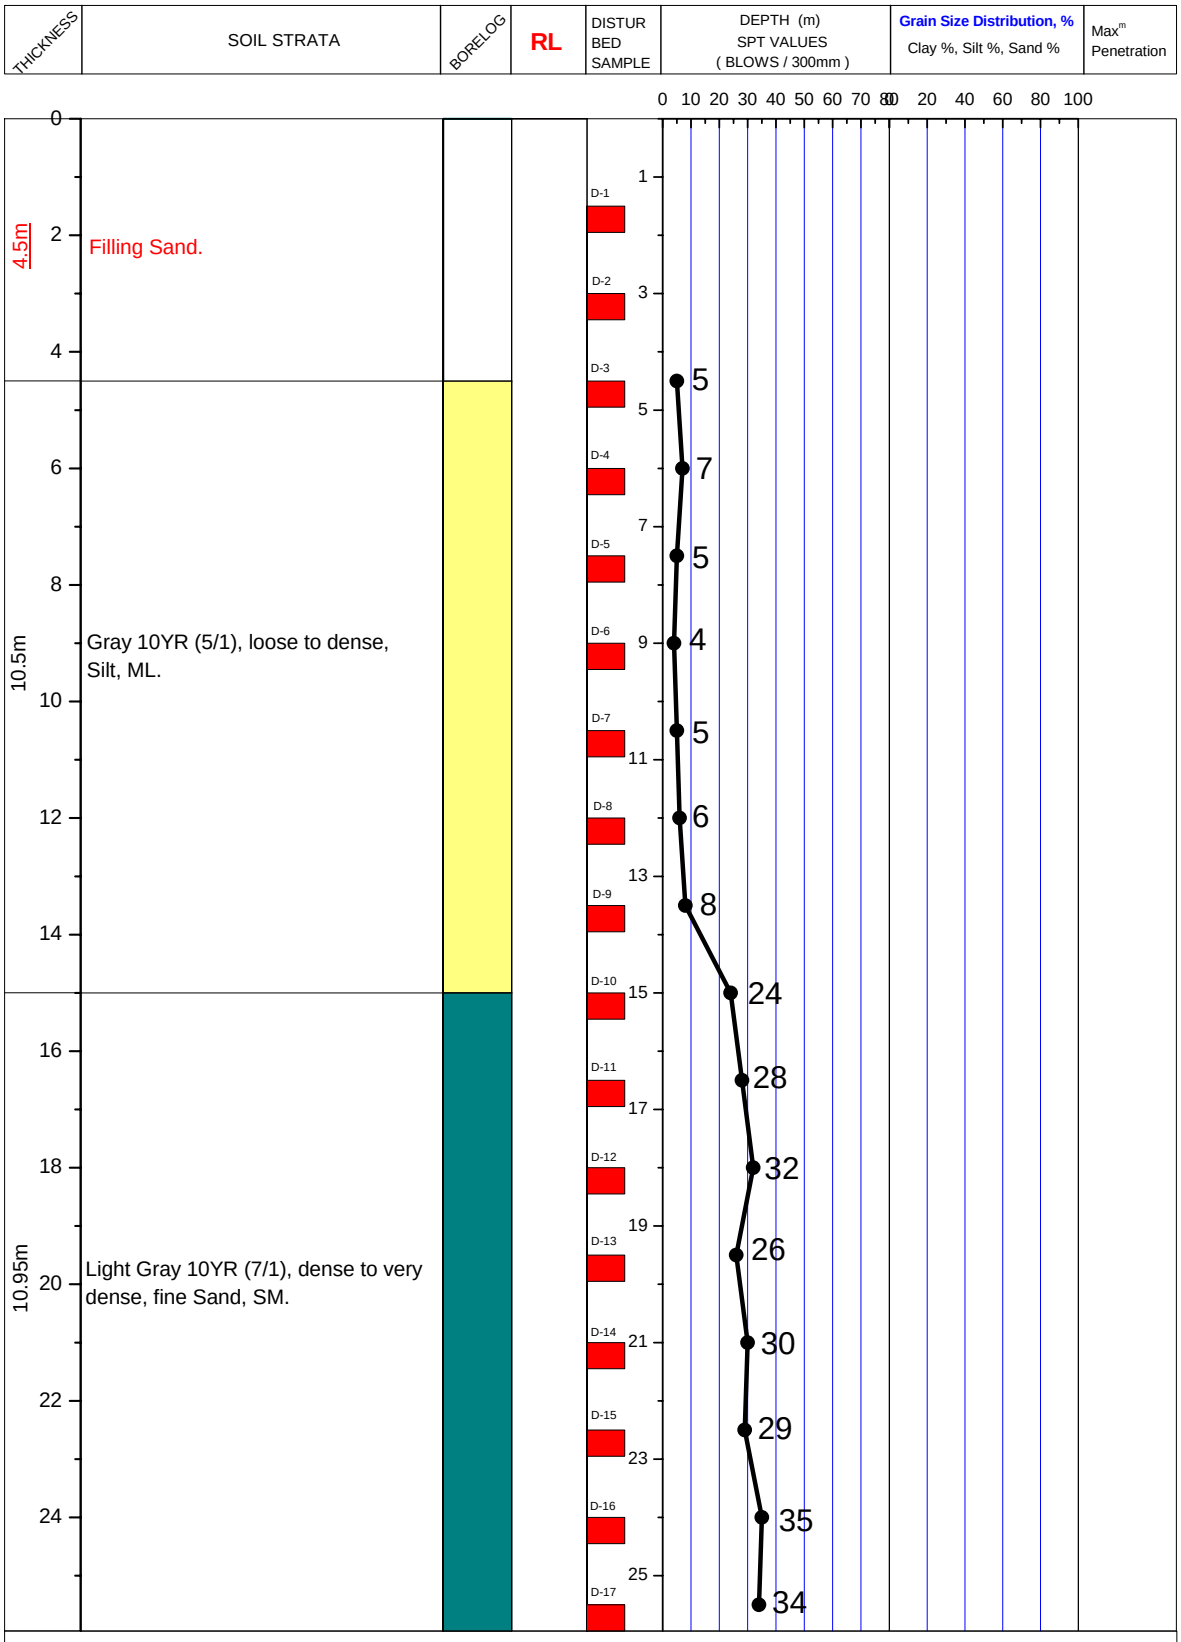

LEGEND FOR BORELOG AND GRAIN SIZE DISTRIBUTION (BASED ON 'ASTM CLASSIFICATION D-2487')

PLASTIC CLAY	SILT	PEAT/HIGHLY ORGANIC SOIL	UNDISTURBED SAMPLE
MICACEOUS FINE SAND/SILT	SAND	SHALE	DISTURBED SAMPLE

N- BLOWS DELIVERED PER FOOT BY A 140 LB HAMMER FALLING 30 INCHES

MAX^{m} PENETRATION= 50 BLOWS. AFTER 50 BLOWS PENETRATION DEPTH WERE MEASURED