A2	PROSOIL	BOREHOLE NO: BH-1	
		LOCATION : Thana Gaon, Balaganj, Sylhet. (24°43'44.4720"N, 91°47'42.8334"E).	
PROJECT : Thana Gaon GPS, (Multi-purpose Cyclone Shelter/Govt. Primary School)		DEPTH OF BORING : 24.0m	R. L.: 0.20m below from Road Level.
CLIENT : US Army Corps of Engr, Alaska District. THROUGH : AUSPICIOUS, QA Contractor.		DATE OF BORING: 15-04-2013.	G. W. T : 2.13m below from E.G.L.

THICKNESS	SOIL STRATA	BORELOG	UNDISTURBED SAMPLE	DISTURBED SAMPLE	DEPTH (m) SPT VALUES (BLOWS / 300mm)	Grain Size Distribution, % Clay %, Silt %, Sand %	Max^{m} Penetration

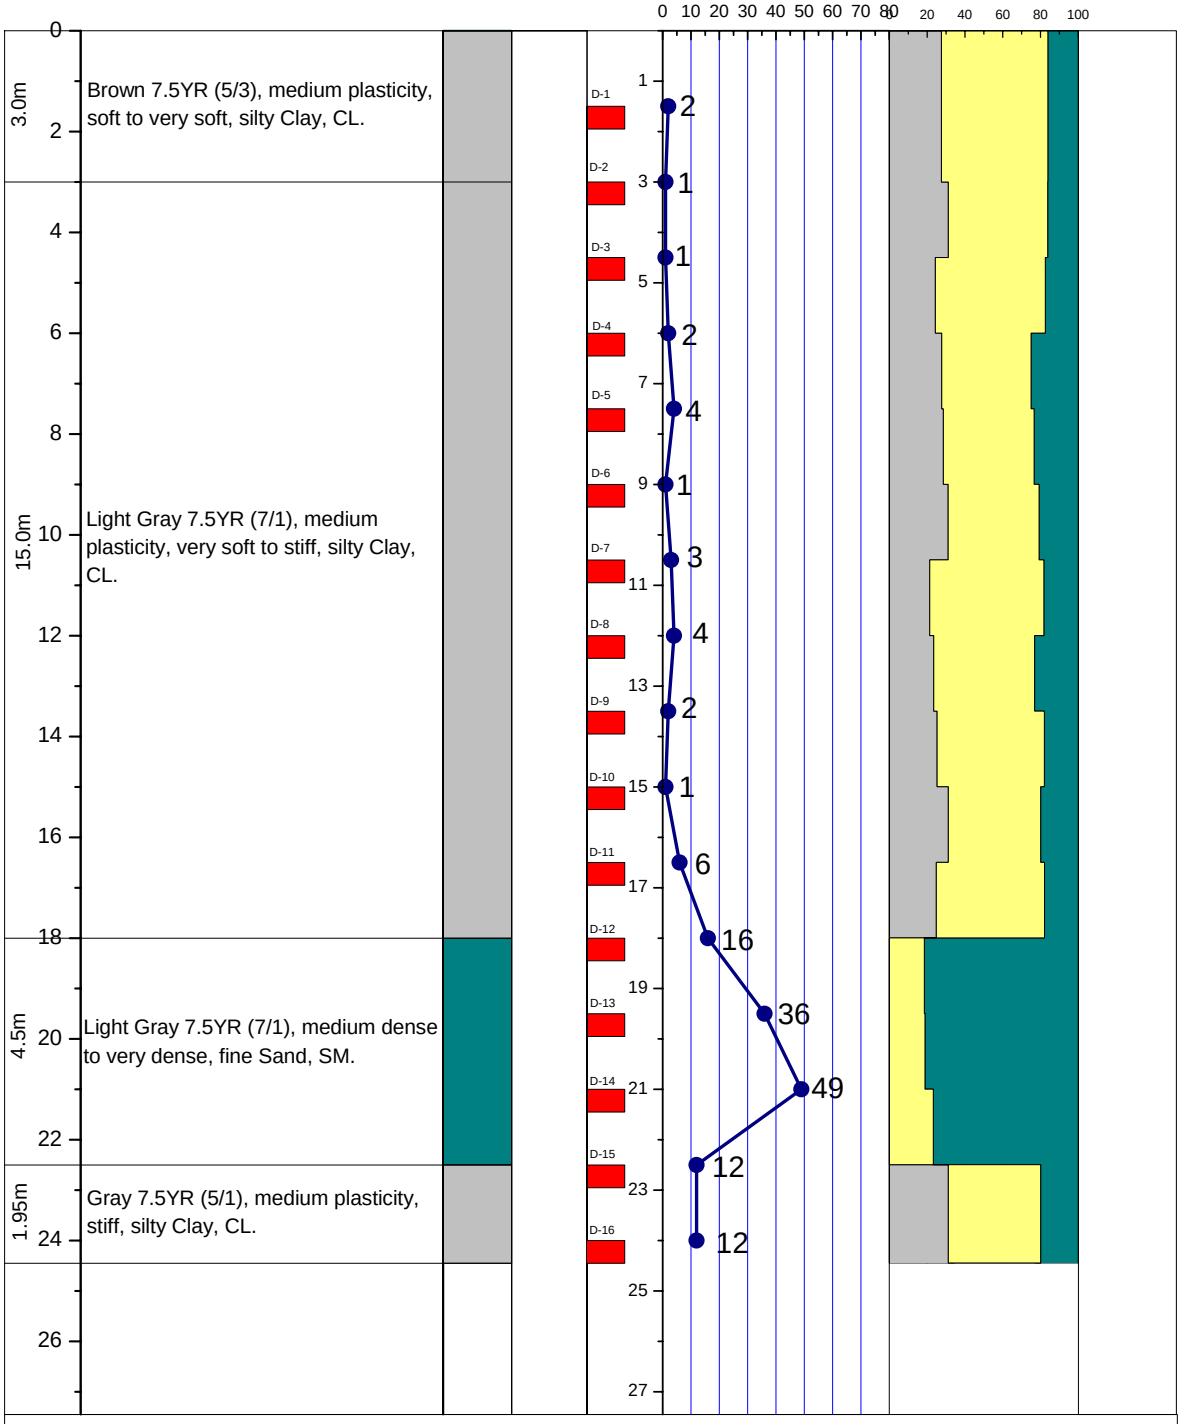

LEGEND FOR BORELOG AND GRAIN SIZE DISTRIBUTION (BASED ON 'ASTM CLASSIFICATION D-2487')

PLASTIC CLAY	SILT	SHALE	UNDISTURBED SAMPLE
MICACEOUS FINE SAND/SILT	SAND	PEAT/HIGHLY ORGANIC SOIL	DISTURBED SAMPLE

N- BLOWS DELIVERED PER FOOT BY A 140 LB HAMMER FALLING 30 INCHES

MAX^{m} PENETRATION= 50 BLOWS
AFTER 50 BLOWS PENETRATION DEPTH WERE MEASURED

A6	PROSOIL	BOREHOLE NO: BH-1 (SETTLEMENT CALCULATION)
		LOCATION : Thana Gaon, Balaganj, Sylhet. (24°43'44.4720"N, 91°47'42.8334"E).
PROJECT : Thana Gaon GPS, (Multi-purpose Cyclone Shelter/Govt. Primary School)		**SHALLOW FOOTING:** B: 0.6m, L=0.9m, P=100kpa
CLIENT : US Army Corps of Engr, Alaska District. THROUGH : AUSPICIOUS, QA Contractor.		**Shear failure Safety Factor=0.3**

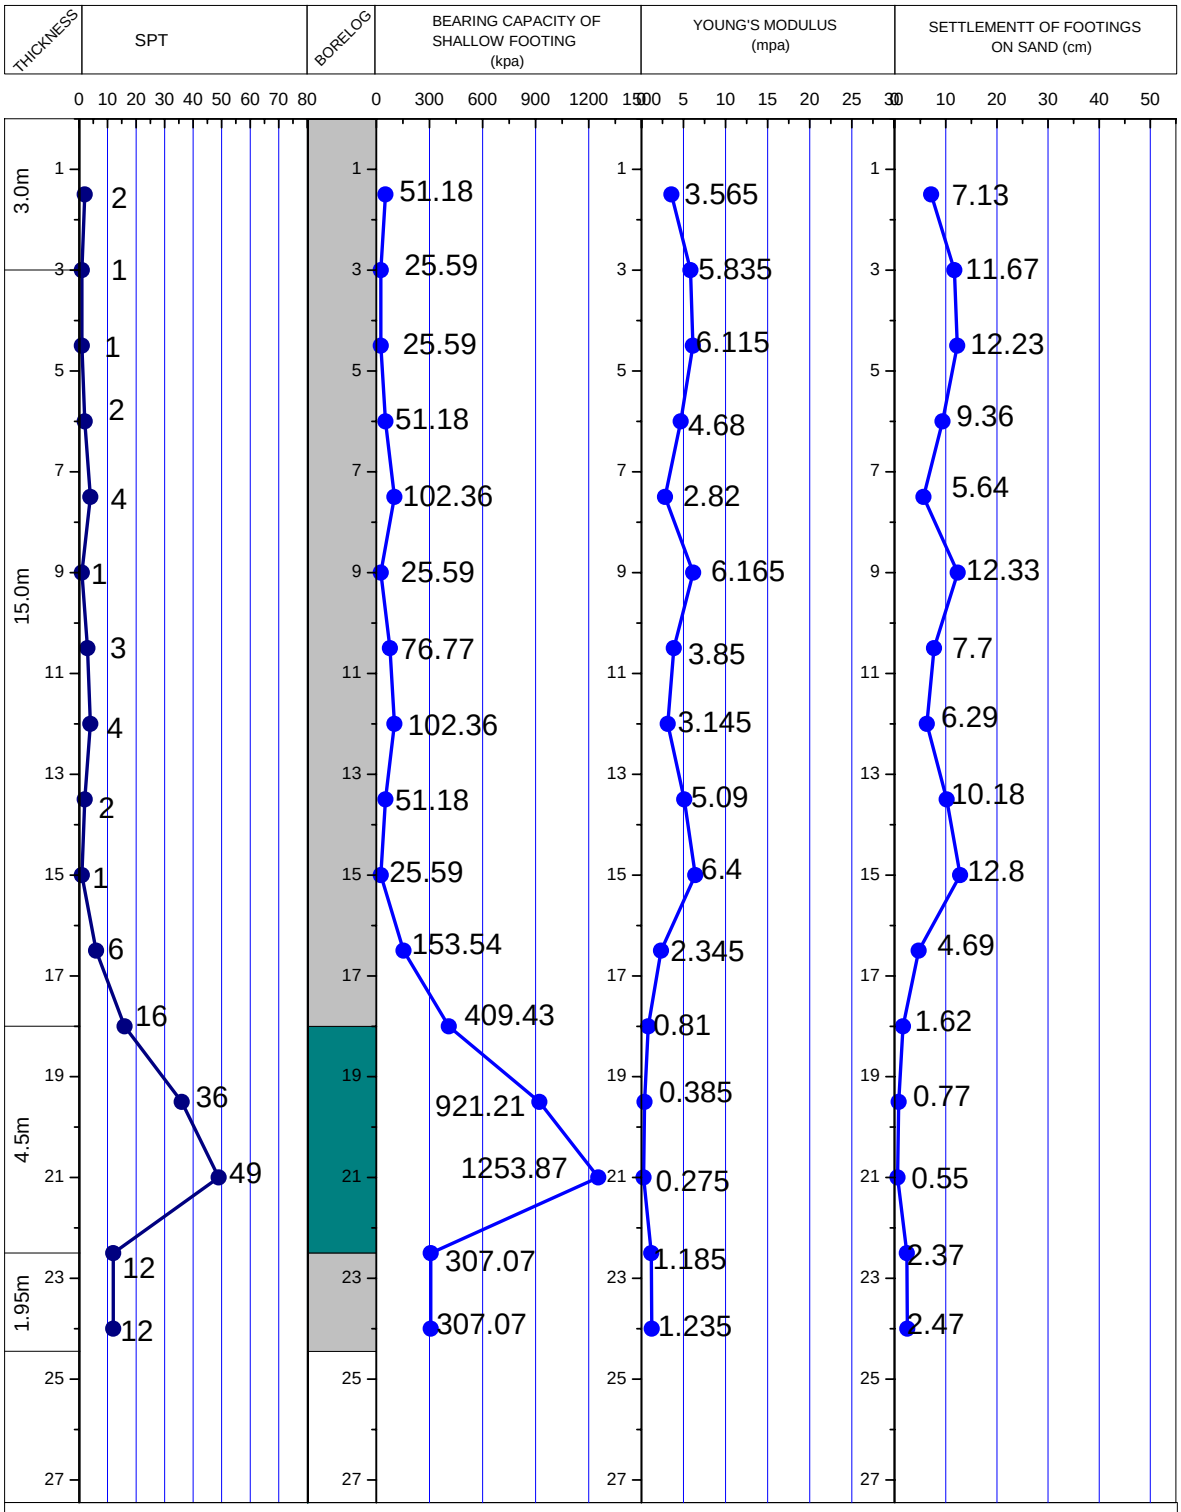

LEGEND FOR BOREHOLE AND GRAIN SIZE DISTRIBUTION (BASED ON 'ASTM CLASSIFICATION D-2487')

PLASTIC CLAY	SILT	SHALE	UNDISTURBED SAMPLE
MICACEOUS FINE SAND/SILT	SAND	PEAT/HIGHLY ORGANIC SOIL	

SETTLEMENT CALCULATION BY SOFTWARE: **NOVO SPT CORRELATION PROGRAM.**