
A2	PROSOIL	BOREHOLE NO: 01	
		LOCATION : P-6, Betuajani End.	
PROJECT : Construction of 520.60m Bridge over Dhaleshwari River.		DEPTH OF BORING : 36.0m	R. L. : 6.154m
CLIENT : LGED Tangail.		DATE OF BORING : 14-11-2014 to 17-11-2014.	G. W. T : 5.954m

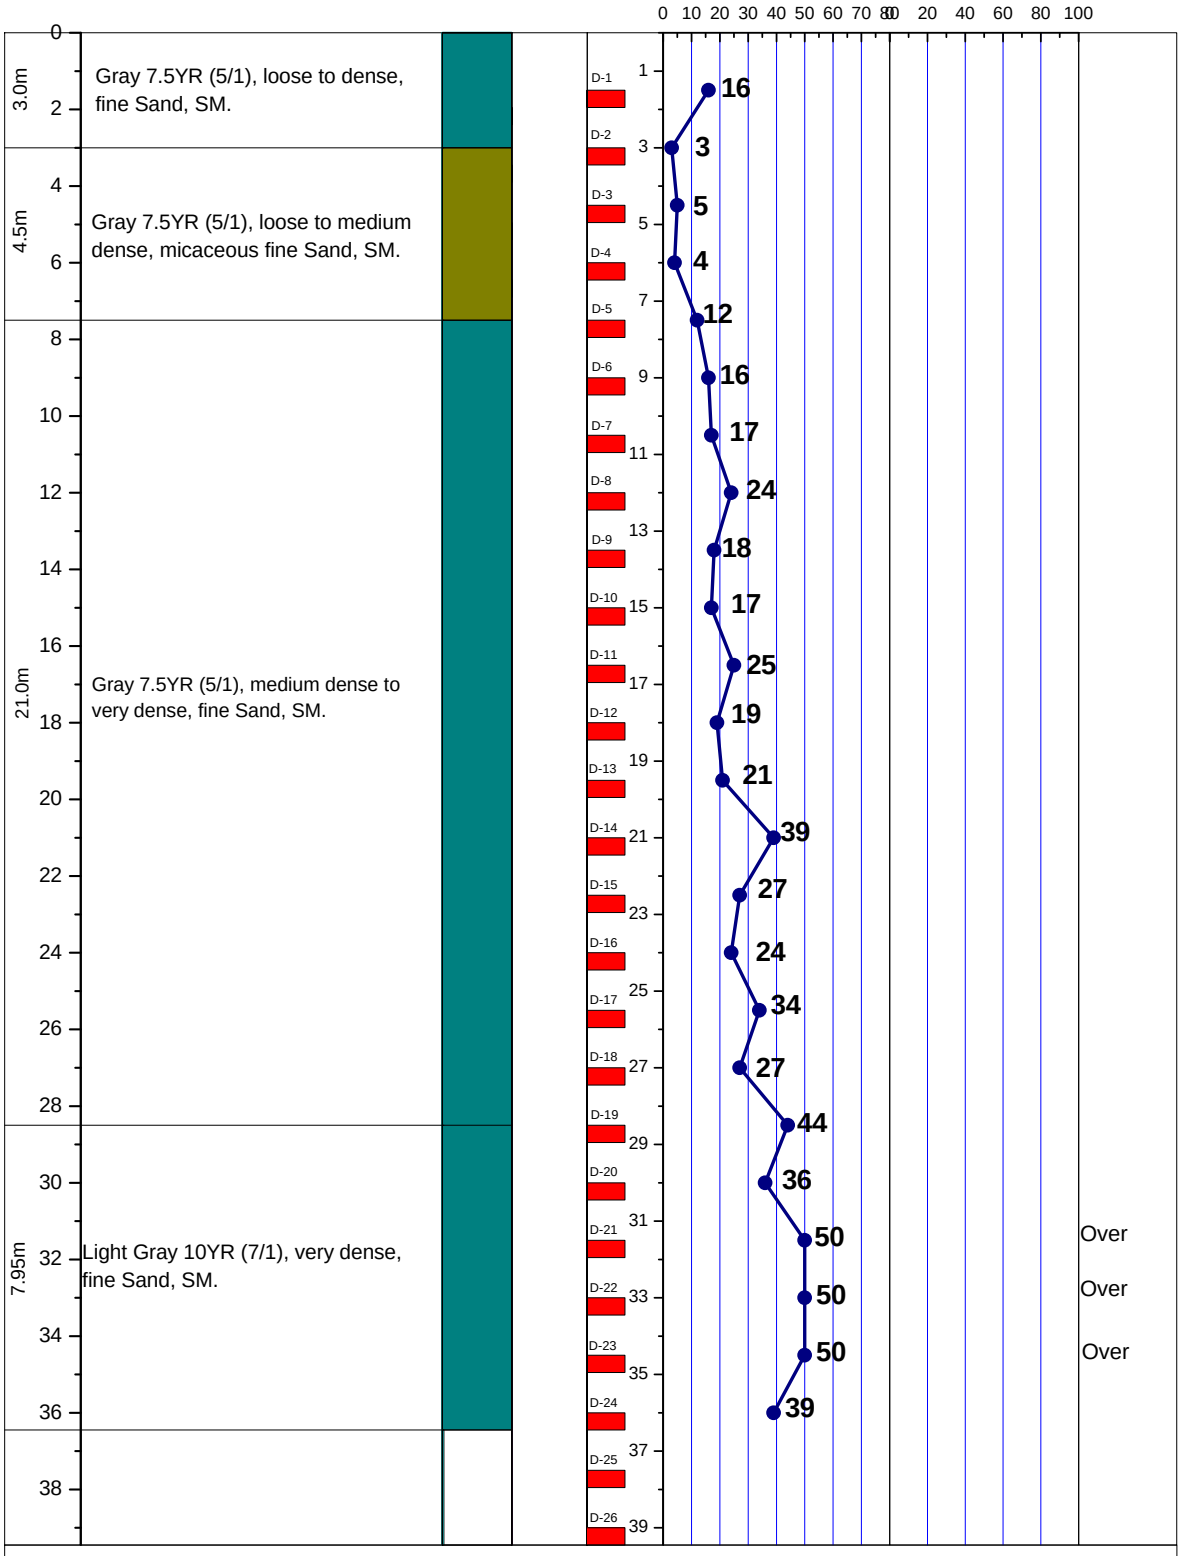

LEGEND FOR BORELOG AND GRAIN SIZE DISTRIBUTION (BASED ON 'ASTM CLASSIFICATION D-2487')

PLASTIC CLAY	SILT	PEAT/HIGHLY ORGANIC SOIL	UNDISTURBED SAMPLE
MICACEOUS FINE SAND/SILT	SAND	SHALE	DISTURBED SAMPLE

N- BLOWS DELIVERED PER FOOT BY A 140 LB HAMMER FALLING 30 INCHES

MAX^{m} PENETRATION= 50 BLOWS. AFTER 50 BLOWS PENETRATION DEPTH WERE MEASURED