A2	PROSOIL	BOREHOLE NO: BH-1	
		LOCATION : Laxmichary, Khagrachary.	
PROJECT : Telecommunication Tower.		DEPTH OF BORING : 10.5m	R. L.: Road Level.
CLIENT : Grameenphone Ltd.		DATE OF BORING : 10-07-2009.	G. W. T : Water table was too deep to measure.

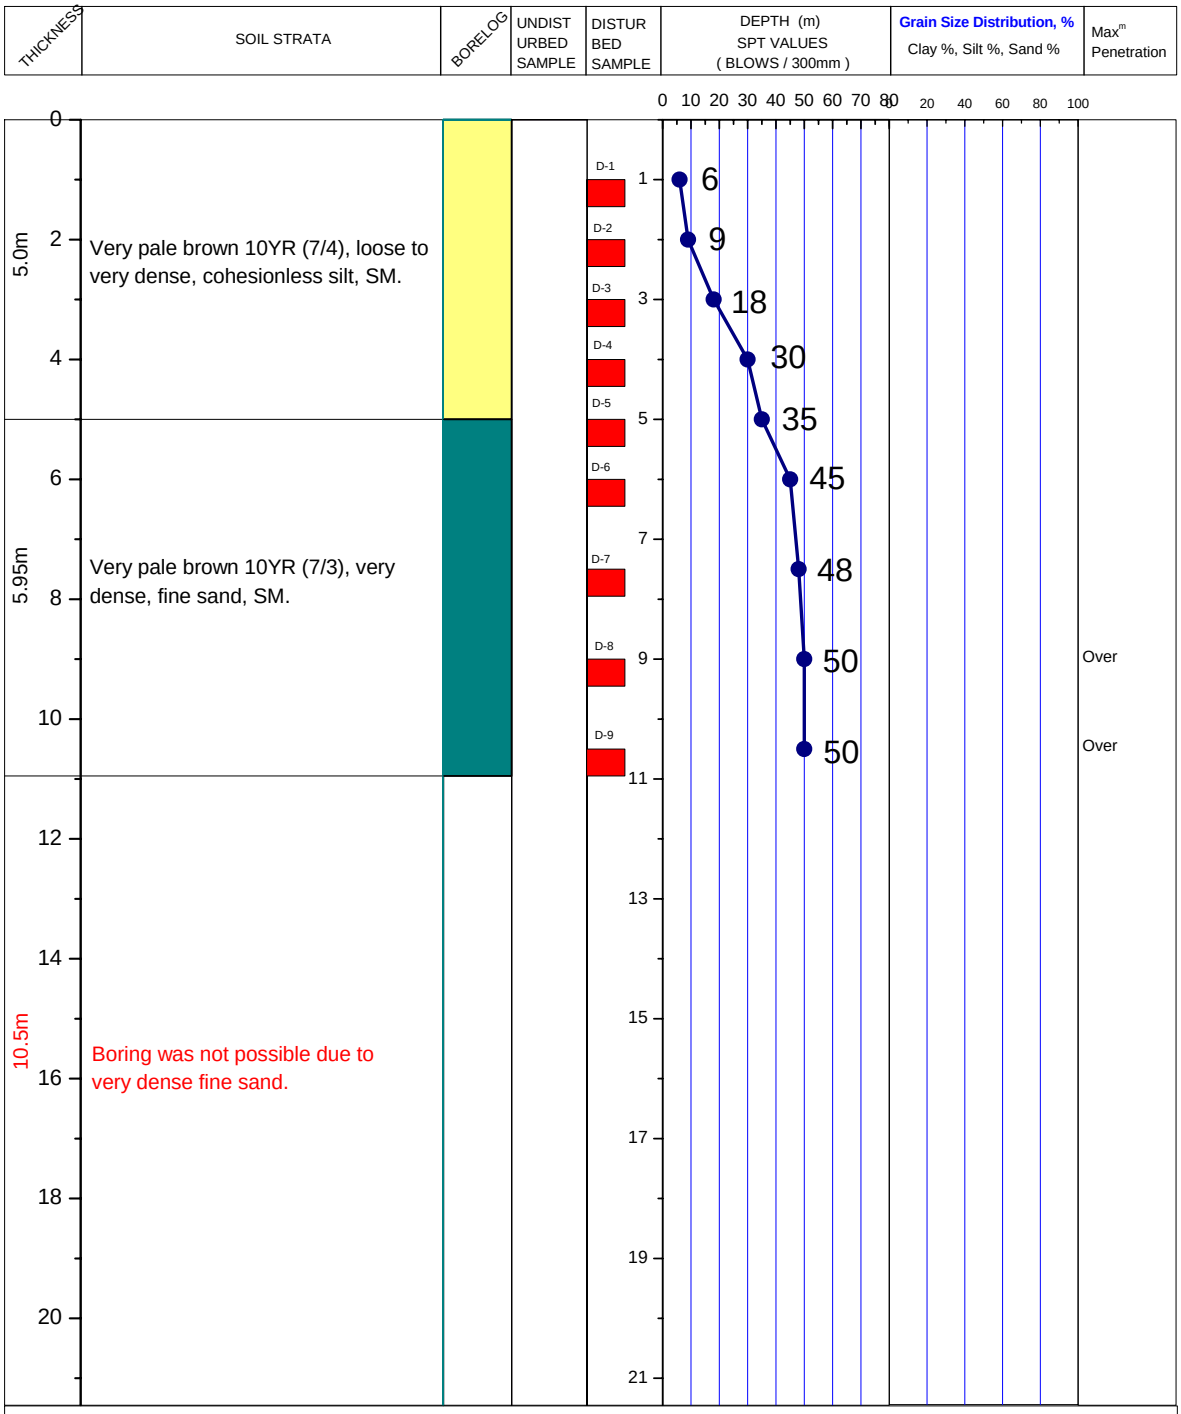

LEGEND FOR BORELOG AND GRAIN SIZE DISTRIBUTION

PLASTIC SILTY CLAY

LOW PLASTIC CLAYEY SILT

NON PLASTIC SILT

SAND

ORGANIC

UNDISTURBED SAMPLE

DISTURBED SAMPLE

SHALE

N- BLOWS DELIVERED PER FOOT BY A 140 LB HAMMER FALLING 30 INCHES

MAX^{m} PENETRATION= 50 BLOWS

AFTER 50 BLOWS PENETRATION DEPTH WERE MEASURED