A2	PROSOIL	BOREHOLE NO: BH-1	
		LOCATION : 64th km (LPR063a: Ch.63+311) of Comilla(Mainamoti) -B.Baria(Sarail)Road (N102).	
PROJECT : Proposed Sultanpur Bridge.		DEPTH OF BORING : 30.0m	Chainage: 63+313.5 R. L. : 7.03
CLIENT : Road Division, Brahmanbaria.		DATE OF BORING : 10-12-2010.	G. W. T : 5.18m below from E.G.L.

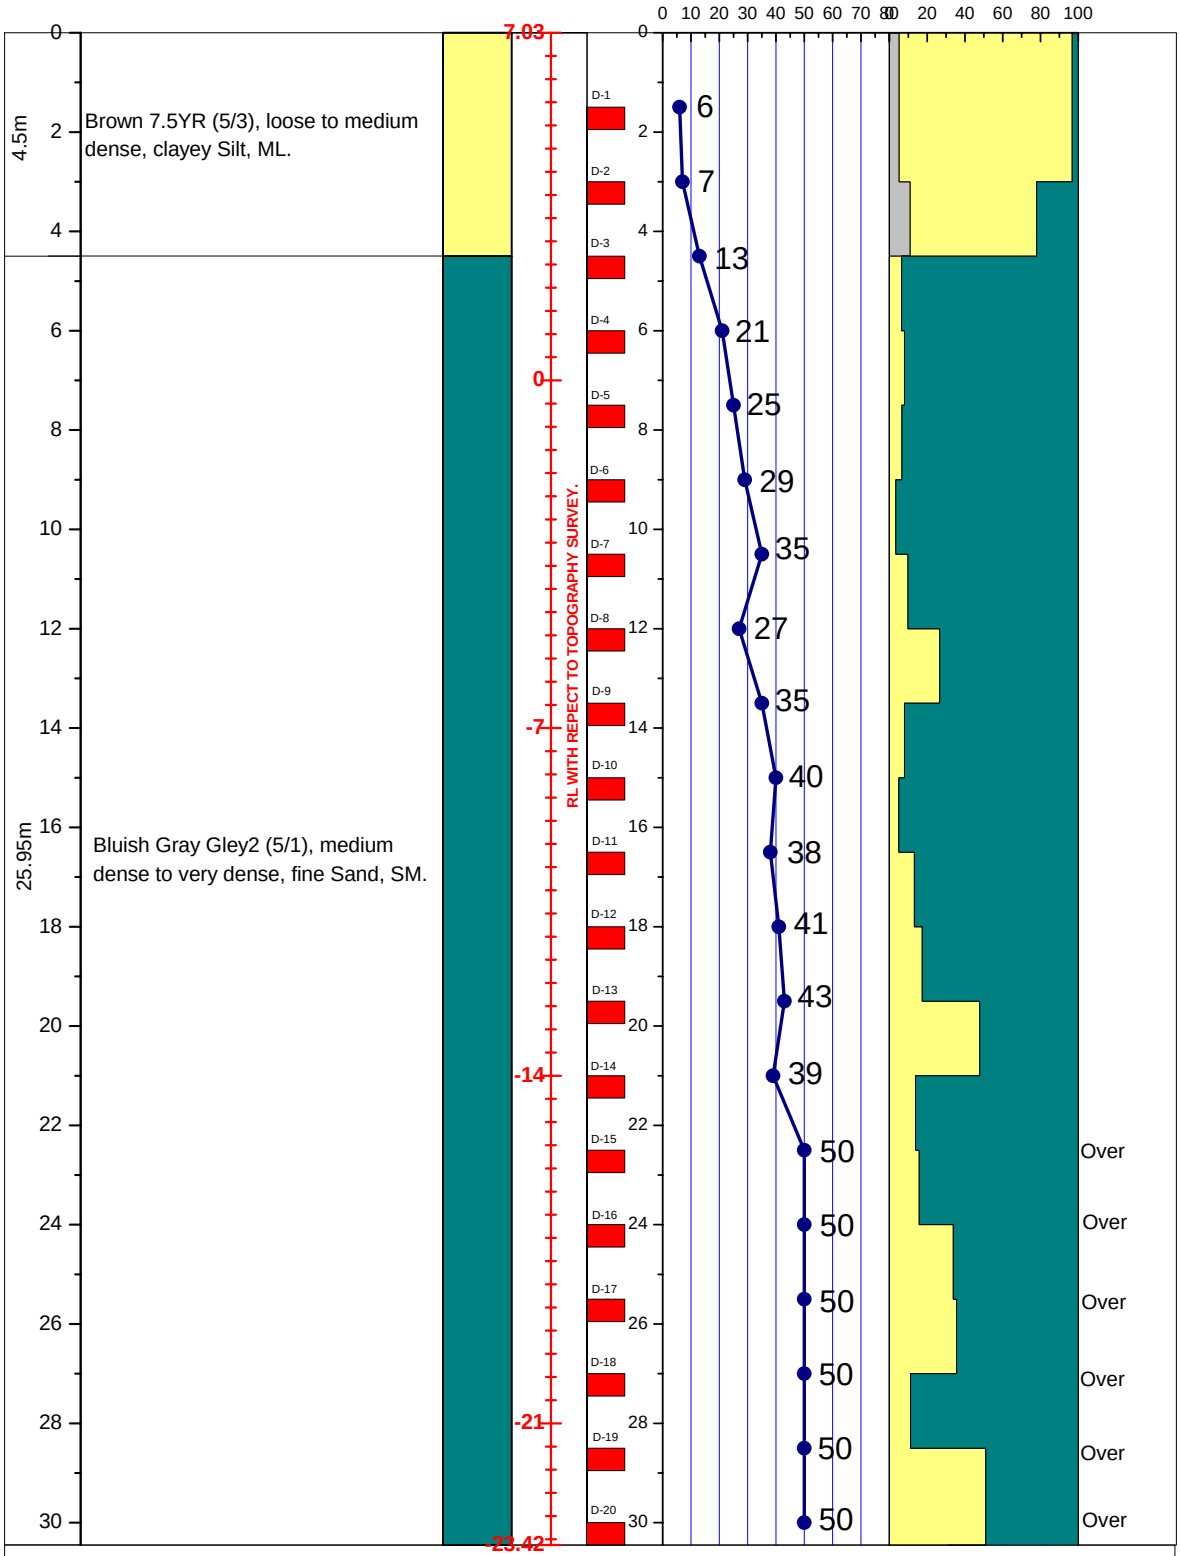

LEGEND FOR BORELOG AND GRAIN SIZE DISTRIBUTION (BASED ON 'ASTM CLASSIFICATION D-2487')

PLASTIC CLAY	SILT	PEAT/HIGHLY ORGANIC SOIL	UNDISTURBED SAMPLE
MICACEOUS FINE SAND/SILT	SAND	SHALE	DISTURBED SAMPLE

N- BLOWS DELIVERED PER FOOT BY A 140 LB HAMMER FALLING 30 INCHES

MAX^{m} PENETRATION= 50 BLOWS. AFTER 50 BLOWS PENETRATION DEPTH WERE MEASURED