
A2	PROSOIL	BOREHOLE NO: BH-1	
		LOCATION: Ramu Cantonment, Ramu, Cox,s bazar.	
PROJECT : Telecommunication Tower.		DEPTH OF BORING: 9.0m	R. L.: 45.371m Above from Road Level.
CLIENT : Grameenphone Ltd.		DATE OF BORING: 25-11-2015.	B. W. T : 4.57m below from E. G. L.

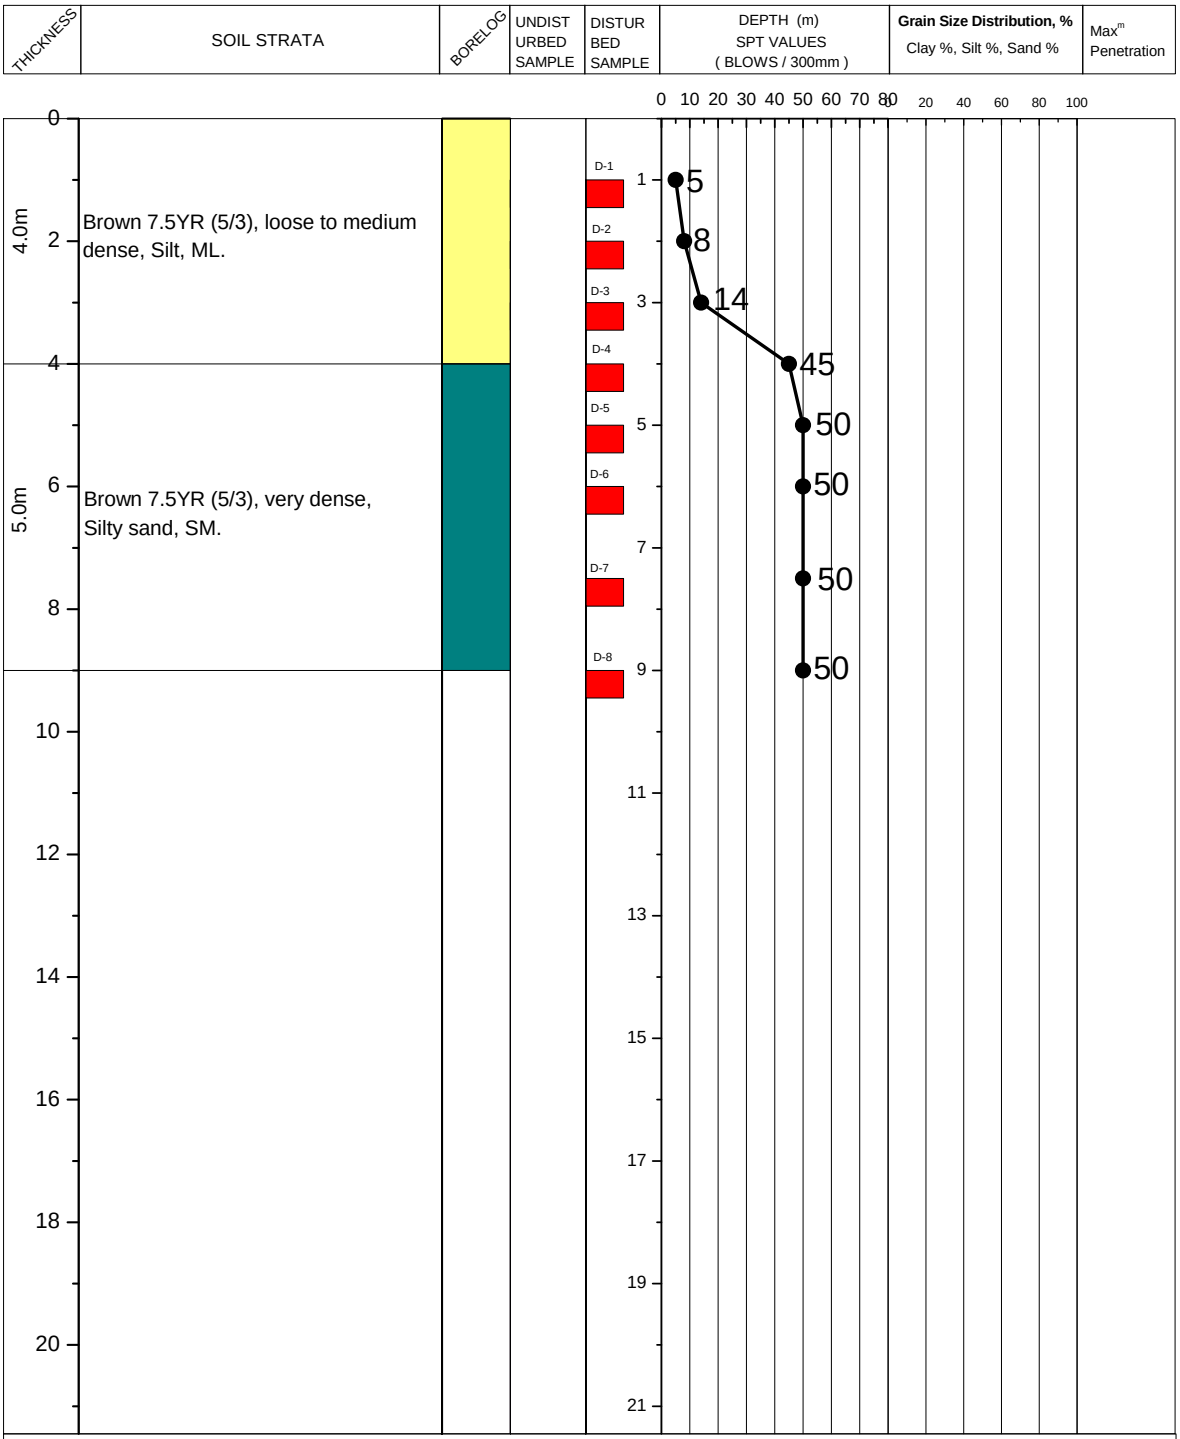

PLASTIC CLAY | SHALE | SAND

PEAT/HIGHLY ORGANIC SOIL | MICACEOUS FINE SAND/SILT | UNDISTURBED SAMPLE | DISTURBED SAMPLE

N- BLOWS DELIVERED PER FOOT BY A 140 LB HAMMER FALLING 30 INCHES

MAX^{m} PENETRATION= 50 BLOWS

AFTER 50 BLOWS PENETRATION DEPTH WERE MEASURED