A2 PROSOIL	BOREHOLE NO: BH-1 (BRAHMANBARIA END)	
	LOCATION : Road #N102, Road Name :Comilla -Brahman Baria Road, Bridge ID #71/1, LRP 070a.	
PROJECT : Proposed Bridge ID #71/1, LRP 070a.	DEPTH OF BORING : 30.0m	Chainage: 78+260 R. L. : 4.997
CLIENT : Roads And Highways Department.	DATE OF BORING: 04-09-2012.	G. W. T : 0.30m below from E.G.L.

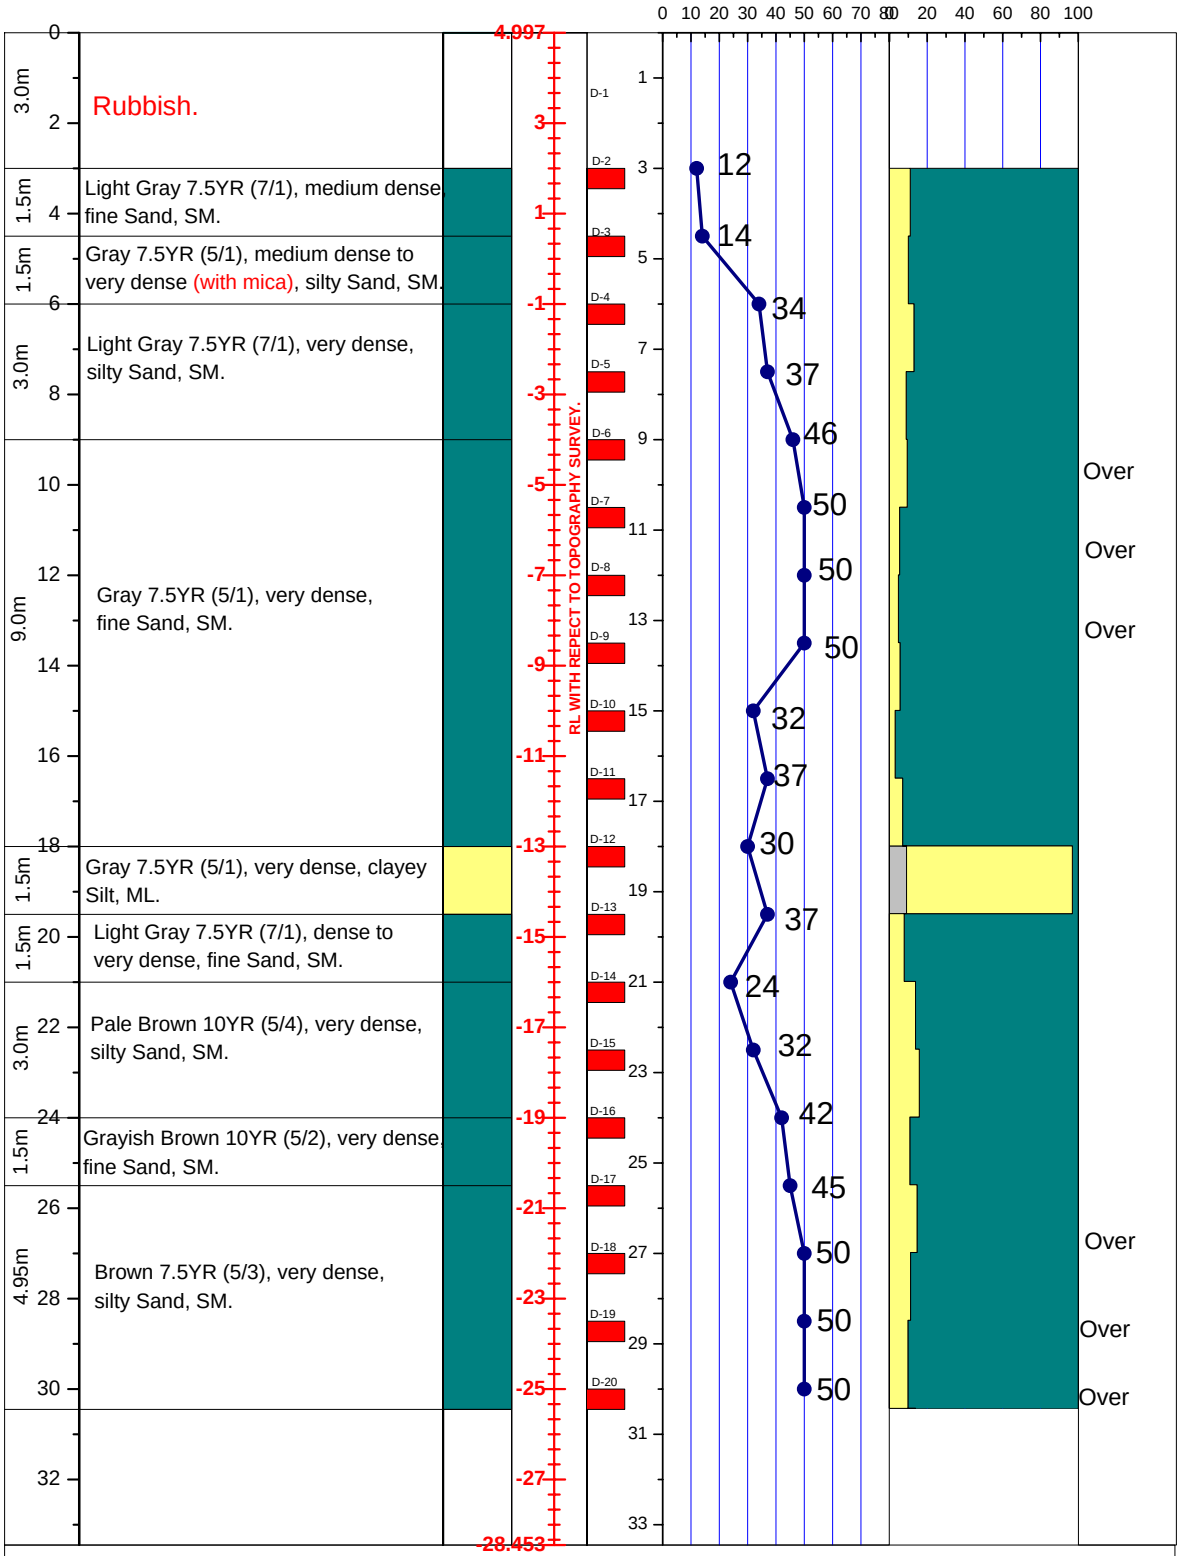

LEGEND FOR BOREHOLE AND GRAIN SIZE DISTRIBUTION (BASED ON 'ASTM CLASSIFICATION D-2487')

PLASTIC CLAY	SILT	PEAT/HIGHLY ORGANIC SOIL	UNDISTURBED SAMPLE
MICACEOUS FINE SAND/SILT	SAND	SHALE	DISTURBED SAMPLE

N- BLOWS DELIVERED PER FOOT BY A 140 LB HAMMER FALLING 30 INCHES

MAX^m PENETRATION= 50 BLOWS. AFTER 50 BLOWS PENETRATION DEPTH WERE MEASURED