A2 PROSOIL	BOREHOLE NO: BH-1	
	LOCATION : at 20th k.m. of Gap No. 20/1 on Bhulta-Araihazar-Bancharampur -Nabinagar- Shibpur-Radhika Road.	
PROJECT : Construction of Proposed Vhorer Bazar Bridge.	DEPTH OF BORING : 51.5m	R. L.: 6.09m below from Road Level.
CLIENT : Road Division, B.Baria.	DATE OF BORING : 25-02-2009.	G. W. T : 1.21m below from E.G.L.

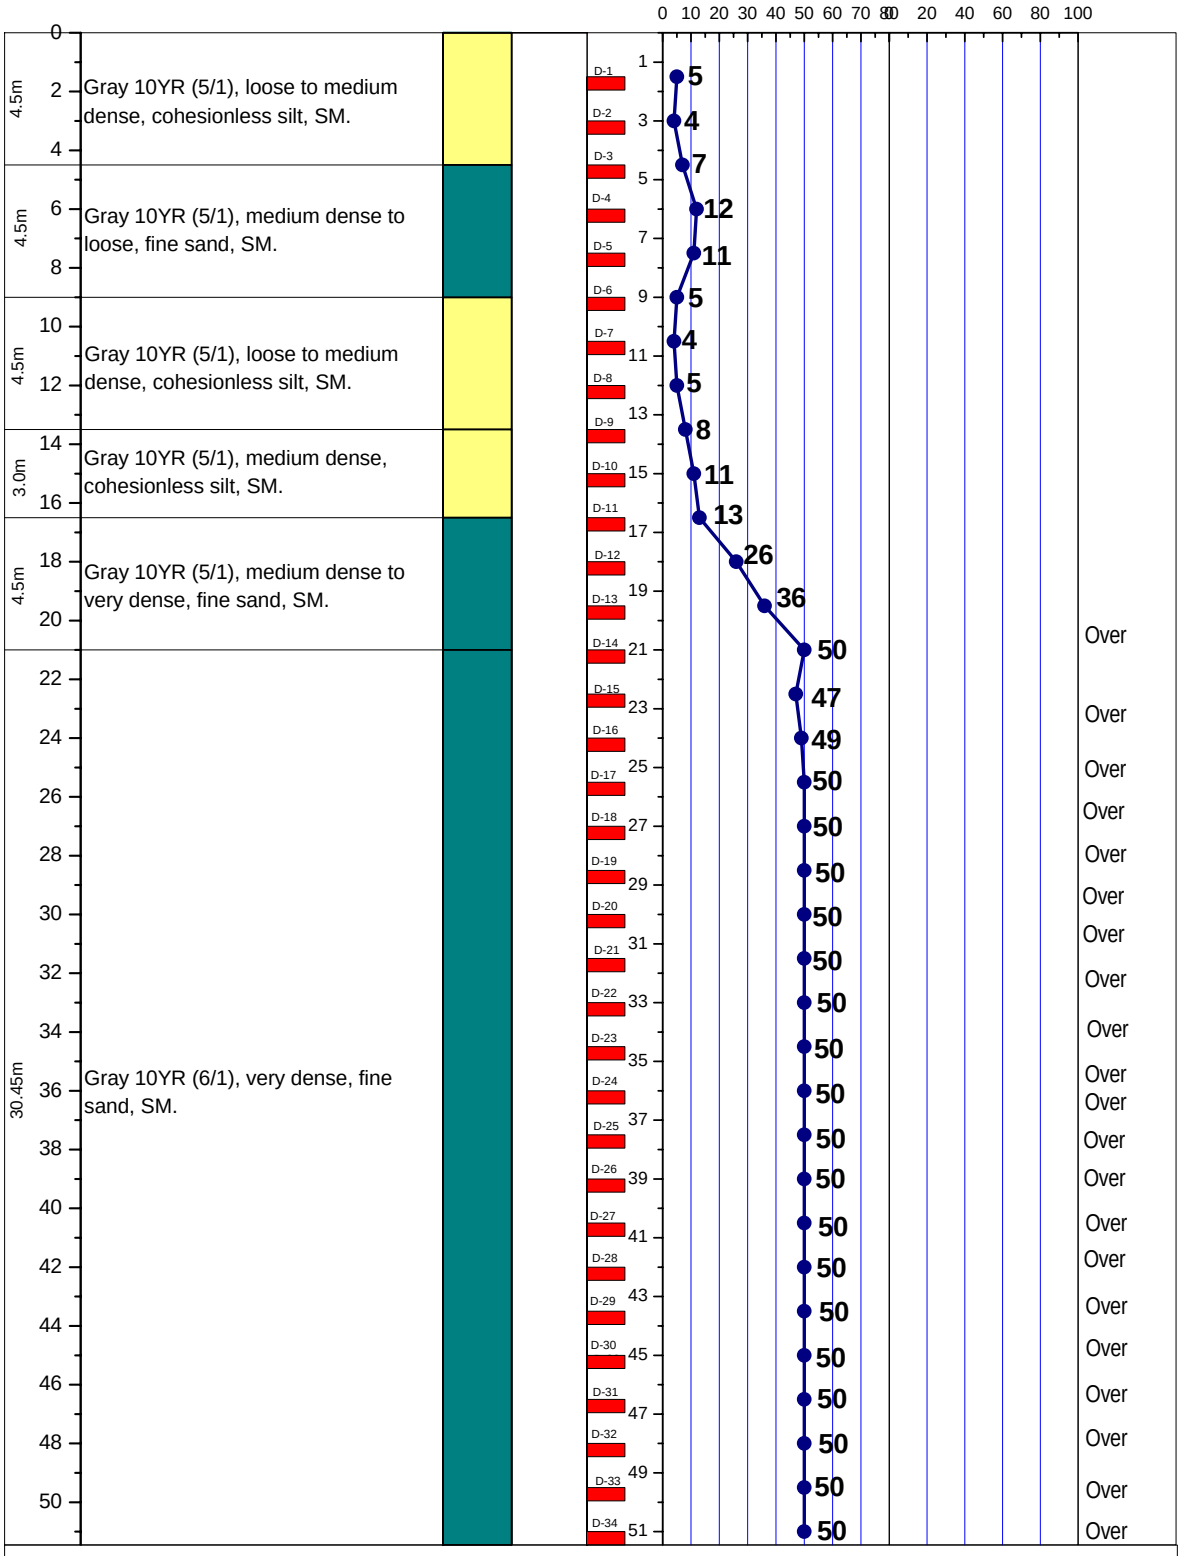

LEGEND FOR BORELOG AND GRAIN SIZE DISTRIBUTION

PLASTIC SILTY CLAY	NON PLASTIC SILT	ORGANIC	DISTURBED SAMPLE
LOW PLASTIC CLAYEY SILT	SAND	SHALE	UNDISTURBED SAMPLE

N- BLOWS DELIVERED PER FOOT BY A 140 LB HAMMER FALLING 30 INCHES

MAX^m PENETRATION= 50 BLOWS. AFTER 50 BLOWS PENETRATION DEPTH WERE MEASURED